

Gerência de Engenharia e Projetos de Eletroeletrônica

PROJETO EXECUTIVO
SINALIZAÇÃO VALE DO PARAÍBA
ABRIGO 15 – ITAPETI – FIP–3

ANOTAÇÕES

LEGENDA:



INCLUIR CIRCUITO/EQUIPAMENTO



RETIRAR CIRCUITO/EQUIPAMENTO



FIRMA CONTRATADA:

–

Nº ARQUIVO MRS:

TÍTULO DES.:

CAPA
PROJETO EXECUTIVO
SINALIZAÇÃO VALE DO PARAÍBA

ENG.RESP.: HAROLDO ENNES

DATA: 10/11/2023

PROJ.: MÁRCIO MOREIRA

ESCALA: S/ESC.

FORMATO: A3

DES.PROJ.: ANTÔNIO LEAL

REV./DATA: –

FIP3_ABR15_CAPA

SUBST./REF.: –

ÍNDICE

CONTEÚDO

NÚMERO MRS		NÚMERO DA REVISÃO								
		1	2	3	4	5	6	7	8	9
✖✖1	EE-SA-OIWO-XXX-XX									
✖✖1	EE-SA-OIWO-XXX-XX									
	PE-OS-OFIP-001-01									
	PE-OS-OFIP-002-01									
	PE-OS-OFIP-003-01									
	PE-OS-OFIP-004-01									
	PE-OS-OFIP-005-01									
	PE-OS-OFIP-006-01									
	PE-OS-OFIP-007-01									
	PE-OS-OFIP-008-01									
	PE-OS-OFIP-009-01									
	PE-OS-OFIP-010-01									
	PE-OS-OFIP-011-01									
	PE-OS-OFIP-012-01									
	PE-OS-OFIP-013-01									
	PE-OS-OFIP-014-01									
	PE-OS-OFIP-015-01									
	PE-OS-OFIP-016-01									
	PE-OS-OFIP-017-01									
	PE-OS-OFIP-018-01									
	PE-OS-OFIP-019-01									
	PE-OS-OFIP-020-01									
	PE-OS-OFIP-021-01									
	PE-OS-OFIP-022-01									
	PE-OS-OFIP-023-01									
	PE-OS-OFIP-024-01									
	PE-OS-OFIP-025-01									





























= DESIGN COMPLETADO

= REVISÃO COMPLETADA

OBSERVAÇÕES:

1.(✖✖1) = ESPAÇO SERÁ PREENCHIDO EM CONJUNTO COM O AS BUILT

ANOTAÇÕES	A Operação dos circuitos e equipamentos aqui representados não podem ser completamente verificados senão após a sua instalação de modo a formar um sistema completo de sinalização ferroviária e ser devidamente submetido a "Testes de seleção de contatos(BREAKDOWN)" e "Testes operacionais de serviço"(Através de planilhas e fluxo de testes) antes de sua colocação em serviços normal definitivo. ENGENHARIA DE ELETROELETRÔNICA DE PROJETOS	MRS Logística S.A.	TÍTULO DES.: LINHA DE SÃO PAULO ÍNDICE (TÍTULO/CONTEÚDO/REVISÕES/OBSERVAÇÕES) ABR 15 ITAPETI – FIP		
			ENG.RESP.: HAROLDO ENNES	DATA: 07/03/2023	
			PROJ.: MÁRCIO MOREIRA	ESCALA: –	FORMATO: A3
			DES.PROJ.: ANTÔNIO LEAL	REV./DATA: –	
			Nº ARQUIVO MRS: PE-OS-OFIP-001-01		SUBST./REF.:

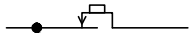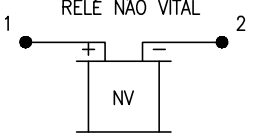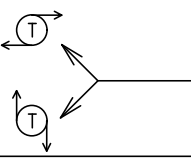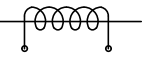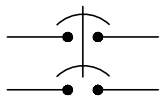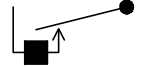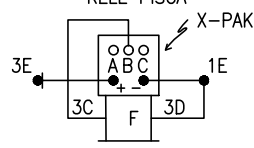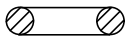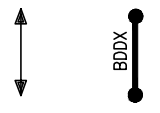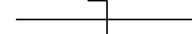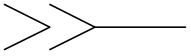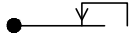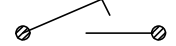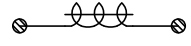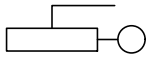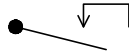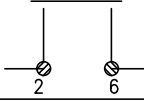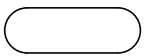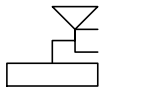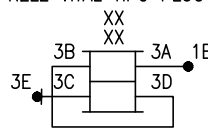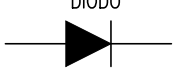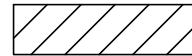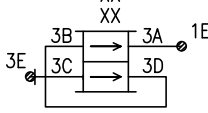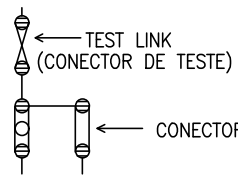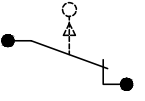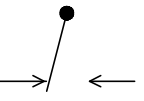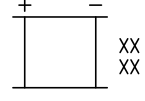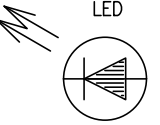 CIRCUITO DE VIA ENTRE JUNTAS ISOLANTE	 CABO DE PAR TRANÇADO	 CONTATO DE ALTA CORRENTE	 RELÉ NÃO VITAL	 TEST LINK CONECTOR DE TESTE	 PAR TRANÇADO	 TRANSDUTOR	 LAYOUT DO BLOCO DE TERMINAL 2X6
 JUNTA ISOLANTE	 DISJUNTOR ELÉTRICO	 CONTATO DE ALTA CORRENTE MAGNÉTICO	 RELÉ PISCA	 CONECTOR	 FONTE DE ENERGIA AC	 DETECTOR DE DESCARRILHAMENTO	 TERMINAL RESISTOR 8Ω/25W
 JUNTA DE FIM DE SINALIZAÇÃO	 INTERRUPTOR DE PÓLO ÚNICO	 CONTATO DE OPERAÇÃO DE MÁQUINA DE CHAVE	 INTERRUPTOR TOGGLE	 CONECTOR DE INTERFACE	 MOTOR	 CAIXA DE PASSAGEM	
 SINALEIRO R = VERMELHO Y = AMARELO G = VERDE	 CONTATO FRONT ENERGIZADO	 CONTATO DE OPERAÇÃO MANUAL DE MÁQUINA DE CHAVE	 SUPRESSOR	 TERRA	 IMPEDÂNCIA FIXA COM NÚCLEO DE FERRO	 POSTE COM ANTENA PLANO TERRA DDvR	
 MÁQUINA DE CHAVE ELÉTRICA	 CONTATO FRONT DESENERGIZADO	 CONTATO DO CIRCUITO DE INDICAÇÃO DA MAQUINA DE CHAVE	 EQUALIZADOR	 ANOTAÇÕES	 RESISTOR VARIÁVEL	 SENSOR DE RODA [CONTADOR DE EIXO]	
 MÁQUINA DE CHAVE COM TRAVADOR ELÉTRICO	 CONTATO BACK ENERGIZADO	 RELÉ VITAL TIPO PLUG	 TERMINAL UNIVERSAL	 DÍODO	 RESISTOR	 CANALETA CABOS	
 AMV; SETA SOMBREADA MOSTRA O ALINHAMENTO NORMAL	 CONTATO BACK DESENERGIZADO	 RELÉ POLARIZADO	 TEST LINK (CONECTOR DE TESTE)	 LAMP, LED PODE SER G, Y, OU R	 SUPRESSOR HÍBRIDO	 CONTATO "NA" FECHADO DO SWITCH	
 ABRIGOS, DIMENSÃO MOSTRADO NO PLANO 1220X1220mm, 1829X1829mm, 2438X1829mm E 3048X1829mm.	 CONTATO POLAR	 RELÉ VITAL TIPO DE PRATELEIRA	 TERMINAIS	 LED	 VARISTOR CLAMPER	 LAYOUT DO TERMINAL UNIVERSAL	

ANOTAÇÕES

A Operação dos circuitos e equipamentos aqui representados não podem ser completamente verificados senão após a sua instalação de modo a formar um sistema completo de sinalização ferroviária e ser devidamente submetido a "Testes de seleção de contatos(BREAKDOWN)" e "Testes operacionais de serviço"(Através de planilhas e fluxo de testes) antes de sua colocação em serviços normal definitivo.
ENGENHARIA DE ELETROELETRÔNICA DE PROJETOS

CONTROLE INTERNO DE PROJETOS GEPEE	DATA
ELABORADOR: ANTÔNIO LEAL	07/03/2023
REVISOR: MÁRCIO MOREIRA	22/03/2023
APROVADOR: MARCOS REINH	31/03/2023



FIRMA CONTRATADA:

Nº ARQUIVO MRS:

TÍTULO DES.:

LINHA DE SÃO PAULO
SÍMBOLOS
ABR 15
ITAPETI – FIP

ENG.RESP.: **HAROLDO ENNES**
PROJ.: **MÁRCIO MOREIRA**
DES.PROJ.: **ANTÔNIO LEAL**


DATA: **07/03/2023**

ESCALA: **–** FORMATO: **A3**

REV./DATA: **–**

SUBST./REF.: **–**

PE-0S-0FIP-002-01

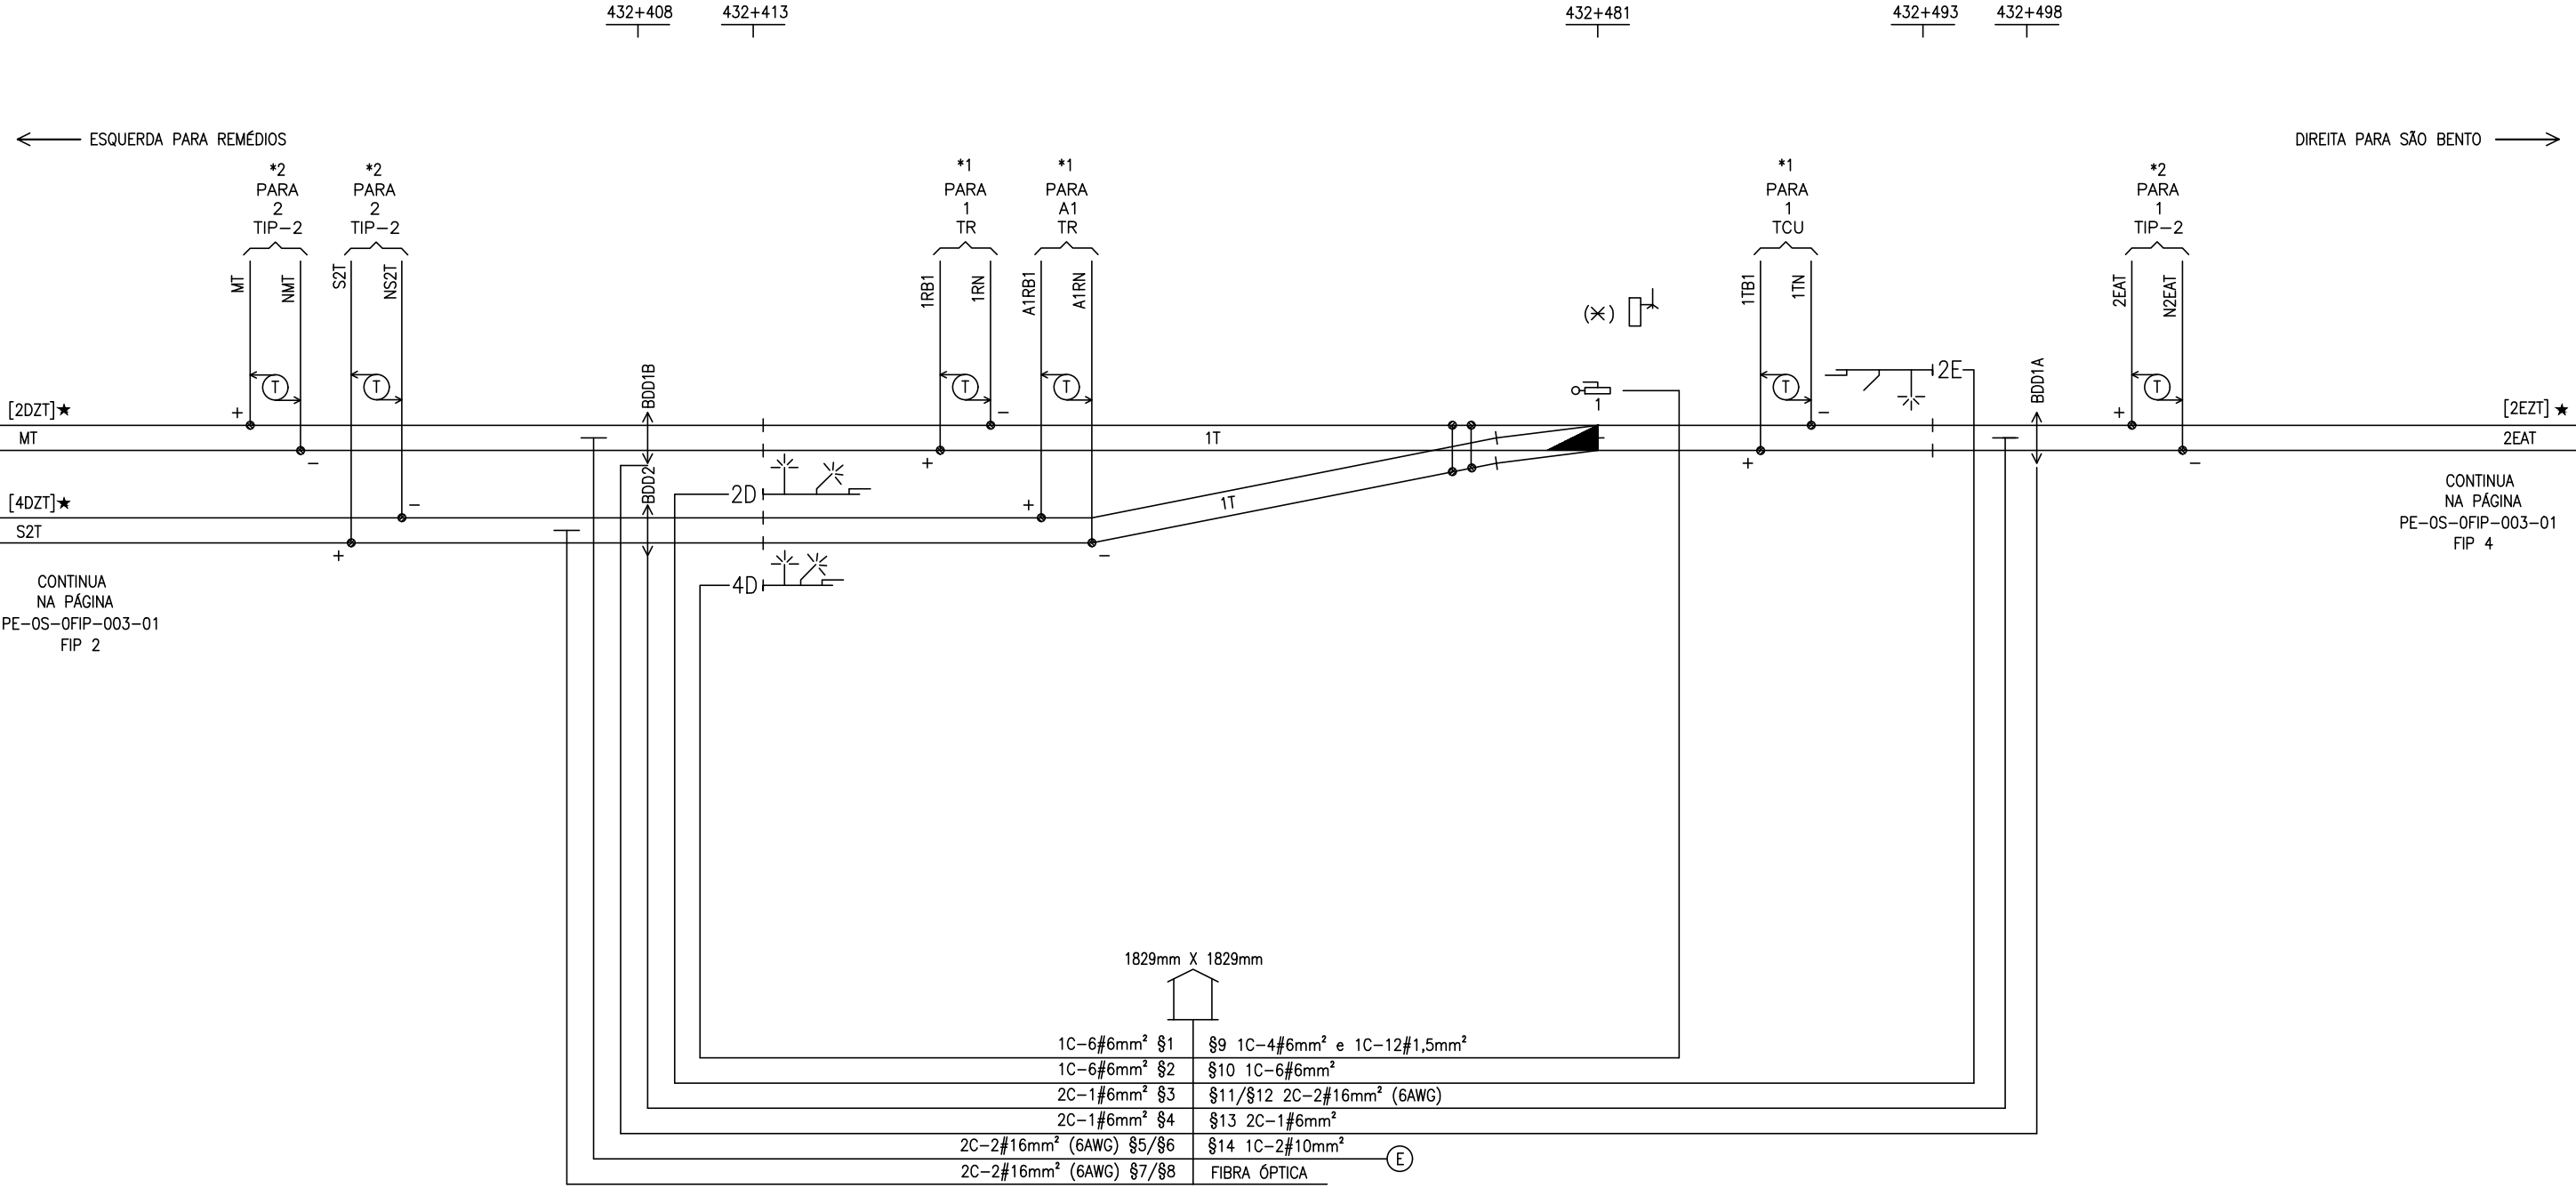

- OBSERVAÇÕES:
1. (X) = LOCALIZAÇÃO DA HOUSE
 2. ★ [XXXX] = NOMENCLATURA NO PROGRAMA DE APLICAÇÃO.
 3. *1 = VER FL. PE-OS-OFIP-012-01
 4. *2 = VER FL. PE-OS-OFIP-013-01
 5. § = VER FL. PE-OS-OFIP-004-01
 6. □ = POSTE COM ANTENA PLANO TERRA PARA DDvR


ANOTAÇÕES	A Operação dos circuitos e equipamentos aqui representados não podem ser completamente verificados senão após a sua instalação de modo a formar um sistema completo de sinalização ferroviária e ser devidamente submetido a "Testes de seleção de contatos(BREAKDOWN)" e "Testes operacionais de serviço"(Através de planilhas e fluxo de testes) antes de sua colocação em serviços normal definitivo. ENGENHARIA DE ELETROELETRÔNICA DE PROJETOS		TÍTULO DES.: LINHA DE SÃO PAULO PLANO DE VIA E SINAL COM CABOS – PVS ABR 15 ITAPETI – FIP	
			ENG.RESP.: HAROLDO ENNES	DATA: 08/03/2023
			PROJ.: MÁRCIO MOREIRA	ESCALA: – FORMATO: A3
			DES.PROJ.: ANTÔNIO LEAL	REV./DATA: –
			SUBST./REF.: –	

CONTROLE INTERNO DE PROJETOS GEPEE	DATA	FIRMA CONTRATADA: –	Nº ARQUIVO MRS: PE-OS-OFIP-003-01	
ELABORADOR: ANTÔNIO LEAL	08/03/2023			
REVISOR: MÁRCIO MOREIRA	22/03/2023			
APROVADOR: MARCOS REINH	31/03/2023			

FIP (3)

← ESQUERDA PARA REMÉDIOS

DIREITA PARA SÃO BENTO →

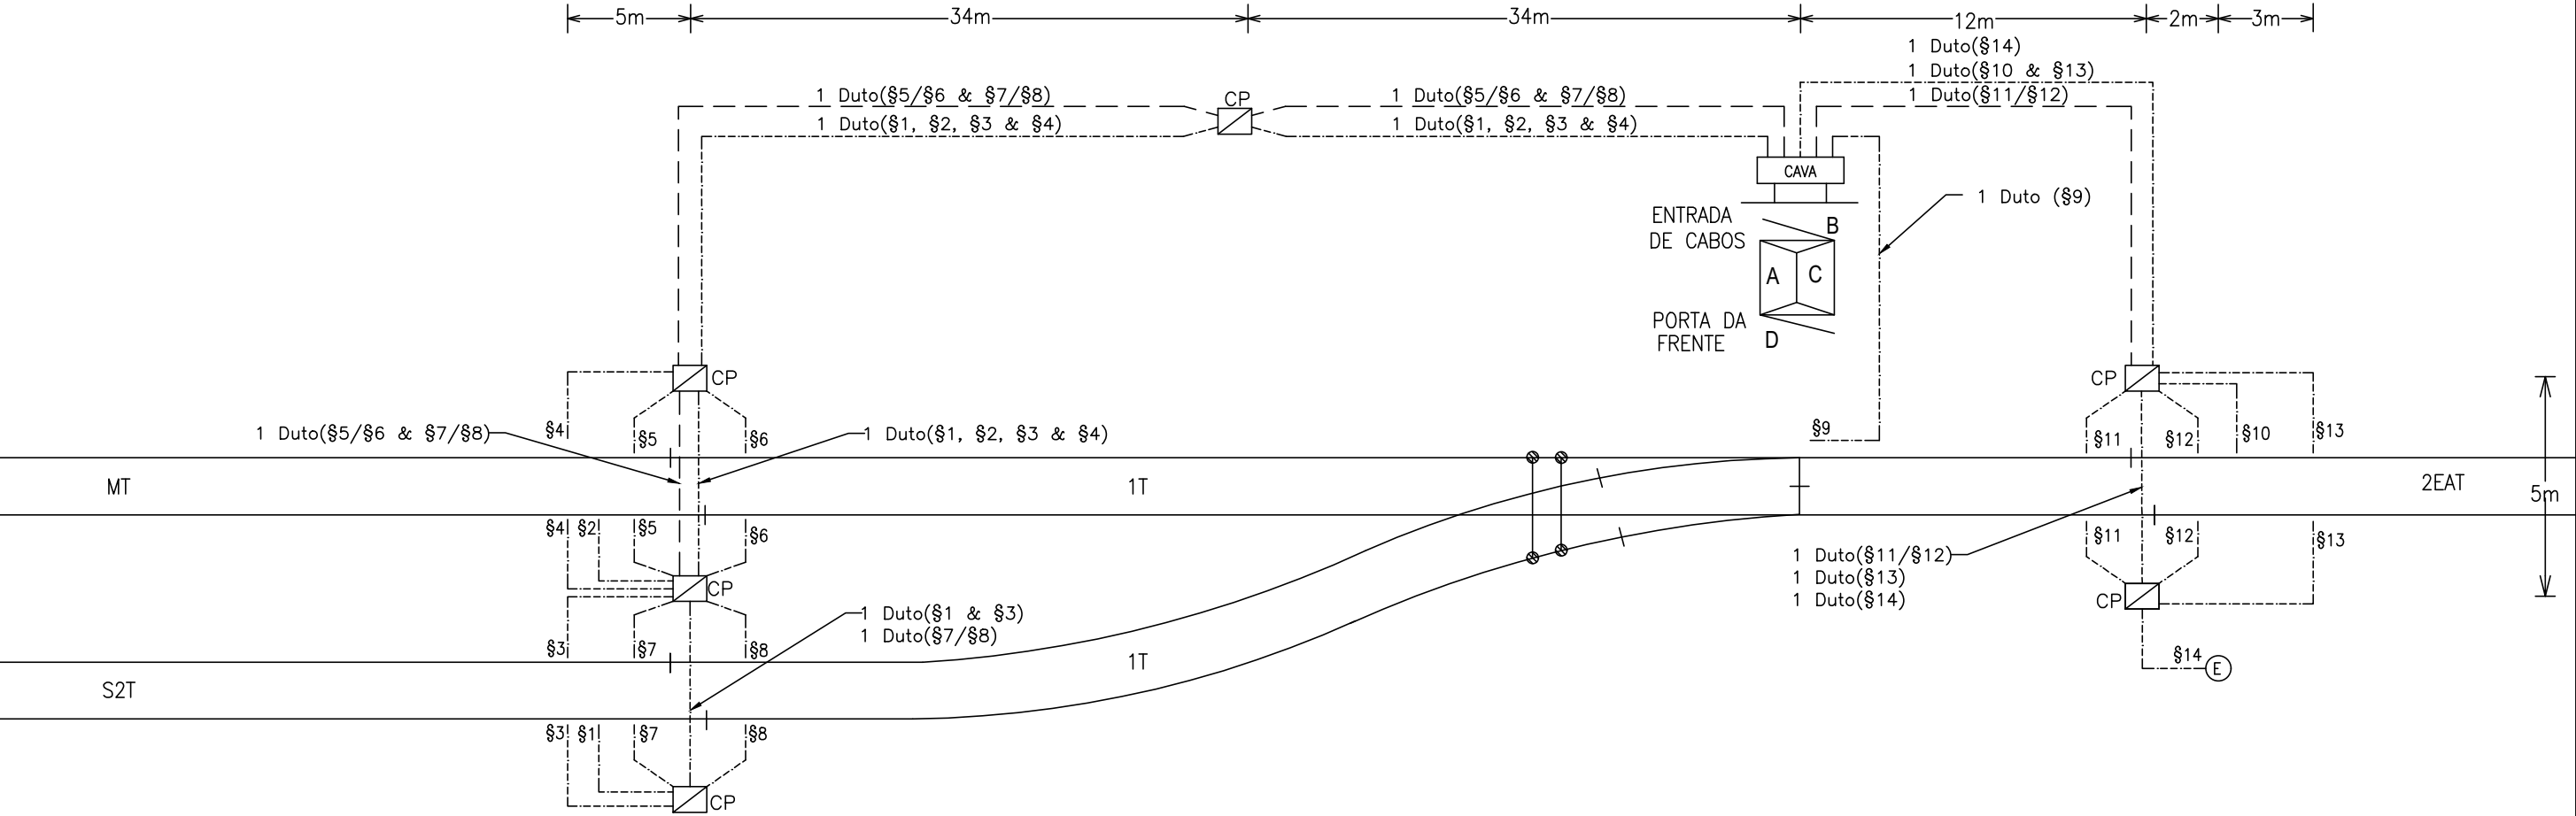

LEGENDA.:

— — — Duto Corrugado 4"
----- Duto Corrugado 2"

OBSERVAÇÃO:
1. DESENHO SEM ESCALA
2. § = VER FL. PE-OS-0FIP-003-01

ANOTAÇÕES

A Operação dos circuitos e equipamentos aqui representados não podem ser completamente verificados senão após a sua instalação de modo a formar um sistema completo de sinalização ferroviária e ser devidamente submetido a "Testes de seleção de contatos(BREAKDOWN)" e "Testes operacionais de serviço"(Através de planilhas e fluxo de testes) antes de sua colocação em serviços normal definitivo.
ENGENHARIA DE ELETROELETRÔNICA DE PROJETOS

CONTROLE INTERNO DE PROJETOS GEPEE	DATA
ELABORADOR: ANTÔNIO LEAL	08/03/2023
REVISOR: MÁRCIO MOREIRA	22/03/2023
APROVADOR: MARCOS REINH	31/03/2023



FIRMA CONTRATADA:

Nº ARQUIVO MRS:

TÍTULO DES.:
LINHA DE SÃO PAULO
REDE DE DUTOS E CABOS
ABR 15
ITAPETI – FIP


ENG.RESP.: HAROLDO ENNES	DATA: 08/03/2023
PROJ.: MÁRCIO MOREIRA	ESCALA: — FORMATO: A3
DES.PROJ.: ANTÔNIO LEAL	REV./DATA: —
SUBST./REF.: —	

PE-OS-0FIP-004-01

FIP (3)

← ESQUERDA PARA REMÉDIOS

DIREITA PARA SÃO BENTO →

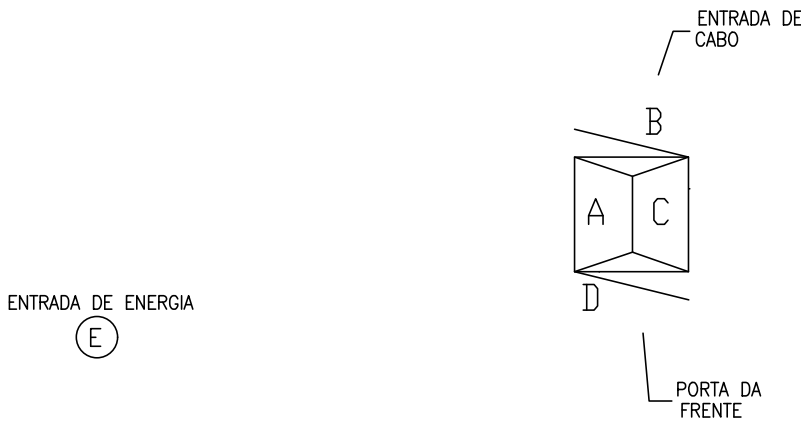

ATENÇÃO:

ESSA PLANTA DEVE SER ATUALIZADA PELO EXECUTOR DO PROJETO COM AS REFERÊNCIA DO ATERRAMENTO DOS ABRIGOS, POSICIONAMENTO DAS HASTES E A EQUIPOTENCIALIZAÇÃO CONFORME AS BUILT.

OBSERVAÇÕES:
1. DESENHO SEM ESCALA

ANOTAÇÕES

A Operação dos circuitos e equipamentos aqui representados não podem ser completamente verificados senão após a sua instalação de modo a formar um sistema completo de sinalização ferroviária e ser devidamente submetido a "Testes de seleção de contatos(BREAKDOWN)" e "Testes operacionais de serviço"(Através de planilhas e fluxo de testes) antes de sua colocação em serviços normal definitivo.
ENGENHARIA DE ELETROELETRÔNICA DE PROJETOS

CONTROLE INTERNO DE PROJETOS GEPEE	DATA
ELABORADOR: ANTÔNIO LEAL	08/03/2023
REVISOR: MÁRCIO MOREIRA	22/03/2023
APROVADOR: MARCOS REINH	31/03/2023



FIRMA CONTRATADA:

-

Nº ARQUIVO MRS:

TÍTULO DES.: LINHA DE SÃO PAULO
AS BUILT DE MALHA DE ATERRAMENTO
ABR 15
ITAPETI – FIP

ENG.RESP.: **HAROLDO ENNES**

PROJ.: **MÁRCIO MOREIRA**

DES.PROJ.: **ANTÔNIO LEAL**

PE-OS-OFIP-005-01

DATA: **08/03/2023**

ESCALA: -

FORMATO: **A3**

REV./DATA: -

SUBST./REF.: -

CONFIGURAÇÃO	
ITEM	CONFIGURAÇÃO
ID DO SITE	INDEFINIDO
ID DO CHASSI	81

CONFIGURAÇÃO DA PORTA DIAGNOSTICA CIO-1A	
ITEM	CONFIGURAÇÃO
TAXA DE BAUD	XXXXXXXX ✕
PARIDADE	NONE XXXXXXXX ✕
BITS DE DADOS	XXXXXXXX ✕
BITS DE PARADA	XXXXXXXX ✕
CONTROLE DE FLUXO	DISABLED XXXXXXXX ✕

TEMPORIZADORES VITAL	
NOME	CONFIGURAÇÃO
TEMPORIZADOR 2ELSR	XXXXXXXX ✕
TEMPORIZADOR 2DLSR	XXXXXXXX ✕
TEMPORIZADOR 4DLSR	XXXXXXXX ✕

INFORMAÇÕES DO APLICATIVO VITAL	
ITEM	CONFIGURAÇÃO
NOME	XXXXXXXX (✕✕1)
ÍNDICE	XXXXXXXX (✕✕1)
EPT CRC	XXXXXXXX (✕✕1)
EPT CHECKSUM	XXXXXXXX (✕✕1)

CONFIGURAÇÃO DO COMUNICAÇÃO VITAL				
ATTACHED REMOTES	NETWORK ID		IP ADDRESS	PORT
	LOCAL	REMOTE		
1	XXX	XXX	XXX	XXX (✕✕1)
2	XXX	XXX	XXX	XXX (✕✕1)
3	XXX	XXX	XXX	XXX (✕✕1)

CONFIGURAÇÃO VITAL		
#	NOME	ESTADO
1	BLOCO LIVRE DIP	FALSE XXXXXXXX

INFORMAÇÕES DO APLICATIVO NÃO VITAL	
ITEM	CONFIGURAÇÃO
NOME	XXXXXXXX (✕✕1)
ÍNDICE	XXXXXXXX (✕✕1)
EPT CRC	XXXXXXXX (✕✕1)
EPT CHECKSUM	XXXXXXXX (✕✕1)

CONFIGURAÇÃO SHUNTS VITAL		
#	NOME	ESTADO
1	BLOCO LIVRE DIP	INTACT XXXXXXXX

CONFIGURAÇÃO DO PROTOCOLO GENESYS E IP	
ITEM	CONFIGURAÇÃO
NOME DA ESTAÇÃO	FXX (XXXXX) (✕✕1)
ENDEREÇO DO GENESYS	XXXXXXXX (✕✕1)
UDP PORT	XXXXXXXX (✕✕1)
CTC GENESYS IP (ENET 1)	XXXXXXXX (✕✕1)
SUBNET MASK (ENET 1)	XXXXXXXX (✕✕1)
DHCP SERVER IP POOL START (ENET 1)	XXXXXXXX (✕✕1)
DHCP SERVER IP POOL END (ENET 1)	XXXXXXXX (✕✕1)
GATEWAY (ENET 1)	XXXXXXXX (✕✕1)
MAINT. IP (ENET 2)	XXXXXXXX (✕✕1)

OBSERVAÇÕES:

1. ✕ = STATUS ESTABELECIDOS/MODIFICADO USANDO O CDU-1. OS OUTROS SÃO MODIFICADOS USANDO O PROGRAMA ACE.

2. (✕✕1) = INFORMAÇÕES SERÃO ATUALIZADAS COM OS DADOS DO PROGRAMA APLICATIVO DO PROJETO APOS ELABORAÇÃO DO SOFTWARE

ANOTAÇÕES

A Operação dos circuitos e equipamentos aqui representados não podem ser completamente verificados senão após a sua instalação de modo a formar um sistema completo de sinalização ferroviária e ser devidamente submetido a "Testes de seleção de contatos(BREAKDOWN)" e "Testes operacionais de serviço"(Através de planilhas e fluxo de testes) antes de sua colocação em serviços normal definitivo.
ENGENHARIA DE ELETROELETRÔNICA DE PROJETOS



TÍTULO DES.: LINHA DE SÃO PAULO
PROGRAMA DO ELECTROLOGIXS
ABR 15
ITAPETI – FIP

CONTROLE INTERNO DE PROJETOS GEPEE	DATA
ELABORADOR: ANTÔNIO LEAL	08/03/2023
REVISOR: MÁRCIO MOREIRA	22/03/2023
APROVADOR: MARCOS REINH	31/03/2023

FIRMA CONTRATADA: -	ENG.RESP.: HAROLDO ENNES	DATA: 08/03/2023	
	PROJ.: MÁRCIO MOREIRA	ESCALA: -	FORMATO: A3
	DES.PROJ.: ANTÔNIO LEAL	REV./DATA: -	
N° ARQUIVO MRS: PE-0S-0FIP-006-01		SUBST./REF.: -	

(✕✕1)

GETS ELECTROLOGIXS WIU SETUP			
LOCATION NAME: (XXXXX)		CBTC NON-VITAL CONFIGURATION	
GENERAL ETHERNET SETTINGS		GENERAL WIU SETTINGS	
ETHERNET PORT 1		EXTERNAL TIME UPDATE TIMEOUT	XXXXXXXXXX
IP ADDRESS	XXXXXXXXXX	BEACON CONTINUOUS	XXXXXXXXXX
SUBNET MASK	XXXXXXXXXX	BROADCAST RATE	XXXXXXXXXX
ETHERNET PORT 2		BEACON BIT TIME	XXXXXXXXXX
IP ADDRESS	XXXXXXXXXX	BEACON END TIME	XXXXXXXXXX
SUBNET MASK	XXXXXXXXXX	MAX BEACON INTERVAL	XXXXXXXXXX
ELX APPLICATION DATA		BROADCAST ON CHANGE	XXXXXXXXXX
APPLICATION NAME	XXXXXXXXXX	EMP SETTINGS	
APPLICATION REV.	XXXXXXXXXX	SOURCE ADDRESS	XXXXXXXXXX
APP. CHECKSUM/CRC	XXXXXXXXXX	DESTINATION ADDRESS	XXXXXXXXXX
CBTC APPLICATION DATA		TTL (TIMED BEACON)	XXXXXXXXXX
APPLICATION NAME	XXXXXXXXXX	QOS (TIMED BEACON)	XXXXXXXXXX
APPLICATION REV.	XXXXXXXXXX	TTL (RESPONSE TO GET WIU STATUS)	XXXXXXXXXX
APPLICATION CRC	XXXXXXXXXX	QOS (RESPONSE TO GET WIU STATUS)	XXXXXXXXXX
WIU APPLICATION DATA		LRM MAX SECS TIME DIFFERENCE	XXXXXXXXXX
APPLICATION NAME	XXXXXXXXXX	NO TIME SYNC MESSAGE	XXXXXXXXXX
APPLICATION REV.	XXXXXXXXXX	CBTC TIME RE-SYNC MESSAGE	XXXXXXXXXX
APPLICATION CRC	XXXXXXXXXX	CLASS D SETTINGS	
		DESTINATION IP ADDRESS	XXXXXXXXXX
		DESTINATION IP PORT	XXXXXXXXXX
		KEEP ALIVE INTERVAL	XXXXXXXXXX
		KEEP ALIVE ACK TIMEOUT	XXXXXXXXXX
		DATA ACK ENABLED	XXXXXXXXXX
		DATA ACK TIMEOUT	XXXXXXXXXX
		DATA NAK RETRY LIMIT	XXXXXXXXXX
		CONNECTION ATTEMPT TIMEOUT	XXXXXXXXXX
		CONNECTION DELAY	XXXXXXXXXX
		CONNECTION RETRY LIMIT	XXXXXXXXXX
		RECONNECTION LIMIT	XXXXXXXXXX
		CBTC VITAL CONFIGURATION	
		WIU ADDRESS	XXXXXXXXXX
		TIME MESSAGES BEFORE SENDING WSM	XXXXXXXXXX
		TIME MESSAGE DEVIATION	XXXXXXXXXX
		IGNORED TIME DIFFERENCE	XXXXXXXXXX
		MAX SECS TIME CHANGE	XXXXXXXXXX
		MAX TIME CHANGE WITHIN MINS	XXXXXXXXXX

(✕✕1)

(✕✕1)

NOTA: _____

1. FOLHA RESERVADA PARA A FUTURA IMPLANTAÇÃO DO CBTC
OBSERVAÇÕES: _____

1. (✕✕1) = INFORMAÇÕES SERÃO ATUALIZADAS COM OS
DADOS DO PROGRAMA APLICATIVO DO PROJETO
APOS ELABORAÇÃO DO SOFTWARE

ANOTAÇÕES

A Operação dos circuitos e equipamentos aqui representados não podem ser completamente verificados senão após a sua instalação de modo a formar um sistema completo de sinalização ferroviária e ser devidamente submetido a "Testes de seleção de contatos(BREAKDOWN)" e "Testes operacionais de serviço"(Através de planilhas e fluxo de testes) antes de sua colocação em serviços normal definitivo.
ENGENHARIA DE ELETROELETRÔNICA DE PROJETOS



TÍTULO DES.: LINHA DE SÃO PAULO PROGRAMA CBTC DO ELECTROLOGIXS ABR 15 ITAPETI – FIP			
FIRMA CONTRATADA:		ENG.RESP.: HAROLDO ENNES	DATA: 08/03/2023
-		PROJ.: MÁRCIO MOREIRA	ESCALA: – FORMATO: A3
		DES.PROJ.: ANTÔNIO LEAL	REV./DATA: –
Nº ARQUIVO MRS: PE-0S-0FIP-007-01			SUBST./REF.: –

CONTROLE INTERNO DE PROJETOS GEPEE	DATA
ELABORADOR: ANTÔNIO LEAL	08/03/2023
REVISOR: MÁRCIO MOREIRA	22/03/2023
APROVADOR: MARCOS REINH	31/03/2023

MODULO DE COMUNICAÇÃO ENTRE CCO E ELECTROLOGIXS BITS DE COMUNICAÇÃO SERIAL								
CONTROLES DO CCO								
PALAVRA	1	2	3	4	5	6	7	8
1								
2								
3								
4								
INDICAÇÕES PARA O CCO								
PALAVRA	1	2	3	4	5	6	7	8
1								
2								
3								
4								
5								
6								

CONTROLES

INDICAÇÕES

OBSERVAÇÕES:

1. = INFORMAÇÕES SERÃO ATUALIZADAS COM OS
DADOS DO PROGRAMA APLICATIVO DO PROJETO
APOS ELABORAÇÃO DO SOFTWARE

ANOTAÇÕES

A Operação dos circuitos e equipamentos aqui representados não podem ser completamente verificados senão após a sua instalação de modo a formar um sistema completo de sinalização ferroviária e ser devidamente submetido a "Testes de seleção de contatos(BREAKDOWN)" e "Testes operacionais de serviço"(Através de planilhas e fluxo de testes) antes de sua colocação em serviços normal definitivo.
ENGENHARIA DE ELETROELETRÔNICA DE PROJETOS



TÍTULO DES.: LINHA DE SÃO PAULO
TABELA E DESCRIÇÃO DAS FUNÇÕES DE CONTROLE E INDICAÇÃO
ABR 15
ITAPETI – FIP

CONTROLE INTERNO DE PROJETOS GEPEE	DATA
ELABORADOR: ANTÔNIO LEAL	08/03/2023
REVISOR: MÁRCIO MOREIRA	22/03/2023
APROVADOR: MARCOS REINH	31/03/2023

FIRMA CONTRATADA:

–

Nº ARQUIVO MRS:

ENG.RESP.: **HAROLDO ENNES**

PROJ.: **MÁRCIO MOREIRA**

DES.PROJ.: **ANTÔNIO LEAL**




PE–OS–OFIP–008–01

DATA: **08/03/2023**

ESCALA: – FORMATO: **A3**

REV./DATA: –

SUBST./REF.: –

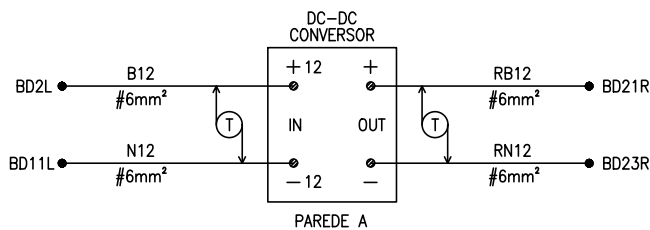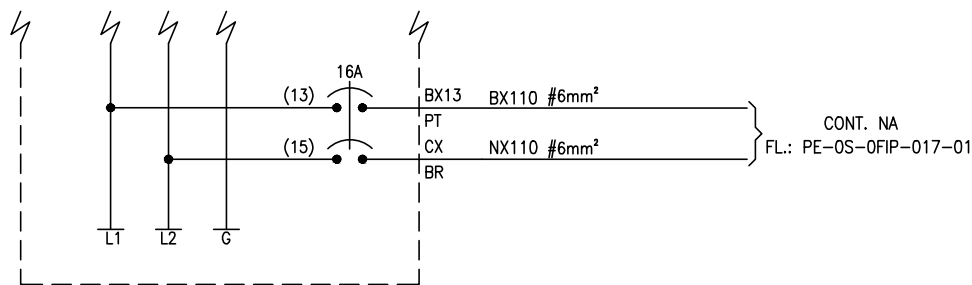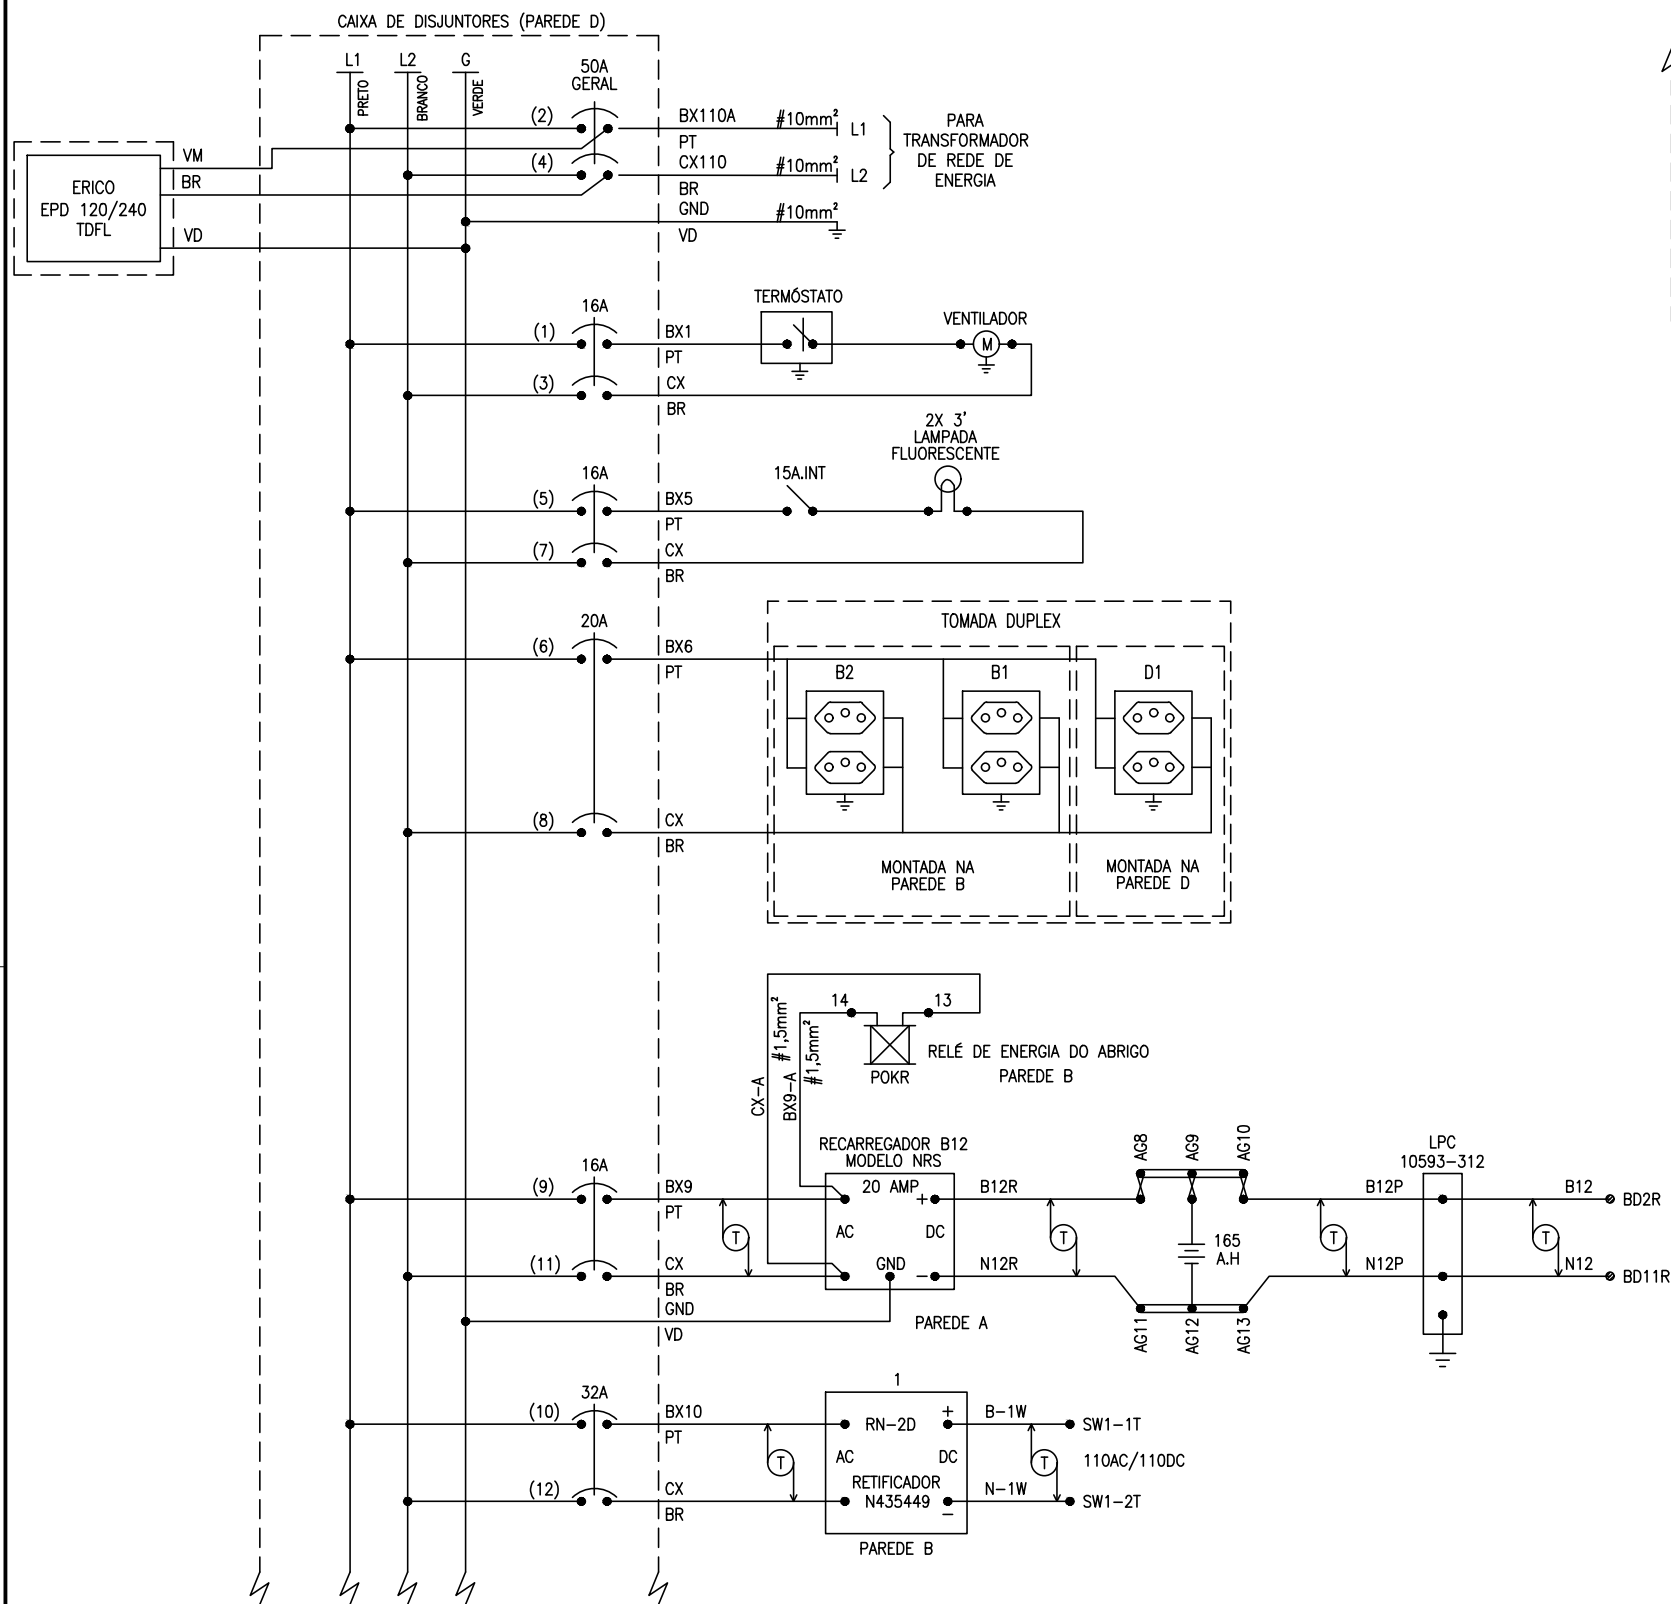

OBSERVAÇÃO:
1. (T) = TRANÇADO
2. CABOS A SEREM INSTALADOS DEVEM SER #6mm² EXCETO QUANDO INDICADO

ANOTAÇÕES

A Operação dos circuitos e equipamentos aqui representados não podem ser completamente verificados senão após a sua instalação de modo a formar um sistema completo de sinalização ferroviária e ser devidamente submetido a "Testes de seleção de contatos(BREAKDOWN)" e "Testes operacionais de serviço"(Através de planilhas e fluxo de testes) antes de sua colocação em serviços normal definitivo.
ENGENHARIA DE ELETROELETRÔNICA DE PROJETOS

CONTROLE INTERNO DE PROJETOS GEPEE	DATA
ELABORADOR: ANTÔNIO LEAL	08/03/2023
REVISOR: MÁRCIO MOREIRA	22/03/2023
APROVADOR: MARCOS REINH	31/03/2023




FIRMA CONTRATADA:
-

Nº ARQUIVO MRS:

TÍTULO DES.:
**LINHA DE SÃO PAULO
DISTRIBUIÇÃO DE ENERGIA
ABR 15
ITAPETI – FIP**

ENG.RESP.:	HAROLDO ENNES	DATA:	08/03/2023	
PROJ.:	MÁRCIO MOREIRA	ESCALA:	—	FORMATO: A3
DES.PROJ.:	ANTÔNIO LEAL	REV./DATA:	—	
PE-0S-0FIP-009-01		SUBST./REF.:	—	

PE-OS-OFIP-009-01

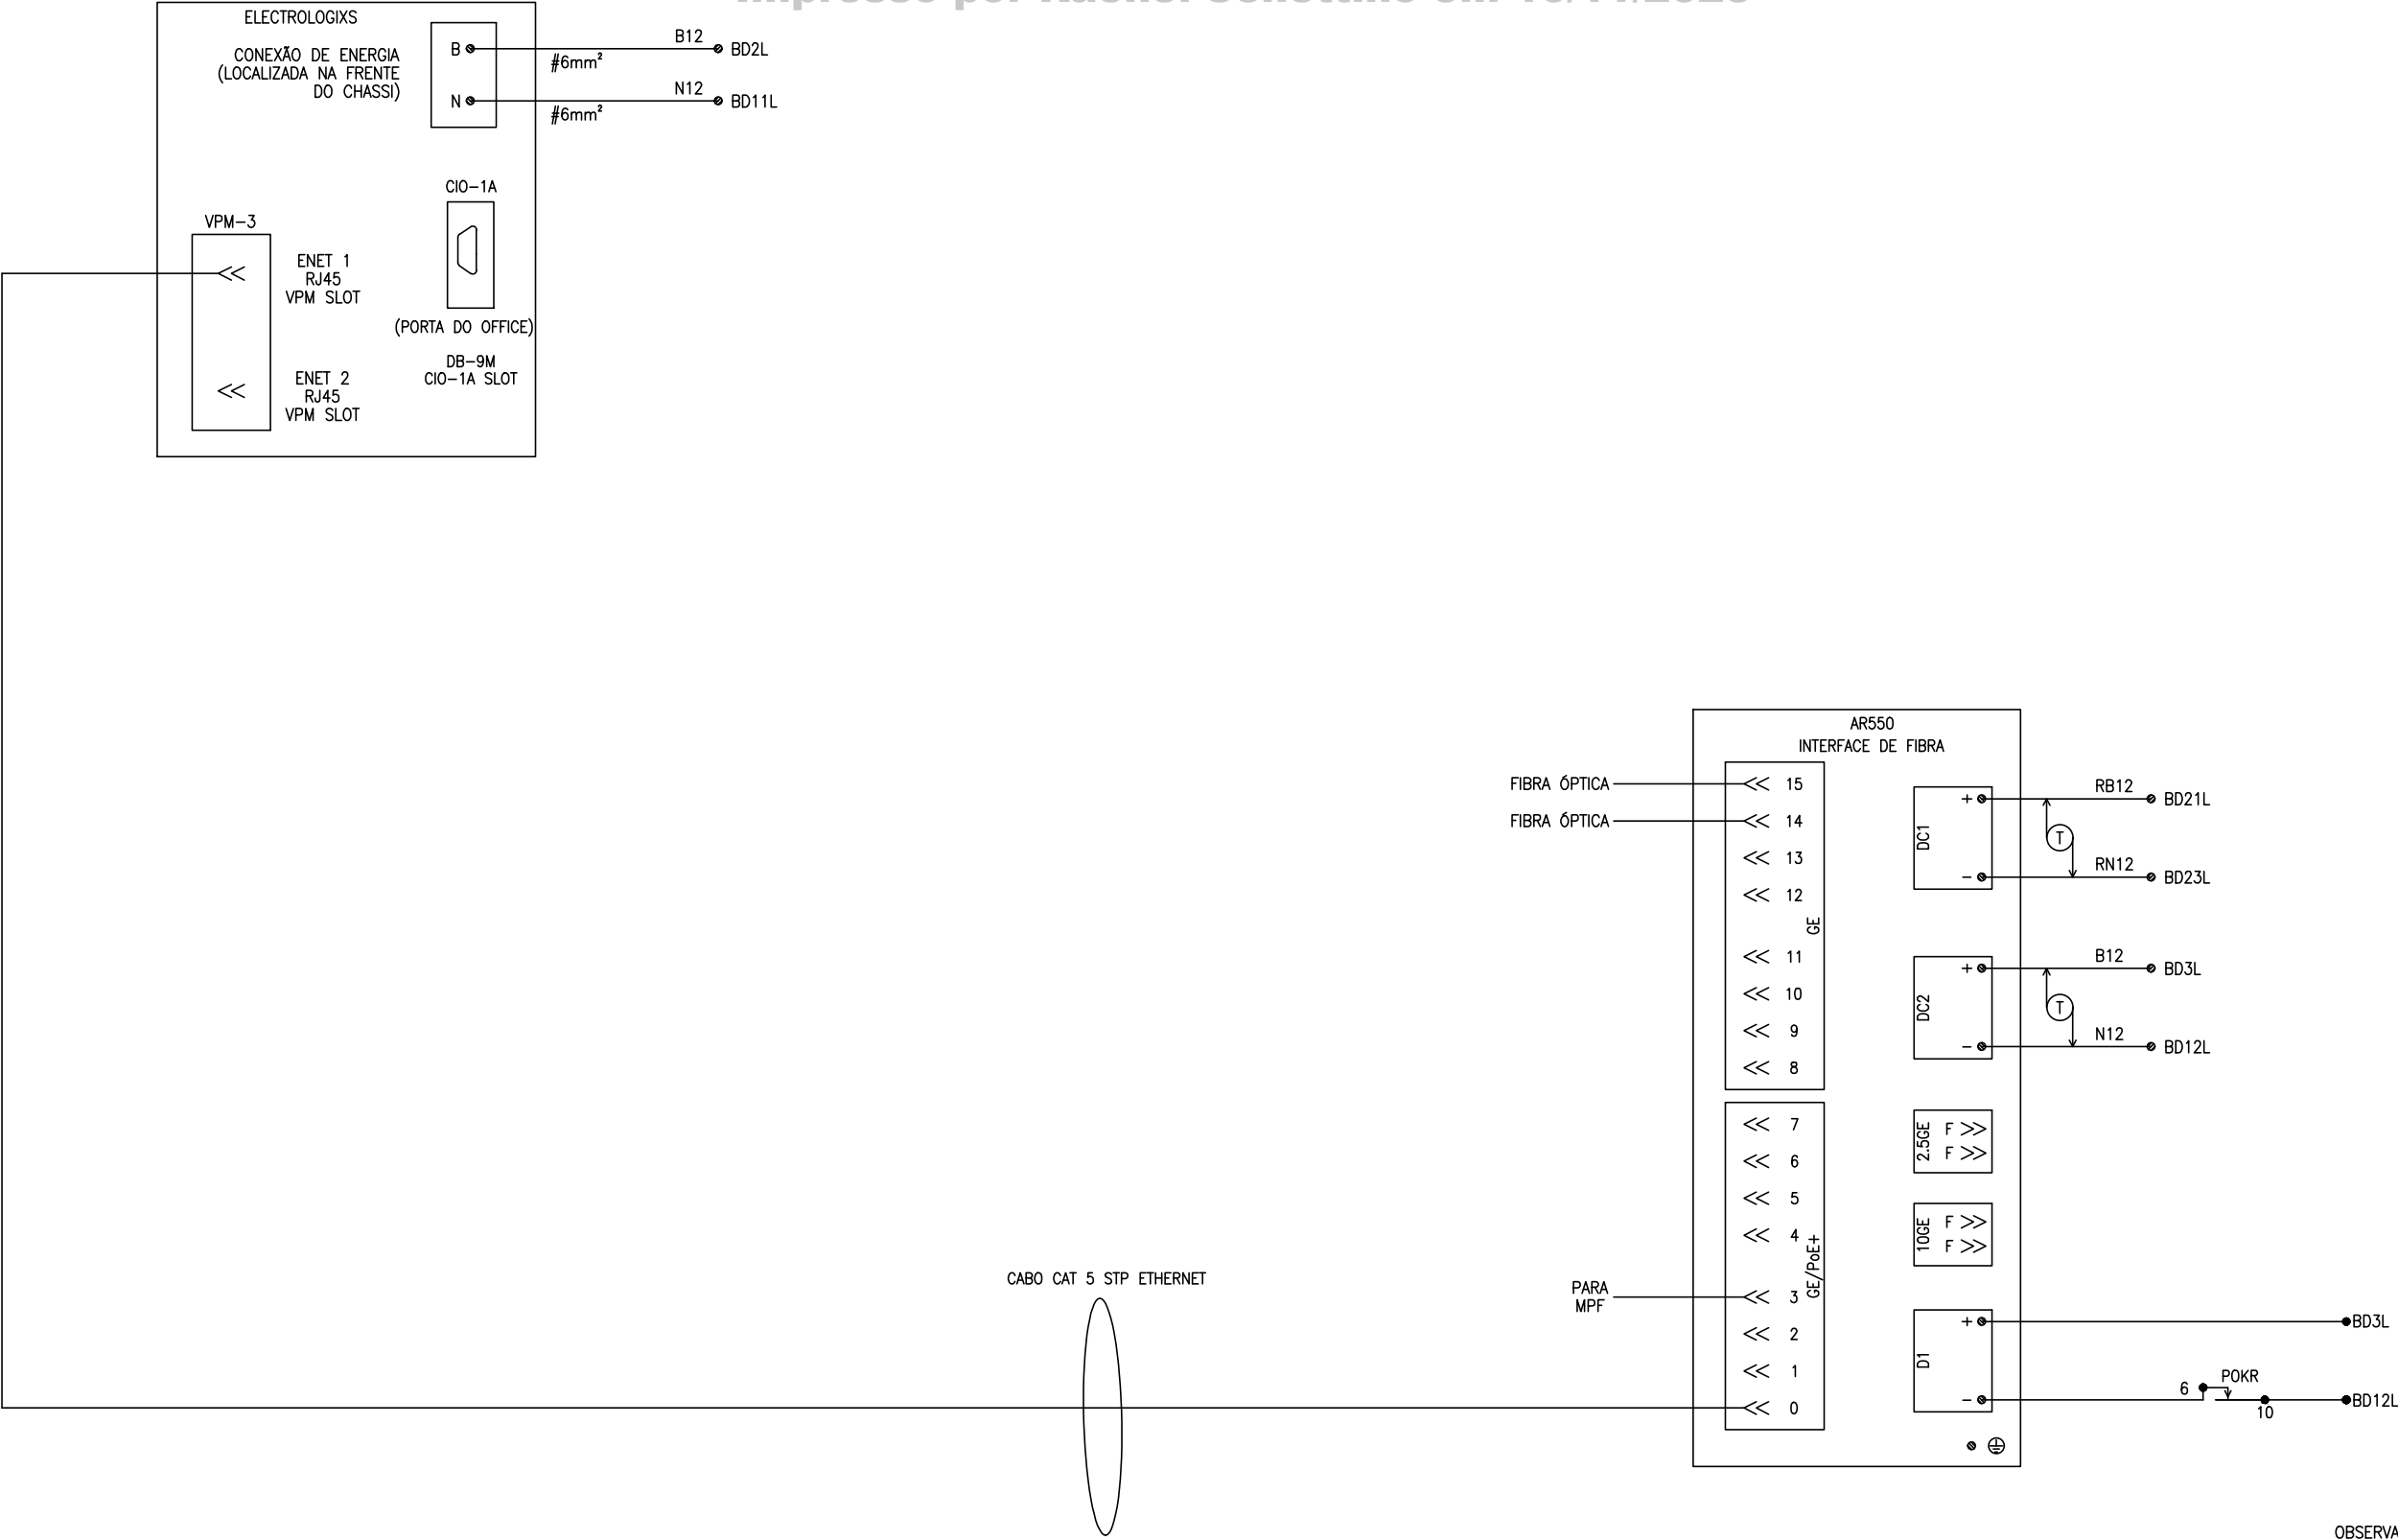

OBSERVAÇÕES:

1. (T) = TRANÇADO

2. CABOS A SEREM INSTALADOS DEVEM SER #1,5mm² EXCETO QUANDO INDICADO

ANOTAÇÕES

A Operação dos circuitos e equipamentos aqui representados não podem ser completamente verificados senão após a sua instalação de modo a formar um sistema completo de sinalização ferroviária e ser devidamente submetido a "Testes de seleção de contatos(BREAKDOWN)" e "Testes operacionais de serviço"(Através de planilhas e fluxo de testes) antes de sua colocação em serviços normal definitivo.
ENGENHARIA DE ELETROELETRÔNICA DE PROJETOS

CONTROLE INTERNO DE PROJETOS GEPEE	DATA
ELABORADOR: ANTÔNIO LEAL	08/03/2023
REVISOR: MÁRCIO MOREIRA	22/03/2023
APROVADOR: MARCOS REINH	31/03/2023




FIRMA CONTRATADA:

Nº ARQUIVO MRS:




TÍTULO DES.:
**LINHA DE SÃO PAULO
CIRCUITOS DE COMUNICAÇÃO DO ABRIGO
ABR 15
ITAPETI – FIP**

ENG.RESP.:	HAROLDO ENNES	DATA:	08/03/2023	
PROJ.:	MÁRCIO MOREIRA	ESCALA:	—	FORMATO: A3
DES.PROJ.:	ANTÔNIO LEAL	REV./DATA:	—	
-0S-0FIP-010-01		SUBST./REF.:	—	

PE-0S-0FIP-010-01

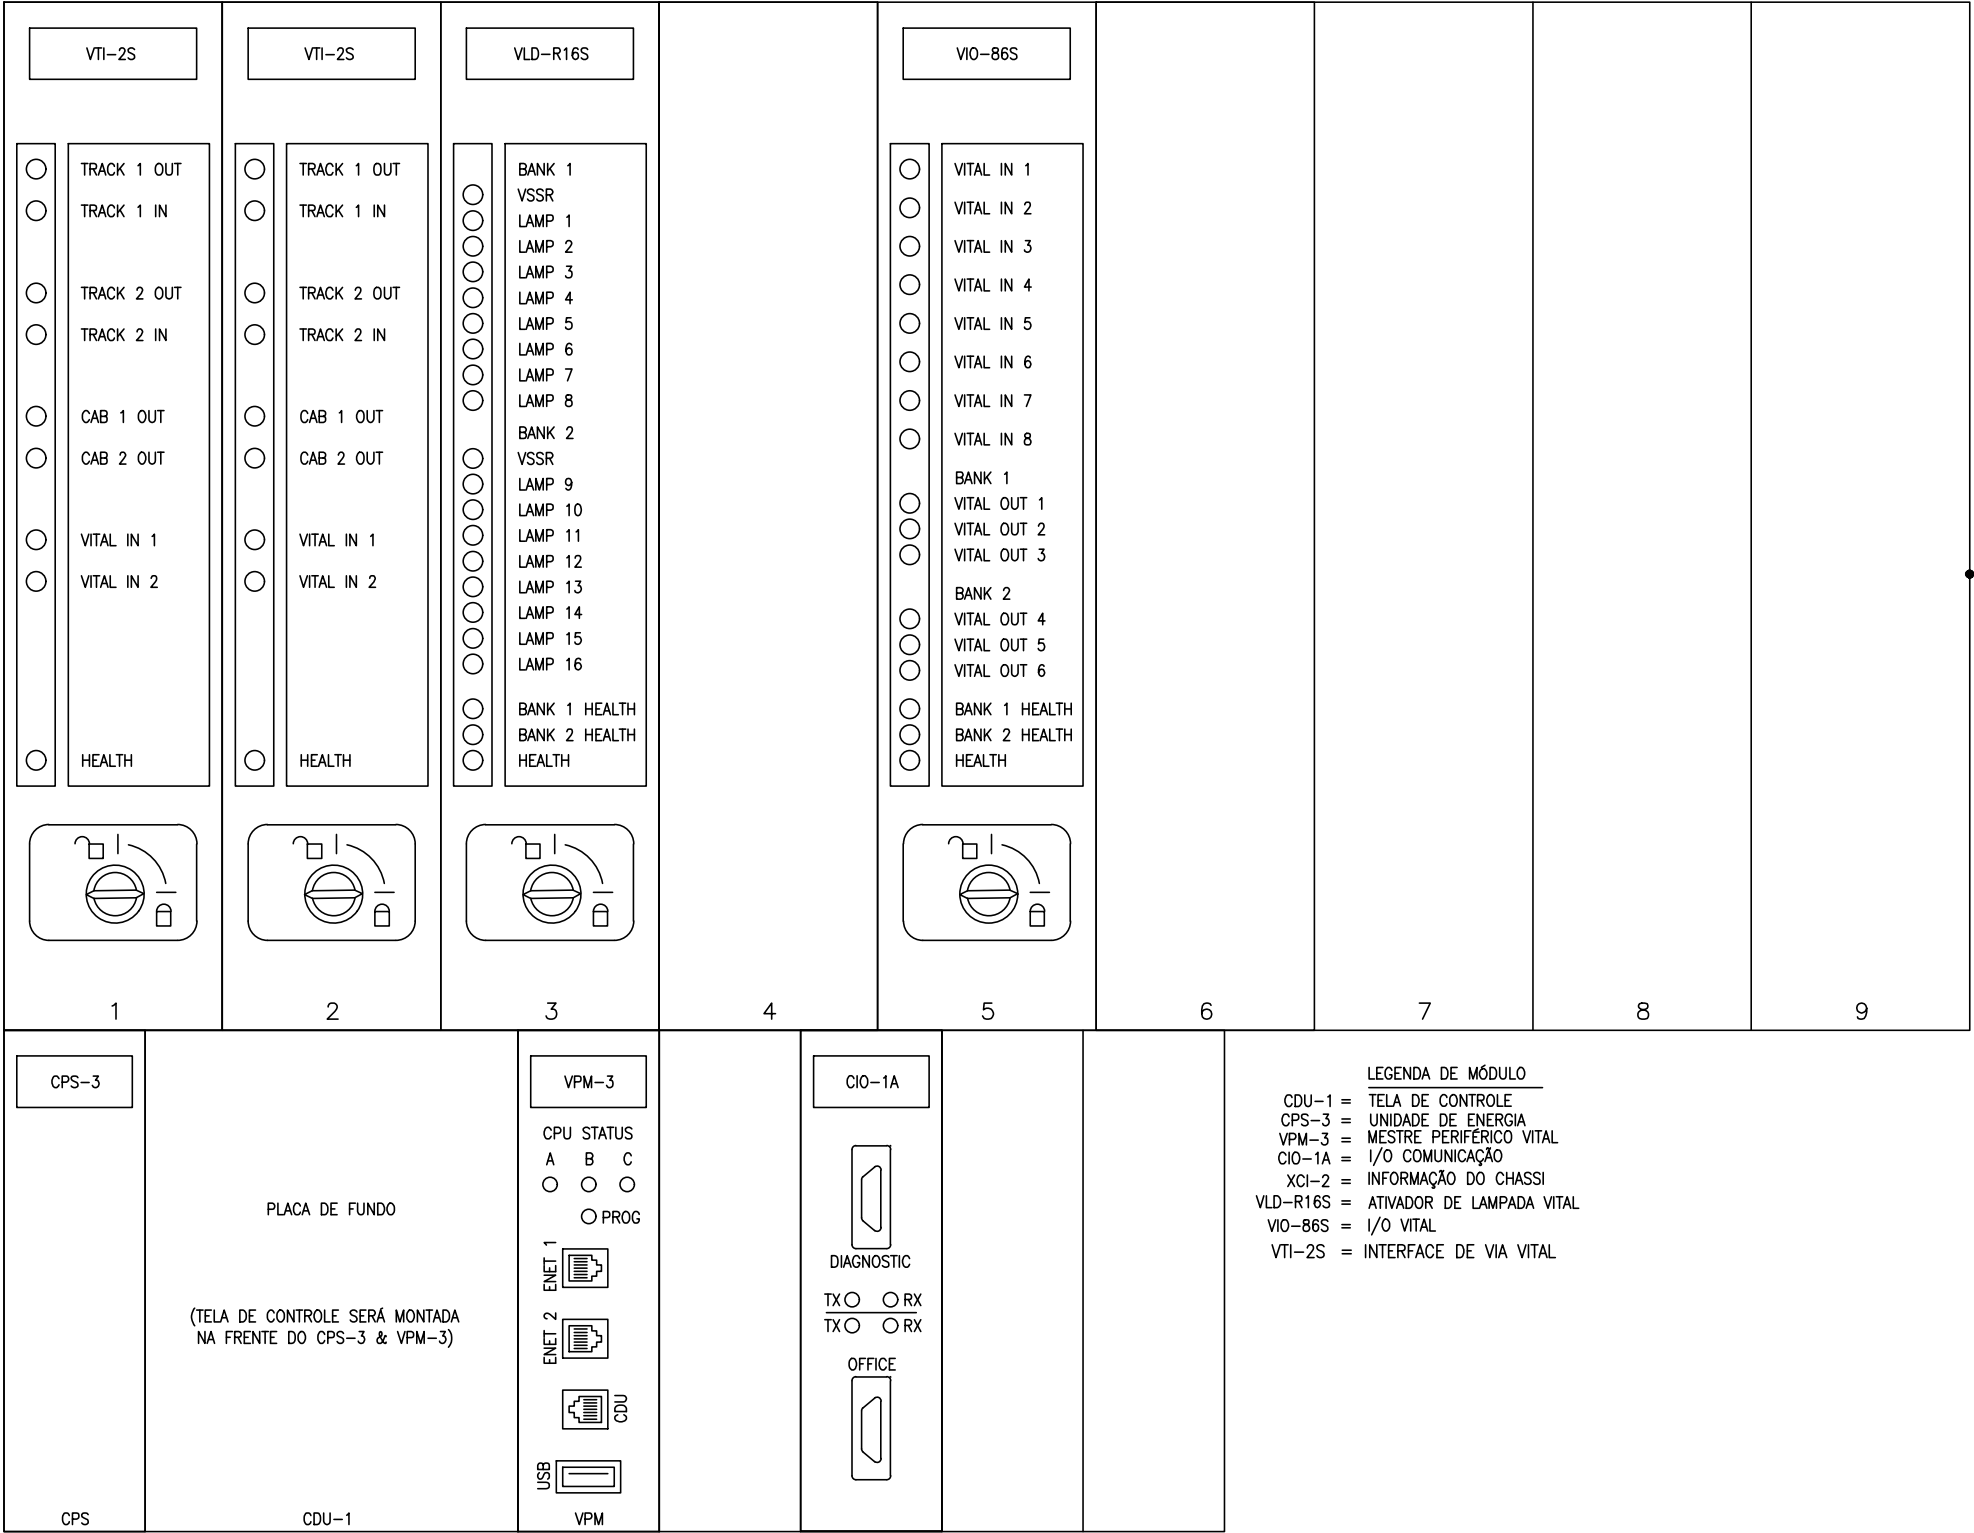

CIO-1A ATRIBUIÇÃO DOS PINOS PORTA DE DIAGNÓSTICO E DE OFFICE		
PINOS	SINAL	NOME DO SINAL
1	CD	CARRIER DETETOR
2	RX	RECEBE DADOS
3	TX	ENVIA DADOS
4	DTR	DTE
5	GND	SINAL COMUM DE RETORNO
6	DSR	DCE
7	RTS	PEDIDO DE ENVIO
8	CTS	LIVRE PARA ENVIAR
9	RI	INDICADOR DE TOQUE

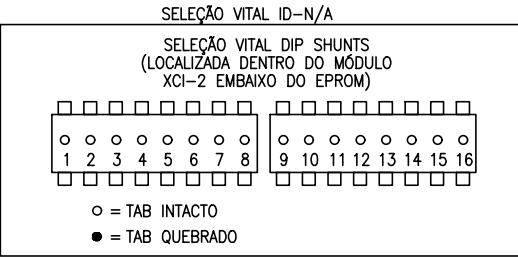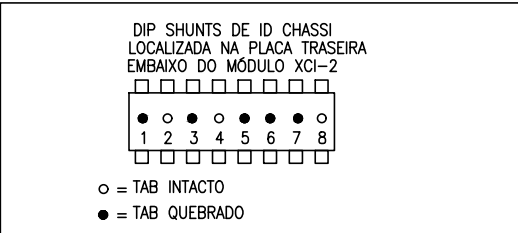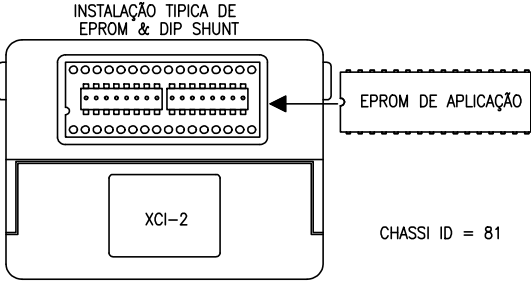

NOTA:
- As informações referente a programação serão incluídas posteriormente.

ANOTAÇÕES

A Operação dos circuitos e equipamentos aqui representados não podem ser completamente verificados senão após a sua instalação de modo a formar um sistema completo de sinalização ferroviária e ser devidamente submetido a "Testes de seleção de contatos(BREAKDOWN)" e "Testes operacionais de serviço"(Através de planilhas e fluxo de testes) antes de sua colocação em serviços normal definitivo.
ENGENHARIA DE ELETROELETRÔNICA DE PROJETOS


CONTROLE INTERNO DE PROJETOS GEPEE	DATA
ELABORADOR: ANTÔNIO LEAL	08/03/2023
REVISOR: MÁRCIO MOREIRA	22/03/2023
APROVADOR: MARCOS REINH	31/03/2023



TÍTULO DES.:
**LINHA DE SÃO PAULO
CONFIGURAÇÃO DO MODULO ELECTROLOGIXS
ABR 15
ITAPETI – FIP**

ENG.RESP.: HAROLDO ENNES	DATA: 08/06/2023
PROJ.: MÁRCIO MOREIRA	ESCALA: – FORMATO: A3
DES.PROJ.: ANTÔNIO LEAL	REV./DATA: –
SUBST./REF.: –	

Nº ARQUIVO MRS: **PE-0S-0FIP-011-01**

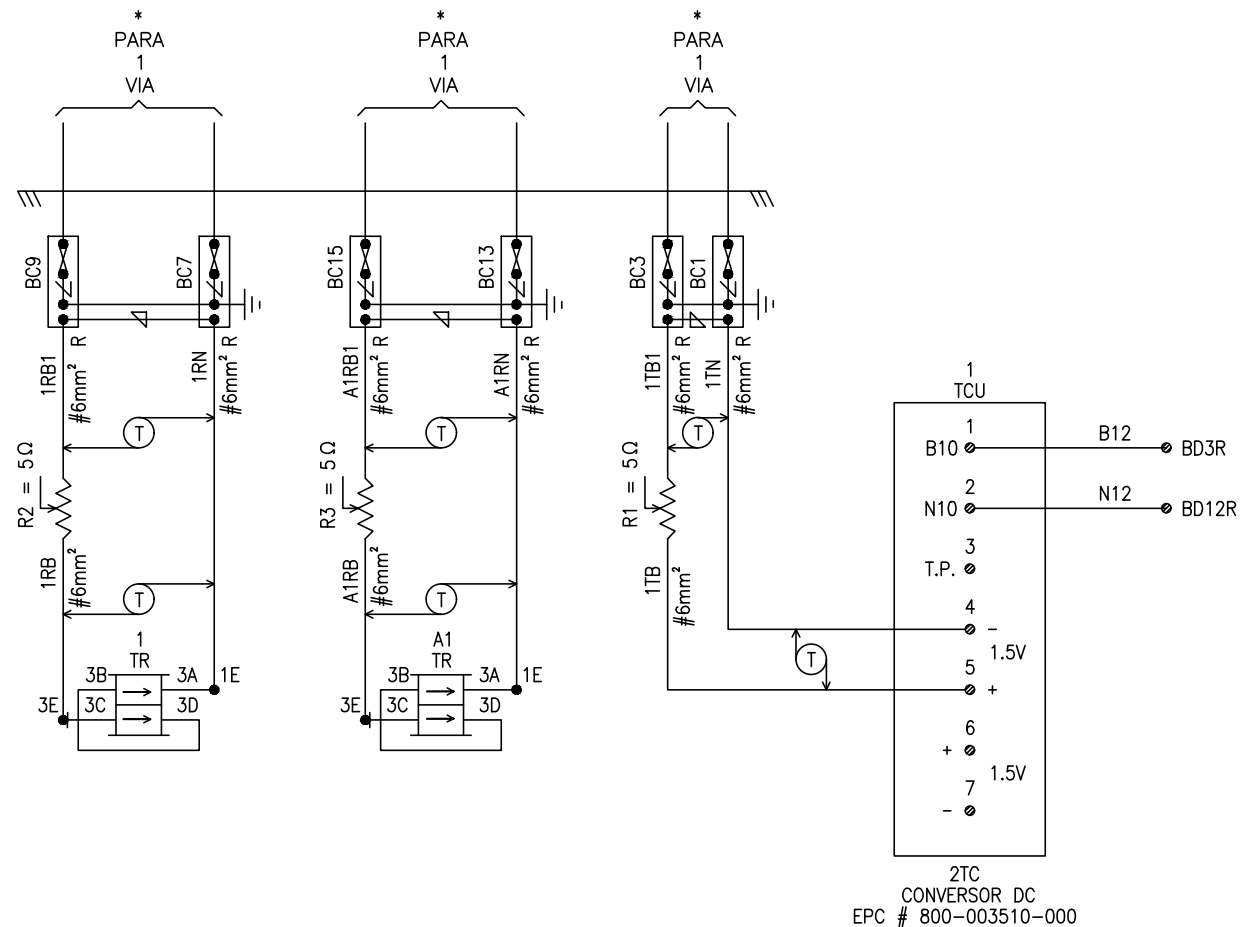

OBSERVAÇÕES:

1. (T) = TRANÇADO
2. ∠ = SUPRESSOR
3. Δ = EQUALIZADOR
4. TODOS CABOS DO ABRIGO #1,5mm EXCETO QUANDO INDICADO.
5. * = VER FL. PE-OS-OFIP-003-01

ANOTAÇÕES

A Operação dos circuitos e equipamentos aqui representados não podem ser completamente verificados senão após a sua instalação de modo a formar um sistema completo de sinalização ferroviária e ser devidamente submetido a "Testes de seleção de contatos(BREAKDOWN)" e "Testes operacionais de serviço"(Através de planilhas e fluxo de testes) antes de sua colocação em serviços normal definitivo.


ENGENHARIA DE ELETROELETRÔNICA DE PROJETOS



TÍTULO DES.:

LINHA DE SÃO PAULO
 CIRCUITOS DE VIA
 ABR 15
 ITAPETI – FIP

CONTROLE INTERNO DE PROJETOS GEPEE	DATA	FIRMA CONTRATADA:	ENG.RESP.: HAROLDO ENNES	DATA:	08/03/2023	
ELABORADOR: ANTÔNIO LEAL	08/03/2023	—	PROJ.: MÁRCIO MOREIRA	ESCALA:	—	FORMATO: A3
REVISOR: MÁRCIO MOREIRA	22/03/2023		DES.PROJ.: ANTÔNIO LEAL	REV./DATA:	—	
APROVADOR: MARCOS REINH	31/03/2023	N° ARQUIVO MRS: PE-0S-0FIP-012-01			SUBST./REF.: —	

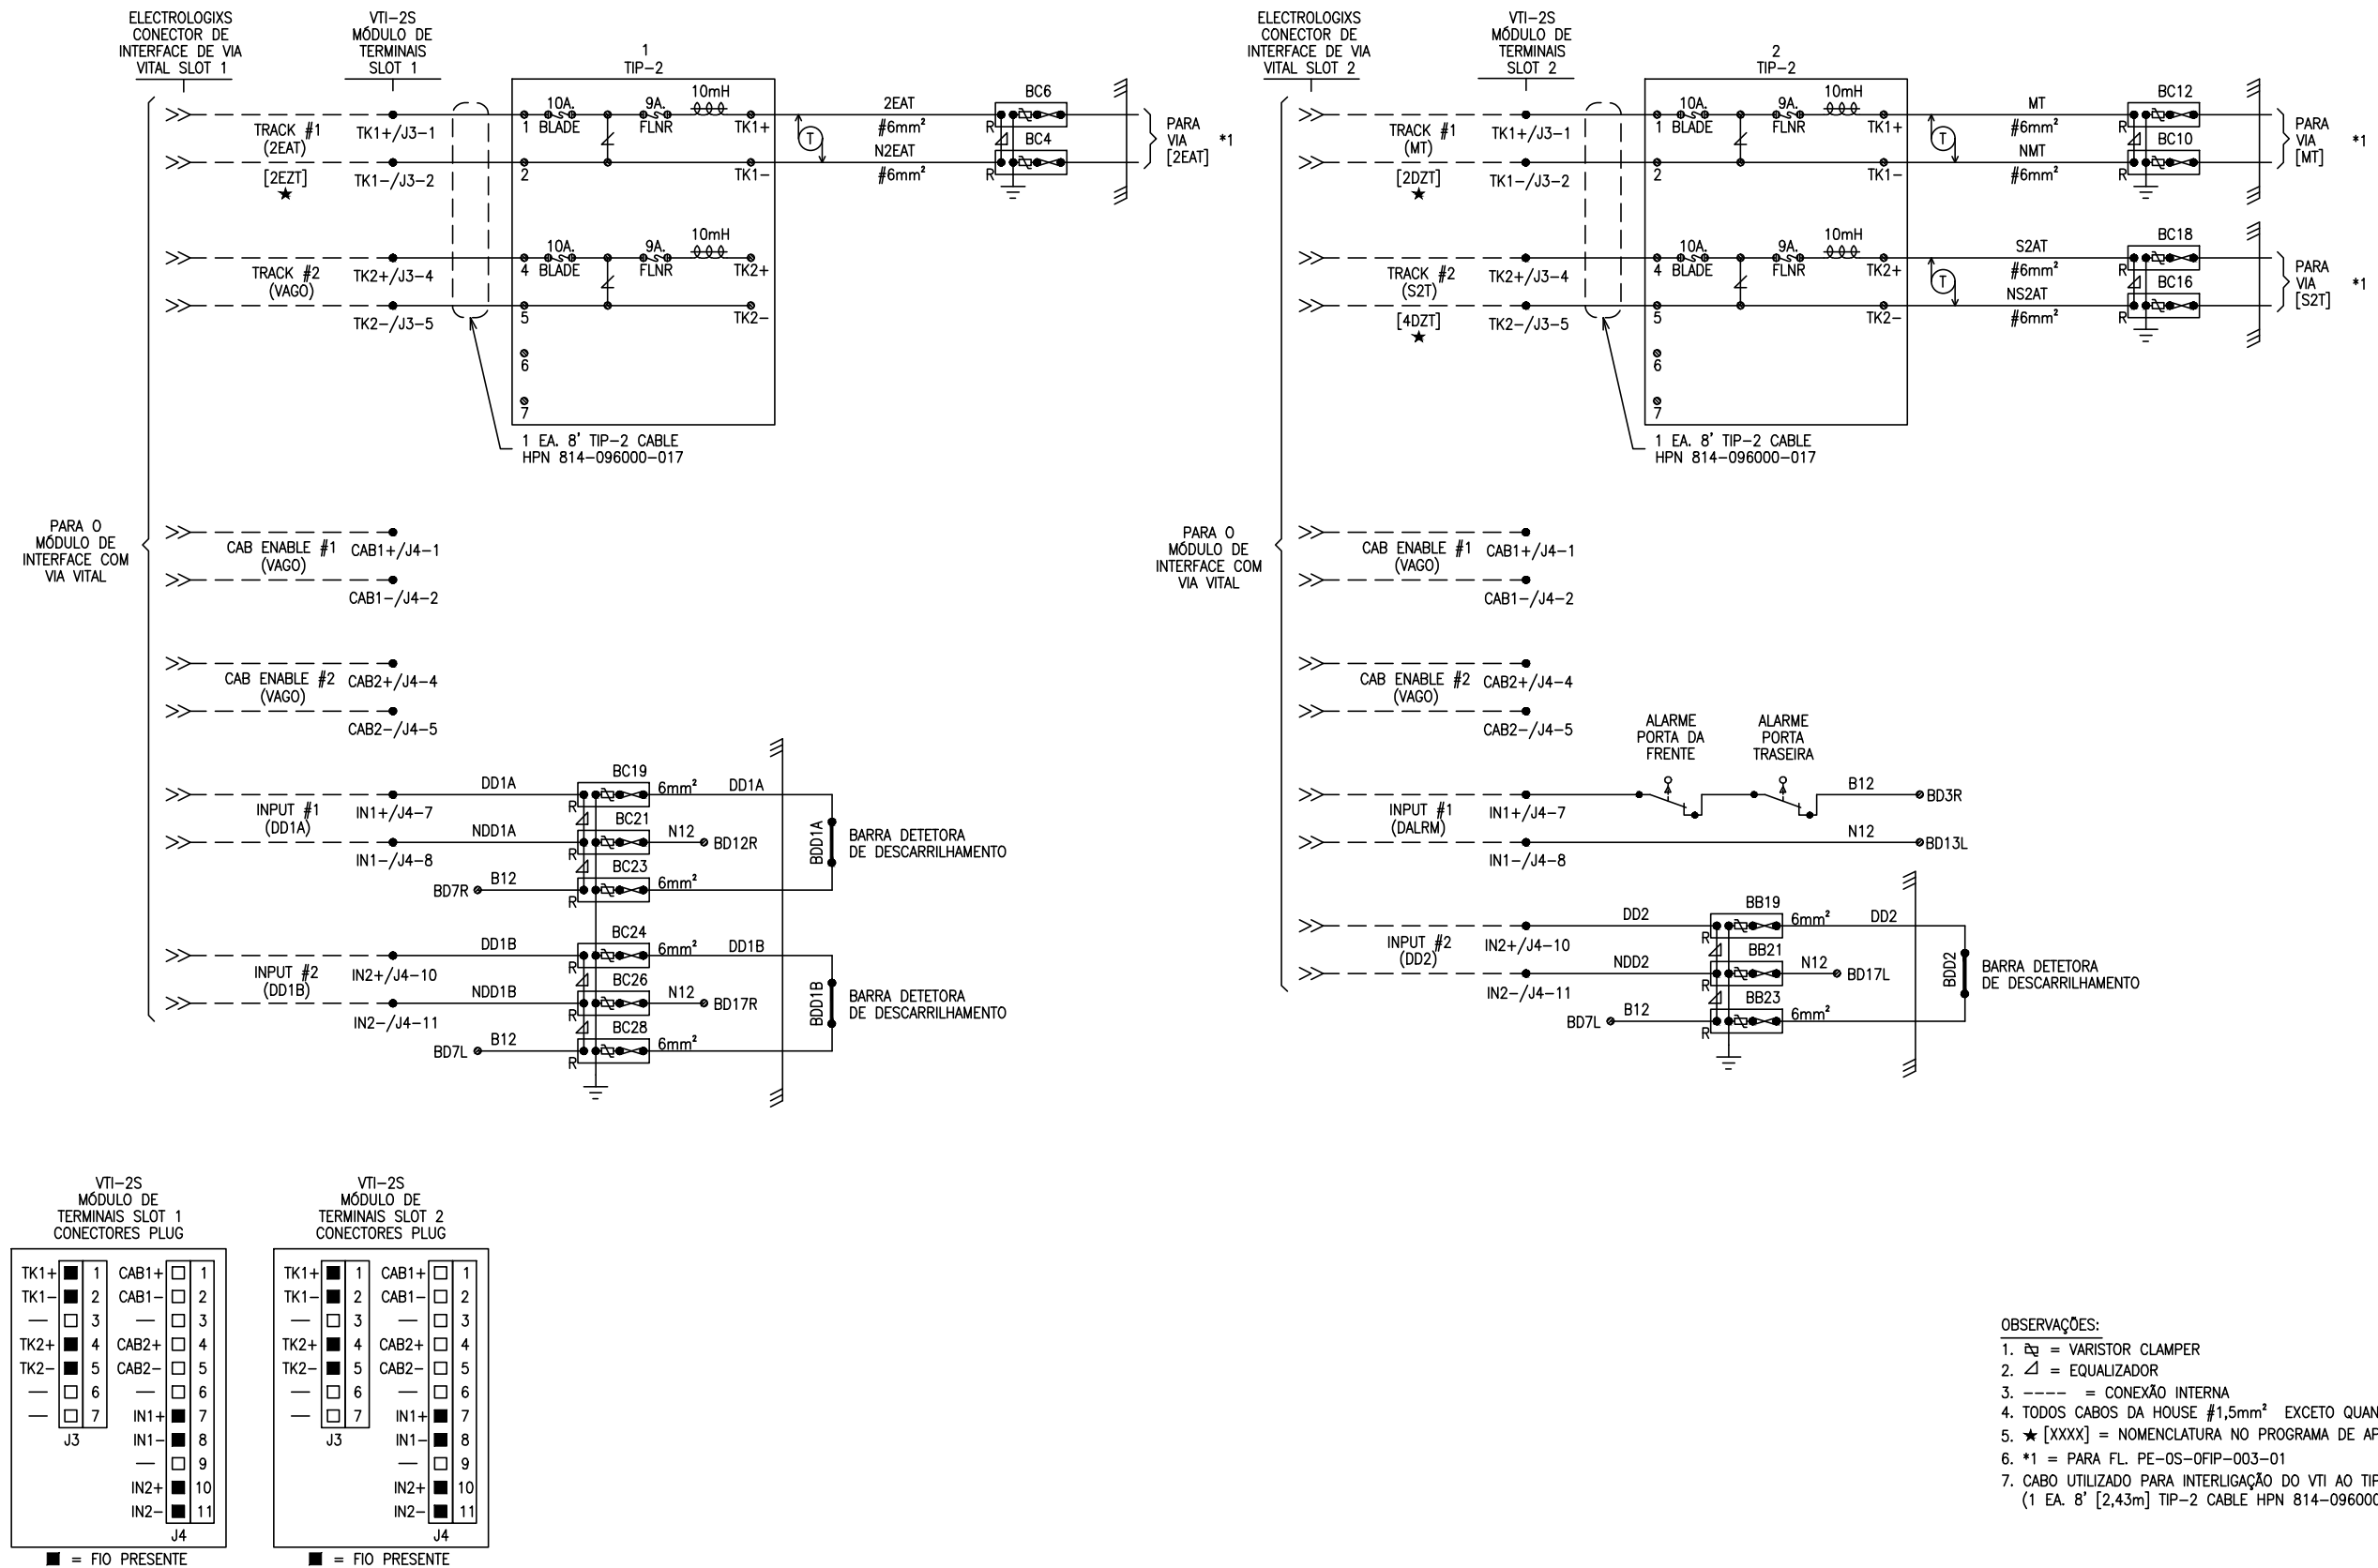

ANOTAÇÕES

A Operação dos circuitos e equipamentos aqui representados não podem ser completamente verificados senão após a sua instalação de modo a formar um sistema completo de sinalização ferroviária e ser devidamente submetido a "Testes de seleção de contatos(BREAKDOWN)" e "Testes operacionais de serviço"(Através de planilhas e fluxo de testes) antes de sua colocação em serviços normal definitivo.

ENGENHARIA DE ELETROELETRÔNICA DE PROJETOS



TÍTULO DES.:

LINHA DE SÃO PAULO
I/O DE VIA E VITAL DO ELECTROLOGIXS
ABR 15
ITAPETI – FIP

CONTROLE INTERNO DE PROJETOS GEPEE	DATA
ELABORADOR: ANTÔNIO LEAL	08/03/2023
REVISOR: MÁRCIO MOREIRA	22/03/2023
APROVADOR: MARCOS REINH	31/03/2023

FIRMA CONTRATADA:

-

Nº ARQUIVO MRS:

PE-OS-OFIP-013-01ENG.RESP.: **HAROLDO ENNES**DATA: **08/03/2023**PROJ.: **MÁRCIO MOREIRA**ESCALA: **-**FORMATO: **A3**DES.PROJ.: **ANTÔNIO LEAL**REV./DATA: **-**SUBST./REF.: **-**

DIP SWITCH DE CONFIGURAÇÃO (INTERNO DO EQUIPAMENTO)




- 1- ON= DET. QUEDA BARREIRA/ OFF= DET. DE DESCARRILHAMENTO
2- ON= VANDALISMO DESATIVADO/ OFF= VANDALISMO ATIVADO
3- ON= FALTA AC DESATIVADO/ OFF= FALTA AC ATIVADO
4- ON= 5 CANAIS/ OFF= 3 CANAIS
5- ON= 2 BARRAS/ OFF= 1 BARRA
6- ON= SIRENE HABILITADA/ OFF= SIRENE DESABILITADA

SIR- Saída para acionamento de sirene externa
FAC- Entrada sensor de falta de AC
VDL- Entrada sensor de vandalismo
BAR1- Entrada para barra 1 de descarrilhamento (ligação direta na barra)- Não necessita de sensor
BAR2- Entrada para barra 2 de descarrilhamento (ligação direta na barra)- Não necessita de sensor
BAT- Entrada para monitorar a tensão da bateria do detetor

OBSERVAÇÕES IMPORTANTES:
1- A única entrada de alimentação é de 12V
2- Se não tiver FAC e ou VDL, basta configurar por DIP SWITCH internamente (não necessita de jumper externo)
3- Usar 1 barra ou 2 barras para descarrilhamento, também é configurado pela DIP SWITCH
4- O valor da tensão da bateria é informado por áudio quando feito um Call Alert.

DADOS DO RÁDIO					
REPETIDORA XXXX	DISPLAY RÁDIO	RÁDIO TX	RAN	INDIVIDUAL LIST ID	TALKGROUP ID
XXXX	TT XX INV	XXXX	XXXX	XXXX	XXXX
XXXX	TT XX	XXXX	XXXX	XXXX	XXXX
XXXX	MAN	XXXX	XXXX	XXXX	XXXX
FREQUÊNCIA DE AJUSTE DA ANTENA = 160MHz					
POTÊNCIA TX RÁDIO = 40W - REFLETIDA > 2W					

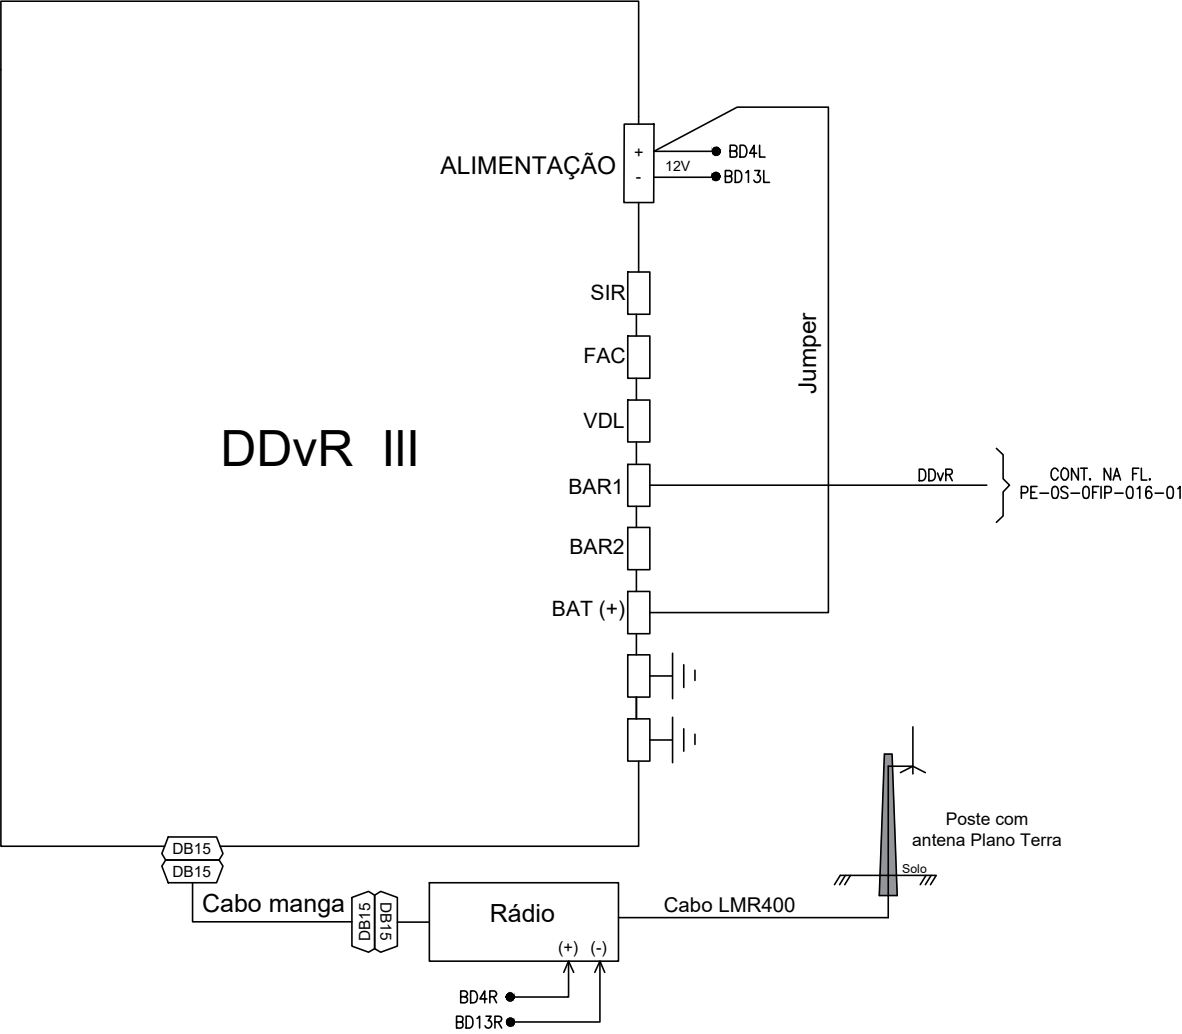

OBSERVAÇÕES:
1. (x)x(1) = INFORMAÇÕES SERÃO ATUALIZADAS COM OS DADOS DE CONFIGURAÇÕES DO RÁDIO COM A IMPLANTAÇÃO

ANOTAÇÕES

A Operação dos circuitos e equipamentos aqui representados não podem ser completamente verificados senão após a sua instalação de modo a formar um sistema completo de sinalização ferroviária e ser devidamente submetido a "Testes de seleção de contatos(BREAKDOWN)" e "Testes operacionais de serviço"(Através de planilhas e fluxo de testes) antes de sua colocação em serviços normal definitivo.
ENGENHARIA DE ELETROELETRÔNICA DE PROJETOS





TÍTULO DES.:
LINHA DE SÃO PAULO
DIAGRAMA DO DETECTOR DE DESCARRILHAMENTO VIA RÁDIO
ABR 15
ITAPETI - FIP

CONTROLE INTERNO DE PROJETOS GEPEE	DATA
ELABORADOR: ANTÔNIO LEAL	08/03/2023
REVISOR: MÁRCIO MOREIRA	22/03/2023
APROVADOR: MARCOS REINH	31/03/2023

FIRMA CONTRATADA:	ENG.RESP.: HAROLDO ENNES	DATA: 08/03/2023
-	PROJ.: MÁRCIO MOREIRA	ESCALA: -
	DES.PROJ.: ANTÔNIO LEAL	FORMATO: A3
Nº ARQUIVO MRS:	SUBST./REF.: -	

PE-OS-OFIP-014-01

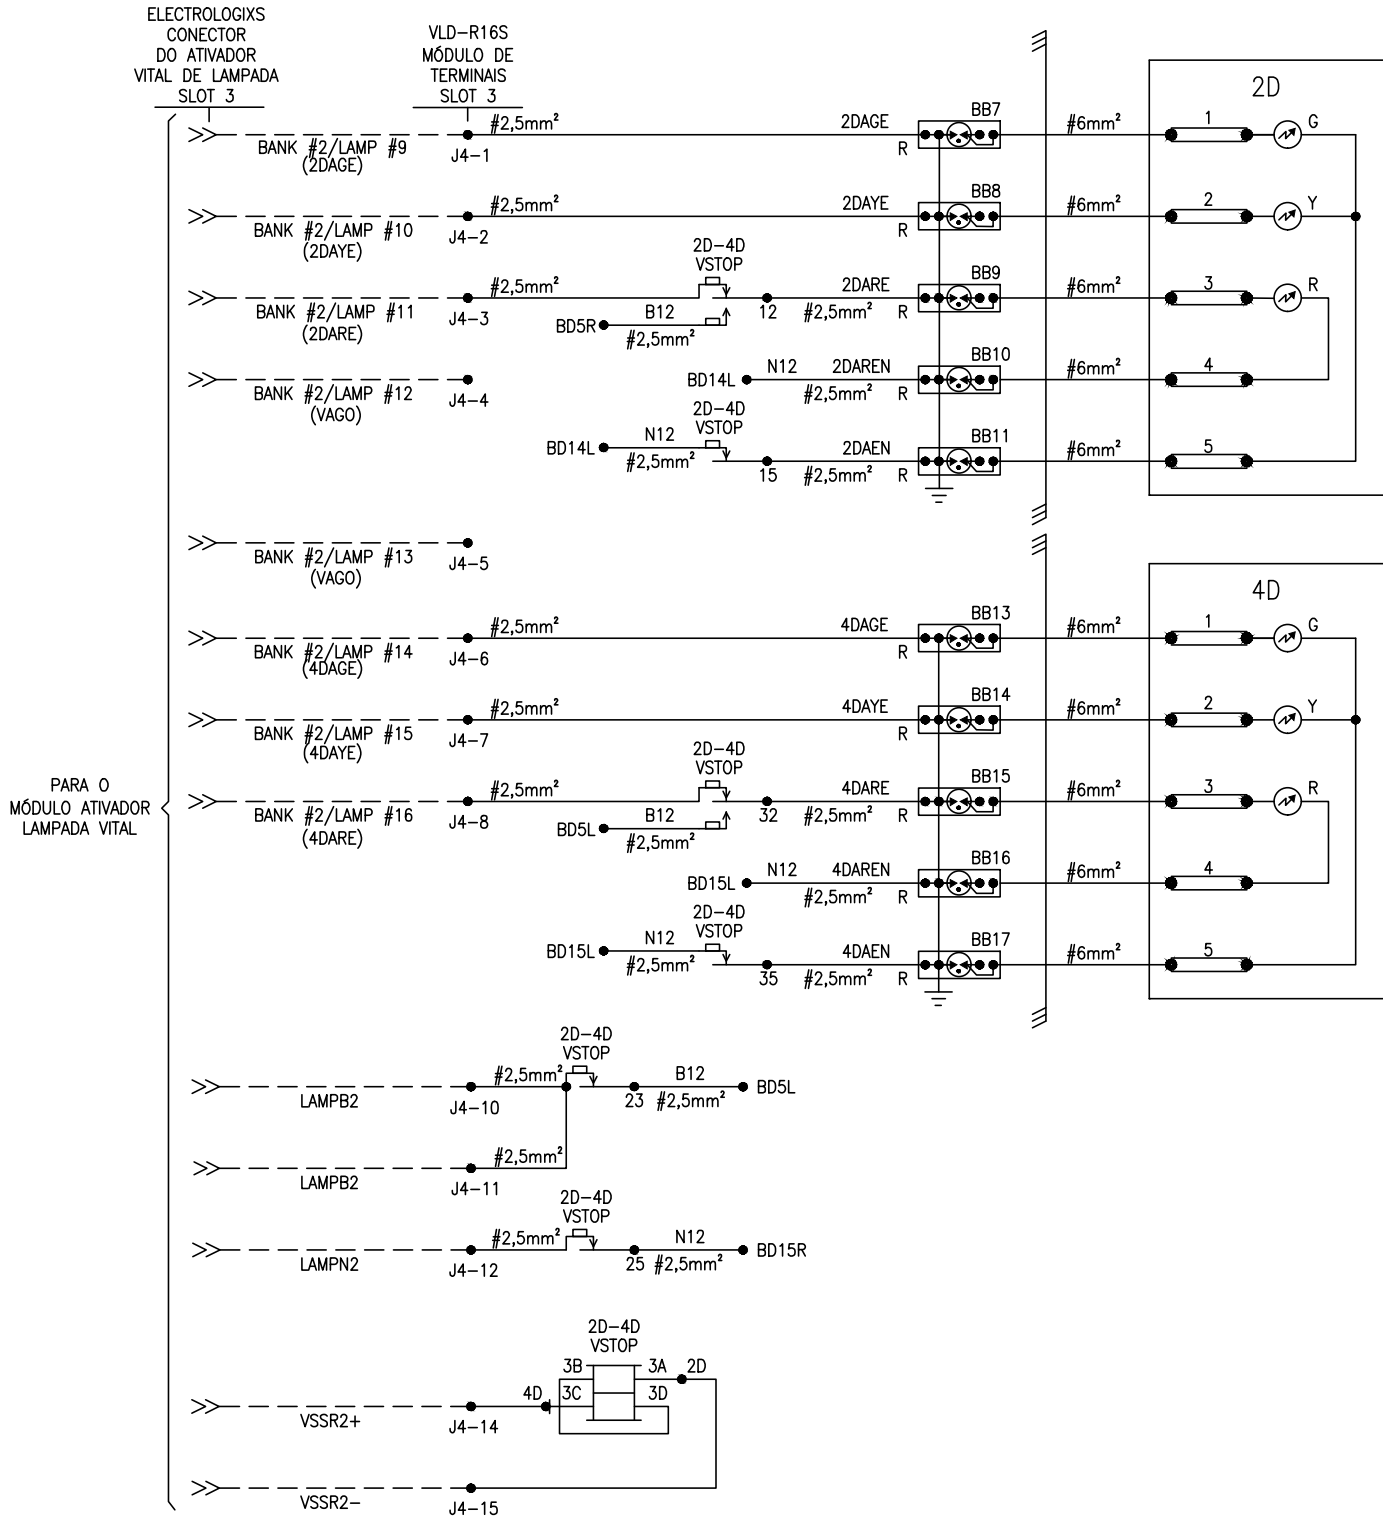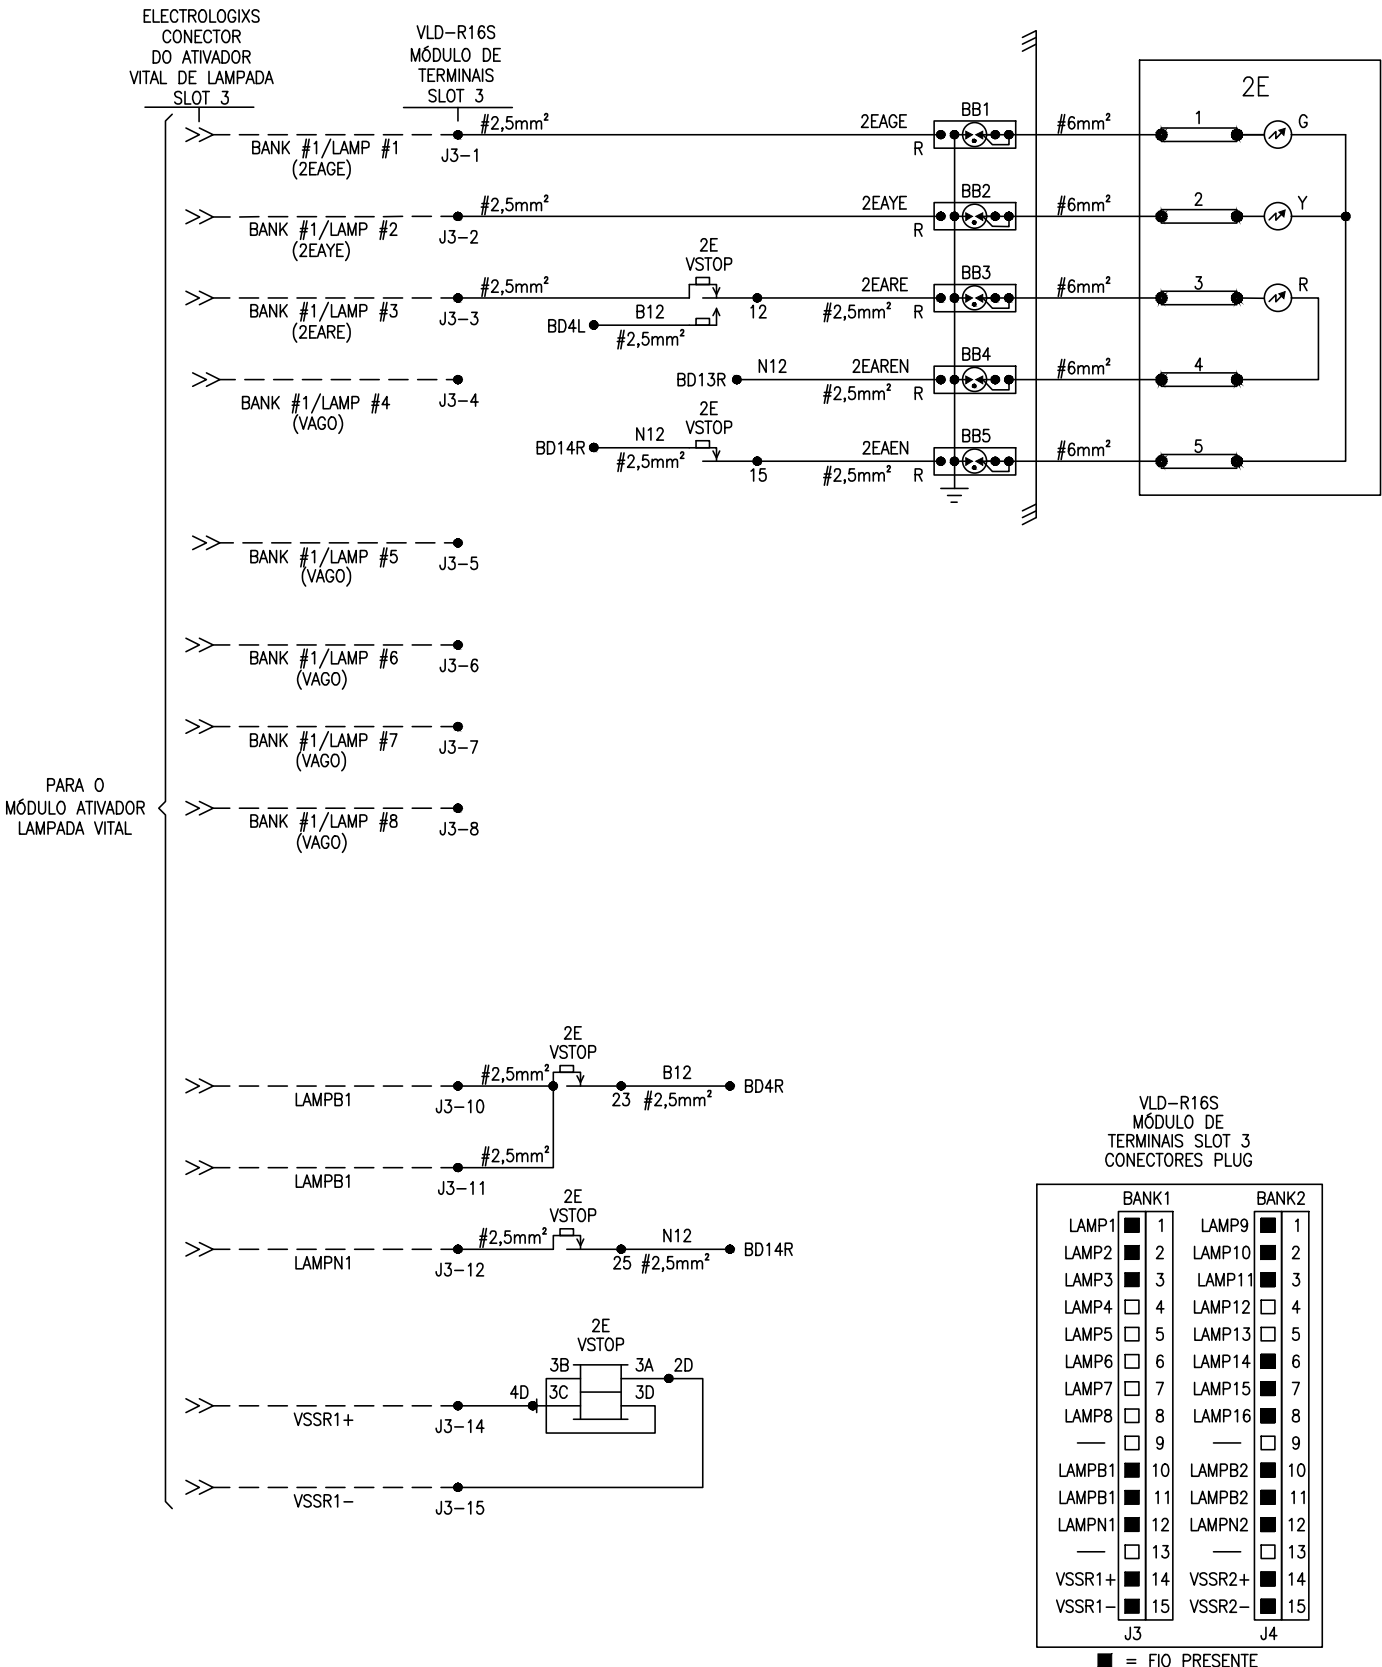

OBSERVAÇÕES:

1. = SUPRESSOR HÍBRIDO
2. = CONEXÃO INTERNA
3. TODOS CABOS DA HOUSE #1,5mm EXCETO QUANDO INDICADO.

ANOTAÇÕES

A Operação dos circuitos e equipamentos aqui representados não podem ser completamente verificados senão após a sua instalação de modo a formar um sistema completo de sinalização ferroviária e ser devidamente submetido a "Testes de seleção de contatos(BREAKDOWN)" e "Testes operacionais de serviço"(Através de planilhas e fluxo de testes) antes de sua colocação em serviços normal definitivo.

ENGENHARIA DE ELETROELETRÔNICA DE PROJETOS






TÍTULO DES.: LINHA DE SÃO PAULO
CIRCUITOS DOS SINAIS 2E, 2D E 4D

ABR 15
ITAPETI – FIP

CONTROLE INTERNO DE PROJETOS GEPEE	DATA
ELABORADOR: ANTÔNIO LEAL	08/03/2023
REVISOR: MÁRCIO MOREIRA	22/03/2023
APROVADOR: MARCOS REINH	31/03/2023

—	ENG.RESP.: HAROLDO ENNES	DATA: 08/03/2023	
	PROJ.: MÁRCIO MOREIRA	ESCALA: —	FORMATO: A3
	DES.PROJ.: ANTÔNIO LEAL	REV./DATA:	
Nº ARQUIVO MRS:	PE-0S-0FIP-015-01	SUBST./REF.:	

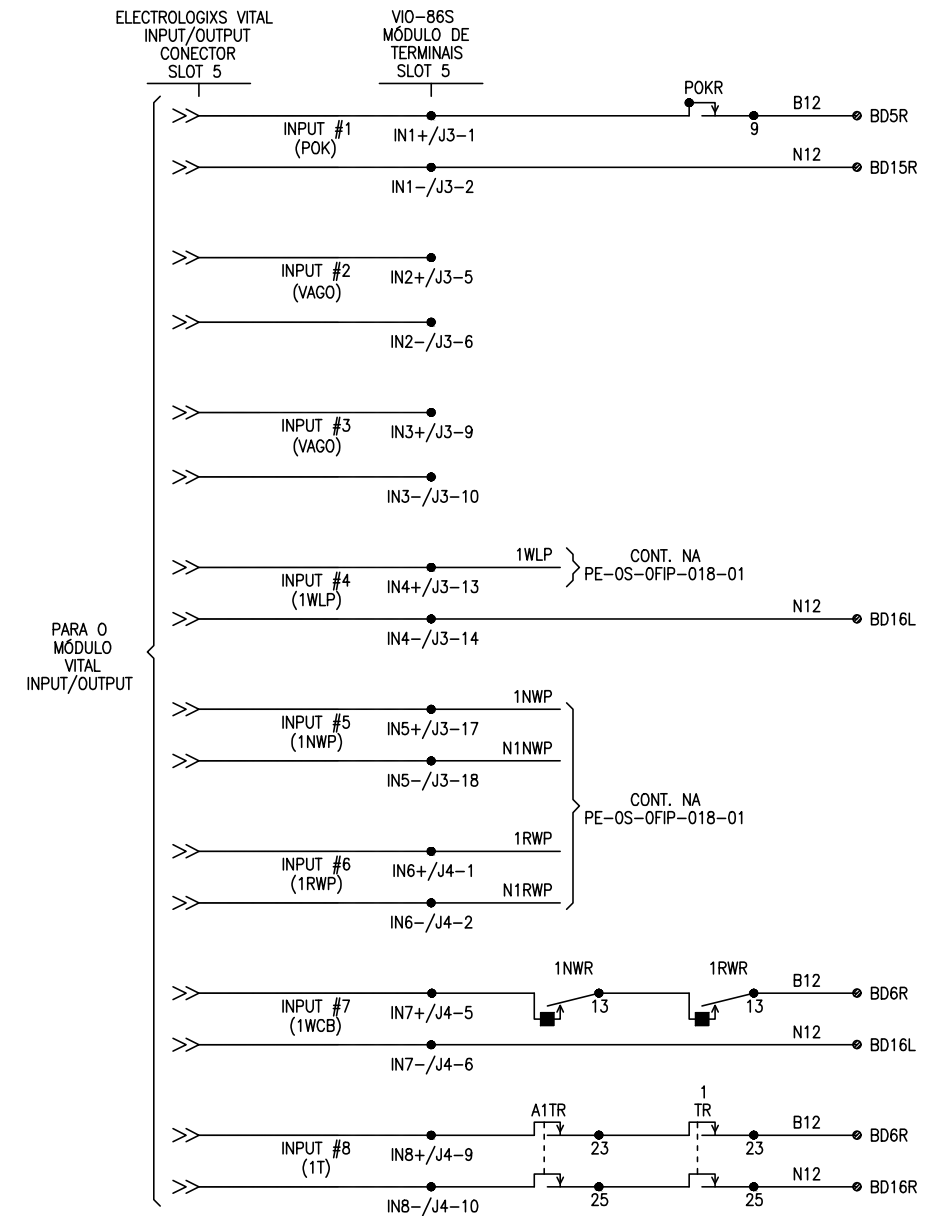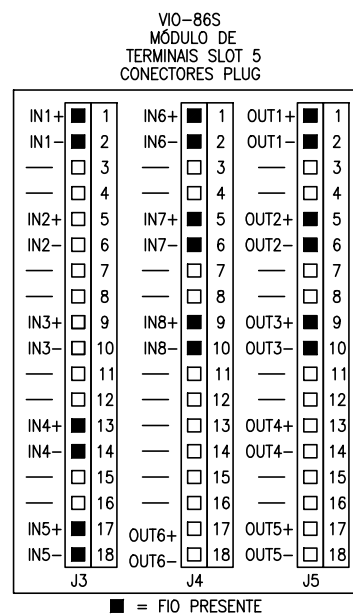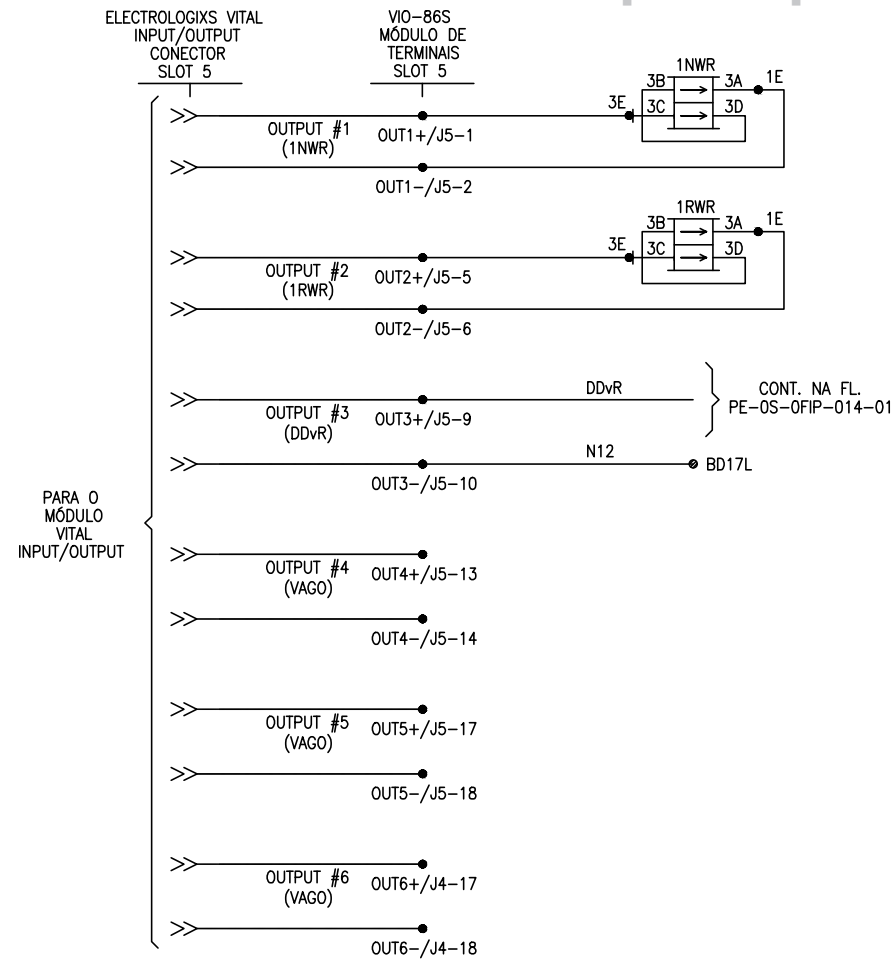

OBSERVAÇÕES:
1. ---- = CONEXÃO INTERNAL
2. TODOS CABOS DA HOUSE #1,5mm² EXCETO QUANDO INDICADO.

ANOTAÇÕES

A Operação dos circuitos e equipamentos aqui representados não podem ser completamente verificados senão após a sua instalação de modo a formar um sistema completo de sinalização ferroviária e ser devidamente submetido a "Testes de seleção de contatos(BREAKDOWN)" e "Testes operacionais de serviço"(Através de planilhas e fluxo de testes) antes de sua colocação em serviços normal definitivo.
ENGENHARIA DE ELETROELETRÔNICA DE PROJETOS



TÍTULO DES.: LINHA DE SÃO PAULO
CIRCUITOS I/O DO ELECTROLOGIXS SLOT 5
ABR 15
ITAPETI – FIP

CONTROLE INTERNO DE PROJETOS GEPEE	DATA
ELABORADOR: ANTÔNIO LEAL	08/03/2023
REVISOR: MÁRCIO MOREIRA	22/03/2023
APROVADOR: MARCOS REINH	31/03/2023

FIRMA CONTRATADA:

-

Nº ARQUIVO MRS:

PE-OS-OFIP-016-01

ENG.RESP.: HAROLDO ENNES

DATA: 08/03/2023

PROJ.: MÁRCIO MOREIRA


ESCALA: -

FORMATO: A3

DES.PROJ.: ANTÔNIO LEAL

REV./DATA: -

SUBST./REF.: -

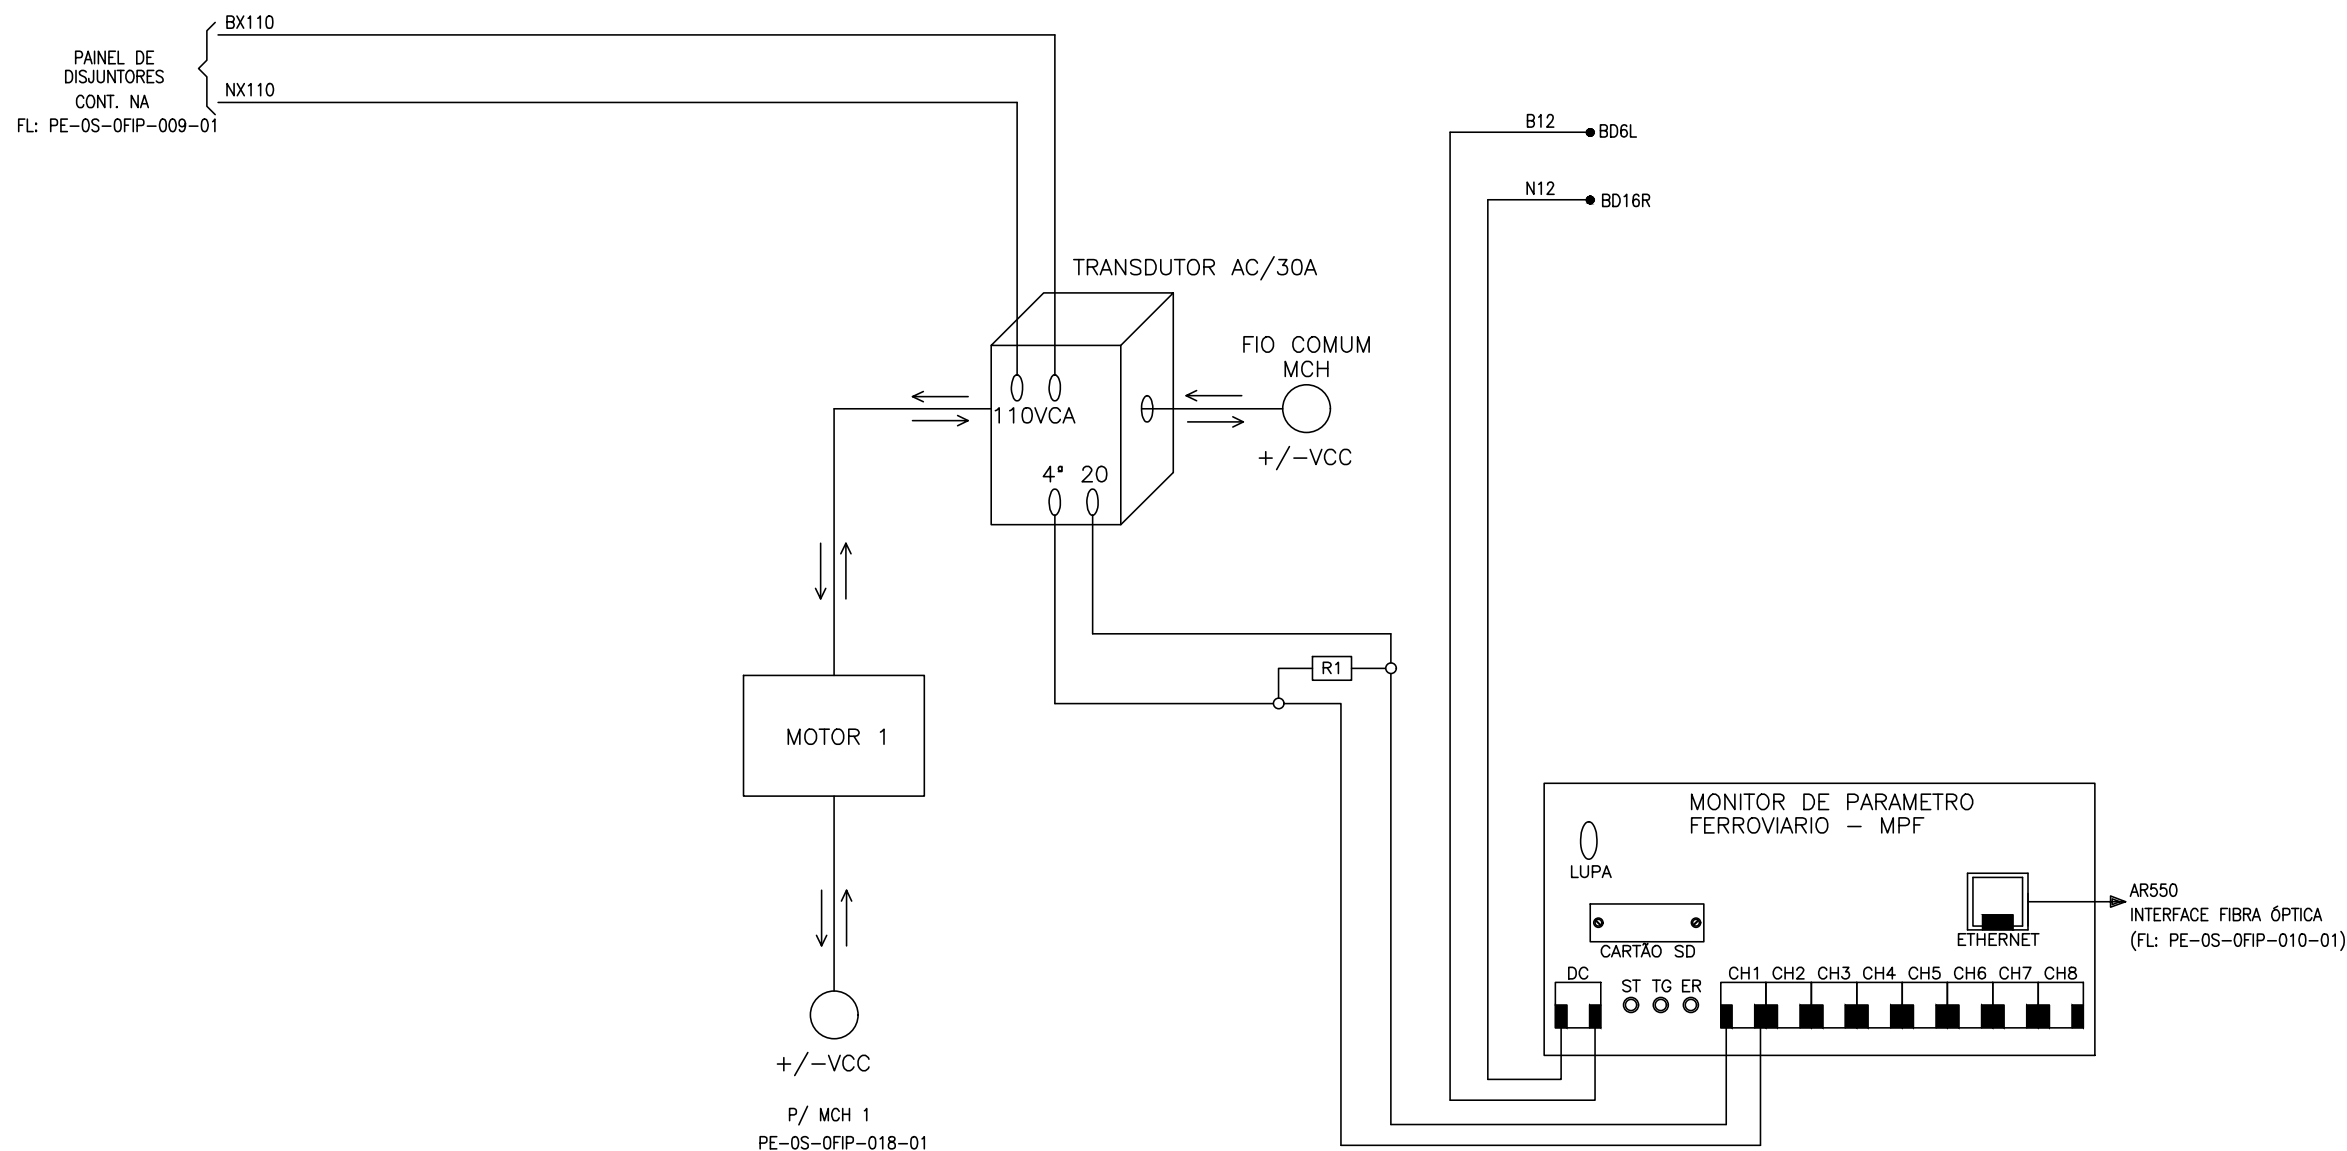

OBSERVAÇÕES:
1. R1= RESISTOR 150R -1/8W DE PRECISÃO
2. TRANSDUTOR AC +/- 30A/4-20mA
3. IP=XXX.XXX.XXX.XXX
GTW=XXX.XXX.XXX.XXX
MASK=XXX.XXX.XXX.XXX
4. INFORMAÇÕES SERÃO ATUALIZADAS COM OS
DADOS DO PROGRAMA APLICATIVO DO PROJETO
APÓS ELABORAÇÃO DO SOFTWARE

ANOTAÇÕES

A Operação dos circuitos e equipamentos aqui representados não podem ser completamente verificados senão após a sua instalação de modo a formar um sistema completo de sinalização ferroviária e ser devidamente submetido a "Testes de seleção de contatos(BREAKDOWN)" e "Testes operacionais de serviço"(Através de planilhas e fluxo de testes) antes de sua colocação em serviços normal definitivo.
ENGENHARIA DE ELETROELETRÔNICA DE PROJETOS

CONTROLE INTERNO DE PROJETOS GEPEE	DATA
ELABORADOR: ANTÔNIO LEAL	08/03/2023
REVISOR: MÁRCIO MOREIRA	22/03/2023
APROVADOR: MARCOS REINH	31/03/2023



FIRMA CONTRATADA:

Nº ARQUIVO MRS:

TÍTULO DES.:

LINHA DE SÃO PAULO
DIAGRAMA TRANSDUTOR/MPF - 1 CANAL
ABR 15
ITAPETI - FIP

ENG.RESP.: **HAROLDO ENNES**

PROJ.: **MÁRCIO MOREIRA**

DES.PROJ.: **ANTÔNIO LEAL**

DATA: **08/03/2023**


ESCALA: **-**

FORMATO: **A3**

REV./DATA: **-**

SUBST./REF.:

PE-0S-0FIP-017-01

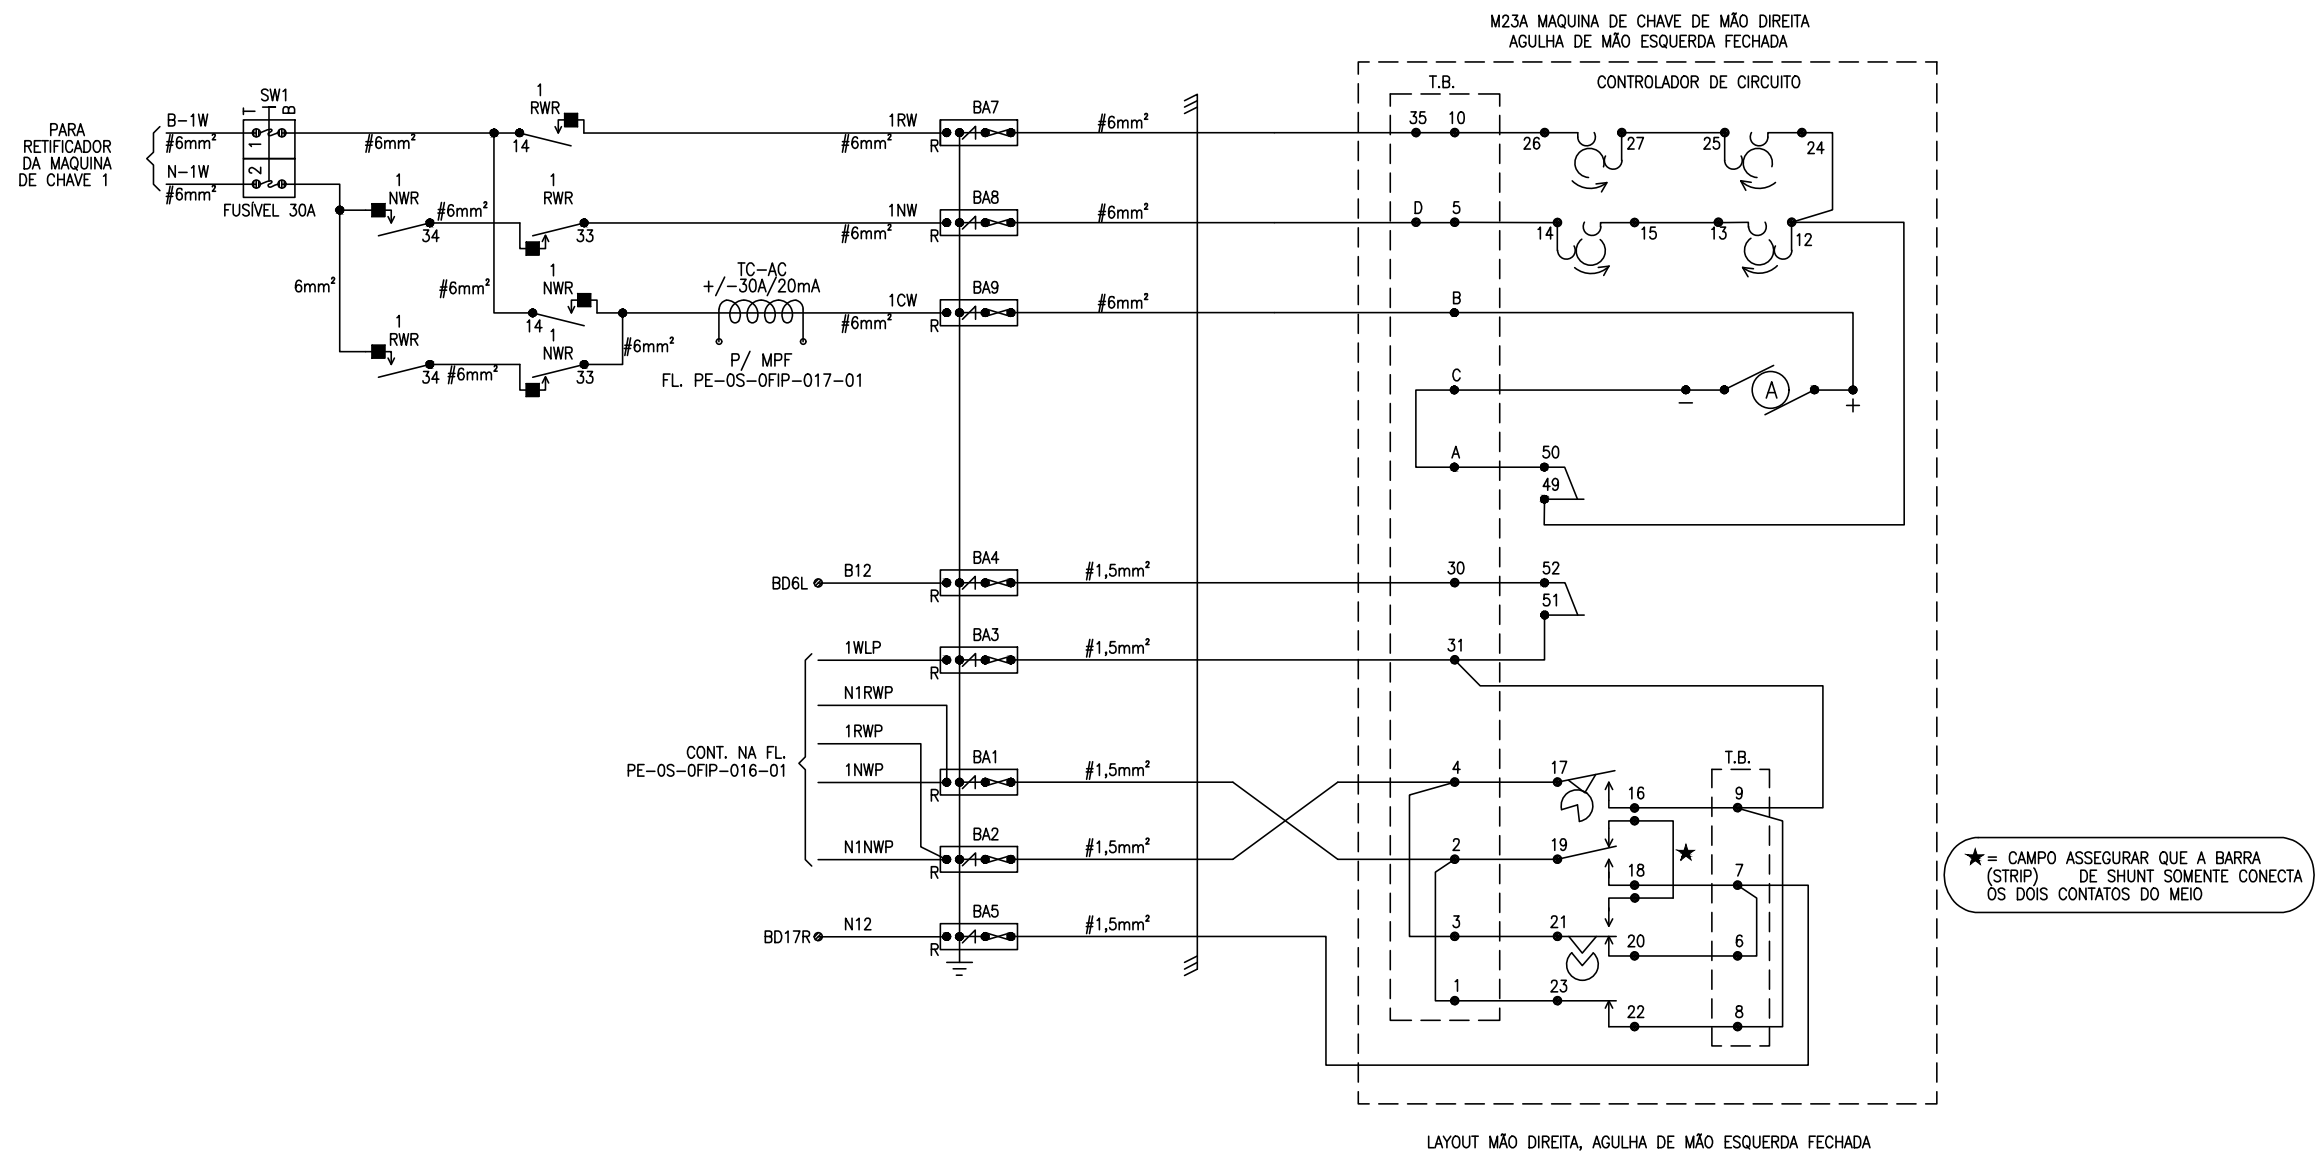

OBSERVAÇÃO:

1. $\angle$ = SUPRESSOR

2. TODOS CABOS DA HOUSE #1,5mm² EXCETO QUANDO INDICADO

ANOTAÇÕES

A Operação dos circuitos e equipamentos aqui representados não podem ser completamente verificados senão após a sua instalação de modo a formar um sistema completo de sinalização ferroviária e ser devidamente submetido a "Testes de seleção de contatos(BREAKDOWN)" e "Testes operacionais de serviço"(Através de planilhas e fluxo de testes) antes de sua colocação em serviços normal definitivo.

ENGENHARIA DE ELETROELETRÔNICA DE PROJETOS



TÍTULO DES.:	LINHA DE SÃO PAULO CIRCUITOS DA MÁQUINA DE CHAVE 1 ABR 15 ITAPETI — FIP
--------------	--

CONTROLE INTERNO DE PROJETOS GEPEE	DATA	FIRMA CONTRATADA: —	ENG.RES.P.: HAROLDO ENNES	DATA: 08/03/2023	
ELABORADOR: ANTÔNIO LEAL	08/03/2023		PROJ.: MÁRCIO MOREIRA	ESCALA: —	FORMATO: A3
REVISOR: MÁRCIO MOREIRA	22/03/2023		DES.PROJ.: ANTÔNIO LEAL	REV./DATA: —	
APROVADOR: MARCOS REINH	31/03/2023		Nº ARQUIVO MRS: PE-0S-0FIP-018-01		SUBST./REF.: —

ATENÇÃO:

ESSA PLANTA SERÁ ATUALIZADA DEPOIS DA ELABORAÇÃO DO SOFTWARE DO PAINEL DE CONTROLE LOCAL

ANOTAÇÕES

A Operação dos circuitos e equipamentos aqui representados não podem ser completamente verificados senão após a sua instalação de modo a formar um sistema completo de sinalização ferroviária e ser devidamente submetido a "Testes de seleção de contatos(BREAKDOWN)" e "Testes operacionais de serviço"(Através de planilhas e fluxo de testes) antes de sua colocação em serviços normal definitivo.
ENGENHARIA DE ELETROELETRÔNICA DE PROJETOS

CONTROLE INTERNO DE PROJETOS GEPEE	DATA
ELABORADOR: ANTÔNIO LEAL	08/03/2023
REVISOR: MÁRCIO MOREIRA	22/03/2023
APROVADOR: MARCOS REINH	31/03/2023



FIRMA CONTRATADA:


-

Nº ARQUIVO MRS:

TÍTULO DES.: LINHA DE SÃO PAULO
LAYOUT DO PAINEL DE CONTROLE LOCAL
ABR 15
ITAPETI – FIP

ENG.RESP.:	HAROLDO ENNES	DATA:	08/03/2023	
PROJ.:	MÁRCIO MOREIRA	ESCALA:	—	FORMATO: A3
DES.PROJ.:	ANTÔNIO LEAL	REV./DATA:	—	
—0S—0FIP—019—01		SUBST./REF.:	—	

PE-0S-0FIP-019-01

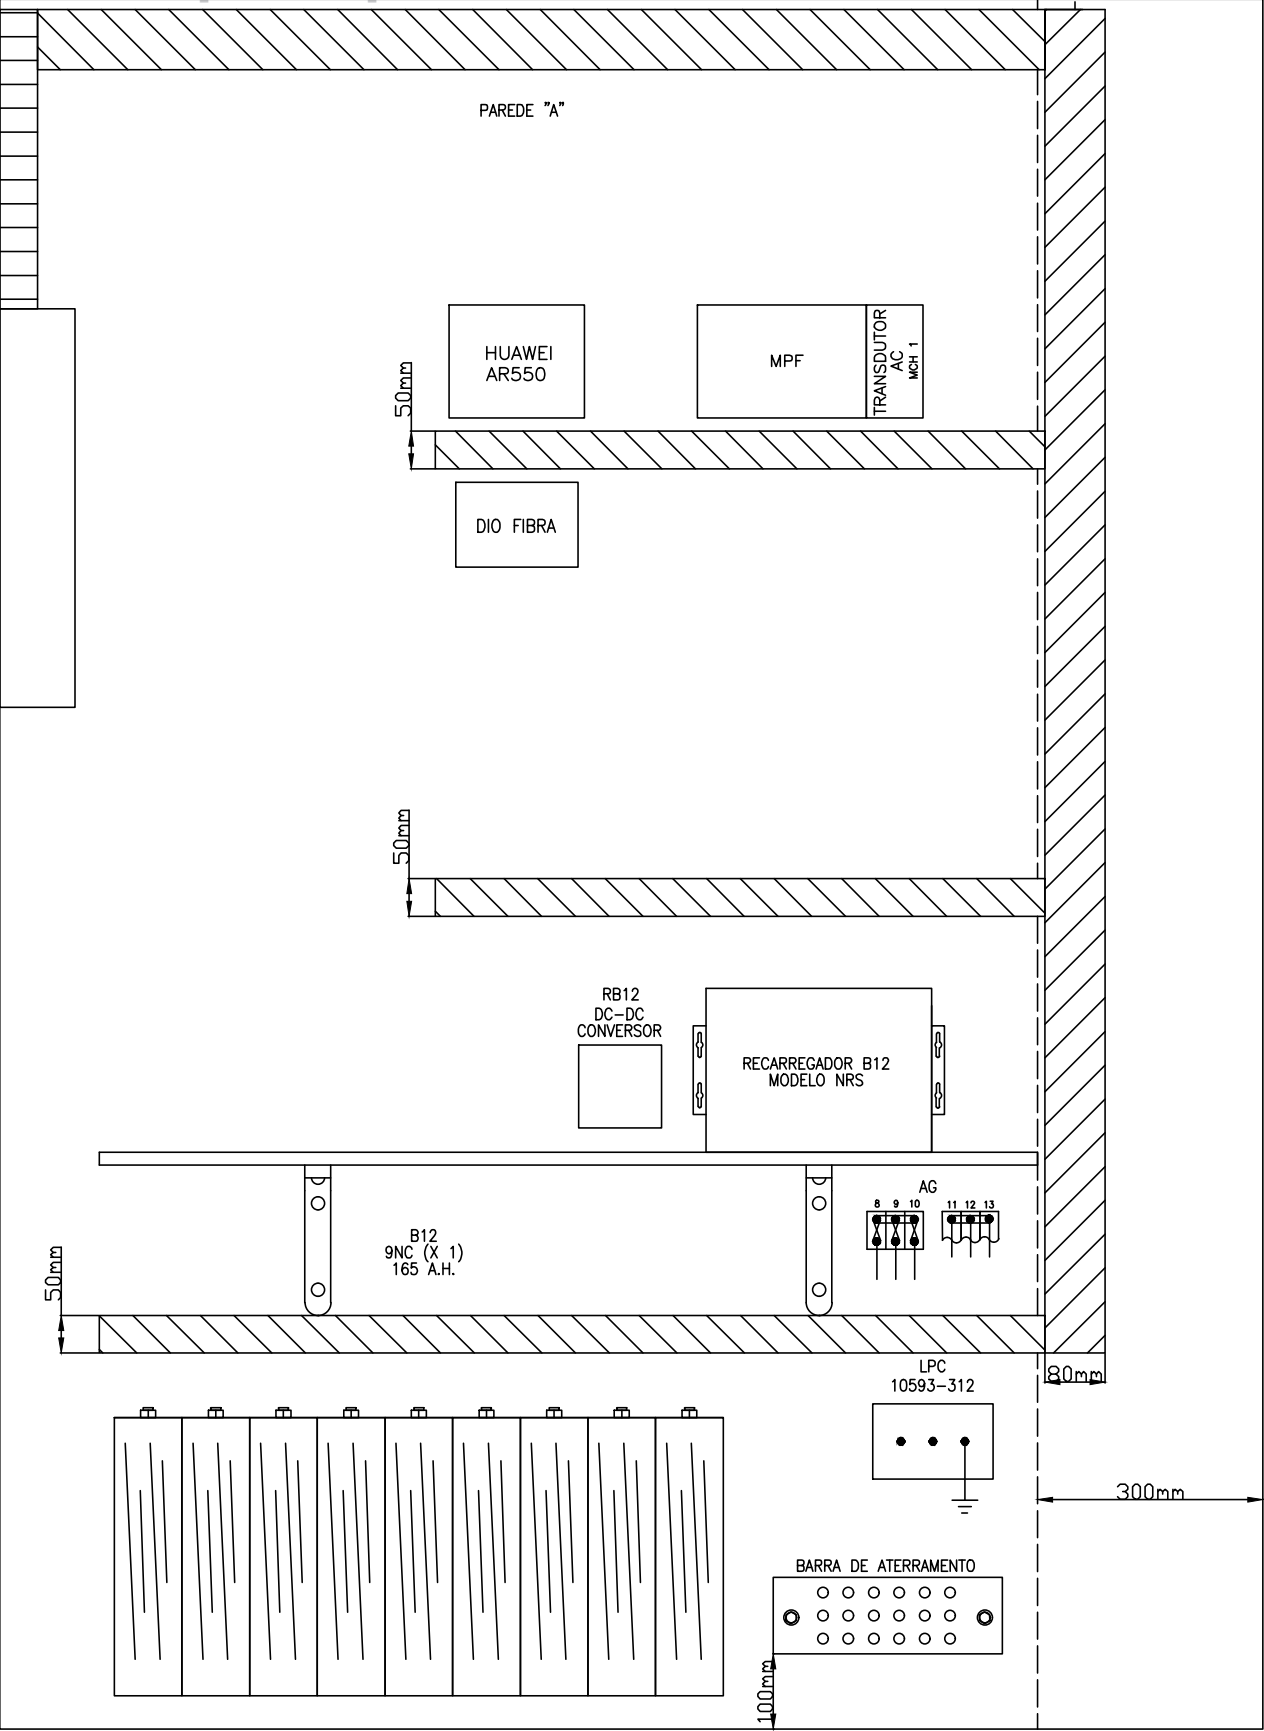

OBSERVAÇÕES:
1. COTAS EM MILÍMETROS

ANOTAÇÕES

A Operação dos circuitos e equipamentos aqui representados não podem ser completamente verificados senão após a sua instalação de modo a formar um sistema completo de sinalização ferroviária e ser devidamente submetido a "Testes de seleção de contatos(BREAKDOWN)" e "Testes operacionais de serviço"(Através de planilhas e fluxo de testes) antes de sua colocação em serviços normal definitivo.
ENGENHARIA DE ELETROELETRÔNICA DE PROJETOS


CONTROLE INTERNO DE PROJETOS GEPEE	DATA
ELABORADOR: ANTÔNIO LEAL	08/03/2023
REVISOR: MÁRCIO MOREIRA	22/03/2023
APROVADOR: MARCOS REINH	31/03/2023



FIRMA CONTRATADA:
-

Nº ARQUIVO MRS:

TÍTULO DES.: LINHA DE SÃO PAULO ABRIGO 1829mm x 1829mm LAYOUT DA PAREDE "A" ABR 15 ITAPETI – FIP		
ENG.RESP.: HAROLDO ENNES	DATA: 08/03/2023	
PROJ.: MÁRCIO MOREIRA	ESCALA: 1:10	FORMATO: A3
DES.PROJ.: ANTÔNIO LEAL	REV./DATA: -	
PE-0S-0FIP-020-01		SUBST./REF.: -

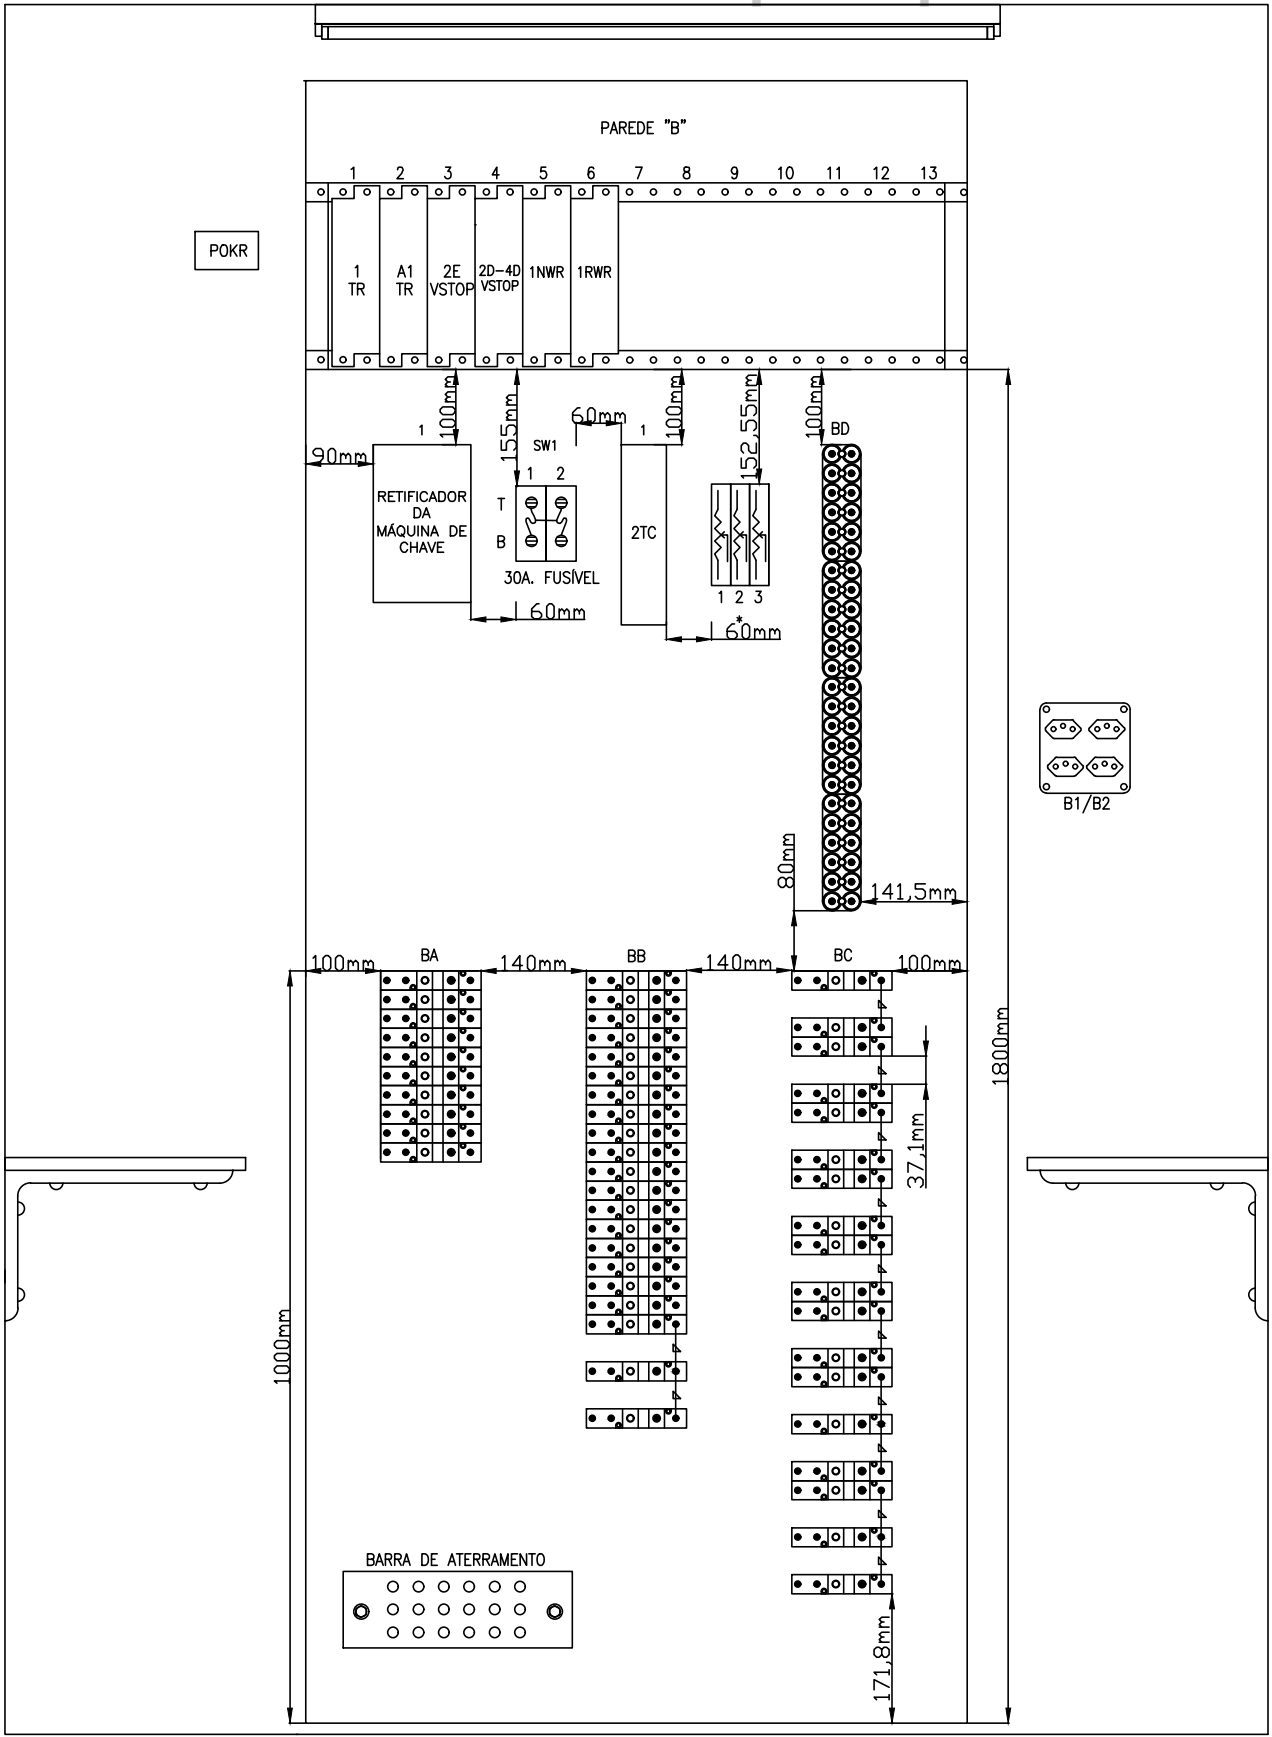

1/1	1/2	1/3	1/4	1/5	1/6	1/7	1/8	1/9	1/10	1/11	
1TR	A1TR	2EVSTOP	2D-4DVSTOP	1NWR	1RWR						CARREIRA DE RELÉ
▼ ▼ ▼ ∧ ▼ ∧ ▼ - ▼ ∧ ∧ ∧	▼ ▼ ▼ ∧ ▼ ∧ ▼ - ▼ ∧ ∧ ∧	▼ ▼ ▼ ∧ ▼ ∧ ▼ - ▼ ▲ ∧ ∧	▼ ▼ ▼ ∧ ▼ ∧ ▼ - ▼ ▲ ∧ ∧	▼ - ▼ - - ▲ - ▲	▼ - ▼ - - ▲ - ▲						
A62-0120	A62-0120	A62-0311	A62-0311	A62-0429	A62-0429						

1/12	1/13



LEGENDA DE RELÉ

▼ = CONTATO FRONT UTILIZADO
▼ = CONTATO FRONT NÃO UTILIZADO
- = CALCANHAR
∧ = CONTATO BACK NÃO UTILIZADO
▲ = CONTATO BACK UTILIZADO

TABELA MRS	ALSTOM RELAY PN	SAFETTRAN RELAY PN	DIAGRAMA DE CONTATO
B49	A62-0429	400520	A
B44	A62-0311	400022	B
B42	A62-0120	400510	B

RESISTORES DE CDV


*1 1TB RES (5 Ω)
*2 1RB RES (5 Ω)
*3 A1RB RES (5 Ω)

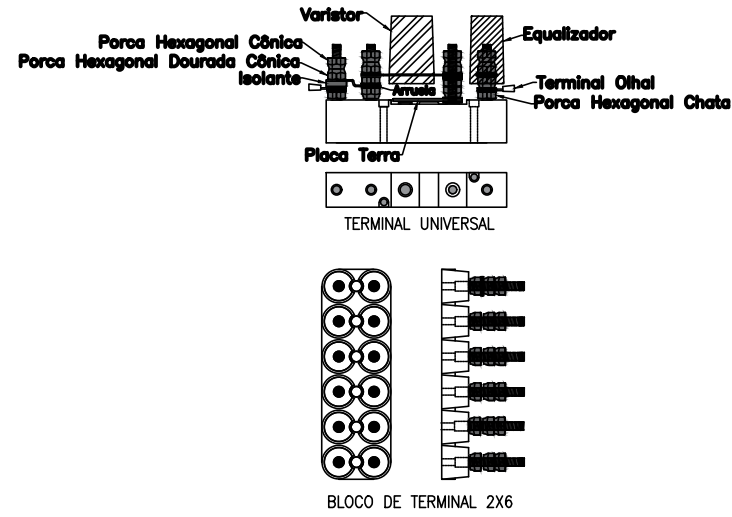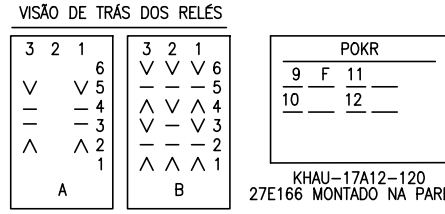

OBSERVAÇÕES:


1. COTAS EM MILÍMETROS

ANOTAÇÕES	A Operação dos circuitos e equipamentos aqui representados não podem ser completamente verificados senão após a sua instalação de modo a formar um sistema completo de sinalização ferroviária e ser devidamente submetido a "Testes de seleção de contatos(BREAKDOWN)" e "Testes operacionais de serviço"(Através de planilhas e fluxo de testes) antes de sua colocação em serviços normal definitivo. ENGENHARIA DE ELETROELETRÔNICA DE PROJETOS			 Logística S.A.	TÍTULO DES.: LINHA DE SÃO PAULO ABRIGO 1829mm x 1829mm LAYOUT DA PAREDE "B" ABR 15 ITAPETI – FIP			
		CONTROLE INTERNO DE PROJETOS GEPEE	DATA		FIRMA CONTRATADA:	ENG.RESP.: HAROLDO ENNES	DATA: 08/03/2023	
		ELABORADOR: ANTÔNIO LEAL	08/03/2023	-	PROJ.: MÁRCIO MOREIRA	ESCALA: 1:10	FORMATO: A3	
		REVISOR: MÁRCIO MOREIRA	22/03/2023		DES.PROJ.: ANTÔNIO LEAL	REV./DATA: -		
		APROVADOR: MARCOS REINH	31/03/2023		Nº ARQUIVO MRS: PE-0S-OFIP-021-01		SUBST./REF.: -	

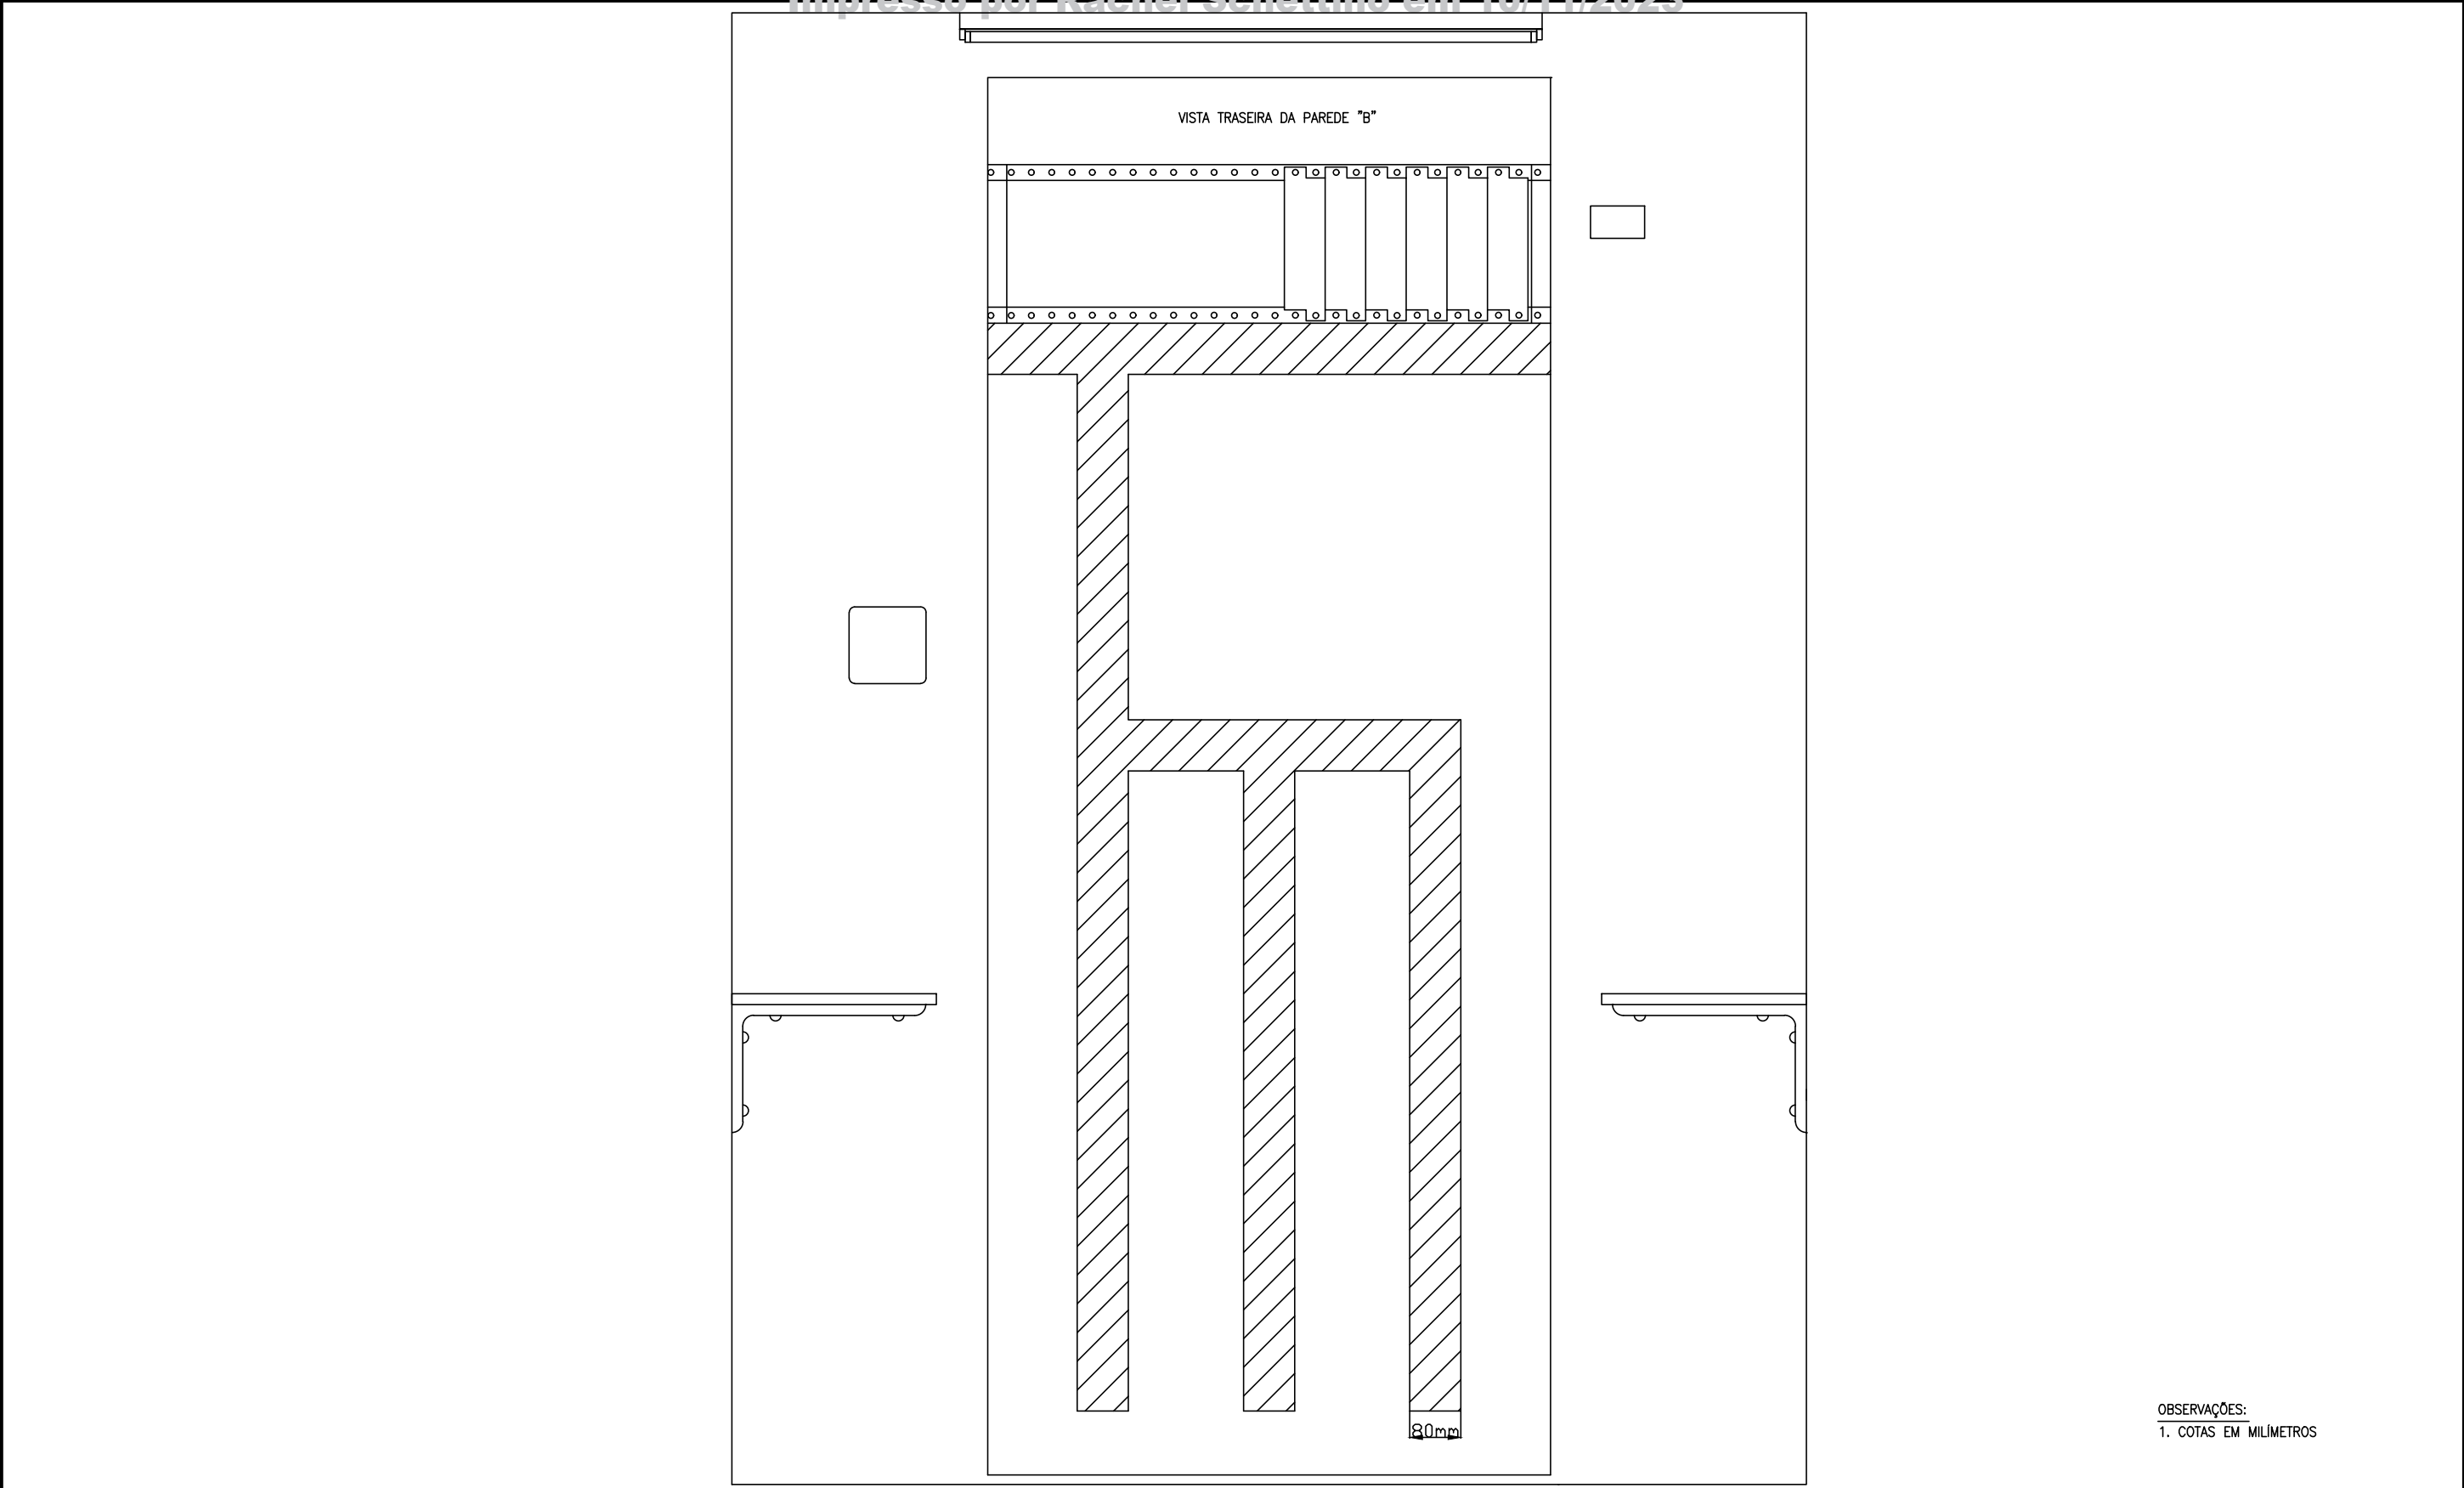


OBSERVAÇÕES:
1. COTAS EM MILÍMETROS

ANOTAÇÕES	A Operação dos circuitos e equipamentos aqui representados não podem ser completamente verificados senão após a sua instalação de modo a formar um sistema completo de sinalização ferroviária e ser devidamente submetido a "Testes de seleção de contatos(BREAKDOWN)" e "Testes operacionais de serviço"(Através de planilhas e fluxo de testes) antes de sua colocação em serviços normal definitivo. ENGENHARIA DE ELETROELETRÔNICA DE PROJETOS			 Logística S.A.	TÍTULO DES.: LINHA DE SÃO PAULO				
					ABRIGO 1829mm x 1829mm LAYOUT DO PAINEL TRASEIRO PAREDE "B"				
						ABR 15			
						ITAPETI – FIP			
		CONTROLE INTERNO DE PROJETOS GEPEE	DATA	FIRMA CONTRATADA: —	ENG.RESP.: HAROLDO ENNES	DATA: 08/03/2023			
		ELABORADOR: ANTÔNIO LEAL	08/03/2023		PROJ.: MÁRCIO MOREIRA	ESCALA: 1:10	FORMATO: A3		
		REVISOR: MÁRCIO MOREIRA	22/03/2023		DES.PROJ.: ANTÔNIO LEAL	REV./DATA: —			
		APROVADOR: MARCOS REINH	31/03/2023		Nº ARQUIVO MRS: PE-0S-0FIP-022-01		SUBST./REF.: —		

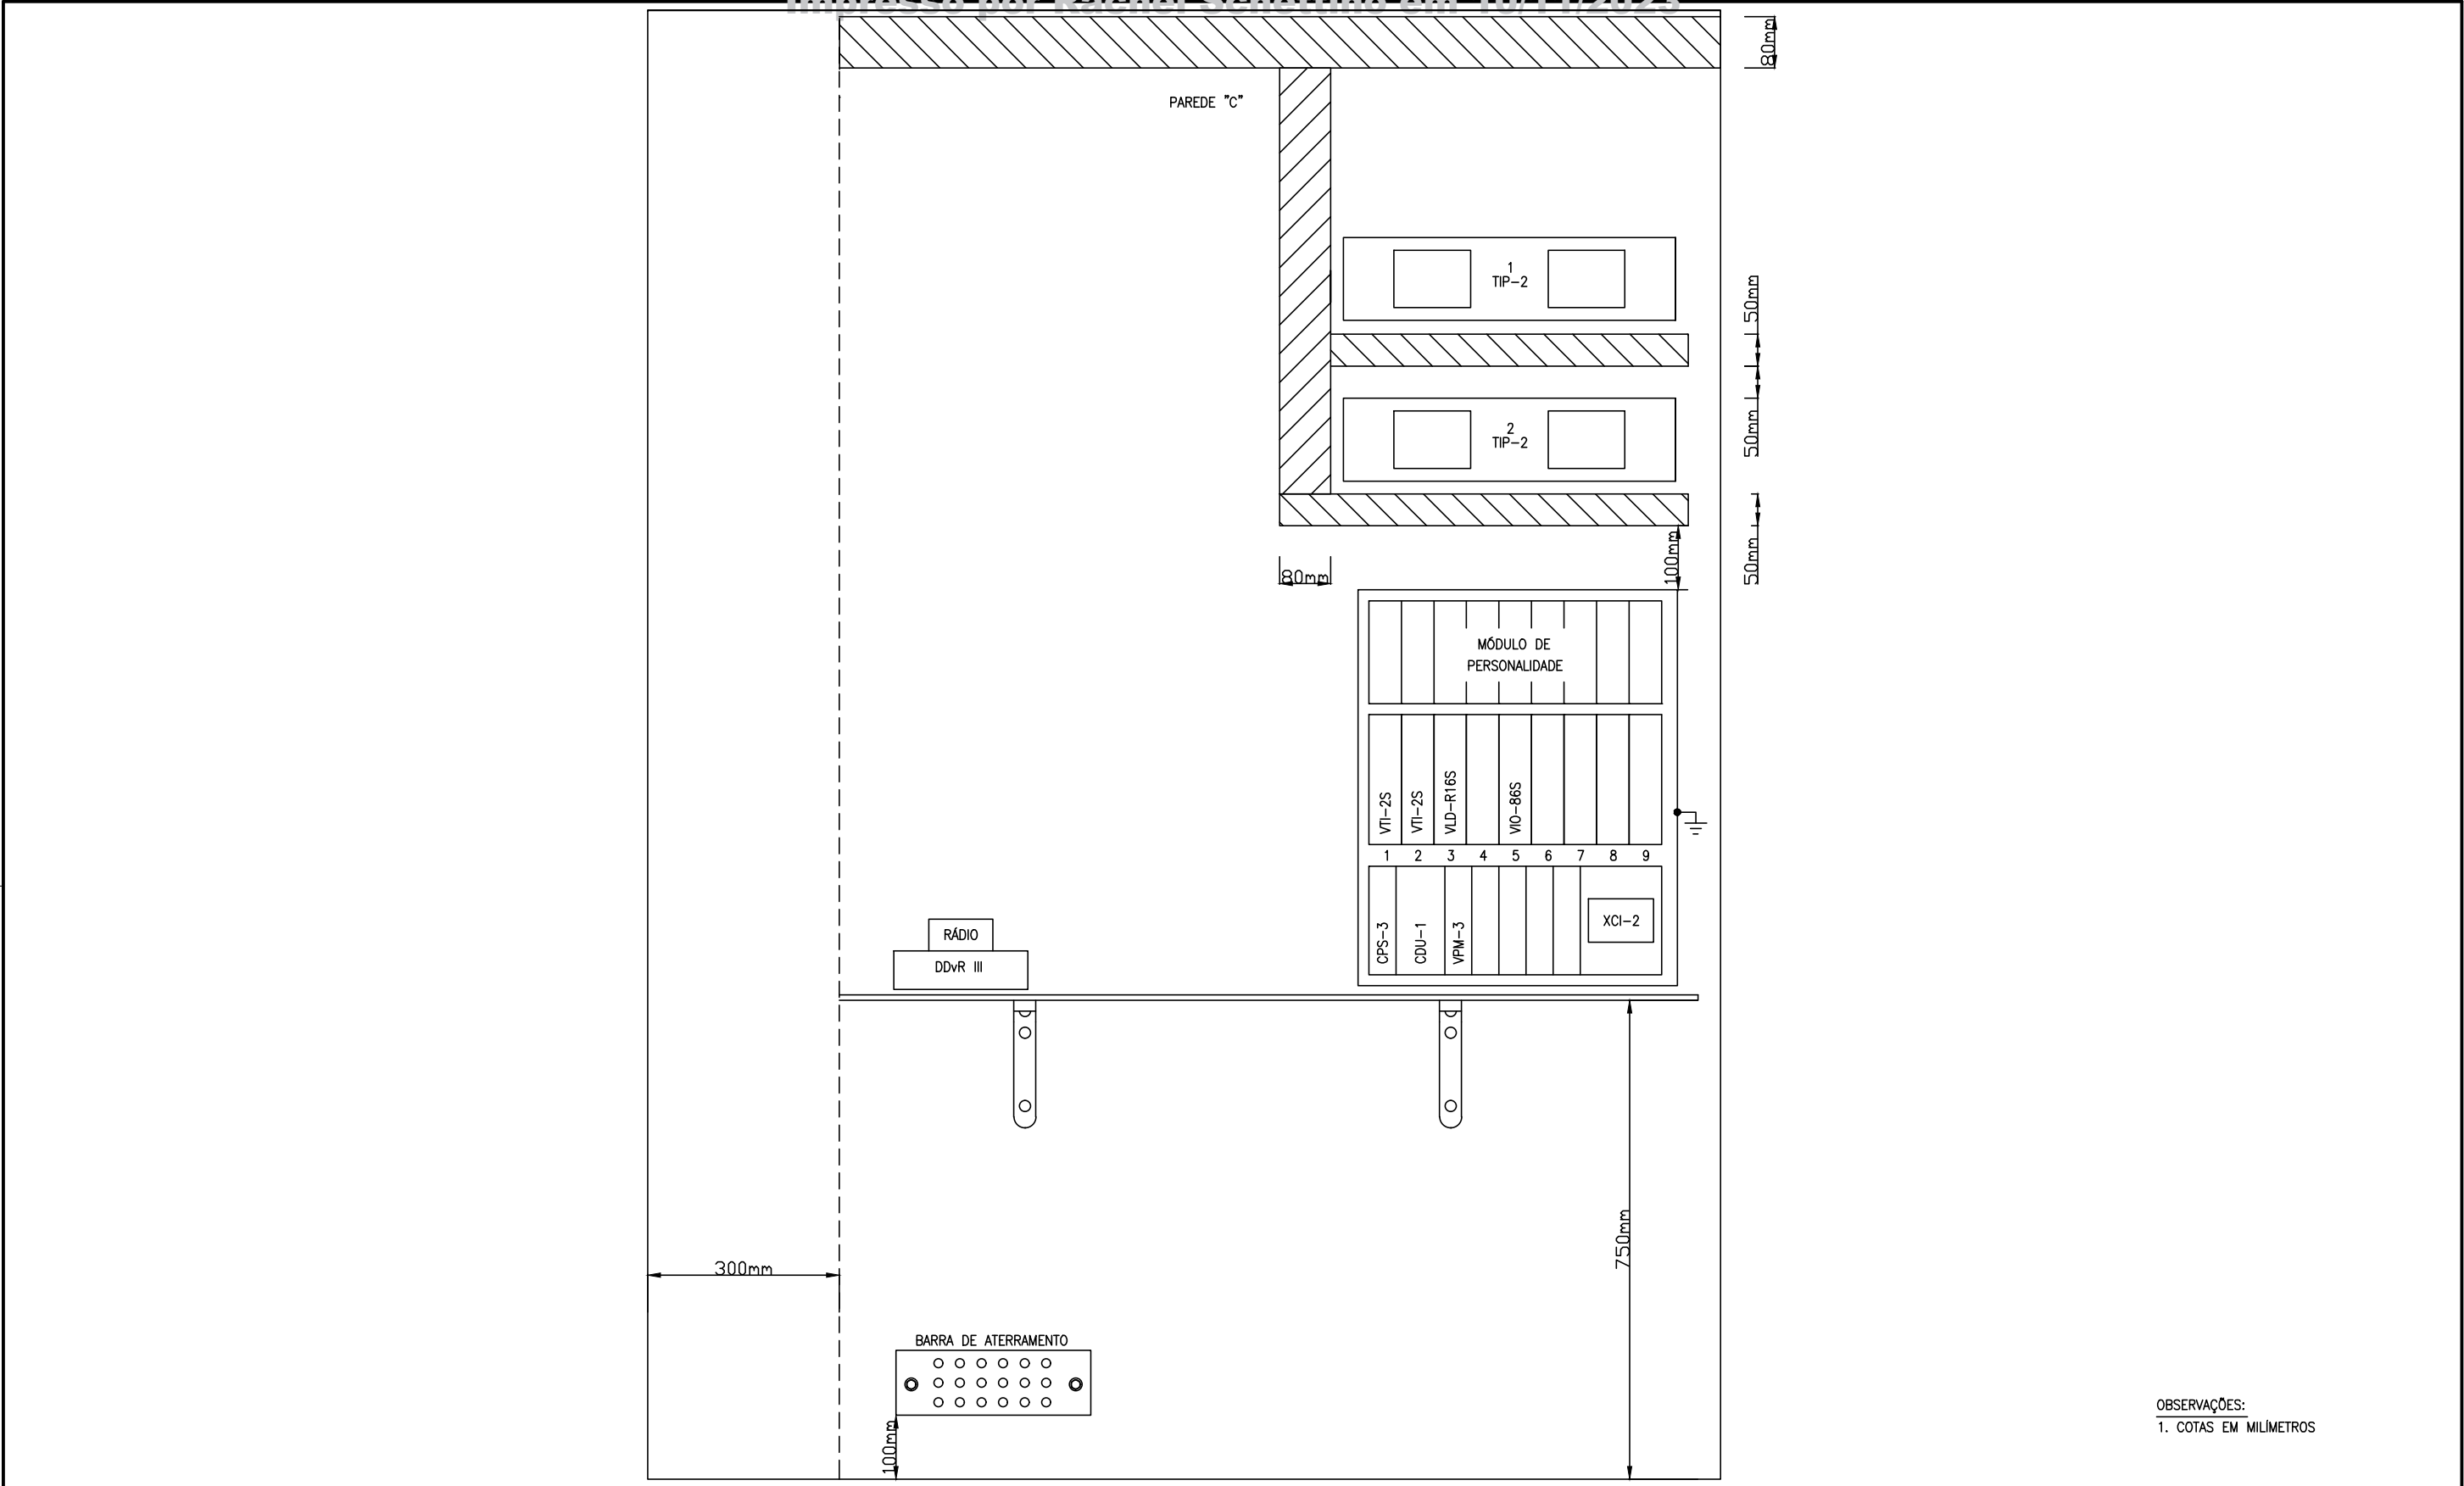

OBSERVAÇÕES:
1. COTAS EM MILÍMETROS

ANOTAÇÕES	A Operação dos circuitos e equipamentos aqui representados não podem ser completamente verificados senão após a sua instalação de modo a formar um sistema completo de sinalização ferroviária e ser devidamente submetido a "Testes de seleção de contatos(BREAKDOWN)" e "Testes operacionais de serviço"(Através de planilhas e fluxo de testes) antes de sua colocação em serviços normal definitivo. ENGENHARIA DE ELETROELETRÔNICA DE PROJETOS			 Logística S.A.	TÍTULO DES.: LINHA DE SÃO PAULO ABRIGO 1829mm x 1829mm LAYOUT DA PAREDE "C" ABR 15 ITAPETI – FIP			
		FIRMA CONTRATADA: -	ENG.RESP.: HAROLDO ENNES		DATA: 08/03/2023			
			PROJ.: MÁRCIO MOREIRA		ESCALA: 1:10	FORMATO: A3		
			DES.PROJ.: ANTÔNIO LEAL		REV./DATA: -			
			Nº ARQUIVO MRS: PE-0S-0FIP-023-01		SUBST./REF.: -			
		CONTROLE INTERNO DE PROJETOS GEPEE	DATA					
ELABORADOR: ANTÔNIO LEAL	08/03/2023							
REVISOR: MÁRCIO MOREIRA	22/03/2023							
APROVADOR: MARCOS REINH	31/03/2023							

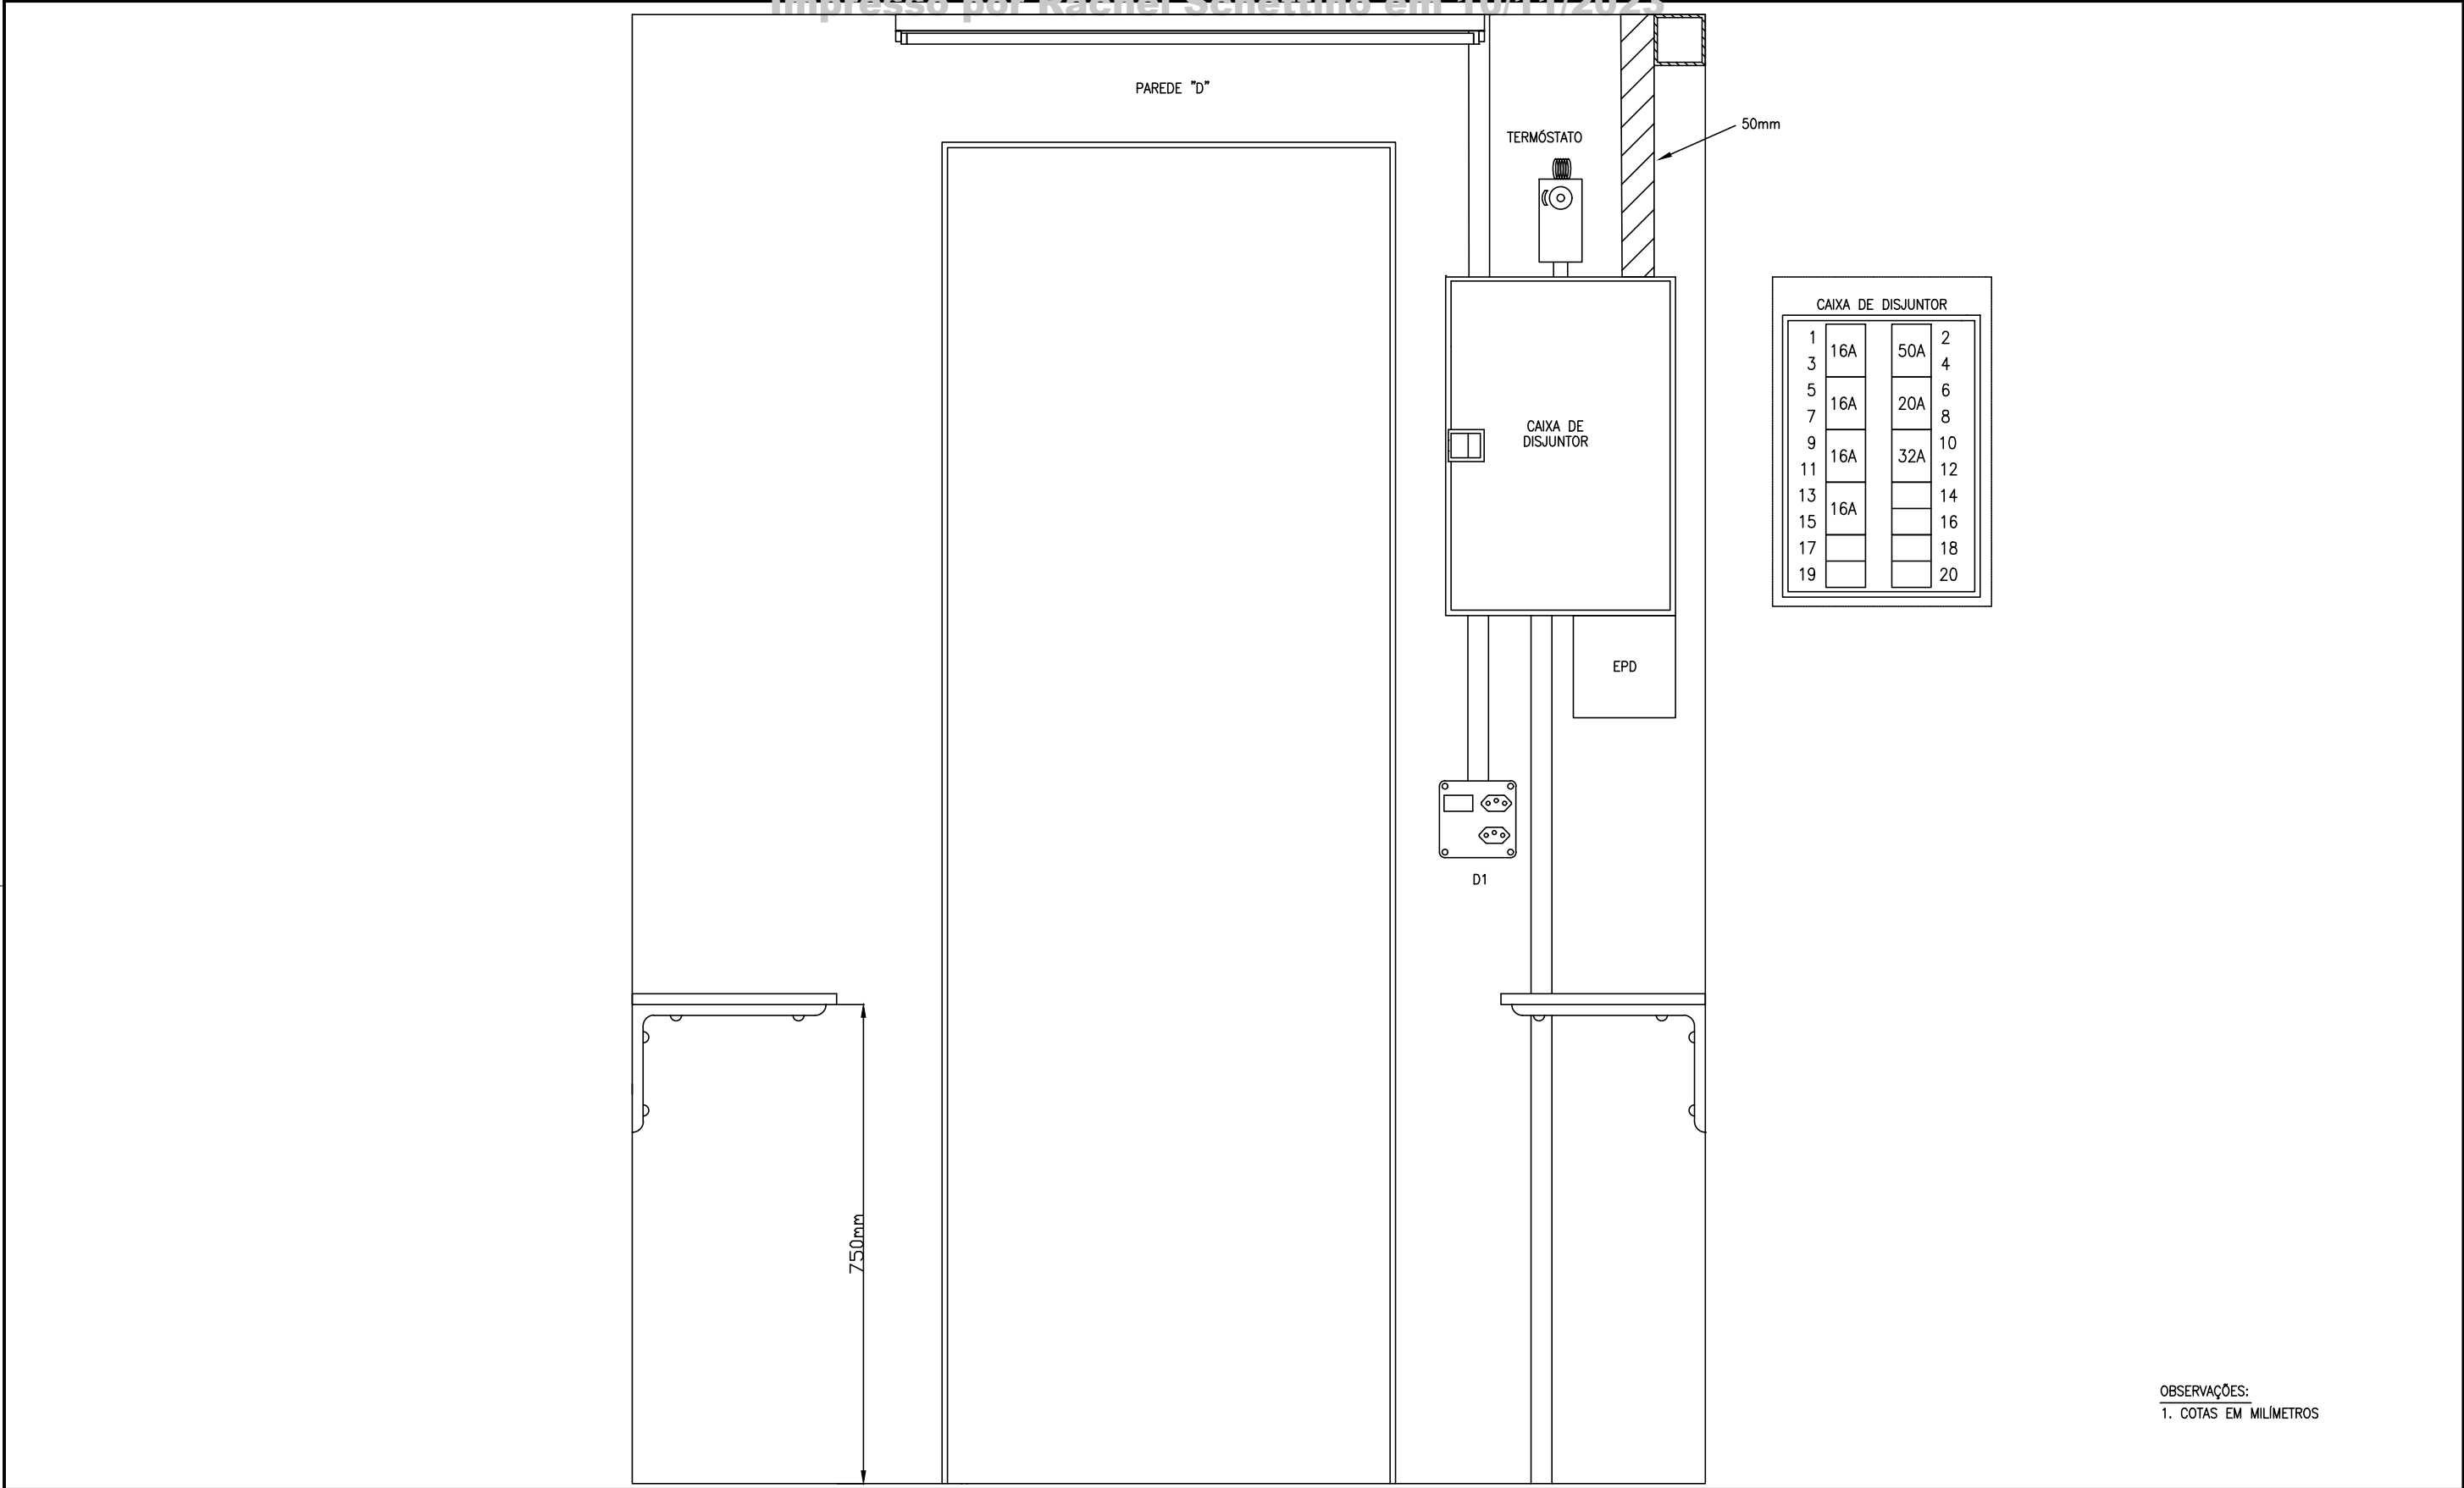

OBSERVAÇÕES:
1. COTAS EM MILÍMETROS

ANOTAÇÕES

A Operação dos circuitos e equipamentos aqui representados não podem ser completamente verificados senão após a sua instalação de modo a formar um sistema completo de sinalização ferroviária e ser devidamente submetido a "Testes de seleção de contatos(BREAKDOWN)" e "Testes operacionais de serviço"(Através de planilhas e fluxo de testes) antes de sua colocação em serviços normal definitivo.
ENGENHARIA DE ELETROELETRÔNICA DE PROJETOS

CONTROLE INTERNO DE PROJETOS GEPEE	DATA
ELABORADOR: ANTÔNIO LEAL	08/03/2023
REVISOR: MÁRCIO MOREIRA	22/03/2023
APROVADOR: MARCOS REINH	31/03/2023







FIRMA CONTRATADA:

Nº ARQUIVO MRS:


TÍTULO DES.: LINHA DE SÃO PAULO
ABRIGO 1829mm x 1829mm LAYOUT DA PAREDE "D"
ABR 15
ITAPETI – FIP

ENG.RESP.: HAROLDO ENNES	DATA: 08/03/2023
PROJ.: MÁRCIO MOREIRA	ESCALA: 1:10 FORMATO: A3
DES.PROJ.: ANTÔNIO LEAL	REV./DATA: –
SUBST./REF.: –	

PE–OS–OFIP–024–01

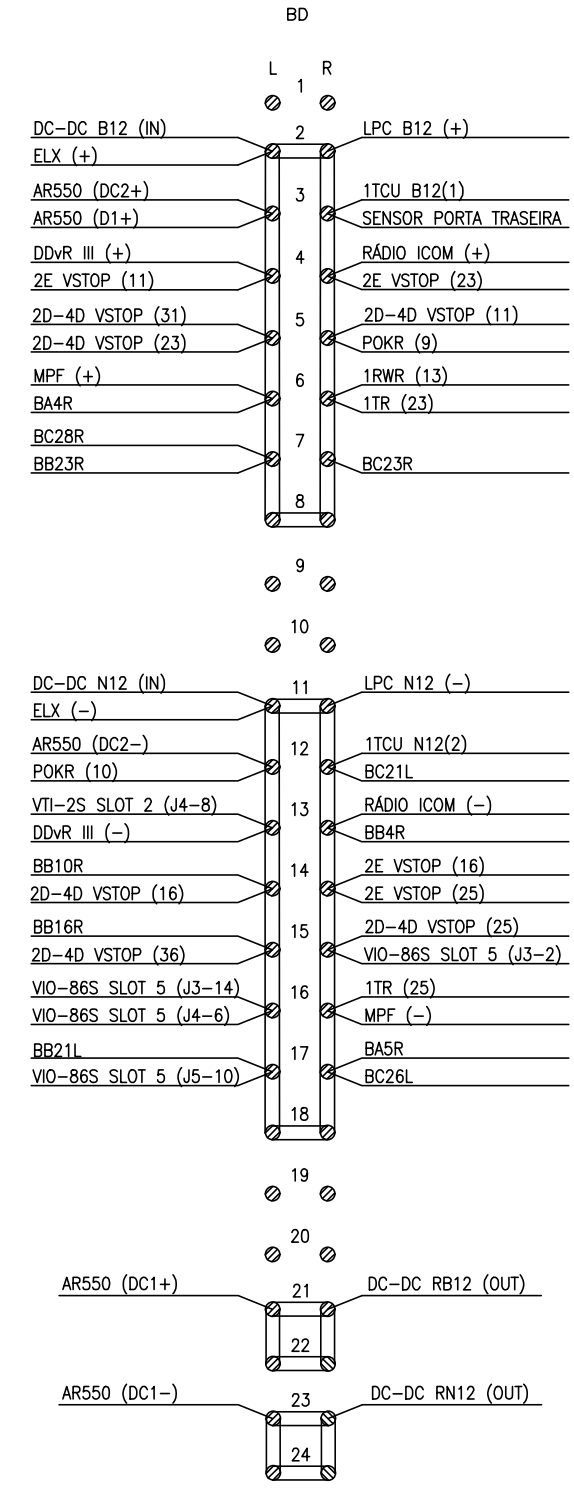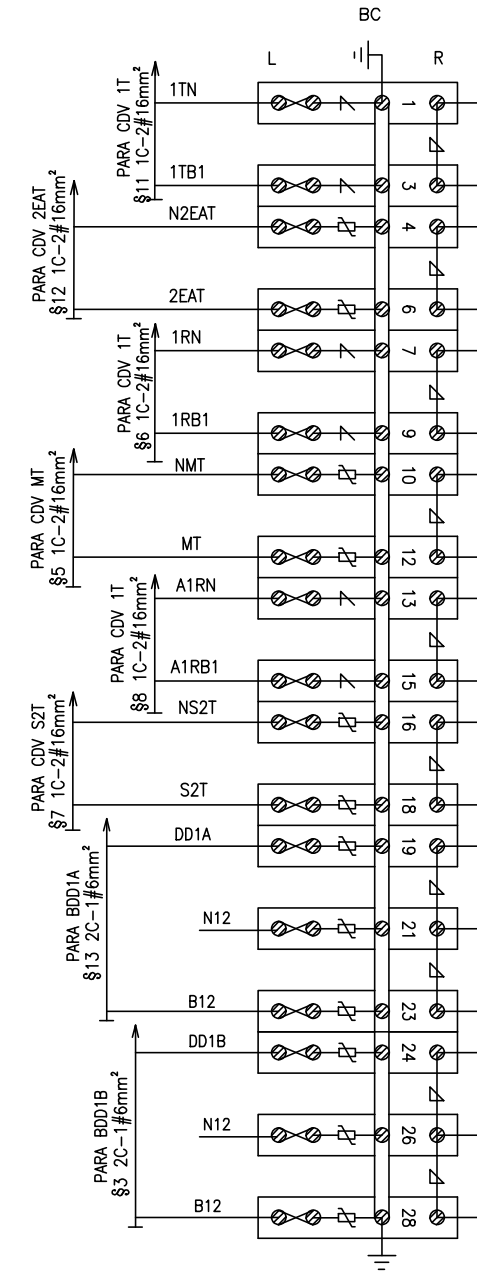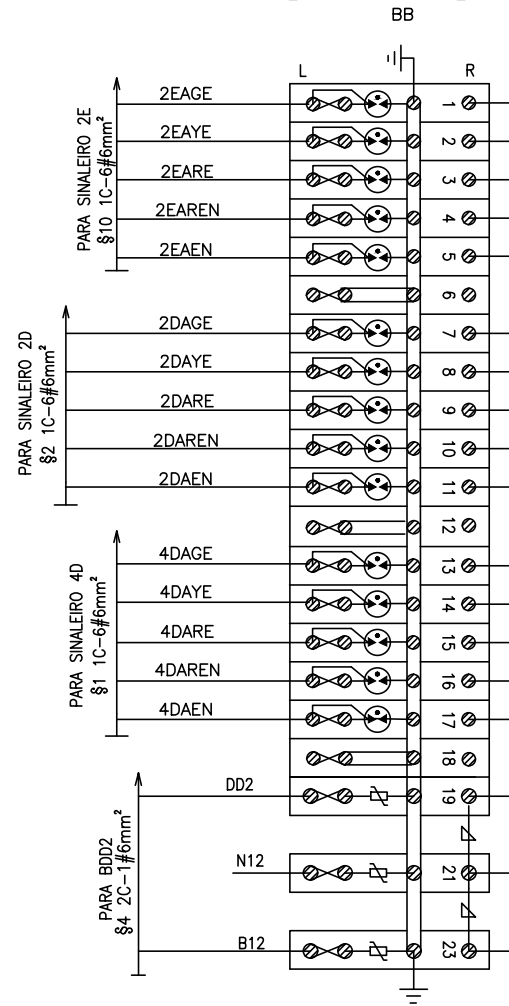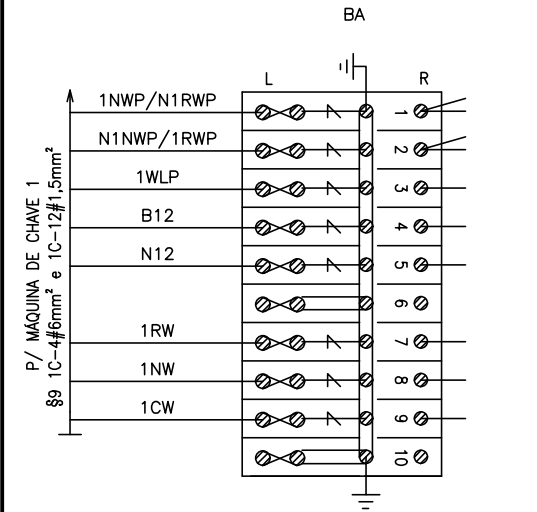

LEGENDA DE NOMENCLATURA

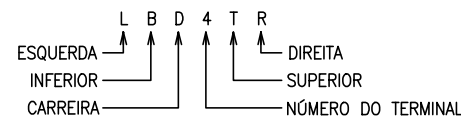

OBSERVAÇÕES:

- ∠ = SUPRESSOR
- ⊗ = VARISTOR CLAMPER
- ⊗ = SUPRESSOR HÍBRIDO
- Δ = EQUALIZADOR
- ⊗ = PINO DE TERMINAL
- ⊗ = LINK DE TESTE
- ⊗ = LINK SOLIDO
- ⊗ = TERRA

ANOTAÇÕES

A Operação dos circuitos e equipamentos aqui representados não podem ser completamente verificados senão após a sua instalação de modo a formar um sistema completo de sinalização ferroviária e ser devidamente submetido a "Testes de seleção de contatos(BREAKDOWN)" e "Testes operacionais de serviço"(Através de planilhas e fluxo de testes) antes de sua colocação em serviços normal definitivo.

ENGENHARIA DE ELETROELETRÔNICA DE PROJETOS



TÍTULO DES.:		LINHA DE SÃO PAULO	
		DETALHE DO PAINEL DE TERMINAIS [TB]	
		ABR 15	
		ITAPETI – FIP	
ENG.RESP.:		HAROLDO ENNES	DATA: 08/03/2023
PROJ.:		MÁRCIO MOREIRA	ESCALA: –
DES.PROJ.:		ANTÔNIO LEAL	FORMATO: A3
			REV./DATA: –
			SUBST./REF.: –

CONTROLE INTERNO DE PROJETOS GEPEE	DATA
ELABORADOR: ANTÔNIO LEAL	08/03/2023
REVISOR: MÁRCIO MOREIRA	22/03/2023
APROVADOR: MARCOS REINH	31/03/2023

FIRMA CONTRATADA:	
Nº ARQUIVO MRS:	PE-0S-0FIP-025-01