

Gerência de Engenharia e Projetos de Eletroeletrônica

PROJETO EXECUTIVO
SINALIZAÇÃO VALE DO PARAÍBA
ABRIGO 20 – ITAPETI – FIP–4

ANOTAÇÕES

LEGENDA:



INCLUIR CIRCUITO/EQUIPAMENTO



RETIRAR CIRCUITO/EQUIPAMENTO



FIRMA CONTRATADA:

–

Nº ARQUIVO MRS:

TÍTULO DES.:

CAPA
PROJETO EXECUTIVO
SINALIZAÇÃO VALE DO PARAÍBA

ENG.RESP.: HAROLDO ENNES

DATA: 10/11/2023

PROJ.: MÁRCIO MOREIRA

ESCALA: S/ESC.

FORMATO: A3

DES.PROJ.: ANTÔNIO LEAL

REV./DATA: –

FIP4_ABR20_CAPA

SUBST./REF.: –

ÍNDICE

CONTEÚDO

NÚMERO MRS		NÚMERO DA REVISÃO								
		1	2	3	4	5	6	7	8	9
PE-OS-OFIP-001-01	ÍNDICE-TÍTULO/CONTEÚDO/REVISÕES/OBSERVAÇÕES									
PE-OS-OFIP-002-01	SÍMBOLOS									
PE-OS-OFIP-003-01	PLANO DE VIA E SINAL COM CABOS – PVS									
PE-OS-OFIP-004-01	REDE DE DUTOS E CABOS									
PE-OS-OFIP-005-01	AS BUILT DE MALHA DE ATERRAMENTO									
PE-OS-OFIP-006-01	PROGRAMA DO ELECTROLOGIXS									
PE-OS-OFIP-007-01	DISTRIBUIÇÃO DE ENERGIA									
PE-OS-OFIP-008-01	CIRCUITOS DE COMUNICAÇÃO DO ABRIGO									
PE-OS-OFIP-009-01	CONFIGURAÇÃO DO MÓDULO ELECTROLOGIXS									
PE-OS-OFIP-010-01	I/O DE VIA E VITAL DO ELECTROLOGIXS									
PE-OS-OFIP-011-01	ABRIGO 1220 mm X 1220 mm LAYOUT DA PAREDE "A"									
PE-OS-OFIP-012-01	ABRIGO 1220 mm X 1220 mm LAYOUT DA PAREDE "B"									
PE-OS-OFIP-013-01	ABRIGO 1220 mm X 1220 mm LAYOUT DO PAINEL TRASEIRO PAREDE "B"									
PE-OS-OFIP-014-01	ABRIGO 1220 mm X 1220 mm LAYOUT DA PAREDE "C"									
PE-OS-OFIP-015-01	ABRIGO 1220 mm X 1220 mm LAYOUT DA PAREDE "D"									
PE-OS-OFIP-016-01	DETALHE DO PAINEL DE TERMINAIS [TB]									

= DESIGN COMPLETADO

= REVISÃO COMPLETADA

ANOTAÇÕES	A Operação dos circuitos e equipamentos aqui representados não podem ser completamente verificados senão após a sua instalação de modo a formar um sistema completo de sinalização ferroviária e ser devidamente submetido a "Testes de seleção de contatos(BREAKDOWN)" e "Testes operacionais de serviço"(Através de planilhas e fluxo de testes) antes de sua colocação em serviços normal definitivo. ENGENHARIA DE ELETROELETRÔNICA DE PROJETOS	MRS Logística S.A.	TÍTULO DES.: LINHA DE SÃO PAULO ÍNDICE (TÍTULO/CONTEÚDO/REVISÕES/OBSERVAÇÕES) ABR 20 ITAPETI – FIP		
			ENG.RESP.: HAROLDO ENNES	DATA: 02/03/2023	
			PROJ.: MÁRCIO MOREIRA	ESCALA: –	FORMATO: A3
			DES.PROJ.: HYGOR TEODORO	REV./DATA: –	
			Nº ARQUIVO MRS: PE-OS-OFIP-001-01		SUBST./REF.:

CIRCUITO DE VIA ENTRE JUNTAS ISOLANTE	CABO DE PAR TRANÇADO	CONTATO DE ALTA CORRENTE	RELÉ NÃO VITAL	TEST LINK CONECTOR DE TESTE	PAR TRANÇADO	TRANSDUTOR	LAYOUT DO BLOCO DE TERMINAL 2X6
JUNTA ISOLANTE	DISJUNTOR ELÉTRICO	CONTATO DE ALTA CORRENTE MAGNÉTICO	RELÉ PISCA	CONECTOR	FONTE DE ENERGIA AC	DETECTOR DE DESCARRILHAMENTO	TERMINAL RESISTOR 8Ω/25W
JUNTA DE FIM DE SINALIZAÇÃO	INTERRUPTOR DE PÓLO ÚNICO	CONTATO DE OPERAÇÃO DE MÁQUINA DE CHAVE	INTERRUPTOR TOGGLE	CONECTOR DE INTERFACE	MOTOR	CAIXA DE PASSAGEM	
SINALEIRO R = VERMELHO Y = AMARELO G = VERDE	CONTATO FRONT ENERGIZADO	CONTATO DE OPERAÇÃO MANUAL DE MÁQUINA DE CHAVE	SUPRESSOR	TERRA	IMPEDÂNCIA FIXA COM NÚCLEO DE FERRO	POSTE COM ANTENA PLANO TERRA DDvR	
MÁQUINA DE CHAVE ELÉTRICA	CONTATO FRONT DESENERGIZADO	CONTATO DO CIRCUITO DE INDICAÇÃO DA MAQUINA DE CHAVE	EQUALIZADOR	ANOTAÇÕES	RESISTOR VARIÁVEL	SENSOR DE RODA [CONTADOR DE EIXO]	
MÁQUINA DE CHAVE COM TRAVADOR ELÉTRICO	CONTATO BACK ENERGIZADO	RELÉ VITAL TIPO PLUG	TERMINAL UNIVERSAL	DIODO	RESISTOR	CANALETA CABOS	
AMV; SETA SOMBREADA MOSTRA O ALINHAMENTO NORMAL	CONTATO BACK DESENERGIZADO	RELÉ POLARIZADO	TEST LINK (CONECTOR DE TESTE)	LAMP, LED PODE SER G, Y, OU R	SUPRESSOR HÍBRIDO	CONTATO "NA" FECHADO DO SWITCH	
ABRIGOS, DIMENSÃO MOSTRADO NO PLANO 1220X1220mm, 1829X1829mm, 2438X1829mm E 3048X1829mm.	CONTATO POLAR	RELÉ VITAL TIPO DE PRATELEIRA	TERMINAIS	LED	VARISTOR CLAMPER	LAYOUT DO TERMINAL UNIVERSAL	

ANOTAÇÕES

A Operação dos circuitos e equipamentos aqui representados não podem ser completamente verificados senão após a sua instalação de modo a formar um sistema completo de sinalização ferroviária e ser devidamente submetido a "Testes de seleção de contatos(BREAKDOWN)" e "Testes operacionais de serviço"(Através de planilhas e fluxo de testes) antes de sua colocação em serviços normal definitivo.
ENGENHARIA DE ELETROELETRÔNICA DE PROJETOS

CONTROLE INTERNO DE PROJETOS GEPEE	DATA
ELABORADOR: HYGOR TEODORO	02/03/2023
REVISOR: ANTÔNIO LEAL	22/03/2023
APROVADOR: MARCOS REINH	05/04/2023



FIRMA CONTRATADA:
-
Nº ARQUIVO MRS:

TÍTULO DES.: LINHA DE SÃO PAULO
SÍMBOLOS
ABR 20
ITAPETI – FIP

ENG.RESP.:	HAROLDO ENNES	DATA:	02/03/2023	
PROJ.:	MÁRCIO MOREIRA	ESCALA:	—	FORMATO: A3
DES.PROJ.:	HYGOR TEODORO	REV./DATA:	—	
—0S—0FIP—002—01		SUBST./REF.:	—	

PE-0S-0FIP-002-01

435+932

← ESQUERDA PARA ITAPETI

DIREITA PARA SÃO BENTO →


(X)

(E1T) 2EAT

2DAT (D1T)

CONTINUA
NA PÁGINA
PE-OS-OFIP-003-01
FIP 3

CONTINUA
NA PÁGINA
PE-OS-OFST-003-01
FST 1

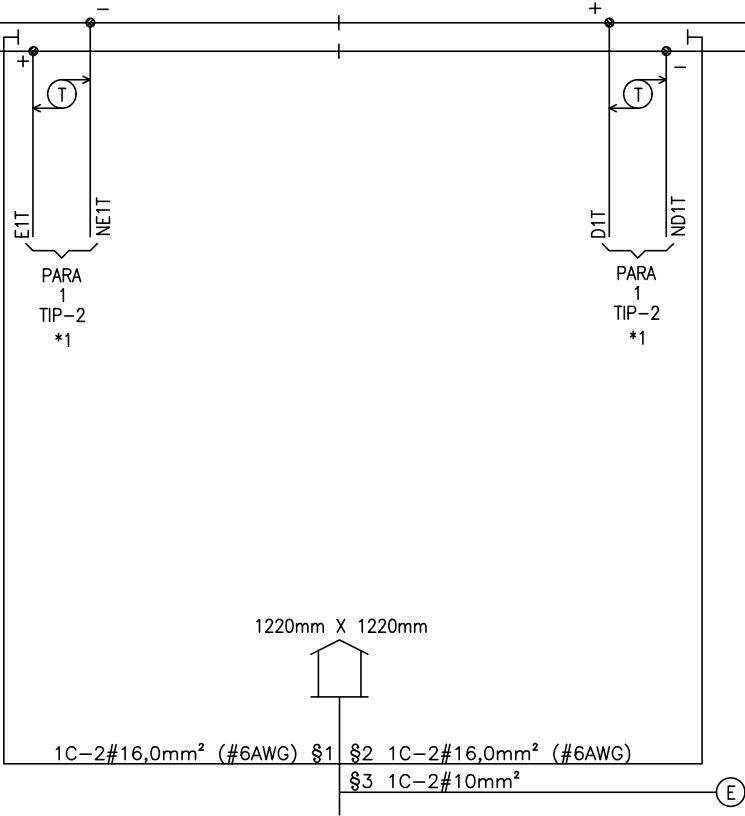

OBSERVAÇÕES:

- 1. (X) = LOCALIZAÇÃO DA HOUSE
- 2. *1 = PARA FL. PE-OS-OFIP-010-01
- 3. § = PARA FL. PE-OS-OFIP-004-01

ANOTAÇÕES

A Operação dos circuitos e equipamentos aqui representados não podem ser completamente verificados senão após a sua instalação de modo a formar um sistema completo de sinalização ferroviária e ser devidamente submetido a "Testes de seleção de contatos(BREAKDOWN)" e "Testes operacionais de serviço"(Através de planilhas e fluxo de testes) antes de sua colocação em serviços normal definitivo.
ENGENHARIA DE ELETROELETRÔNICA DE PROJETOS



TÍTULO DES.: LINHA DE SÃO PAULO
PLANO DE VIA E SINAL COM CABOS – PVS
ABR 20
ITAPETI – FIP

CONTROLE INTERNO DE PROJETOS CEPEE	DATA
ELABORADOR: HYGOR TEODORO	02/03/2023
REVISOR: ANTÔNIO LEAL	22/03/2023
APROVADOR: MARCOS REINH	05/04/2023

FIRMA CONTRATADA:

-

Nº ARQUIVO MRS:

ENG.RESP.: HAROLDO ENNES
PROJ.: MARCIO MOREIRA
DES.PROJ.: HYGOR TEODORO
PE-OS-OFIP-003-01

DATA: 02/03/2023

ESCALA: - FORMATO: A3


REV./DATA: -

SUBST./REF.: -

FIP (4)

← ESQUERDA PARA ITAPETI

DIREITA PARA SÃO BENTO →

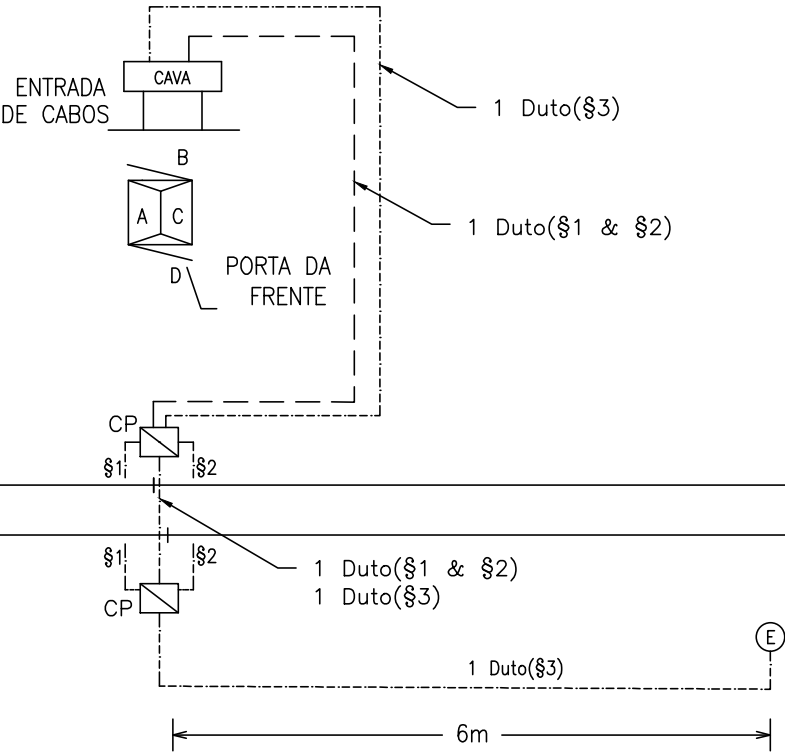

(E1T) 2EAT

(D1T) 2DAT

LEGENDA:

— — — Duto Corrugado 4"

----- Duto Corrugado 2"

OBSERVAÇÕES:

1. DESENHO SEM ESCALA


2. § = VER FL. PE-OS-OFIP-003-01

ANOTAÇÕES	A Operação dos circuitos e equipamentos aqui representados não podem ser completamente verificados senão após a sua instalação de modo a formar um sistema completo de sinalização ferroviária e ser devidamente submetido a "Testes de seleção de contatos(BREAKDOWN)" e "Testes operacionais de serviço"(Através de planilhas e fluxo de testes) antes de sua colocação em serviços normal definitivo. ENGENHARIA DE ELETROELETRÔNICA DE PROJETOS			 Logística S.A.	TÍTULO DES.: LINHA DE SÃO PAULO REDE DE DUTOS E CABOS ABR 20 ITAPETI – FIP		
		CONTROLE INTERNO DE PROJETOS GEPEE	DATA		FIRMA CONTRATADA:	ENG.RESP.: HAROLDO ENNES	DATA: 02/03/2023
		ELABORADOR: HYGOR TEODORO	02/03/2023	-	PROJ.: MÁRCIO MOREIRA	ESCALA: –	FORMATO: A3
		REVISOR: ANTÔNIO LEAL	22/03/2023		DES.PROJ.: HYGOR TEODORO	REV./DATA: –	
		APROVADOR: MARCOS REINH	05/04/2023		Nº ARQUIVO MRS: PE-0S-0FIP-004-01		SUBST./REF.: –

FIP (4)

← ESQUERDA PARA ITAPETI

DIREITA PARA SÃO BENTO →

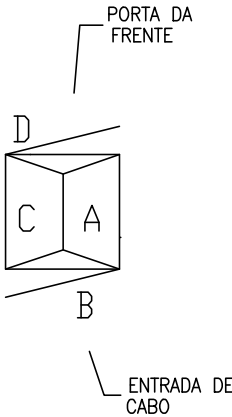

ENTRADA DE ENERGIA
ⓔ

ATENÇÃO:

ESSA PLANTA DEVE SER ATUALIZADA PELO EXECUTOR DO PROJETO COM AS REFERÊNCIA DO ATERRAMENTO DOS ABRIGOS, POSICIONAMENTO DAS HASTES E A EQUIPOTENCIALIZAÇÃO CONFORME AS BUILT.

OBSERVAÇÕES:
1. DESENHO SEM ESCALA

ANOTAÇÕES	A Operação dos circuitos e equipamentos aqui representados não podem ser completamente verificados senão após a sua instalação de modo a formar um sistema completo de sinalização ferroviária e ser devidamente submetido a "Testes de seleção de contatos(BREAKDOWN)" e "Testes operacionais de serviço"(Através de planilhas e fluxo de testes) antes de sua colocação em serviços normal definitivo. ENGENHARIA DE ELETROELETRÔNICA DE PROJETOS			 Logística S.A.	TÍTULO DES.: LINHA DE SÃO PAULO AS BUILT DE MALHA DE ATERRAMENTO ABR 20 ITAPETI – FIP			
		CONTROLE INTERNO DE PROJETOS GEPEE	DATA		FIRMA CONTRATADA:	ENG.RESP.: HAROLDO ENNES	DATA: 02/03/2023	
		ELABORADOR: HYGOR TEODORO	02/03/2023	-	PROJ.: MÁRCIO MOREIRA	ESCALA: -	FORMATO: A3	
		REVISOR: ANTÔNIO LEAL	22/03/2023		DES.PROJ.: HYGOR TEODORO	REV./DATA: -		
		APROVADOR: MARCOS REINH	05/04/2023		Nº ARQUIVO MRS: PE-OS-0FIP-005-01		SUBST./REF.: -	

CONFIGURAÇÃO

ITEM	CONFIGURAÇÃO
ID DO SITE	INDEFINIDO
ID DO CHASSI	32

INFORMAÇÕES DO APLICATIVO VITAL

ITEM	CONFIGURAÇÃO	
NOME	0XXX_XXXXXXX	(✕✕1)
ÍNDICE	XXX	(✕✕1)
EPT CRC	XXXX	(✕✕1)
EPT CHECKSUM	XXXX	(✕✕1)

'DIP SHUNTS' DE SELEÇÃO VITAL

#	NOME	ESTADO	
1	DES LMP DIP	INTACTA	(✕✕1)

OBSERVAÇÕES:

1. ✕ = STATUS ESTABELECIDOS/MODIFICADO USANDO O CDU-1. OS OUTROS SÃO MODIFICADOS USANDO O PROGRAMA ACE.

2. (✕✕1) = INFORMAÇÕES SERÃO ATUALIZADAS COM OS DADOS DO PROGRAMA APLICATIVO DO PROJETO APÓS ELABORAÇÃO DO SOFTWARE


ANOTAÇÕES

A Operação dos circuitos e equipamentos aqui representados não podem ser completamente verificados senão após a sua instalação de modo a formar um sistema completo de sinalização ferroviária e ser devidamente submetido a "Testes de seleção de contatos(BREAKDOWN)" e "Testes operacionais de serviço"(Através de planilhas e fluxo de testes) antes de sua colocação em serviços normal definitivo.
ENGENHARIA DE ELETROELETRÔNICA DE PROJETOS



TÍTULO DES.: LINHA DE SÃO PAULO
PROGRAMA DO ELECTROLOGIXS
ABR 20
ITAPETI — FIP

CONTROLE INTERNO DE PROJETOS GEPEE	DATA	FIRMA CONTRATADA:	ENG.RESP.: HAROLDO ENNES	DATA: 02/03/2023
ELABORADOR: HYGOR TEODORO	02/03/2023	-	PROJ.: MÁRCIO MOREIRA	ESCALA: -
REVISOR: ANTÔNIO LEAL	22/03/2023		DES.PROJ.: HYGOR TEODORO	FORMATO: A3
APROVADOR: MARCOS REINH	05/04/2023	Nº ARQUIVO MRS:	PE-OS-OFIP-006-01	REV./DATA: -
				SUBST./REF.: -

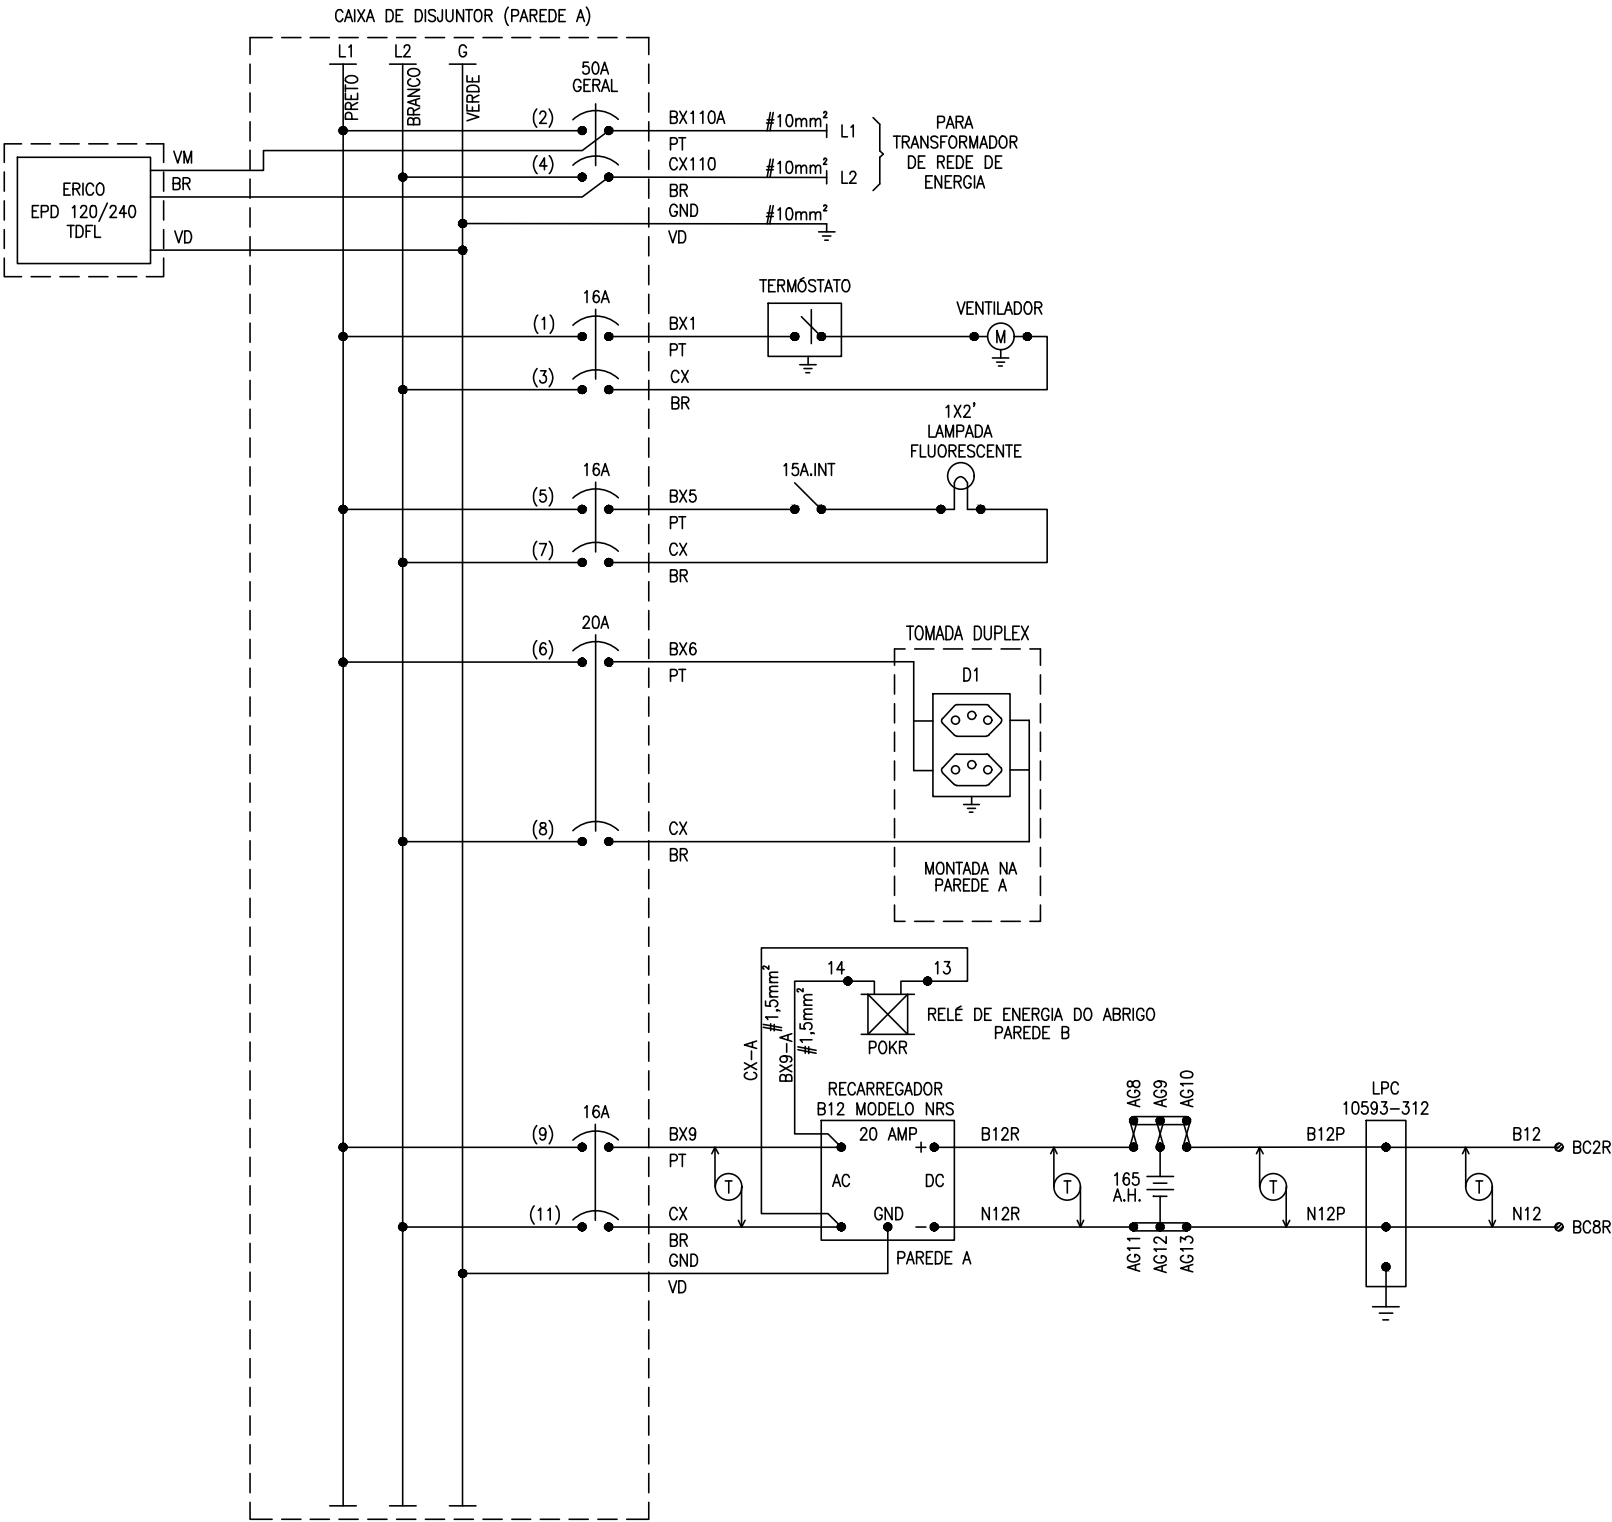

OBSERVAÇÃO:
1. (T) = TRANÇADO
2. CABOS A SEREM INSTALADOS DEVEM SER #6mm² EXCETO QUANDO INDICADO

ANOTAÇÕES

A Operação dos circuitos e equipamentos aqui representados não podem ser completamente verificados senão após a sua instalação de modo a formar um sistema completo de sinalização ferroviária e ser devidamente submetido a "Testes de seleção de contatos(BREAKDOWN)" e "Testes operacionais de serviço"(Através de planilhas e fluxo de testes) antes de sua colocação em serviços normal definitivo.
ENGENHARIA DE ELETROELETRÔNICA DE PROJETOS




TÍTULO DES.:		LINHA DE SÃO PAULO DISTRIBUIÇÃO DE ENERGIA ABR 20 ITAPETI – FIP	
ENG.RESP.:	HAROLDO ENNES	DATA: 02/03/2023	
PROJ.:	MÁRCIO MOREIRA	ESCALA:	FORMATO: A3
DES.PROJ.:	HYGOR TEODORO	REV./DATA:	
SUBST./REF.: –			

CONTROLE INTERNO DE PROJETOS GEPEE	DATA
ELABORADOR: HYGOR TEODORO	02/03/2023
REVISOR: ANTÔNIO LEAL	22/03/2023
APROVADOR: MARCOS REINH	05/04/2023

FIRMA CONTRATADA:
–
Nº ARQUIVO MRS:

PE-OS-0FIP-007-01





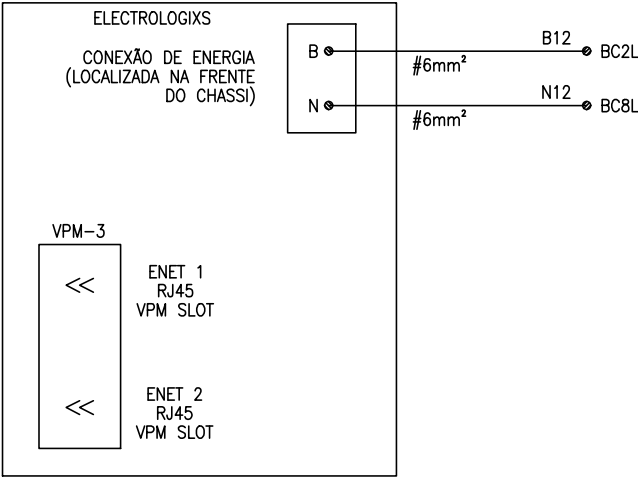


OBSERVAÇÕES:

1. $\textcircled{T}$ = TRANÇADO

2. CABOS A SEREM INSTALADOS DEVEM SER #1,5mm² EXCETO QUANDO INDICADO NA PLANTA

ANOTAÇÕES	A Operação dos circuitos e equipamentos aqui representados não podem ser completamente verificados senão após a sua instalação de modo a formar um sistema completo de sinalização ferroviária e ser devidamente submetido a "Testes de seleção de contatos(BREAKDOWN)" e "Testes operacionais de serviço"(Através de planilhas e fluxo de testes) antes de sua colocação em serviços normal definitivo. ENGENHARIA DE ELETROELETRÔNICA DE PROJETOS	MRS Logística S.A.	TÍTULO DES.: LINHA DE SÃO PAULO CIRCUITOS DE COMUNICAÇÃO DO ABRIGO ABR 20 ITAPETI – FIP		
			ENG.RESP.: HAROLDO ENNES	DATA: 02/03/2023	
			PROJ.: MÁRCIO MOREIRA	ESCALA: –	FORMATO: A3
			DES.PROJ.: HYGOR TEODORO	REV./DATA: –	
			Nº ARQUIVO MRS: PE–OS–OFIP–008–01		SUBST./REF.: –

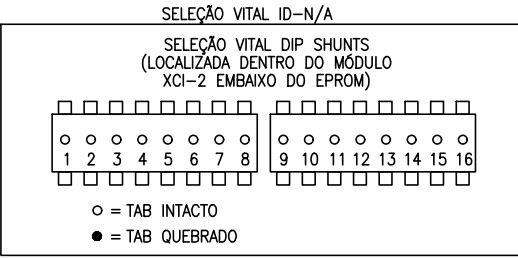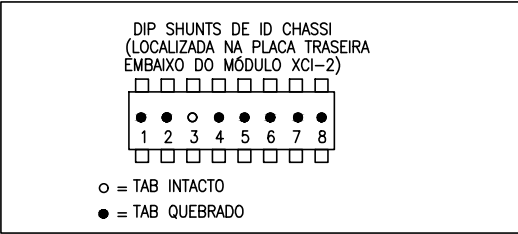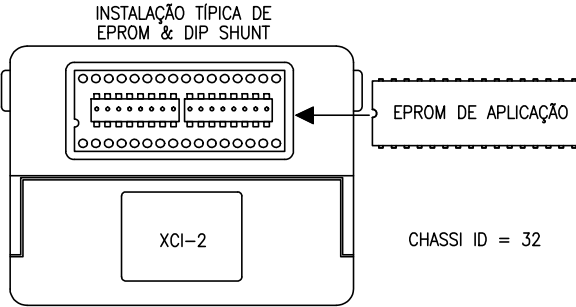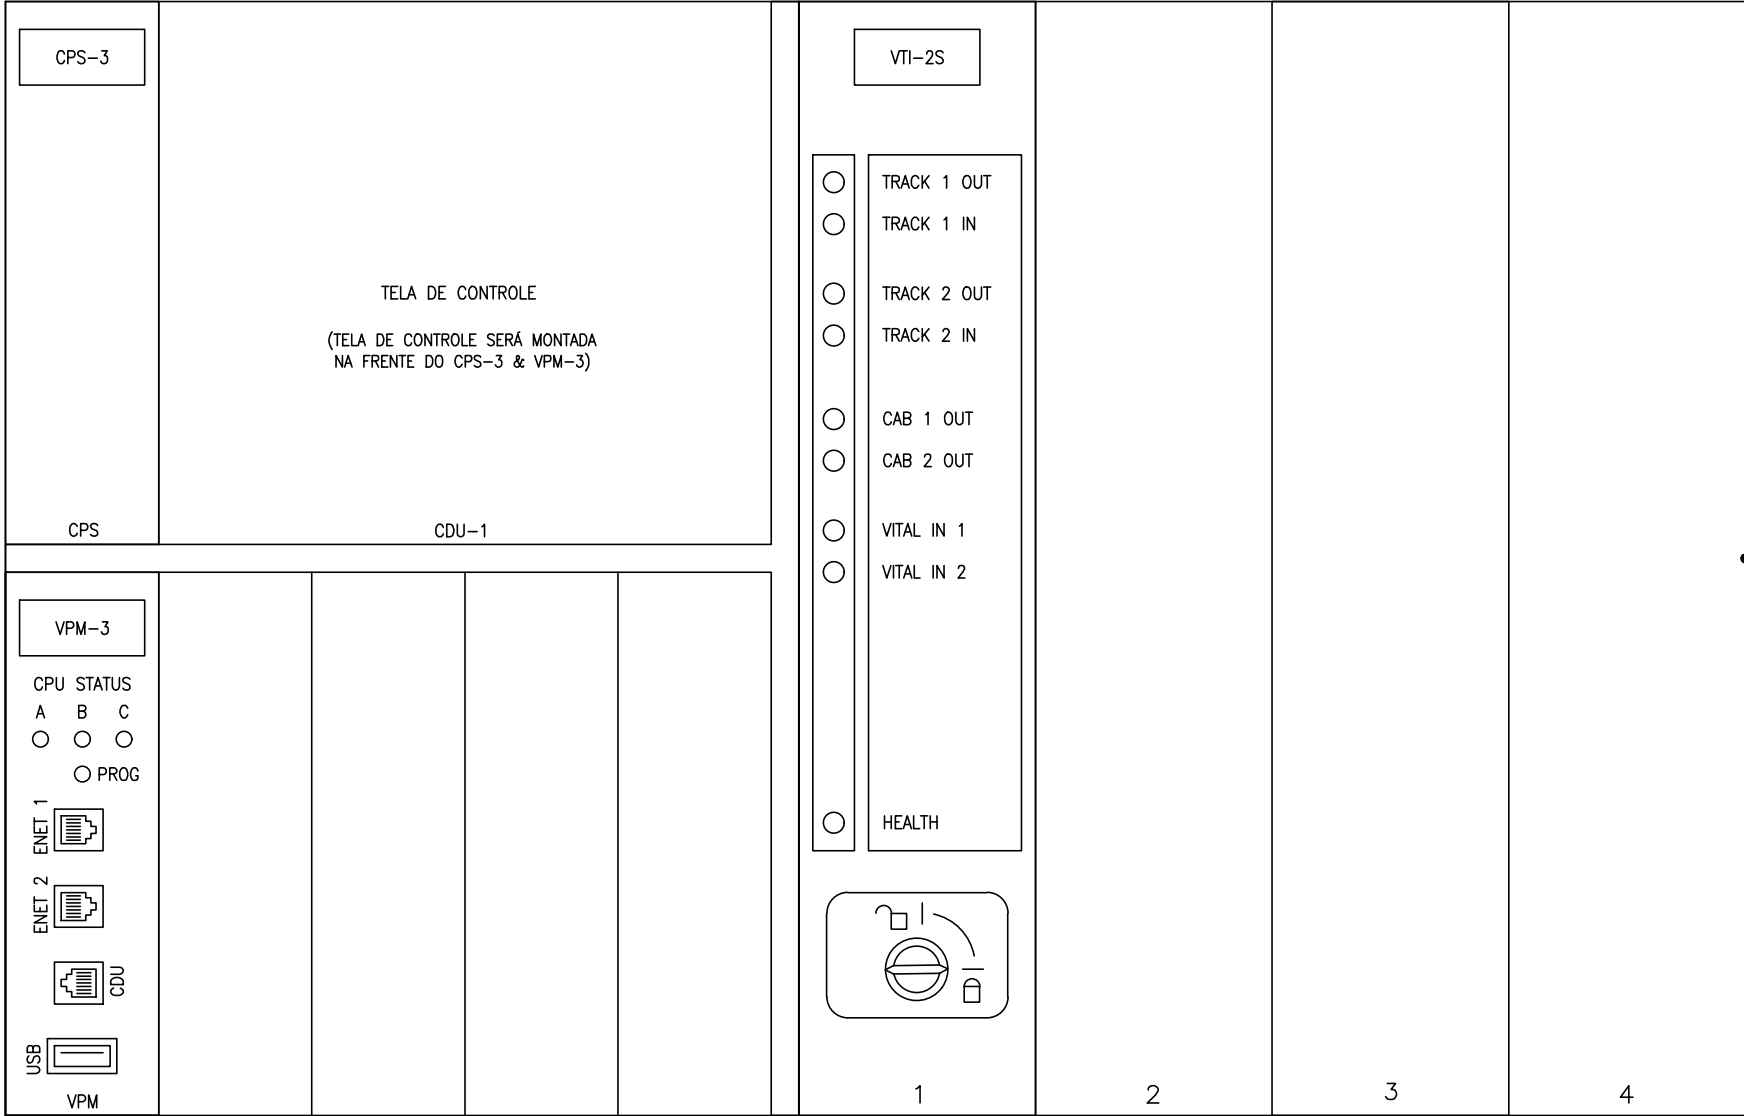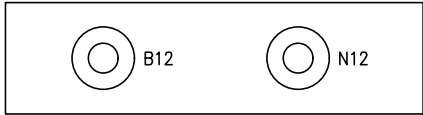

LEGENDA DE MÓDULO
CDU-1 = TELA DE CONTROLE
CPS-3 = UNIDADE DE ENERGIA
VPM-3 = MESTRE PERIFÉRICO VITAL
XCI-2 = INFORMAÇÃO DO CHASSI
VTI-2S = INTERFACE DE VIA VITAL

ANOTAÇÕES


A Operação dos circuitos e equipamentos aqui representados não podem ser completamente verificados senão após a sua instalação de modo a formar um sistema completo de sinalização ferroviária e ser devidamente submetido a "Testes de seleção de contatos(BREAKDOWN)" e "Testes operacionais de serviço"(Através de planilhas e fluxo de testes) antes de sua colocação em serviços normal definitivo.
ENGENHARIA DE ELETROELETRÔNICA DE PROJETOS



TÍTULO DES.: LINHA DE SÃO PAULO
CONFIGURAÇÃO DO MÓDULO ELECTROLOGIXS
ABR 20
ITAPETI – FIP

CONTROLE INTERNO DE PROJETOS GEPEE	DATA
ELABORADOR: HYGOR TEODORO	02/03/2023
REVISOR: ANTÔNIO LEAL	22/03/2023
APROVADOR: MARCOS REINH	05/04/2023

FIRMA CONTRATADA:	ENG.RESP.: HAROLDO ENNES	DATA: 02/03/2023
-	PROJ.: MÁRCIO MOREIRA	ESCALA: -
	DES.PROJ.: HYGOR TEODORO	FORMATO: A3
Nº ARQUIVO MRS:	PE-0S-0FIP-009-01	REV./DATA: -
		SUBST./REF.: -

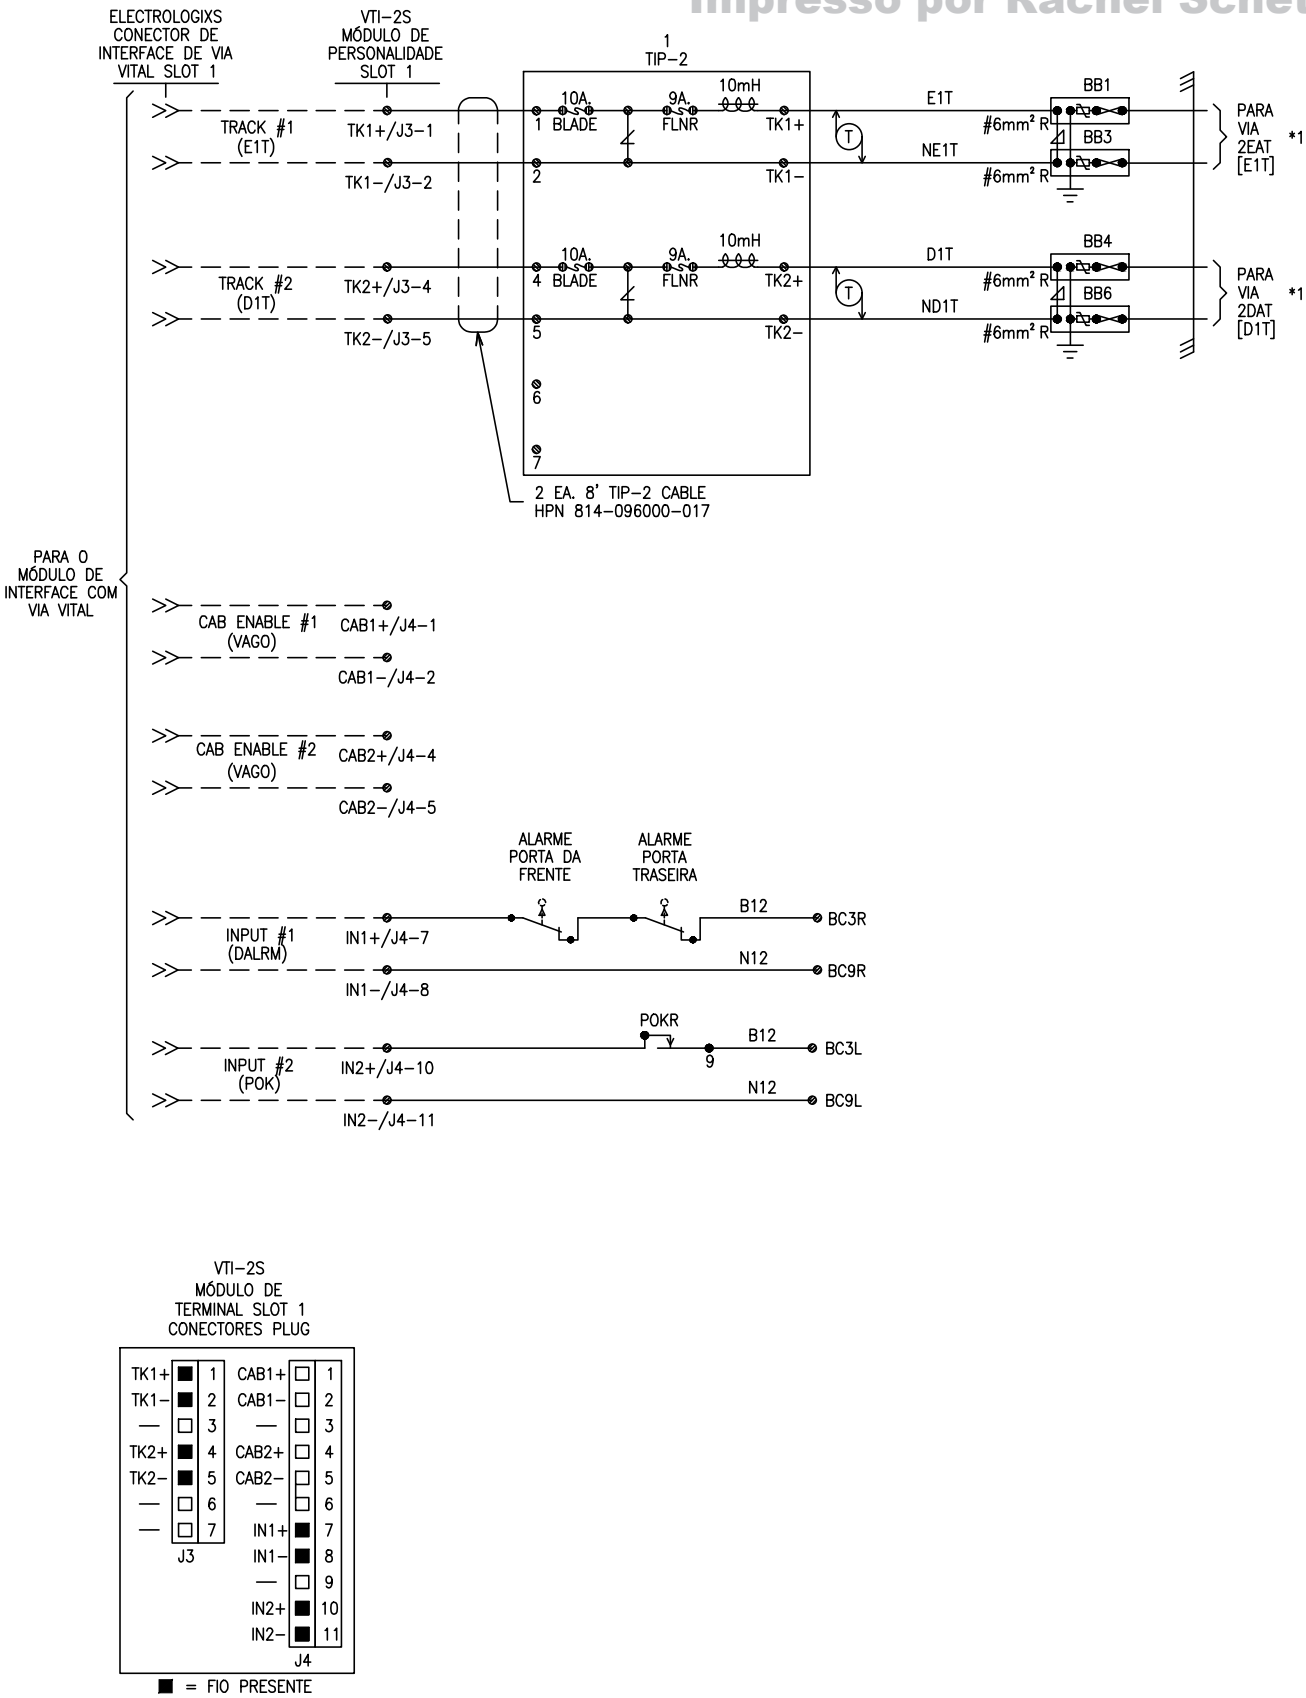

OBSERVAÇÕES:

1. = VARISTOR CLAMPER
2. = EQUALIZADOR
3. ---- = CONEXÃO INTERNA
4. TODOS CABOS DA HOUSE #1,5mm² EXCETO QUANDO INDICADO.
5. *1 = PARA FL. PE-OS-OFIP-003-01
6. CABO UTILIZADO PARA INTERLIGAÇÃO DO VTI AO TIP-2
(1 EA. 8' [2,43m] TIP-2 CABLE HPN 814-096000-017)

ANOTAÇÕES


A Operação dos circuitos e equipamentos aqui representados não podem ser completamente verificados senão após a sua instalação de modo a formar um sistema completo de sinalização ferroviária e ser devidamente submetido a "Testes de seleção de contatos(BREAKDOWN)" e "Testes operacionais de serviço"(Através de planilhas e fluxo de testes) antes de sua colocação em serviços normal definitivo.
ENGENHARIA DE ELETROELETRÔNICA DE PROJETOS



TÍTULO DES.: LINHA DE SÃO PAULO
I/O DE VIA E VITAL DO ELECTROLOGIXS
ABR 20
ITAPETI — FIP

CONTROLE INTERNO DE PROJETOS GEPEE	DATA
ELABORADOR: HYGOR TEODORO	02/03/2023
REVISOR: ANTÔNIO LEAL	22/03/2023
APROVADOR: MARCOS REINH	05/04/2023

FIRMA CONTRATADA: —	ENG.RESP.: HAROLDO ENNES	DATA: 02/03/2023	
	PROJ.: MÁRCIO MOREIRA	ESCALA: —	FORMATO: A3
	DES.PROJ.: HYGOR TEODORO	REV./DATA: —	
N° ARQUIVO MRS: PE-OS-OFIP-010-01		SUBST./REF.: —	

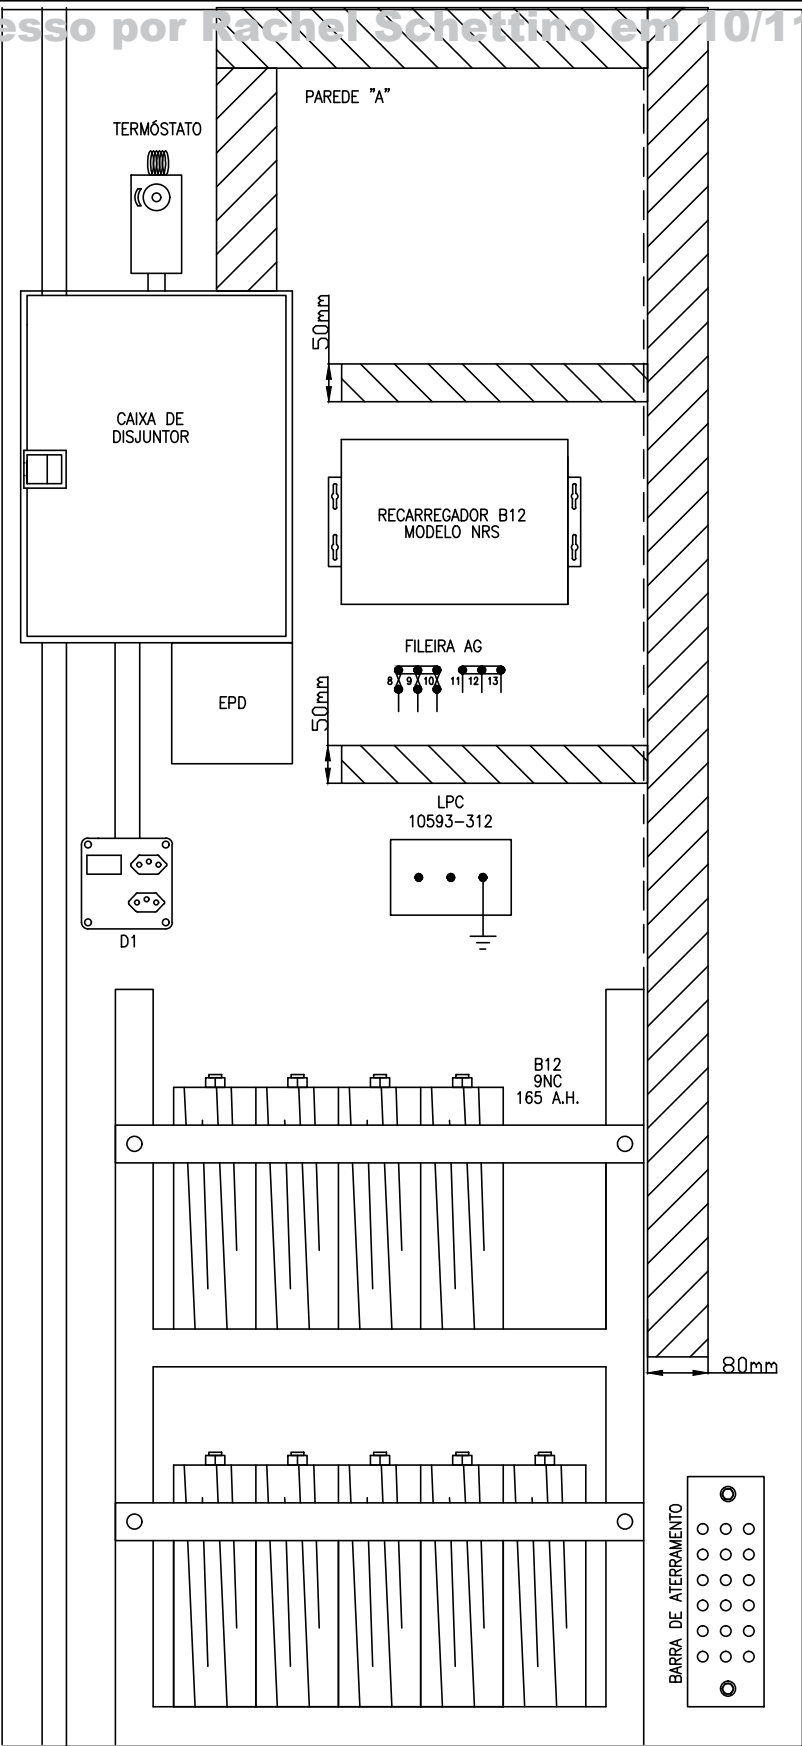

CAIXA DE DISJUNTOR			
1	16A	50A	2
3			4
5	16A	20A	6
7			8
9	16A		10
11			12
13			14
15			16
17			18
19			20

OBSERVAÇÕES:
1. COTAS EM MILÍMETROS

ANOTAÇÕES

A Operação dos circuitos e equipamentos aqui representados não podem ser completamente verificados senão após a sua instalação de modo a formar um sistema completo de sinalização ferroviária e ser devidamente submetido a "Testes de seleção de contatos(BREAKDOWN)" e "Testes operacionais de serviço"(Através de planilhas e fluxo de testes) antes de sua colocação em serviços normal definitivo.
ENGENHARIA DE ELETROELETRÔNICA DE PROJETOS


CONTROLE INTERNO DE PROJETOS GEPEE	DATA
ELABORADOR: HYGOR TEODORO	02/03/2023
REVISOR: ANTÔNIO LEAL	22/03/2023
APROVADOR: MARCOS REINH	05/04/2023



FIRMA CONTRATADA:

Nº ARQUIVO MRS:

TÍTULO DES.: LINHA DE SÃO PAULO ABRIGO 1220 mm X 1220 mm LAYOUT DA PAREDE "A" ABR 20 ITAPETI – FIP		
ENG.RESP.: HAROLDO ENNES	DATA: 02/03/2023	
PROJ.: MÁRCIO MOREIRA	ESCALA: 1:10	FORMATO: A3
DES.PROJ.: HYGOR TEODORO	REV./DATA: –	
Nº ARQUIVO MRS: PE–OS–0FIP–011–01		SUBST./REF.: –

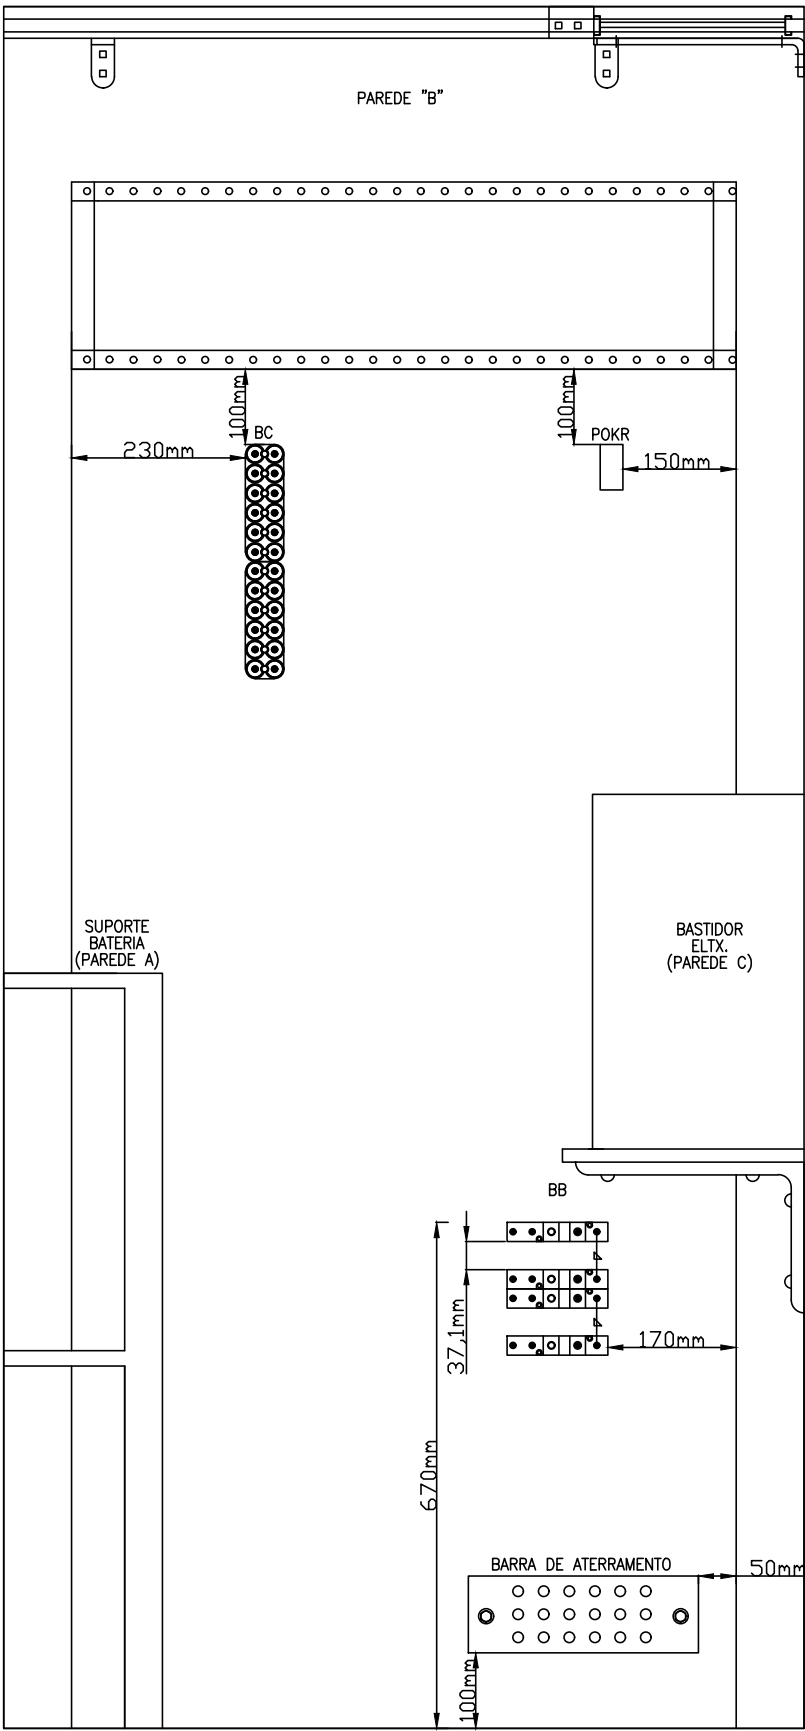

1/1	1/2	1/3	1/4	1/5	1/6	1/7	1/8	1/9	1/10	1/11	1/12	1/13

CARREIRA DE
RELÉ

LEGENDA DE RELÉ

- ▼ = CONTATO FRONT UTILIZADO
- ∨ = CONTATO FRONT NÃO UTILIZADO
- = CALCANHAR
- ^ = CONTATO BACK NÃO UTILIZADO
- ▲ = CONTATO BACK UTILIZADO

REFERÊNCIA CRUZADA


TABELA MRS	ALSTOM RELAY PN	SAFETTRAN RELAY PN	DIAGRAMA DE CONTATO

VISÃO DE TRÁS DOS RELÉS

3	2	1
∨	∨	∨
—	—	—
^	∨	^
∨	—	∨
—	—	2
^	^	1
B		

POKR		
9	F	11
10	—	12

KHAU-17A12-120
27E166 MONTADO NA PAREDE

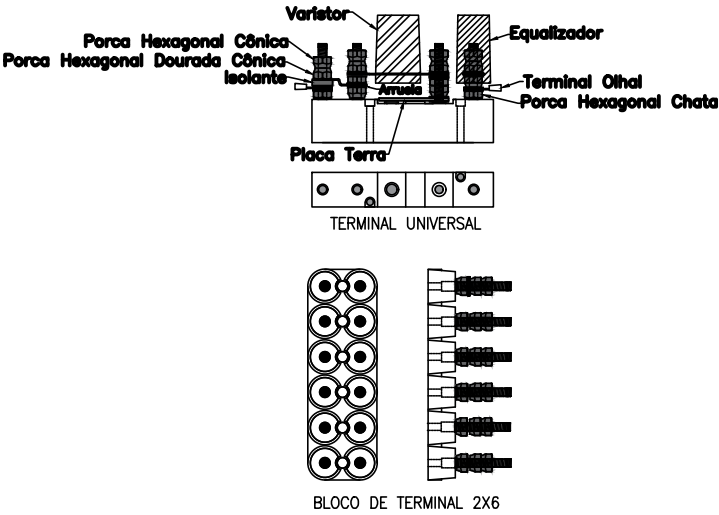

OBSERVAÇÕES:
1. COTAS EM MILÍMETROS

ANOTAÇÕES

A Operação dos circuitos e equipamentos aqui representados não podem ser completamente verificados senão após a sua instalação de modo a formar um sistema completo de sinalização ferroviária e ser devidamente submetido a "Testes de seleção de contatos(BREAKDOWN)" e "Testes operacionais de serviço"(Através de planilhas e fluxo de testes) antes de sua colocação em serviços normal definitivo.
ENGENHARIA DE ELETROELETRÔNICA DE PROJETOS



TÍTULO DES.: LINHA DE SÃO PAULO
ABRIGO 1220 mm X 1220 mm LAYOUT DA PAREDE "B"
ABR 20
ITAPETI — FIP

CONTROLE INTERNO DE PROJETOS GEPEE	DATA
ELABORADOR: HYGOR TEODORO	02/03/2023
REVISOR: ANTÔNIO LEAL	22/03/2023
APROVADOR: MARCOS REINH	05/04/2023

FIRMA CONTRATADA:

—

N° ARQUIVO MRS:

ENG.RESP.: HAROLDO ENNES

PROJ.: MÁRCIO MOREIRA

DES.PROJ.: HYGOR TEODORO

PE-0S-0FIP-012-01


DATA: 02/03/2023

ESCALA: 1:10

FORMATO: A3


REV./DATA: —

SUBST./REF.: —

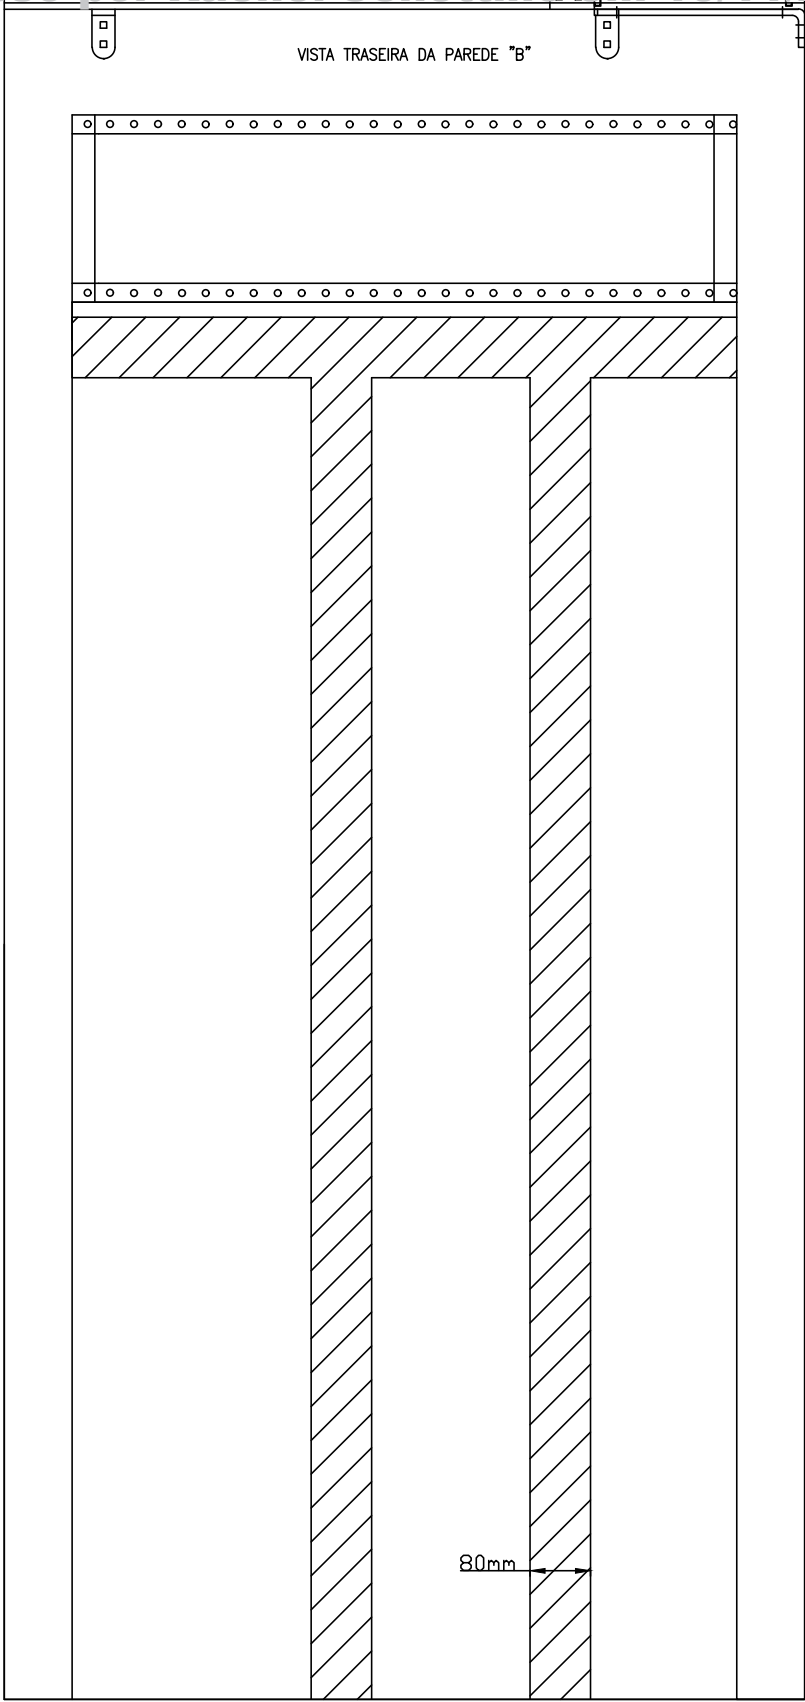

OBSERVAÇÕES:
1. COTAS EM MILÍMETROS

ANOTAÇÕES	A Operação dos circuitos e equipamentos aqui representados não podem ser completamente verificados senão após a sua instalação de modo a formar um sistema completo de sinalização ferroviária e ser devidamente submetido a "Testes de seleção de contatos(BREAKDOWN)" e "Testes operacionais de serviço"(Através de planilhas e fluxo de testes) antes de sua colocação em serviços normal definitivo. ENGENHARIA DE ELETROELETRÔNICA DE PROJETOS	MRS Logística S.A.	TÍTULO DES.: LINHA DE SÃO PAULO ABRIGO 1220mm X 1220mm LAYOUT DO PAINEL TRASEIRO PAREDE "B" ABR 20 ITAPETI – FIP					
			FIRMA CONTRATADA: —		ENG.RESP.: HAROLDO ENNES		DATA: 02/03/2023	
					PROJ.: MÁRCIO MOREIRA		ESCALA: 1:10	FORMATO: A3
					DES.PROJ.: HYGOR TEODORO		REV./DATA: —	
					N° ARQUIVO MRS: PE–OS–0FIP–013–01		SUBST./REF.: —	
CONTROLE INTERNO DE PROJETOS GEPEE		DATA						
ELABORADOR: HYGOR TEODORO		02/03/2023						
REVISOR: ANTÔNIO LEAL		22/03/2023						
APROVADOR: MARCOS REINH		05/04/2023						

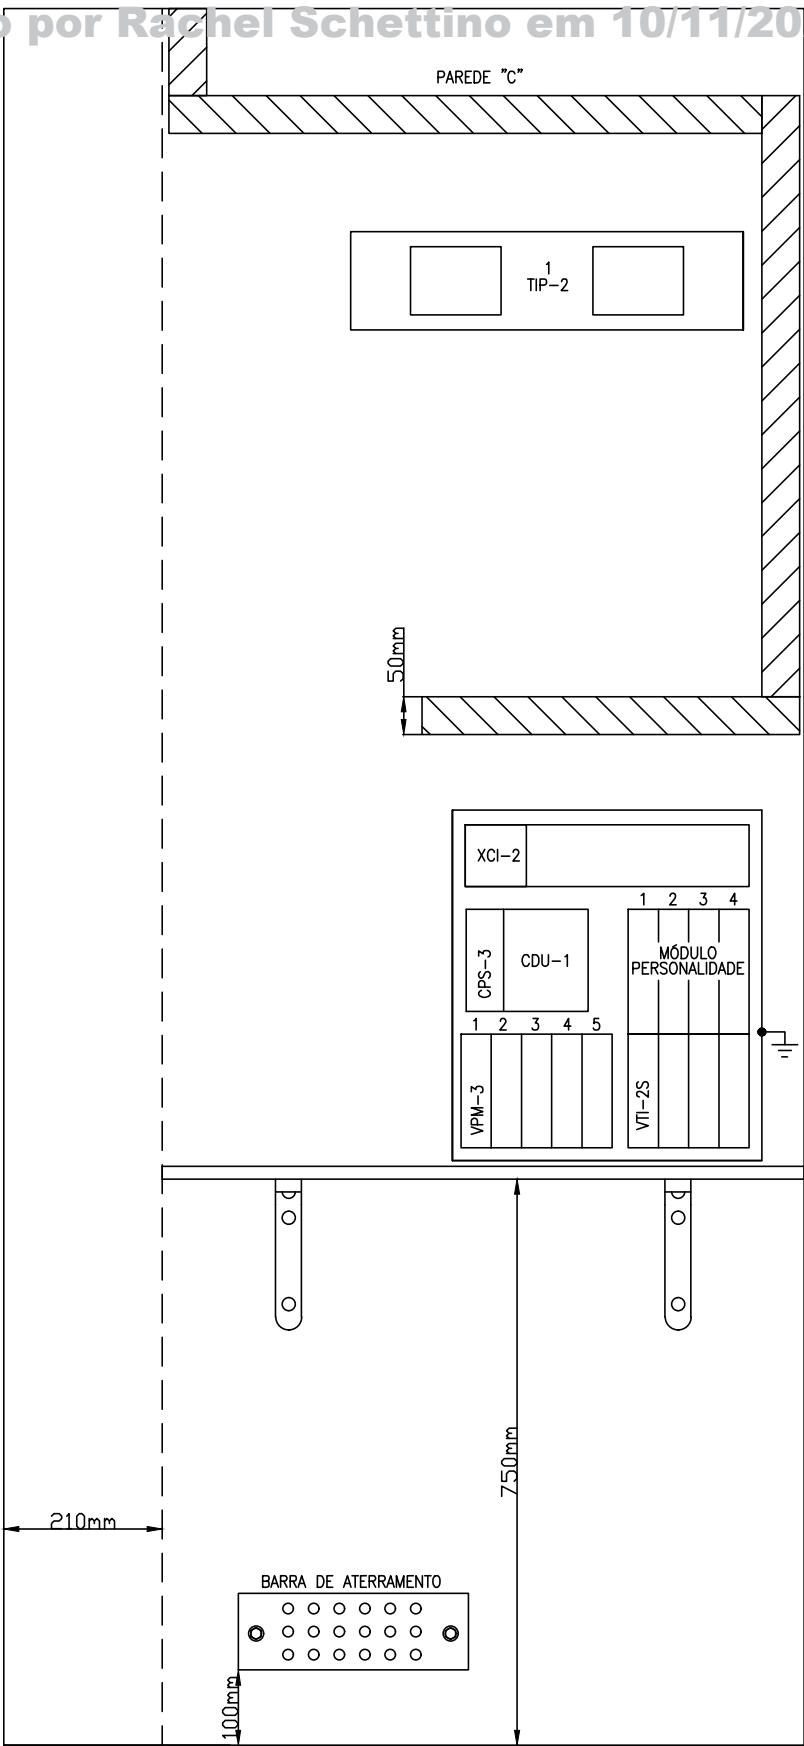

OBSERVAÇÕES:
1. COTAS EM MILÍMETROS

ANOTAÇÕES	A Operação dos circuitos e equipamentos aqui representados não podem ser completamente verificados senão após a sua instalação de modo a formar um sistema completo de sinalização ferroviária e ser devidamente submetido a "Testes de seleção de contatos(BREAKDOWN)" e "Testes operacionais de serviço"(Através de planilhas e fluxo de testes) antes de sua colocação em serviços normal definitivo. ENGENHARIA DE ELETROELETRÔNICA DE PROJETOS		MRS Logística S.A.	TÍTULO DES.: LINHA DE SÃO PAULO		
				ABRIGO 1220 mm X 1220 mm LAYOUT DA PAREDE "C"		
				ABR 20		
				ITAPETI – FIP		
		CONTROLE INTERNO DE PROJETOS GEPEE	DATA	FIRMA CONTRATADA: -	ENG.RESP.: HAROLDO ENNES	DATA: 02/03/2023
		ELABORADOR: HYGOR TEODORO	02/03/2023		PROJ.: MÁRCIO MOREIRA	ESCALA: 1:10 FORMATO: A3
		REVISOR: ANTÔNIO LEAL	22/03/2023		DES.PROJ.: HYGOR TEODORO	REV./DATA: -
		APROVADOR: MARCOS REINH	05/04/2023		SUBST./REF.: -	
				Nº ARQUIVO MRS:	PE-0S-0FIP-014-01	

PAREDE "D"

BASTIDOR
ELTX.
(PAREDE C)

SUPORTE
BATERIA
(PAREDE A)

OBSERVAÇÕES:
1. COTAS EM MILÍMETROS

ANOTAÇÕES

A Operação dos circuitos e equipamentos aqui representados não podem ser completamente verificados senão após a sua instalação de modo a formar um sistema completo de sinalização ferroviária e ser devidamente submetido a "Testes de seleção de contatos(BREAKDOWN)" e "Testes operacionais de serviço"(Através de planilhas e fluxo de testes) antes de sua colocação em serviços normal definitivo.
ENGENHARIA DE ELETROELETRÔNICA DE PROJETOS

CONTROLE INTERNO DE PROJETOS GEPEE	DATA
ELABORADOR: HYGOR TEODORO	02/03/2023
REVISOR: ANTÔNIO LEAL	22/03/2023
APROVADOR: MARCOS REINH	05/04/2023



FIRMA CONTRATADA:

-


Nº ARQUIVO MRS:

TÍTULO DES.: LINHA DE SÃO PAULO
ABRIGO 1220 mm X 1220 mm LAYOUT DA PAREDE "D"
ABR 20
ITAPETI – FIP

ENG.RESP.: HAROLDO ENNES
PROJ.: MÁRCIO MOREIRA
DES.PROJ.: HYGOR TEODORO

DATA: 02/03/2023
ESCALA: 1:10 FORMATO: A3
REV./DATA: -
SUBST./REF.: -

PE-0S-0FIP-015-01

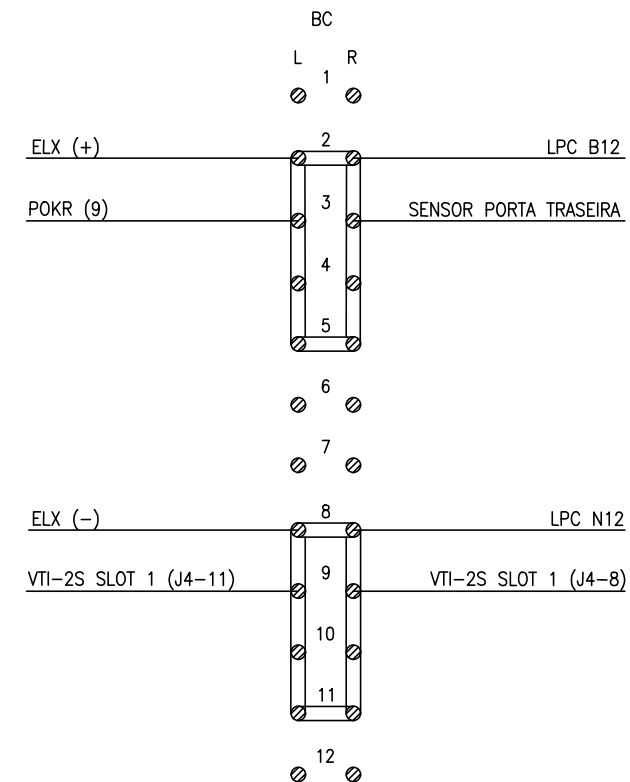

L B D 4 T R

ESQUERDA ———— ↑
INFERIOR ———— ↑
CARREIRA ———— ↑

————— ↓ DIREITA
————— ↓ SUPERIOR
————— ↓ NÚMERO DO TERMINAL

 = SUPRESSOR
 = VARISTOR CLAMPER
 = SUPRESSOR HÍBRIDO
 = EQUALIZADOR
 = PINO DE TERMINAL
 = LINK DE TESTE
 = LINK SOLIDO
 = TERRA

A Operação dos circuitos e equipamentos aqui representados não podem ser completamente verificados senão após a sua instalação de modo a formar um sistema completo de sinalização ferroviária e ser devidamente submetido a "Testes de seleção de contatos(BREAKDOWN)" e "Testes operacionais de serviço"(Através de planilhas e fluxo de testes) antes de sua colocação em serviços normal definitivo.

ENGENHARIA DE ELETROELETRÔNICA DE PROJETOS



LINHA DE SÃO PAULO
 DETALHE DO PAINEL DE TERMINAIS [TB]
 ABR 20
 ITAPETI – FIP

FIRMA CONTRATADA:

PE-OS-OFIP-016-01

ENG.RESP.:	HAROLDO ENNES	DATA:	02/03/2023
PROJ.:	MÁRCIO MOREIRA	ESCALA:	—
DES.PROJ.:	HYGOR TEODORO	FORMATO:	A3
		REV./DATA:	—
E-05-051P-016-01		SUBST./REF.:	—

ANOTAÇÕES