

Gerência de Engenharia e Projetos de Eletroeletrônica

PROJETO EXECUTIVO
SINALIZAÇÃO VALE DO PARAÍBA
ABRIGO 25 – SÃO JOSÉ DOS CAMPOS – FSJ–5

ANOTAÇÕES

LEGENDA:



INCLUIR CIRCUITO/EQUIPAMENTO



RETIRAR CIRCUITO/EQUIPAMENTO



FIRMA CONTRATADA:

–

Nº ARQUIVO MRS:

TÍTULO DES.:

CAPA
PROJETO EXECUTIVO
SINALIZAÇÃO VALE DO PARAÍBA

ENG.RESP.: HAROLDO ENNES

DATA: 09/03/2023

PROJ.: MÁRCIO MOREIRA

ESCALA: S/ESC. FORMATO: A3

DES.PROJ.: ANTÔNIO LEAL

REV./DATA: –

FSJ5_ABR25_CAPA

SUBST./REF.: –

ÍNDICE

CONTEÚDO

	NÚMERO MRS		NÚMERO DA REVISÃO								
			1	2	3	4	5	6	7	8	9
✖✖1	EE-SA-OIWO-XXX-XX	MAPA DE SINAIS	✖								
✖✖1	EE-SA-OIWO-XXX-XX	MAPA DE SINAIS	✖								
	PE-OS-OFSJ-001-01	ÍNDICE-TÍTULO/CONTEÚDO/REVISÕES/OBSERVAÇÕES	✖	✖							
	PE-OS-OFSJ-002-01	SÍMBOLOS									
	PE-OS-OFSJ-003-01	PLANO DE VIA E SINAL COM CABOS – PVS	✖	✖							
	PE-OS-OFSJ-004-01	REDE DE DUTOS E CABOS									
	PE-OS-OFSJ-005-01	AS BUILT DE MALHA DE ATERRAMENTO									
	PE-OS-OFSJ-006-01	PROGRAMA DO ELECTROLOGIXS	✖	✖							
	PE-OS-OFSJ-007-01	PROGRAMA CBTC DO ELECTROLOGIXS									
	PE-OS-OFSJ-008-01	TABELA E DESCRIÇÃO DAS FUNÇÕES DE CONTROLE E INDICAÇÃO									
	PE-OS-OFSJ-009-01	DISTRIBUIÇÃO DE ENERGIA									
	PE-OS-OFSJ-010-01	CIRCUITOS DE COMUNICAÇÃO DO ABRIGO									
	PE-OS-OFSJ-011-01	CONFIGURAÇÃO DO MÓDULO ELECTROLOGIXS									
	PE-OS-OFSJ-012-01	CIRCUITOS DE VIA									
	PE-OS-OFSJ-013-01	I/O DE VIA E VITAL DO ELECTROLOGIXS	✖	✖							
OBSOLETAR	PE-OS-OFSJ-014-01	CIRCUITOS DOS SINAIS 22E, 14D E 16D	✖								
	PE-OS-OFSJ-014-02	CIRCUITOS DOS SINAIS 18E, 12D E 14D									
	PE-OS-OFSJ-015-01	CIRCUITOS I/O DO ELECTROLOGIXS SLOT 5									
	PE-OS-OFSJ-016-01	DIAGRAMA TRANSDUTOR/MPF – 1 CANAL									
	PE-OS-OFSJ-017-01	CIRCUITOS DA MÁQUINA DE CHAVE 15									
	PE-OS-OFSJ-018-01	LAYOUT DO PAINEL DE CONTROLE LOCAL									
	PE-OS-OFSJ-019-01	ABRIGO 1829mm x 1829mm LAYOUT DA PAREDE "A"									
	PE-OS-OFSJ-020-01	ABRIGO 1829mm x 1829mm LAYOUT DA PAREDE "B"	✖	✖							
	PE-OS-OFSJ-021-01	ABRIGO 1829mm x 1829mm LAYOUT DO PAINEL TRASEIRO PAREDE "B"									
	PE-OS-OFSJ-022-01	ABRIGO 1829mm x 1829mm LAYOUT DA PAREDE "C"									
	PE-OS-OFSJ-023-01	ABRIGO 1829mm x 1829mm LAYOUT DA PAREDE "D"									
	PE-OS-OFSJ-024-01	DETALHE DO PAINEL DE TERMINAIS [TB]	✖	✖							

= DESIGN COMPLETADO

= REVISÃO COMPLETADA

OBSERVAÇÕES:

1.(✖✖1) = ESPAÇO SERÁ PREENCHIDO EM CONJUNTO COM O AS BUILT

ANOTAÇÕES	REV. 1 – 18/05/2023		A Operação dos circuitos e equipamentos aqui representados não podem ser completamente verificados senão após a sua instalação de modo a formar um sistema completo de sinalização ferroviária e ser devidamente submetido a "Testes de seleção de contatos(BREAKDOWN)" e "Testes operacionais de serviço"(Através de planilhas e fluxo de testes) antes de sua colocação em serviços normal definitivo. ENGENHARIA DE ELETROELETRÔNICA DE PROJETOS		MRS Logística S.A.	TÍTULO DES.: LINHA DE SÃO PAULO ÍNDICE (TÍTULO/CONTEÚDO/REVISÕES/OBSERVAÇÕES) ABR 25 SÃO JOSÉ DOS CAMPOS – FSJ	
	REV. 2 – 04/10/2023					FIRMA CONTRATADA:		ENG.RESP.: HAROLDO ENNES		DATA: 27/01/2023	
	REV. 3 – 04/10/2023					-		PROJ.: MÁRCIO MOREIRA		ESCALA: –		FORMATO: A3	
	REV. 4 – 04/10/2023					-		DES.PROJ.: ANTÔNIO LEAL		REV./DATA: 2 – 04/10/2023	
	REV. 5 – 04/10/2023					-		Nº ARQUIVO MRS: PE-OS-OFSJ-001-01		SUBST./REF.:	
REV. 6 – 04/10/2023		REV. 7 – 04/10/2023		REV. 8 – 04/10/2023		REV. 9 – 04/10/2023		REV. 10 – 04/10/2023		REV. 11 – 04/10/2023		REV. 12 – 04/10/2023		REV. 13 – 04/10/2023		REV. 14 – 04/10/2023		REV. 15 – 04/10/2023		REV. 16 – 04/10/2023		REV. 17 – 04/10/2023		REV. 18 – 04/10/2023		REV. 19 – 04/10/2023		REV. 20 – 04/10/2023		REV. 21 – 04/10/2023		REV. 22 – 04/10/2023		REV. 23 – 04/10/2023		REV. 24 – 04/10/2023		REV. 25 – 04/10/2023		REV. 26 – 04/10/2023		REV. 27 – 04/10/2023		REV. 28 – 04/10/2023		REV. 29 – 04/10/2023		REV. 30 – 04/10/2023		REV. 31 – 04/10/2023		REV. 32 – 04/10/2023		REV. 33 – 04/10/2023		REV. 34 – 04/10/2023		REV. 35 – 04/10/2023		REV. 36 – 04/10/2023		REV. 37 – 04/10/2023		REV. 38 – 04/10/2023		REV. 39 – 04/10/2023		REV. 40 – 04/10/2023		REV. 41 – 04/10/2023		REV. 42 – 04/10/2023		430 – 04/10/2023		REV. 431 – 04/10/2023		REV. 432 – 04/10/2023		REV. 433 – 04/10/2023		REV. 434 – 04/10/2023		REV. 435 – 04/10/2023		REV. 436 – 04/10/2023		REV. 437 – 04/10/2023		REV. 438 – 04/10/2023		REV. 439 – 04/10/2023		REV. 440 – 04/10/2023		REV. 441 – 04/10/2023		REV. 442 – 04/10/2023		REV. 443 – 04/10/2023		REV. 444 – 04/10/2023		REV. 445 – 04/10/2023		REV. 446 – 04/10/2023		REV. 447 – 04/10/2023		REV. 448 – 04/10/2023		REV. 449 – 04/10/2023		REV. 450 – 04/10/2023		REV. 451 – 04/10/2023		REV. 452 – 04/10/2023		REV. 453 – 04/10/2023		REV. 454 – 04/10/2023		REV. 455 – 04/10/2023		REV. 456 – 04/10/2023		REV. 457 – 04/10/2023		REV. 458 – 04/10/2023		REV. 459 – 04/10/2023		REV. 460 – 04/10/2023		REV. 461 – 04/10/2023		REV. 462 – 04/10/2023		REV. 463 – 04/10/2023		REV. 464 – 04	

CIRCUITO DE VIA ENTRE JUNTAS ISOLANTE	CABO DE PAR TRANÇADO	CONTATO DE ALTA CORRENTE	RELÉ NÃO VITAL	TEST LINK CONECTOR DE TESTE	PAR TRANÇADO	TRANSDUTOR	LAYOUT DO BLOCO DE TERMINAL 2X6
JUNTA ISOLANTE	DISJUNTOR ELÉTRICO	CONTATO DE ALTA CORRENTE MAGNÉTICO	RELÉ PISCA	CONECTOR	FONTE DE ENERGIA AC	DETECTOR DE DESCARRILHAMENTO	TERMINAL RESISTOR 8Ω/25W
JUNTA DE FIM DE SINALIZAÇÃO	INTERRUPTOR DE PÓLO ÚNICO	CONTATO DE OPERAÇÃO DE MÁQUINA DE CHAVE	INTERRUPTOR TOGGLE	CONECTOR DE INTERFACE	MOTOR	CAIXA DE PASSAGEM	
SINALEIRO R = VERMELHO Y = AMARELO G = VERDE	CONTATO FRONT ENERGIZADO	CONTATO DE OPERAÇÃO MANUAL DE MÁQUINA DE CHAVE	SUPRESSOR	TERRA	IMPEDÂNCIA FIXA COM NÚCLEO DE FERRO	POSTE COM ANTENA PLANO TERRA DDvR	
MÁQUINA DE CHAVE ELÉTRICA	CONTATO FRONT DESENERGIZADO	CONTATO DO CIRCUITO DE INDICAÇÃO DA MAQUINA DE CHAVE	EQUALIZADOR	ANOTAÇÕES	RESISTOR VARIÁVEL	SENSOR DE RODA [CONTADOR DE EIXO]	
MÁQUINA DE CHAVE COM TRAVADOR ELÉTRICO	CONTATO BACK ENERGIZADO	RELÉ VITAL TIPO PLUG	TERMINAL UNIVERSAL	DIODO	RESISTOR	CANALETA CABOS	
AMV; SETA SOMBREADA MOSTRA O ALINHAMENTO NORMAL	CONTATO BACK DESENERGIZADO	RELÉ POLARIZADO	TEST LINK (CONECTOR DE TESTE)	LAMP, LED PODE SER G, Y, OU R	SUPRESSOR HÍBRIDO	CONTATO "NA" FECHADO DO SWITCH	
ABRIGOS, DIMENSÃO MOSTRADO NO PLANO 1220X1220mm, 1829X1829mm, 2438X1829mm E 3048X1829mm.	CONTATO POLAR	RELÉ VITAL TIPO DE PRATELEIRA	TERMINAIS	LED	VARISTOR CLAMPER	LAYOUT DO TERMINAL UNIVERSAL	

ANOTAÇÕES

A Operação dos circuitos e equipamentos aqui representados não podem ser completamente verificados senão após a sua instalação de modo a formar um sistema completo de sinalização ferroviária e ser devidamente submetido a "Testes de seleção de contatos(BREAKDOWN)" e "Testes operacionais de serviço"(Através de planilhas e fluxo de testes) antes de sua colocação em serviços normal definitivo.
ENGENHARIA DE ELETROELETRÔNICA DE PROJETOS

CONTROLE INTERNO DE PROJETOS GEPEE	DATA
ELABORADOR: ANTÔNIO LEAL	27/01/2023
REVISOR: MÁRCIO MOREIRA	07/02/2023
APROVADOR: MARCOS REINH	28/02/2023



FIRMA CONTRATADA:

Nº ARQUIVO MRS:

TÍTULO DES.:

LINHA DE SÃO PAULO
SÍMBOLOS
ABR 25
SÃO JOSÉ DOS CAMPOS – FSJ

ENG.RESP.: **HAROLDO ENNES**

PROJ.: **MÁRCIO MOREIRA**

DES.PROJ.: **ANTÔNIO LEAL**


DATA: **27/01/2023**

ESCALA: **—** FORMATO: **A3**

REV./DATA: **—**


SUBST./REF.: **—**

PE-0S-0FSJ-002-01

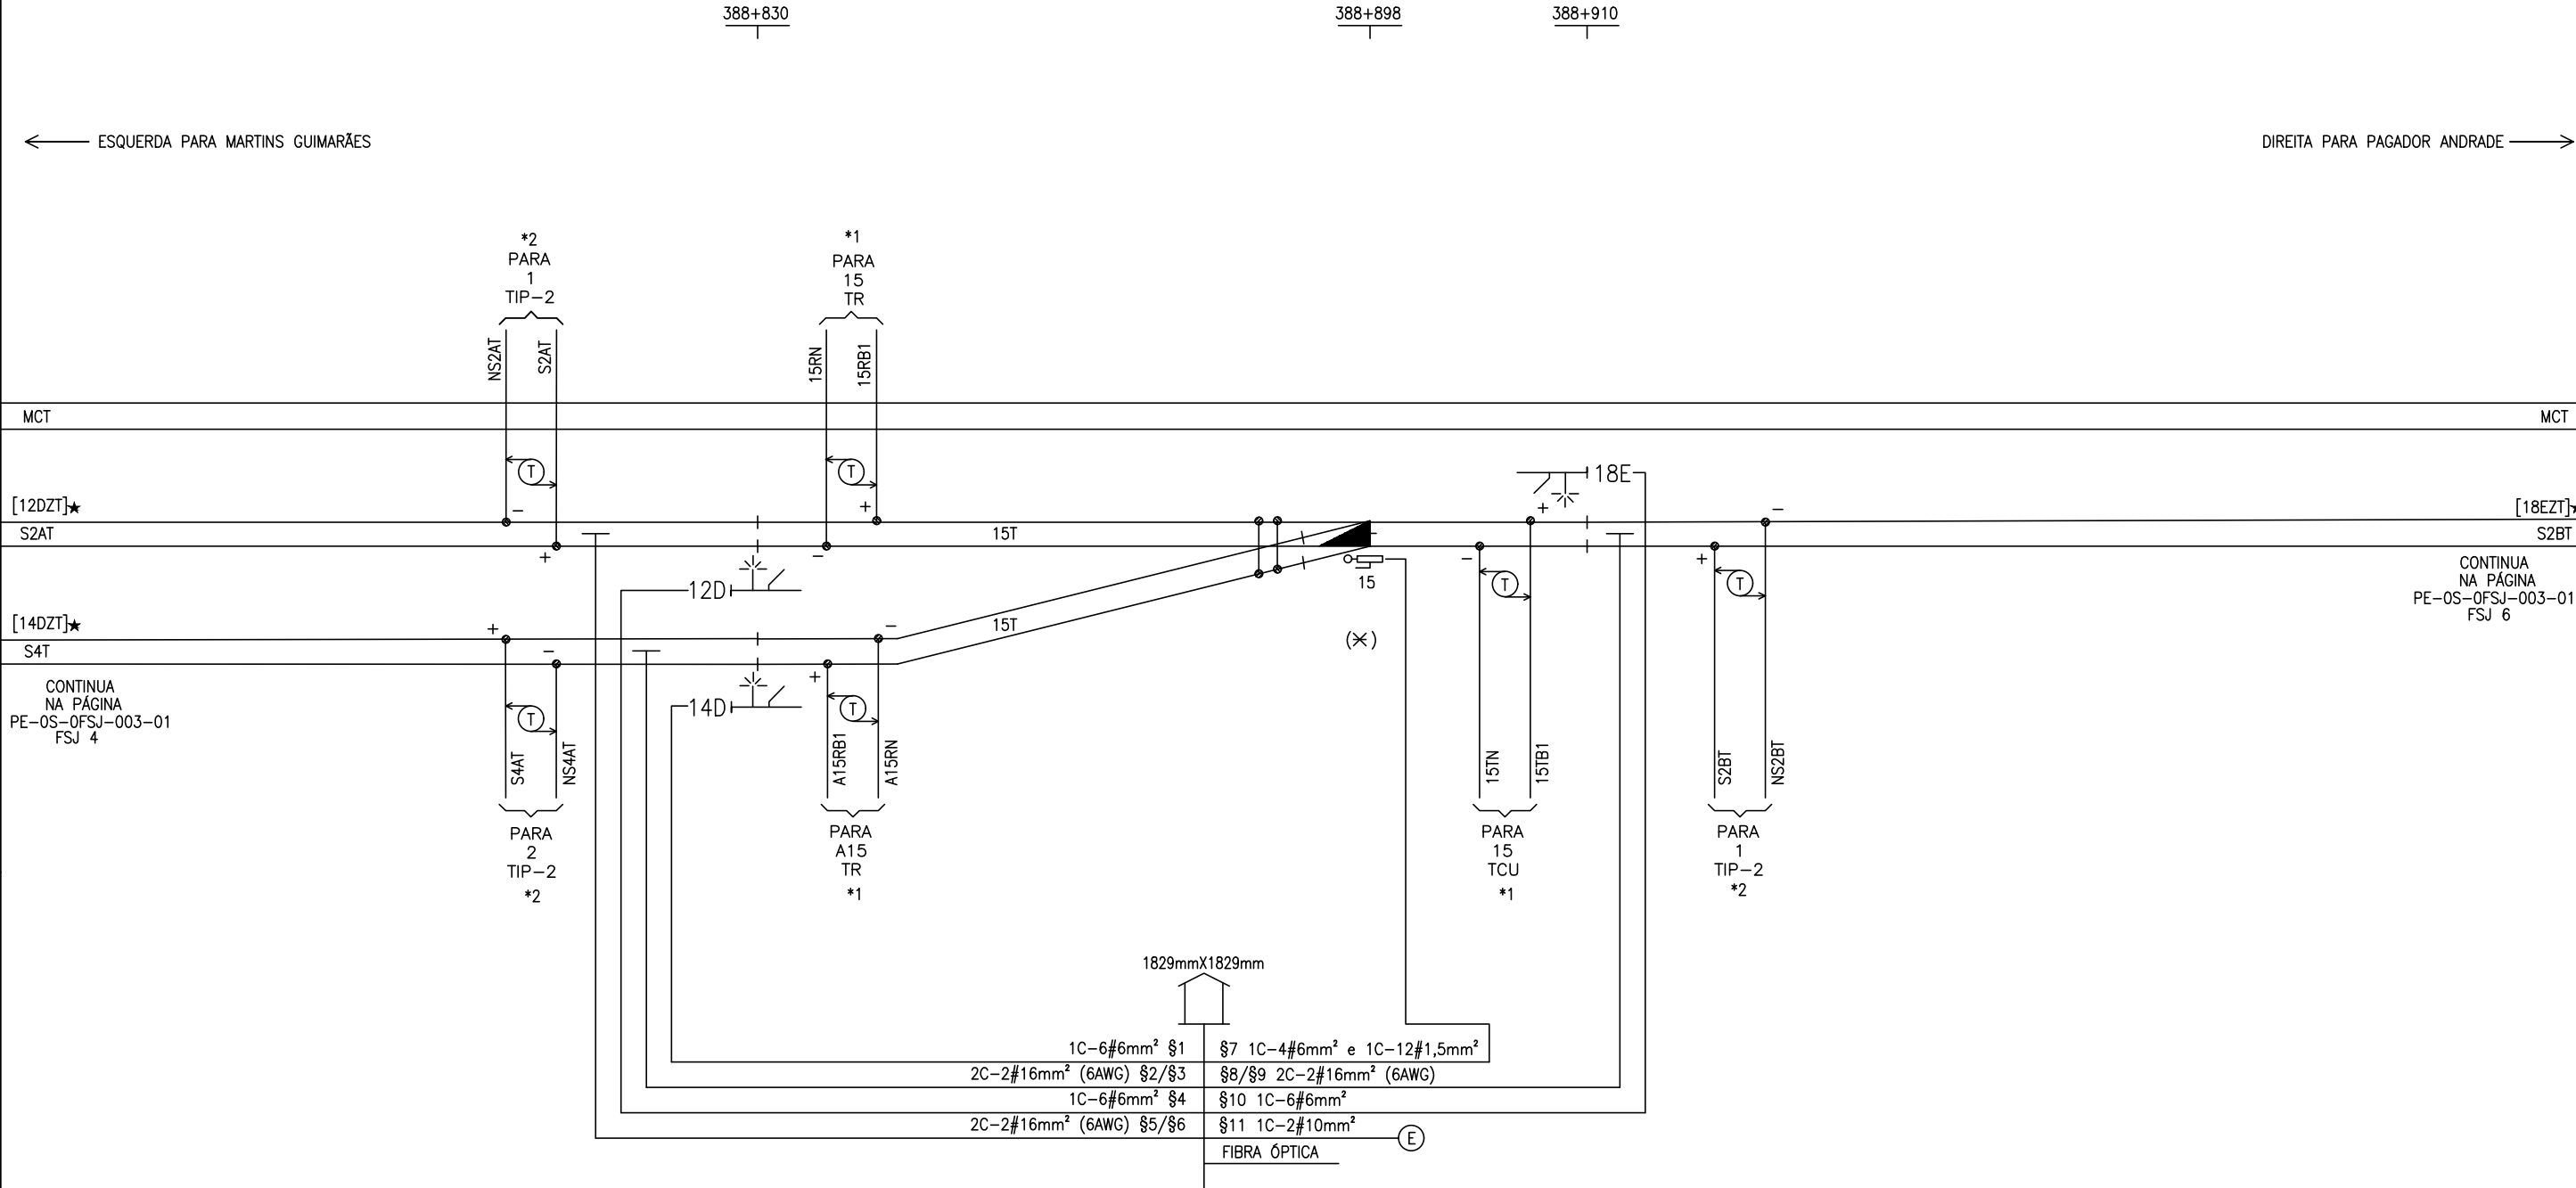

- OBSERVAÇÕES:
1. (X) = LOCALIZAÇÃO DA HOUSE
 2. ★ [XXXX] = NOMENCLATURA NO PROGRAMA DE APLICAÇÃO.
 3. *1 = VER FL. PE-OS-0FSJ-012-01
 4. *2 = VER FL. PE-OS-0FSJ-013-01
 5. § = VER FL. PE-OS-0FSJ-004-01
 6. □ = POSTE COM ANTENA PLANO TERRA PARA DDvR

ANOTAÇÕES	REV. 1 – 18/05/2023	A Operação dos circuitos e equipamentos aqui representados não podem ser completamente verificados senão após a sua instalação de modo a formar um sistema completo de sinalização ferroviária e ser devidamente submetido a "Testes de seleção de contatos(BREAKDOWN)" e "Testes operacionais de serviço"(Através de planilhas e fluxo de testes) antes de sua colocação em serviços normal definitivo. ENGENHARIA DE ELETROELETRÔNICA DE PROJETOS	MRS Logística S.A.	TÍTULO DES.: LINHA DE SÃO PAULO PLANO DE VIA E SINAL COM CABOS – PVS ABR 25 SÃO JOSÉ DOS CAMPOS – FSJ			
	REVISÃO DEVIDO ALTERAÇÃO DO PROJETO PELA ÁREA DE ENG. OPERAÇÕES, RETIRANDO A MCH 5 E 11 E PASSANDO PARA TRAVADORES ELÉTRICOS			ENG.RESP.: HAROLDO ENNES		DATA: 27/01/2023	
	PROJ.: MÁRCIO MOREIRA DES.: HYGOR TEODORO REVISOR: MARCOS REINH			PROJ.: MÁRCIO MOREIRA		ESCALA: –	FORMATO: A3
	REV. 2 – 04/10/2023			DES.PROJ.: ANTÔNIO LEAL		REV./DATA: 2 – 04/10/2023	
	REVISÃO DO PROJETO RETIRANDO O VERMELHO E AMARELO E REALIZANDO A ENTREGA EM DEFINITIVO (PRETO)			SUBST./REF.: –			
	PROJ.: MÁRCIO MOREIRA DES.: ANTONIO LEAL REVISOR: HYGOR TEODORO						
				CONTROLE INTERNO DE PROJETOS GEPEE	DATA	FIRMA CONTRATADA:	
	ELABORADOR: ANTÔNIO LEAL	04/10/2023	–				
	REVISOR: MARCOS REINH	19/10/2023					
	APROVADOR: ALEXANDRE MENEGHEL	05/12/2023	Nº ARQUIVO MRS:	PE-OS-0FSJ-003-01			

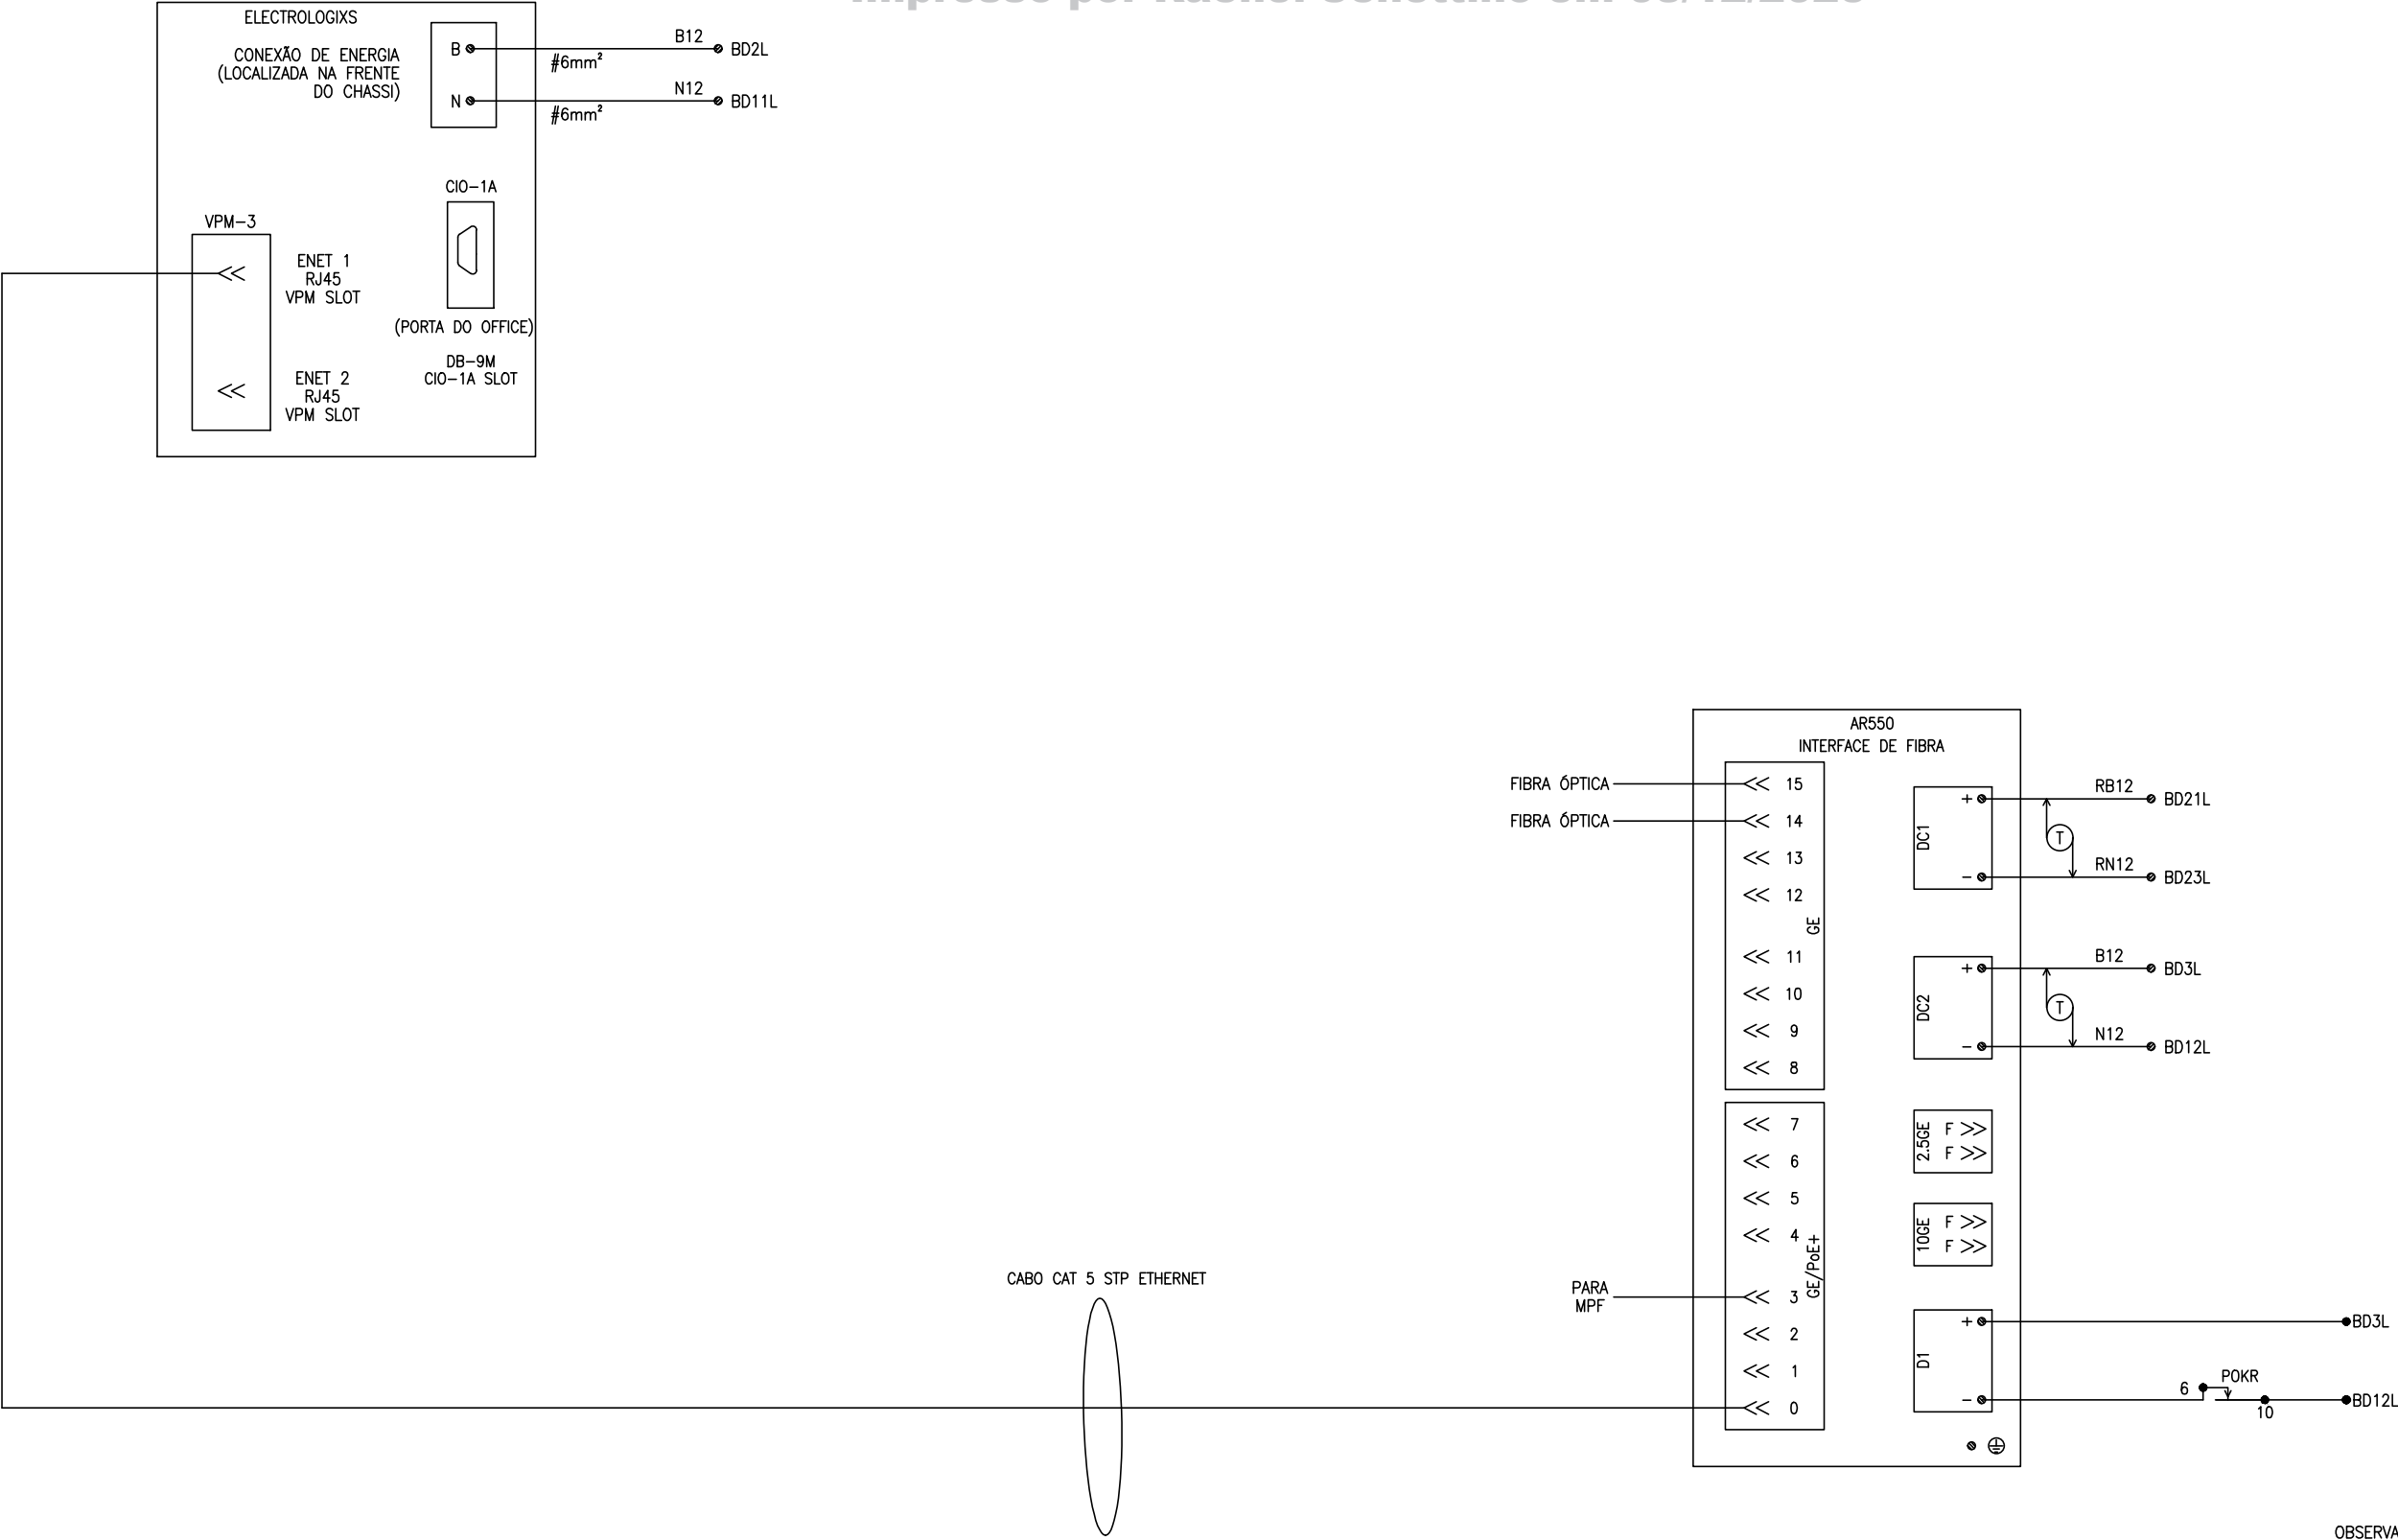

OBSERVAÇÕES:

1. (T) = TRANÇADO
2. CABOS A SEREM INSTALADOS DEVEM SER #1,5mm² EXCETO QUANDO INDICADO

ANOTAÇÕES

A Operação dos circuitos e equipamentos aqui representados não podem ser completamente verificados senão após a sua instalação de modo a formar um sistema completo de sinalização ferroviária e ser devidamente submetido a "Testes de seleção de contatos(BREAKDOWN)" e "Testes operacionais de serviço"(Através de planilhas e fluxo de testes) antes de sua colocação em serviços normal definitivo.
ENGENHARIA DE ELETROELETRÔNICA DE PROJETOS

CONTROLE INTERNO DE PROJETOS GEPEE	DATA
ELABORADOR: ANTÔNIO LEAL	27/01/2023
REVISOR: MÁRCIO MOREIRA	07/02/2023
APROVADOR: MARCOS REINH	28/02/2023



FIRMA CONTRATADA:

—

Nº ARQUIVO MRS:




TÍTULO DES.:
LINHA DE SÃO PAULO
CIRCUITOS DE COMUNICAÇÃO DO ABRIGO
ABR 25
SÃO JOSÉ DOS CAMPOS — FSJ

ENG.RESP.:	HAROLDO ENNES	DATA:	27/01/2023	
PROJ.:	MÁRCIO MOREIRA	ESCALA:	—	FORMATO: A3
DES.PROJ.:	ANTONIO LEAL	REV./DATA:	—	
—0S—0FSJ—010—01		SUBST./REF.:	—	


PE-0S-0FSJ-010-01



CIO-1A ATRIBUIÇÃO DOS PINOS PORTA DE DIAGNÓSTICO E DE OFFICE		
PINOS	SINAL	NOME DO SINAL
1	CD	CARRIER DETETOR
2	RX	RECEBE DADOS
3	TX	ENVA DADOS
4	DTR	DTE
5	GND	SINAL COMUM DE RETORNO
6	DSR	DCE
7	RTS	PEDIDO DE ENVIO
8	CTS	LIVRE PARA ENVIAR
9	RI	INDICADOR DE TOQUE

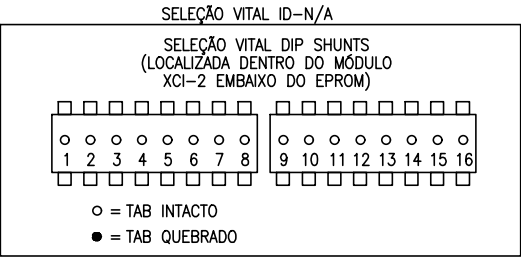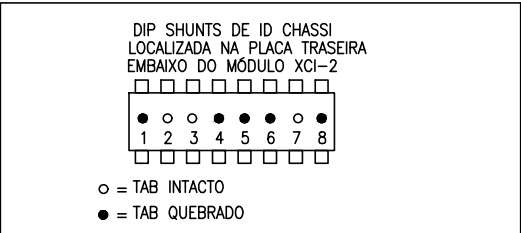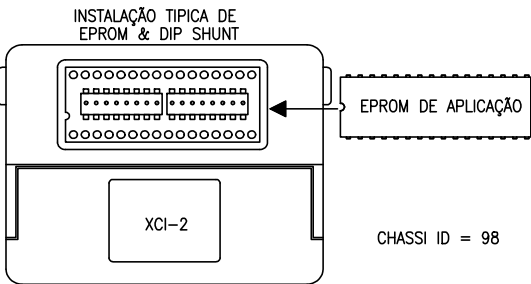

NOTA:
- As informações referente a programação serão incluídas posteriormente.

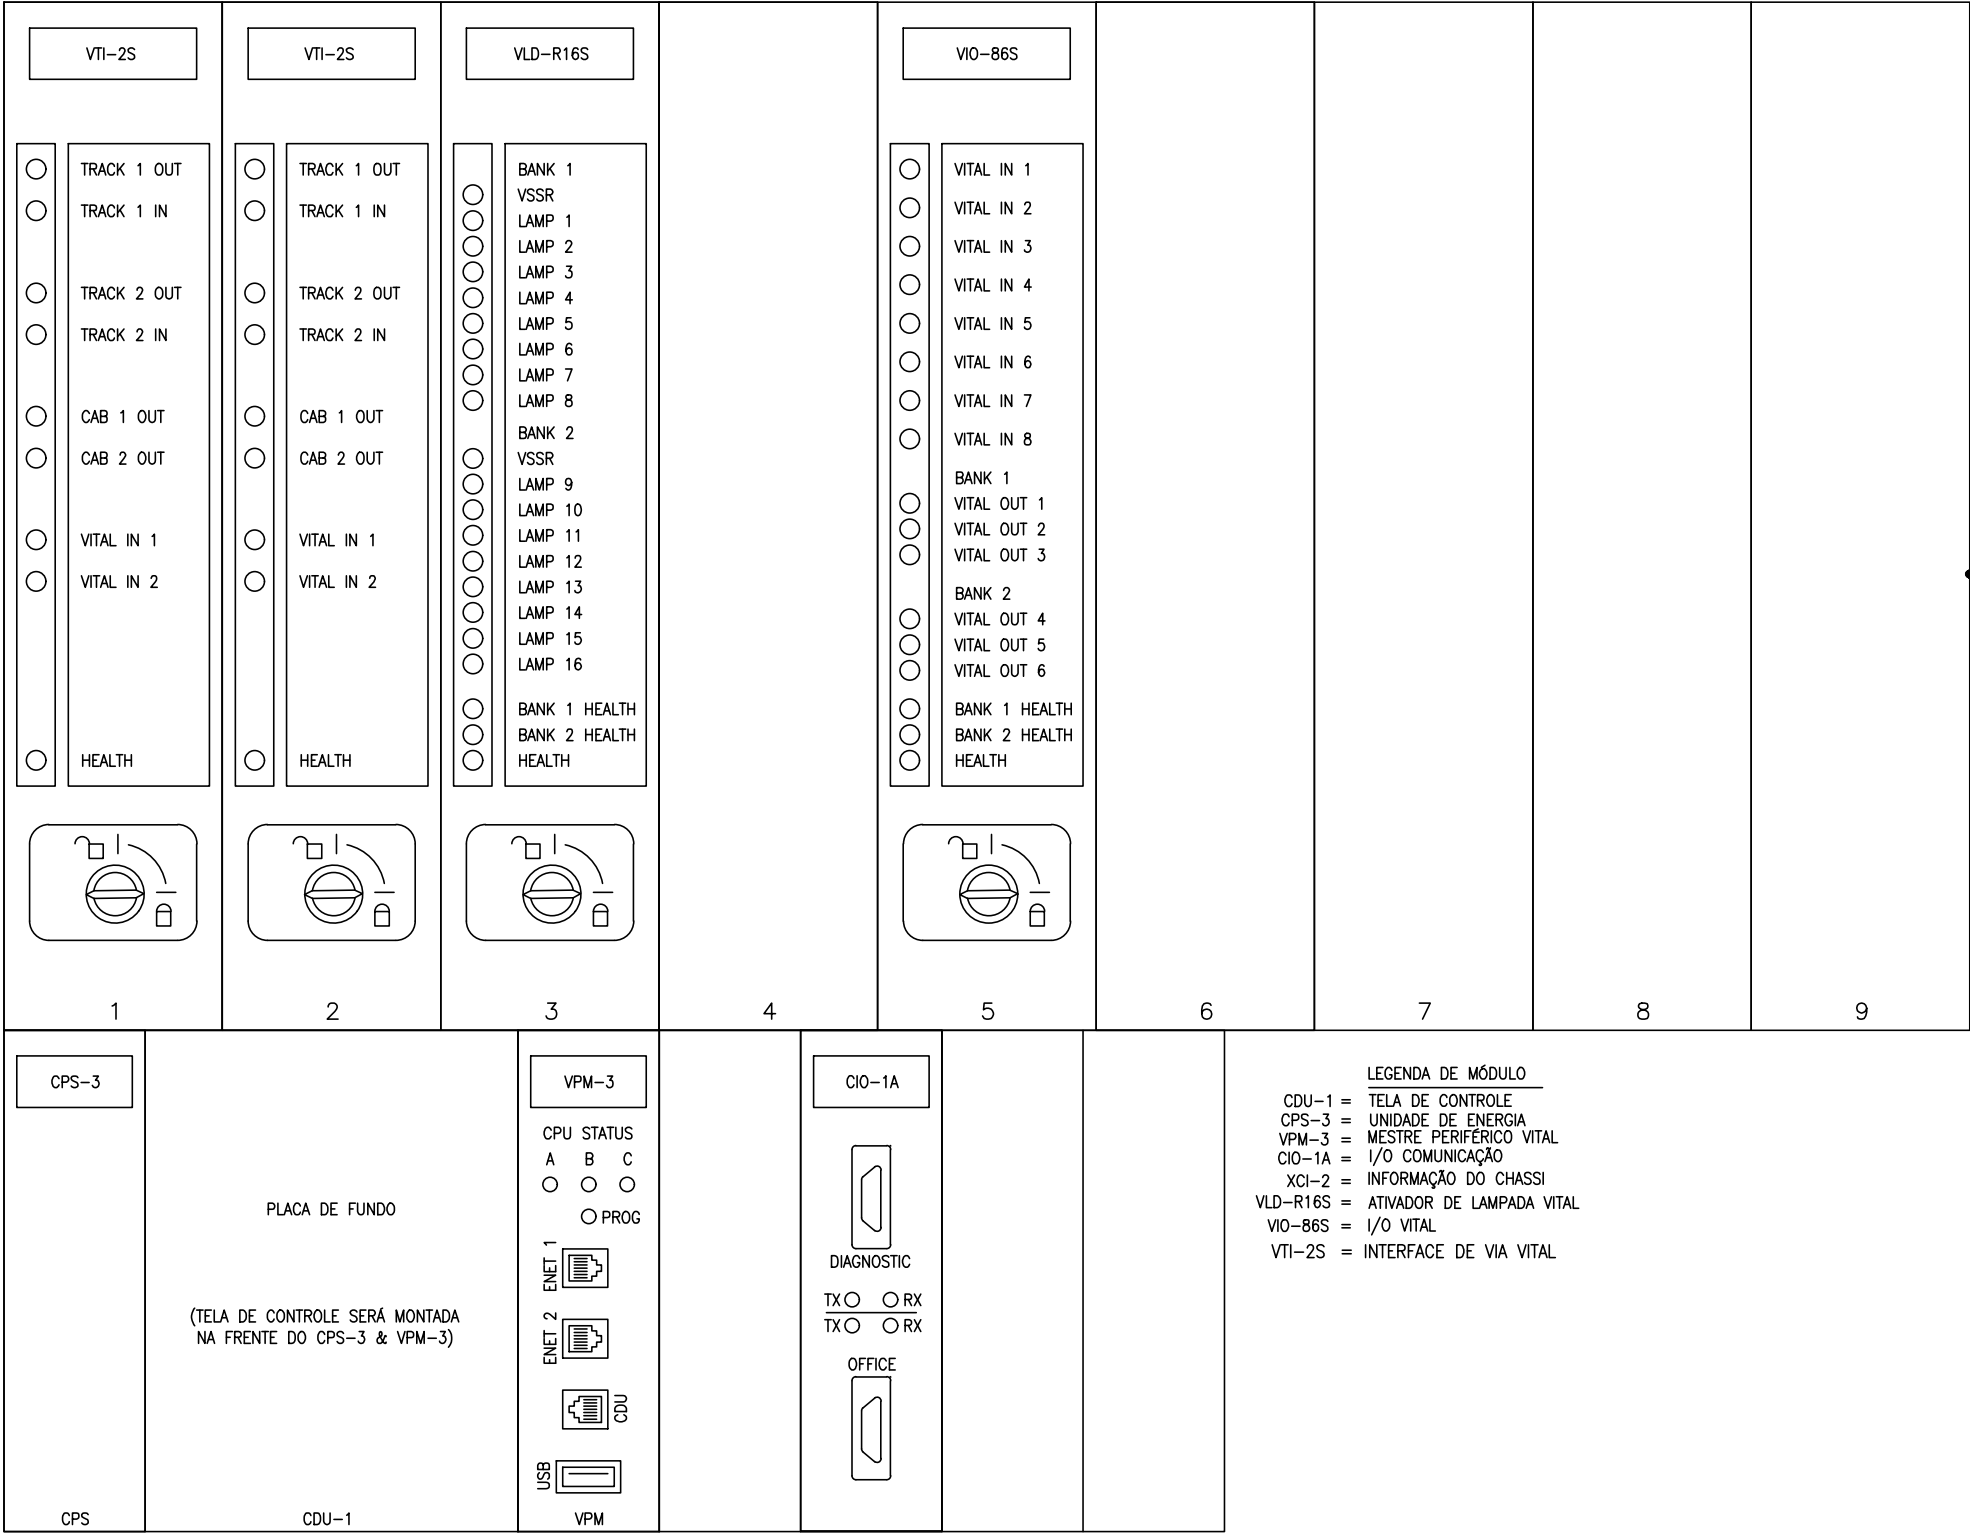

LEGENDA DE MÓDULO

CDU-1 = TELA DE CONTROLE
CPS-3 = UNIDADE DE ENERGIA
VPM-3 = MESTRE PERIFÉRICO VITAL
CIO-1A = I/O COMUNICAÇÃO
XCI-2 = INFORMAÇÃO DO CHASSI
VLD-R16S = ATIVADOR DE LAMPADA VITAL
VIO-86S = I/O VITAL
VTI-2S = INTERFACE DE VIA VITAL

ANOTAÇÕES

A Operação dos circuitos e equipamentos aqui representados não podem ser completamente verificados senão após a sua instalação de modo a formar um sistema completo de sinalização ferroviária e ser devidamente submetido a "Testes de seleção de contatos(BREAKDOWN)" e "Testes operacionais de serviço"(Através de planilhas e fluxo de testes) antes de sua colocação em serviços normal definitivo.
ENGENHARIA DE ELETROELETRÔNICA DE PROJETOS


CONTROLE INTERNO DE PROJETOS GEPEE	DATA
ELABORADOR: ANTÔNIO LEAL	27/01/2023
REVISOR: MÁRCIO MOREIRA	07/02/2023
APROVADOR: MARCOS REINH	28/02/2023



TÍTULO DES.:
LINHA DE SÃO PAULO
CONFIGURAÇÃO DO MODULO ELECTROLOGIXS
ABR 25
SÃO JOSÉ DOS CAMPOS – FSJ

ENG.ESP.: HAROLDO ENNES	DATA: 27/01/2023
PROJ.: MÁRCIO MOREIRA	ESCALA: — FORMATO: A3
DES.PROJ.: ANTÔNIO LEAL	REV./DATA: —
SUBST./REF.: —	

Nº ARQUIVO MRS: **PE-0S-OFSJ-011-01**

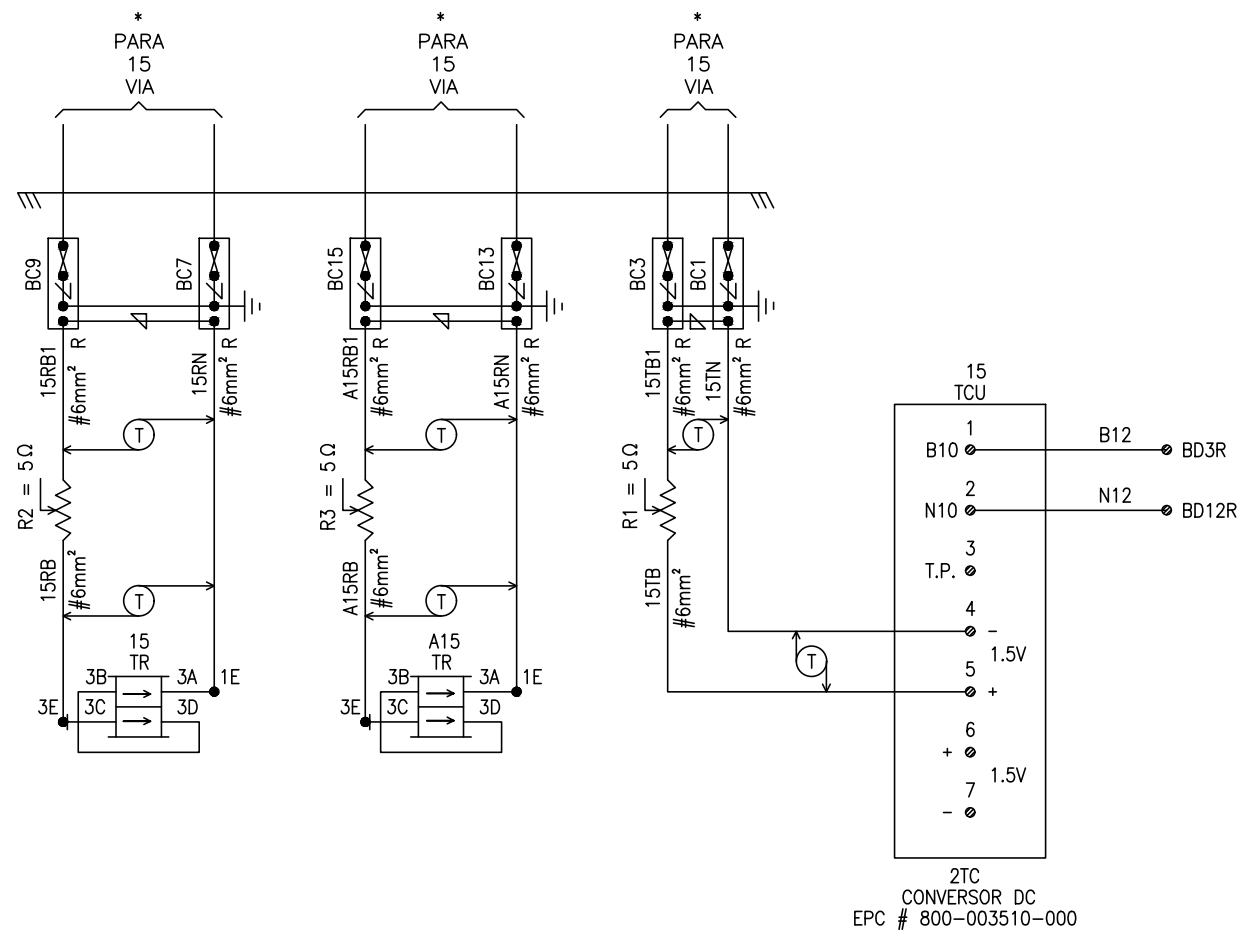

OBSERVAÇÕES:

1. (T) = TRANÇADO
2. ∠ = SUPRESSOR
3. ∇ = EQUALIZADOR
4. TODOS CABOS DO ABRIGO #1,5mm EXCETO QUANDO INDICADO.
5. * = VER FL. PE-0S-0FSJ-003-01

ANOTAÇÕES

A Operação dos circuitos e equipamentos aqui representados não podem ser completamente verificados senão após a sua instalação de modo a formar um sistema completo de sinalização ferroviária e ser devidamente submetido a "Testes de seleção de contatos(BREAKDOWN)" e "Testes operacionais de serviço"(Através de planilhas e fluxo de testes) antes de sua colocação em serviços normal definitivo.
ENGENHARIA DE ELETROELETRÔNICA DE PROJETOS



TÍTULO DES.: LINHA DE SÃO PAULO
CIRCUITOS DE VIA
ABR 25
SÃO JOSÉ DOS CAMPOS – FSJ

CONTROLE INTERNO DE PROJETOS GEPEE	DATA
ELABORADOR: ANTÔNIO LEAL	27/01/2023
REVISOR: MÁRCIO MOREIRA	07/02/2023
APROVADOR: MARCOS REINH	28/02/2023

FIRMA CONTRATADA:

-

Nº ARQUIVO MRS:

ENG.RESP.: HAROLDO ENNES

PROJ.: MÁRCIO MOREIRA

DES.PROJ.: ANTÔNIO LEAL

PE-0S-0FSJ-012-01



DATA: 27/01/2023

ESCALA: -

FORMATO: A3

REV./DATA: -

SUBST./REF.: -

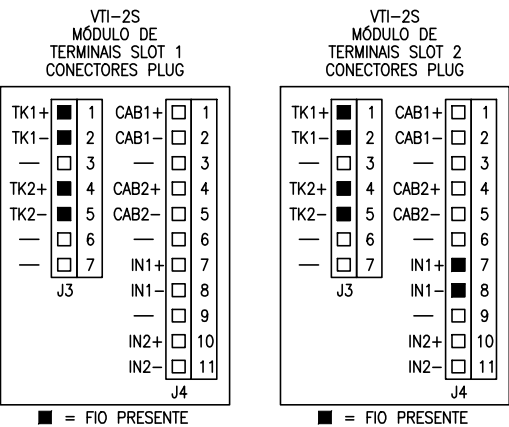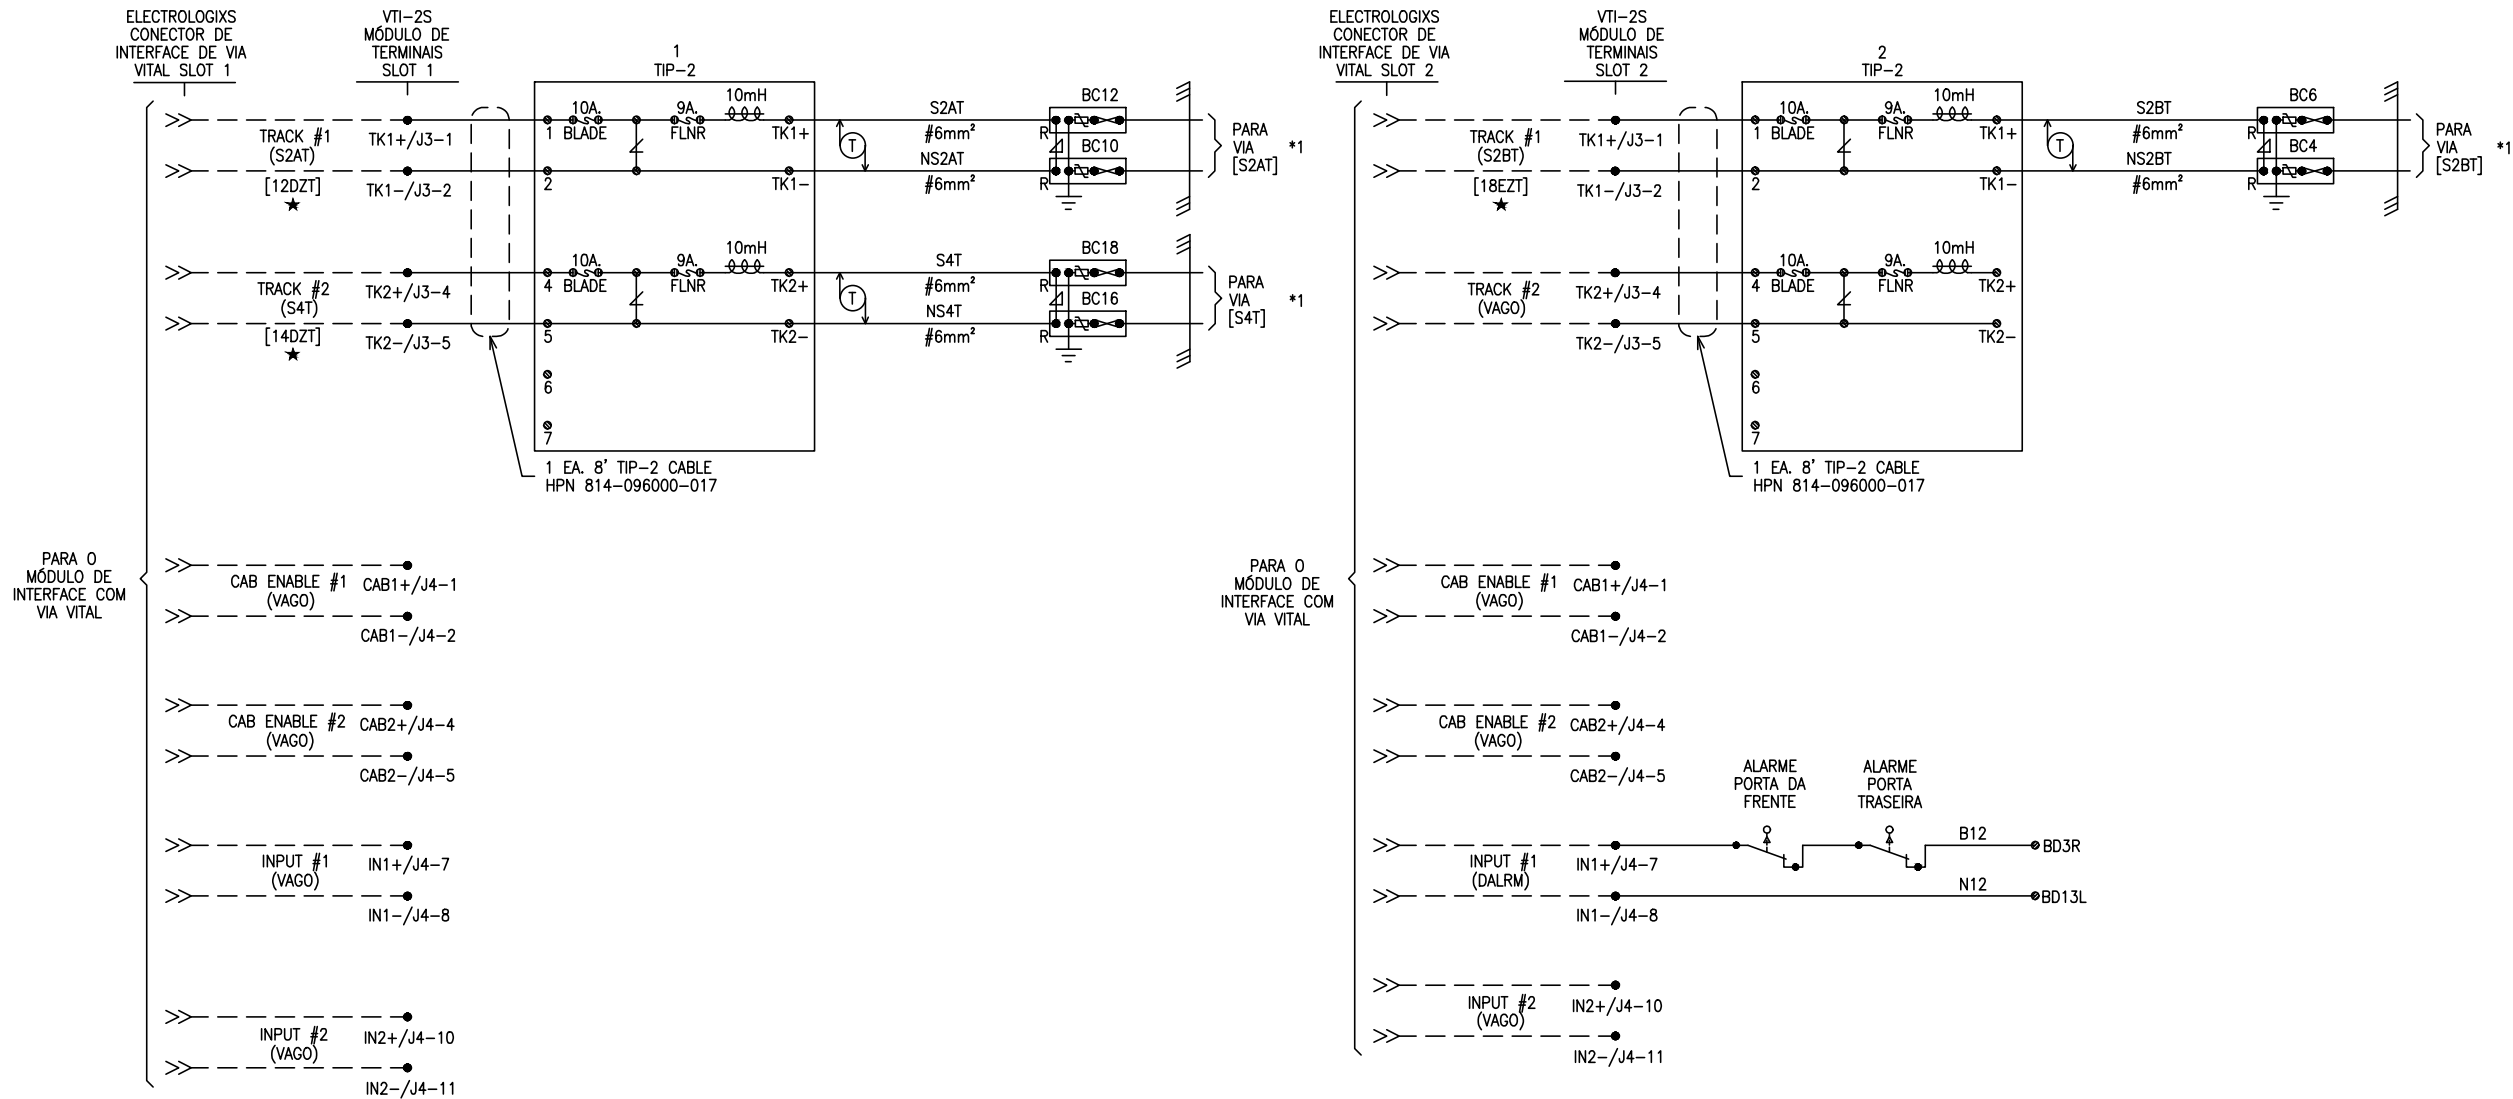

- OBSERVAÇÕES:
1. = VARISTOR CLAMPER
 2. = EQUALIZADOR
 3. ---- = CONEXÃO INTERNA
 4. TODOS CABOS DA HOUSE #1,5mm² EXCETO QUANDO INDICADO.
 5. ★ [XXXX] = NOMENCLATURA NO PROGRAMA DE APLICAÇÃO.
 6. *1 = PARA FL. PE-OS-OFSJ-003-01
 7. CABO UTILIZADO PARA INTERLIGAÇÃO DO VTI AO TIP-2 (1 EA. 8' [2,43m] TIP-2 CABLE HPN 814-096000-017)

ANOTAÇÕES

REV. 1 - 18/05/2023
REVISÃO DEVIDO ALTERAÇÃO DO PROJETO PELA ÁREA DE ENG. OPERAÇÕES, RETIRANDO A MCH 5 E 11 E PASSANDO PARA TRAVADORES ELÉTRICOS
PROJ.: MÁRCIO MOREIRA
DES.: HYGOR TEODORO
REVISOR: MARCOS REINH
REV. 2 - 04/10/2023
REVISÃO DO PROJETO RETIRANDO O VERMELHO E AMARELO E REALIZANDO A ENTREGA EM DEFINITIVO (PRETO)
PROJ.: MÁRCIO MOREIRA
DES.: ANTONIO LEAL
REVISOR: HYGOR TEODORO

A Operação dos circuitos e equipamentos aqui representados não podem ser completamente verificados senão após a sua instalação de modo a formar um sistema completo de sinalização ferroviária e ser devidamente submetido a "Testes de seleção de contatos(BREAKDOWN)" e "Testes operacionais de serviço"(Através de planilhas e fluxo de testes) antes de sua colocação em serviços normal definitivo.
ENGENHARIA DE ELETROELETRÔNICA DE PROJETOS





TÍTULO DES.:
LINHA DE SÃO PAULO
I/O DE VIA E VITAL DO ELECTROLOGIXS
ABR 25
SÃO JOSÉ DOS CAMPOS – FSJ

CONTROLE INTERNO DE PROJETOS GEPEE	DATA
ELABORADOR: ANTONIO LEAL	04/10/2023
REVISOR: MARCOS REINH	19/10/2023
APROVADOR: ALEXANDRE MENEHUEL	05/12/2023

FIRMA CONTRATADA:
-

ENG.RESP.: HAROLDO ENNES	DATA: 27/01/2023	
PROJ.: MÁRCIO MOREIRA	ESCALA: –	FORMATO: A3
DES.PROJ.: ANTÔNIO LEAL	REV./DATA: 2 – 04/10/2023	
–0S–0FSJ–013–01	SUBST./REF.: –	




Nº ARQUIVO MRS: **PE-OS-OFSJ-013-01**

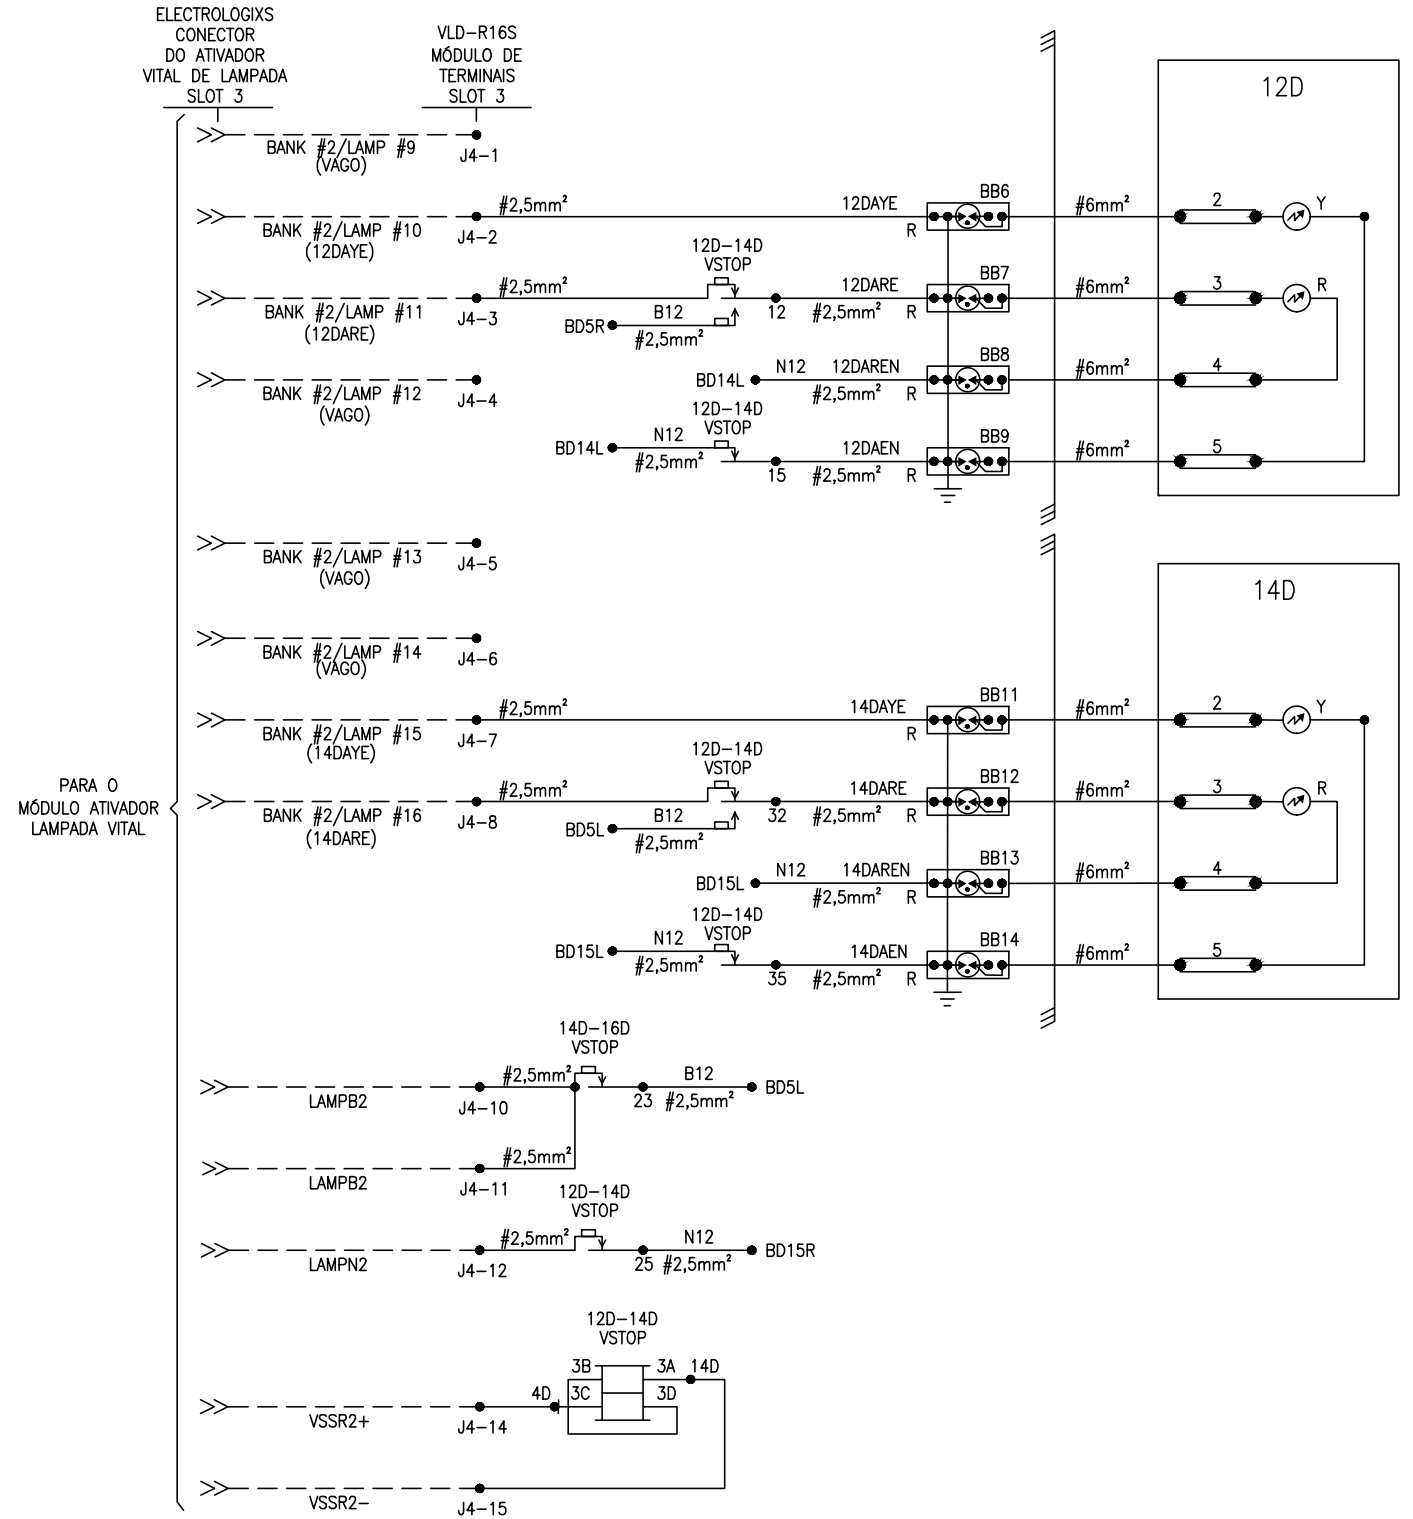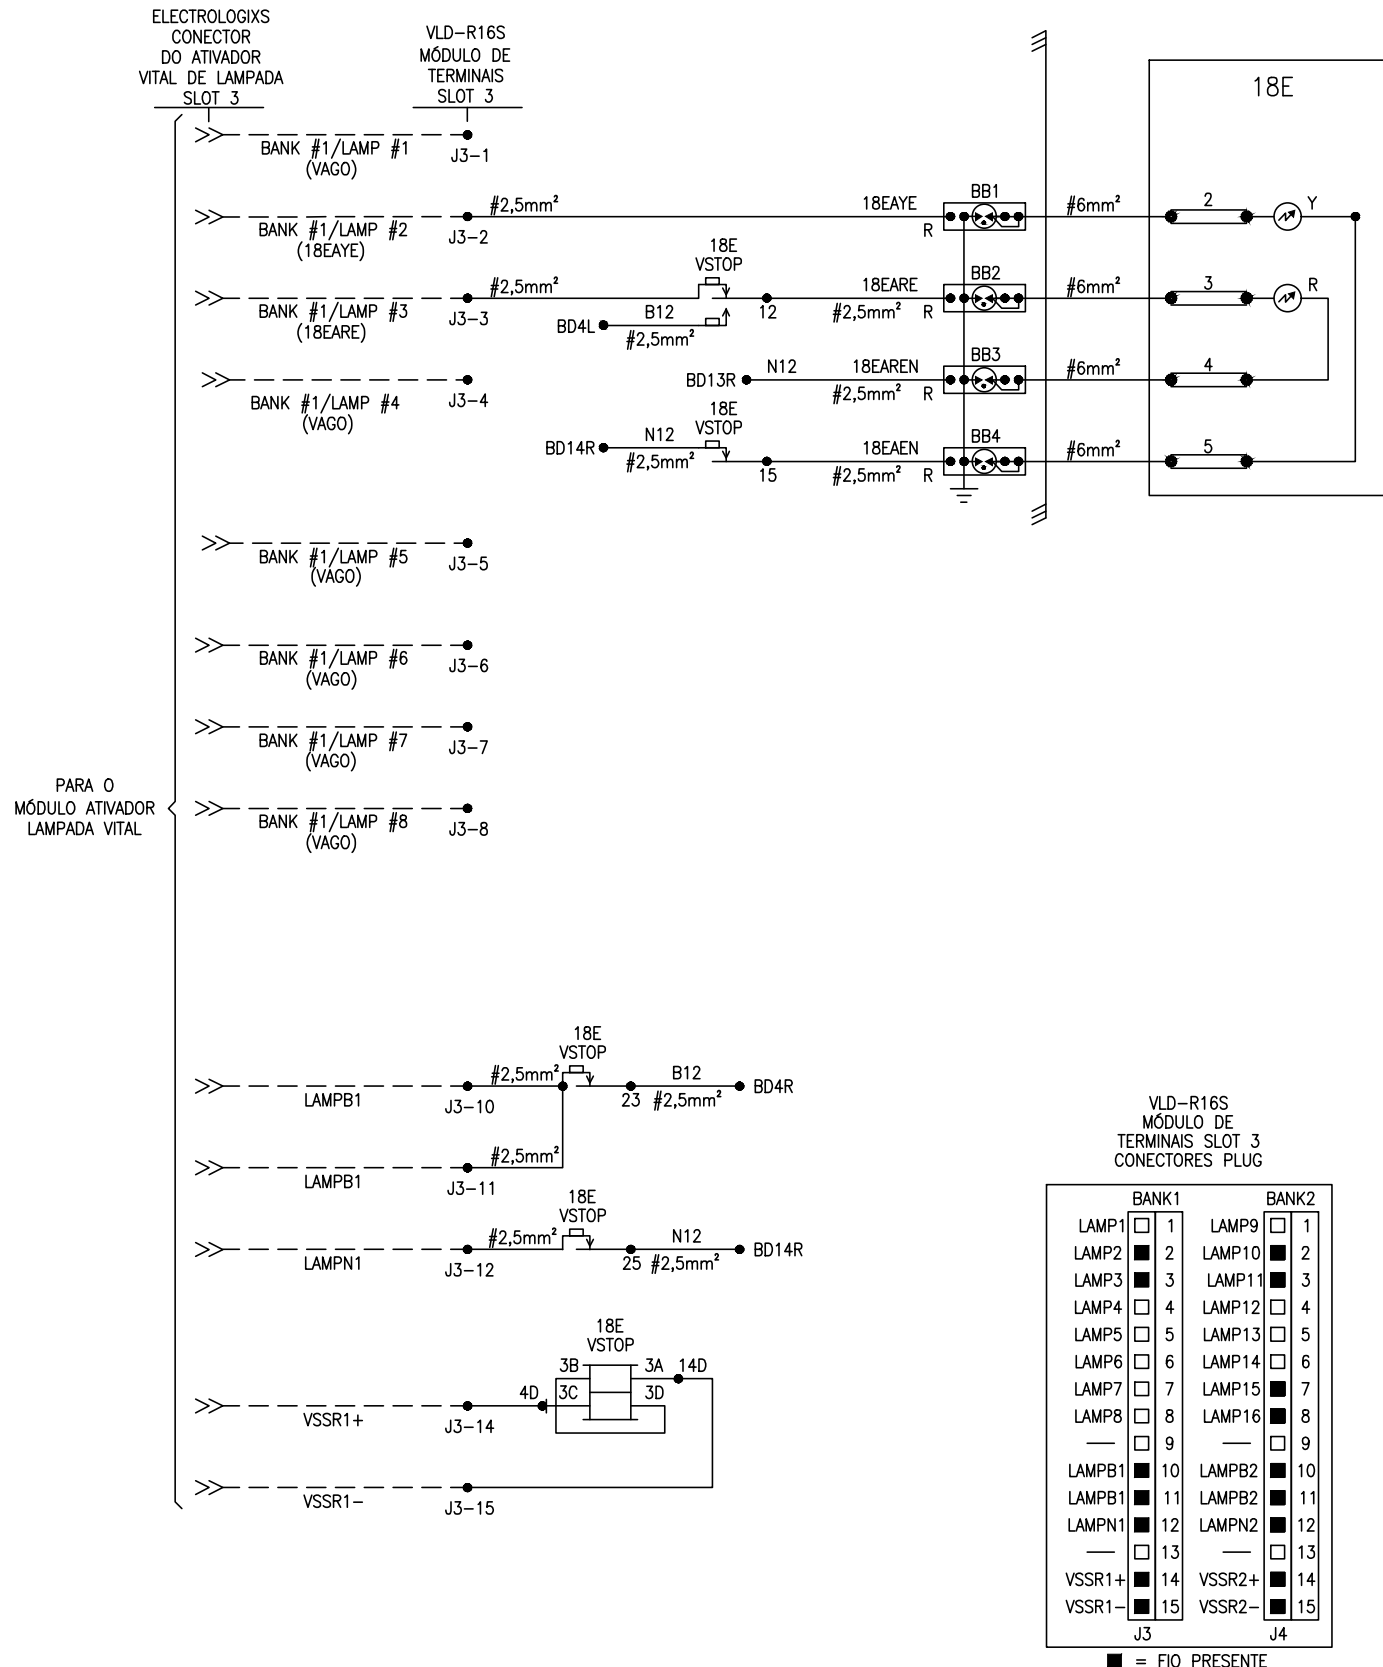

OBSERVAÇÕES:

1.  = SUPRESSOR HÍBRIDO
2. ---- = CONEXÃO INTERNA
3. TODOS CABOS DA HOUSE #1,5mm EXCETO QUANDO INDICADO.

ANOTAÇÕES	REV. 1 – 18/05/2023		REVISÃO DEVIDO ALTERAÇÃO DO PROJETO PELA ÁREA DE ENG OPERAÇÕES, RETIRANDO A MCH 5 E 11 E PASSANDO PARA TRAVADORES ELÉTRICOS			
	REV. 2 – 04/10/2023		PROJ.: MÁRCIO MOREIRA DES.: HYGOR TEODORO REVISOR: MARCOS REINH			
			REVISÃO DO PROJETO RETIRANDO O VERMELHO E AMARELO E REALIZANDO A ENTREGA EM DEFINITIVO (PRETO)			
			PROJ.: MÁRCIO MOREIRA DES.: ANTONIO LEAL REVISOR: HYGOR TEODORO			
			A Operação dos circuitos e equipamentos aqui representados não podem ser completamente verificados senão após a sua instalação de modo a formar um sistema completo de sinalização ferroviária e ser devidamente submetido a "Testes de seleção de contatos(BREAKDOWN)" e "Testes operacionais de serviço"(Através de planilhas e fluxo de testes) antes de sua colocação em serviços normal definitivo. ENGENHARIA DE ELETROELETRÔNICA DE PROJETOS			
				 Logística S.A.	TÍTULO DES.: LINHA DE SÃO PAULO CIRCUITOS DOS SINAIS 18E, 12D E 14D ABR 25 SÃO JOSÉ DOS CAMPOS – FSJ	
	CONTROLE INTERNO DE PROJETOS GEPEE	DATA	-	ENG.RESP.: HAROLDO ENNES	DATA: 27/01/2023	
	ELABORADOR: ANTONIO LEAL	04/10/2023		PROJ.: MÁRCIO MOREIRA	ESCALA: –	FORMATO: A3
	REVISOR: MARCOS REINH	19/10/2023		DES.PROJ.: ANTONIO LEAL	REV./DATA: 2 – 04/10/2023	
	APROVADOR: ALEXANDRE MENEGHEL	05/12/2023		Nº ARQUIVO MRS: PE-0S-0FSJ-014-01		SUBST./REF.:

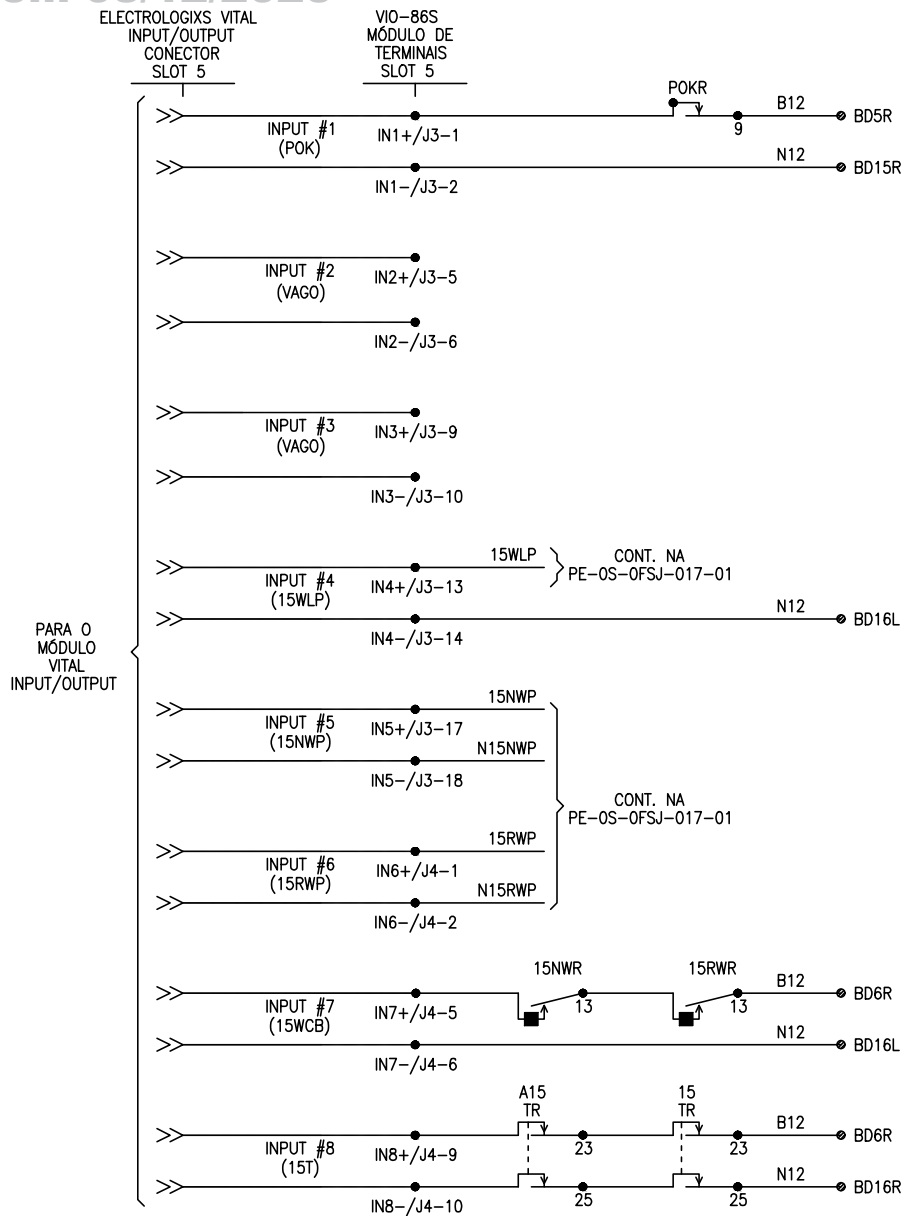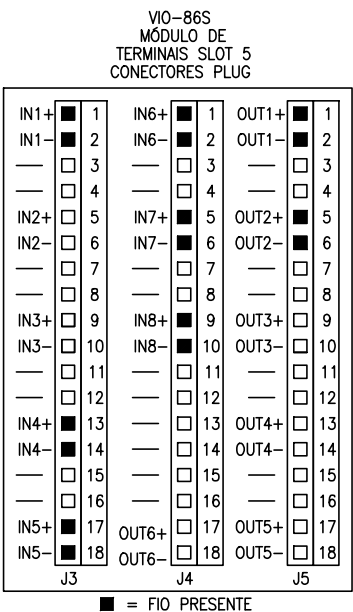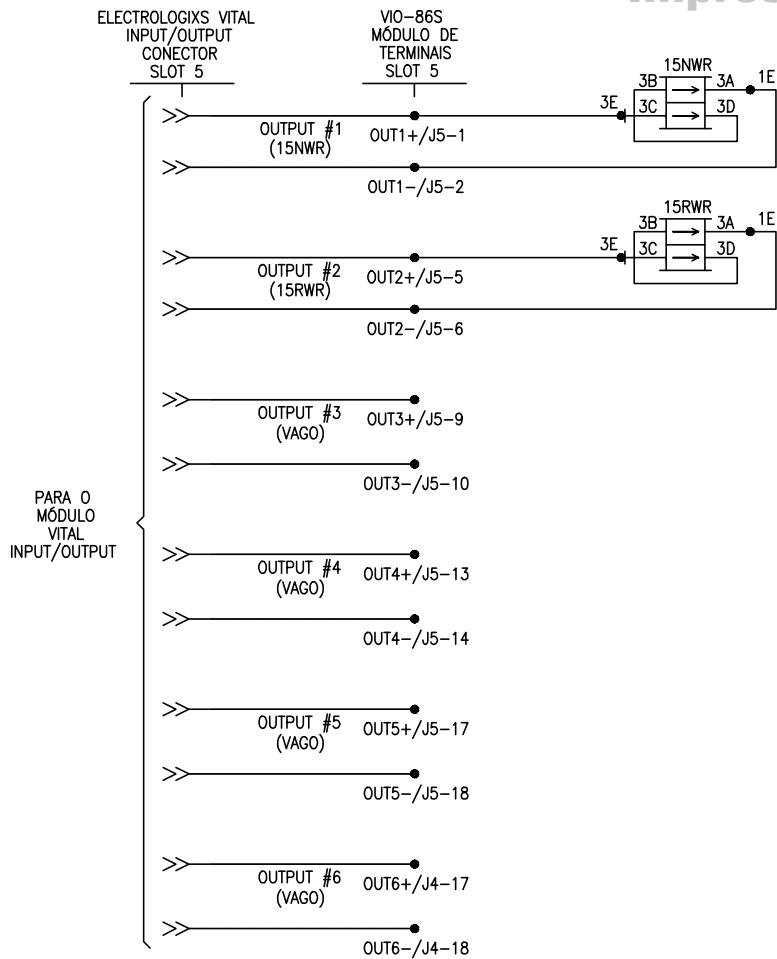

OBSERVAÇÕES:
1. ---- = CONEXÃO INTERNAL
2. TODOS CABOS DA HOUSE #1,5mm² EXCETO QUANDO INDICADO.

ANOTAÇÕES

A Operação dos circuitos e equipamentos aqui representados não podem ser completamente verificados senão após a sua instalação de modo a formar um sistema completo de sinalização ferroviária e ser devidamente submetido a "Testes de seleção de contatos(BREAKDOWN)" e "Testes operacionais de serviço"(Através de planilhas e fluxo de testes) antes de sua colocação em serviços normal definitivo.
ENGENHARIA DE ELETROELETRÔNICA DE PROJETOS



TÍTULO DES.:
LINHA DE SÃO PAULO
CIRCUITOS I/O DO ELECTROLOGIXS SLOT 5
ABR 25
SÃO JOSÉ DOS CAMPOS – FSJ

CONTROLE INTERNO DE PROJETOS GEPEE	DATA
ELABORADOR: ANTÔNIO LEAL	27/01/2023
REVISOR: MÁRCIO MOREIRA	07/02/2023
APROVADOR: MARCOS REINH	28/02/2023

FIRMA CONTRATADA:

—

Nº ARQUIVO MRS:

ENG.RESP.: HAROLDO ENNES

PROJ.: MÁRCIO MOREIRA

DES.PROJ.: ANTÔNIO LEAL

PE-OS-0FSJ-015-01


DATA: 27/01/2023

ESCALA: —

FORMATO: A3

REV./DATA: —

SUBST./REF.: —

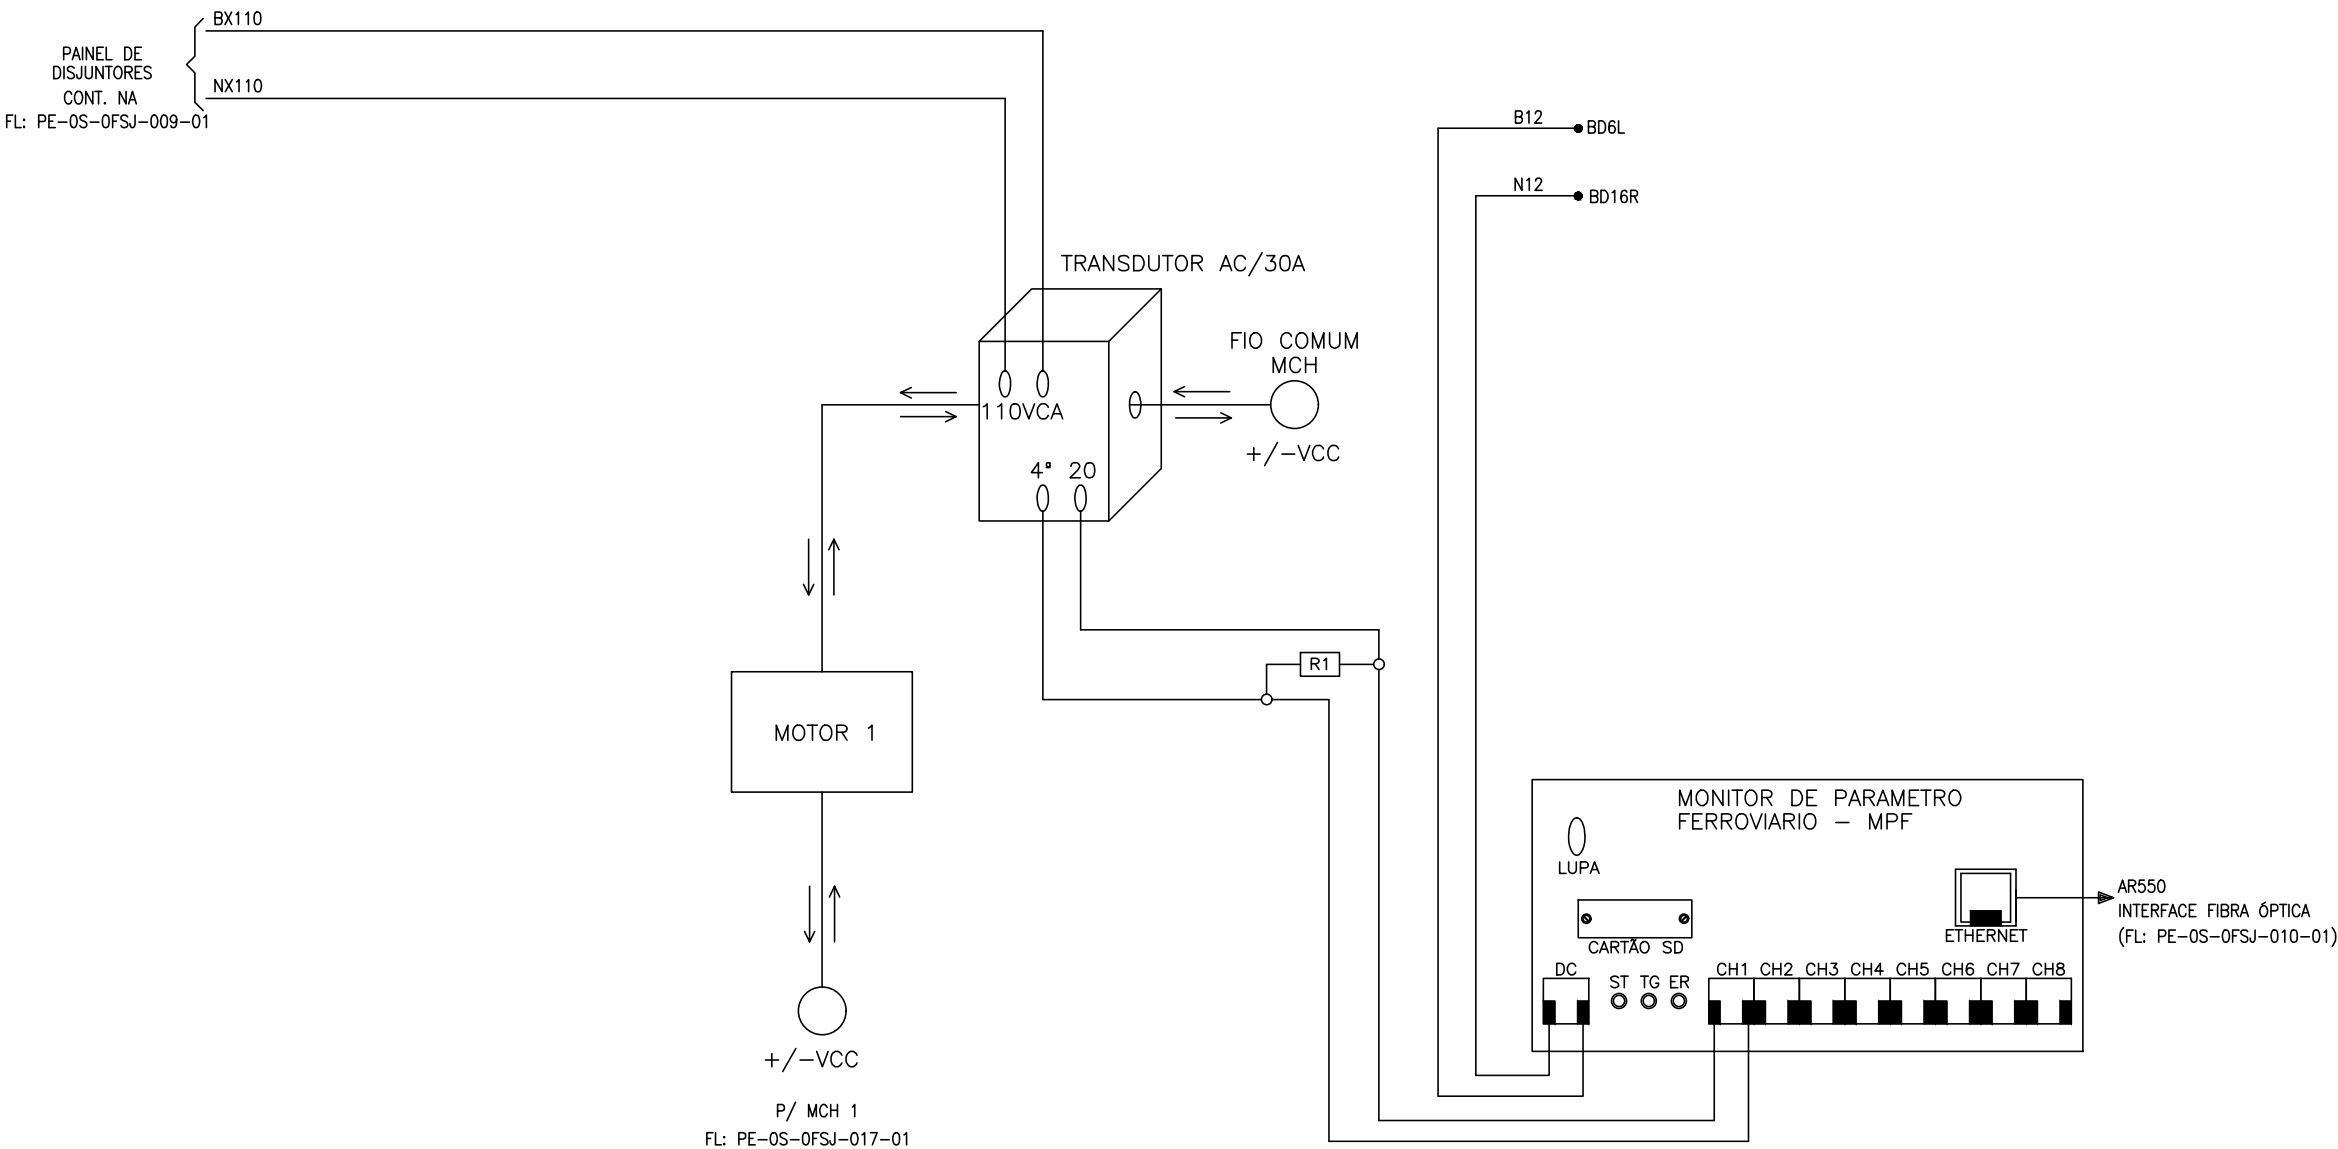

OBSERVAÇÕES:
1. R1= RESISTOR 150R -1/8W DE PRECISÃO
2. TRANSDUTOR AC +/- 30A/4-20mA
3. IP=XXX.XXX.XXX.XXX
GTW=XXX.XXX.XXX.XXX
MASK=XXX.XXX.XXX.XXX
4. INFORMAÇÕES SERÃO ATUALIZADAS COM OS
DADOS DO PROGRAMA APLICATIVO DO PROJETO
APÓS ELABORAÇÃO DO SOFTWARE

ANOTAÇÕES

A Operação dos circuitos e equipamentos aqui representados não podem ser completamente verificados senão após a sua instalação de modo a formar um sistema completo de sinalização ferroviária e ser devidamente submetido a "Testes de seleção de contatos(BREAKDOWN)" e "Testes operacionais de serviço"(Através de planilhas e fluxo de testes) antes de sua colocação em serviços normal definitivo.
ENGENHARIA DE ELETROELETRÔNICA DE PROJETOS

CONTROLE INTERNO DE PROJETOS GEPEE	DATA
ELABORADOR: ANTÔNIO LEAL	27/01/2023
REVISOR: MÁRCIO MOREIRA	07/02/2023
APROVADOR: MARCOS REINH	28/02/2023




FIRMA CONTRATADA:
-
Nº ARQUIVO MRS:

TÍTULO DES.:
LINHA DE SÃO PAULO
DIAGRAMA TRANSDUTOR/MPF - 1 CANAL
ABR 25
SÃO JOSÉ DOS CAMPOS - FSJ

ENG.RESP.:	HAROLDO ENNES	DATA:	27/01/2023	
PROJ.:	MÁRCIO MOREIRA	ESCALA:	—	FORMATO: A3
DES.PROJ.:	ANTÔNIO LEAL	REV./DATA:	—	
—OS—OFSJ—016—01		SUBST./REF.:		

PE-0S-0FSJ-016-01

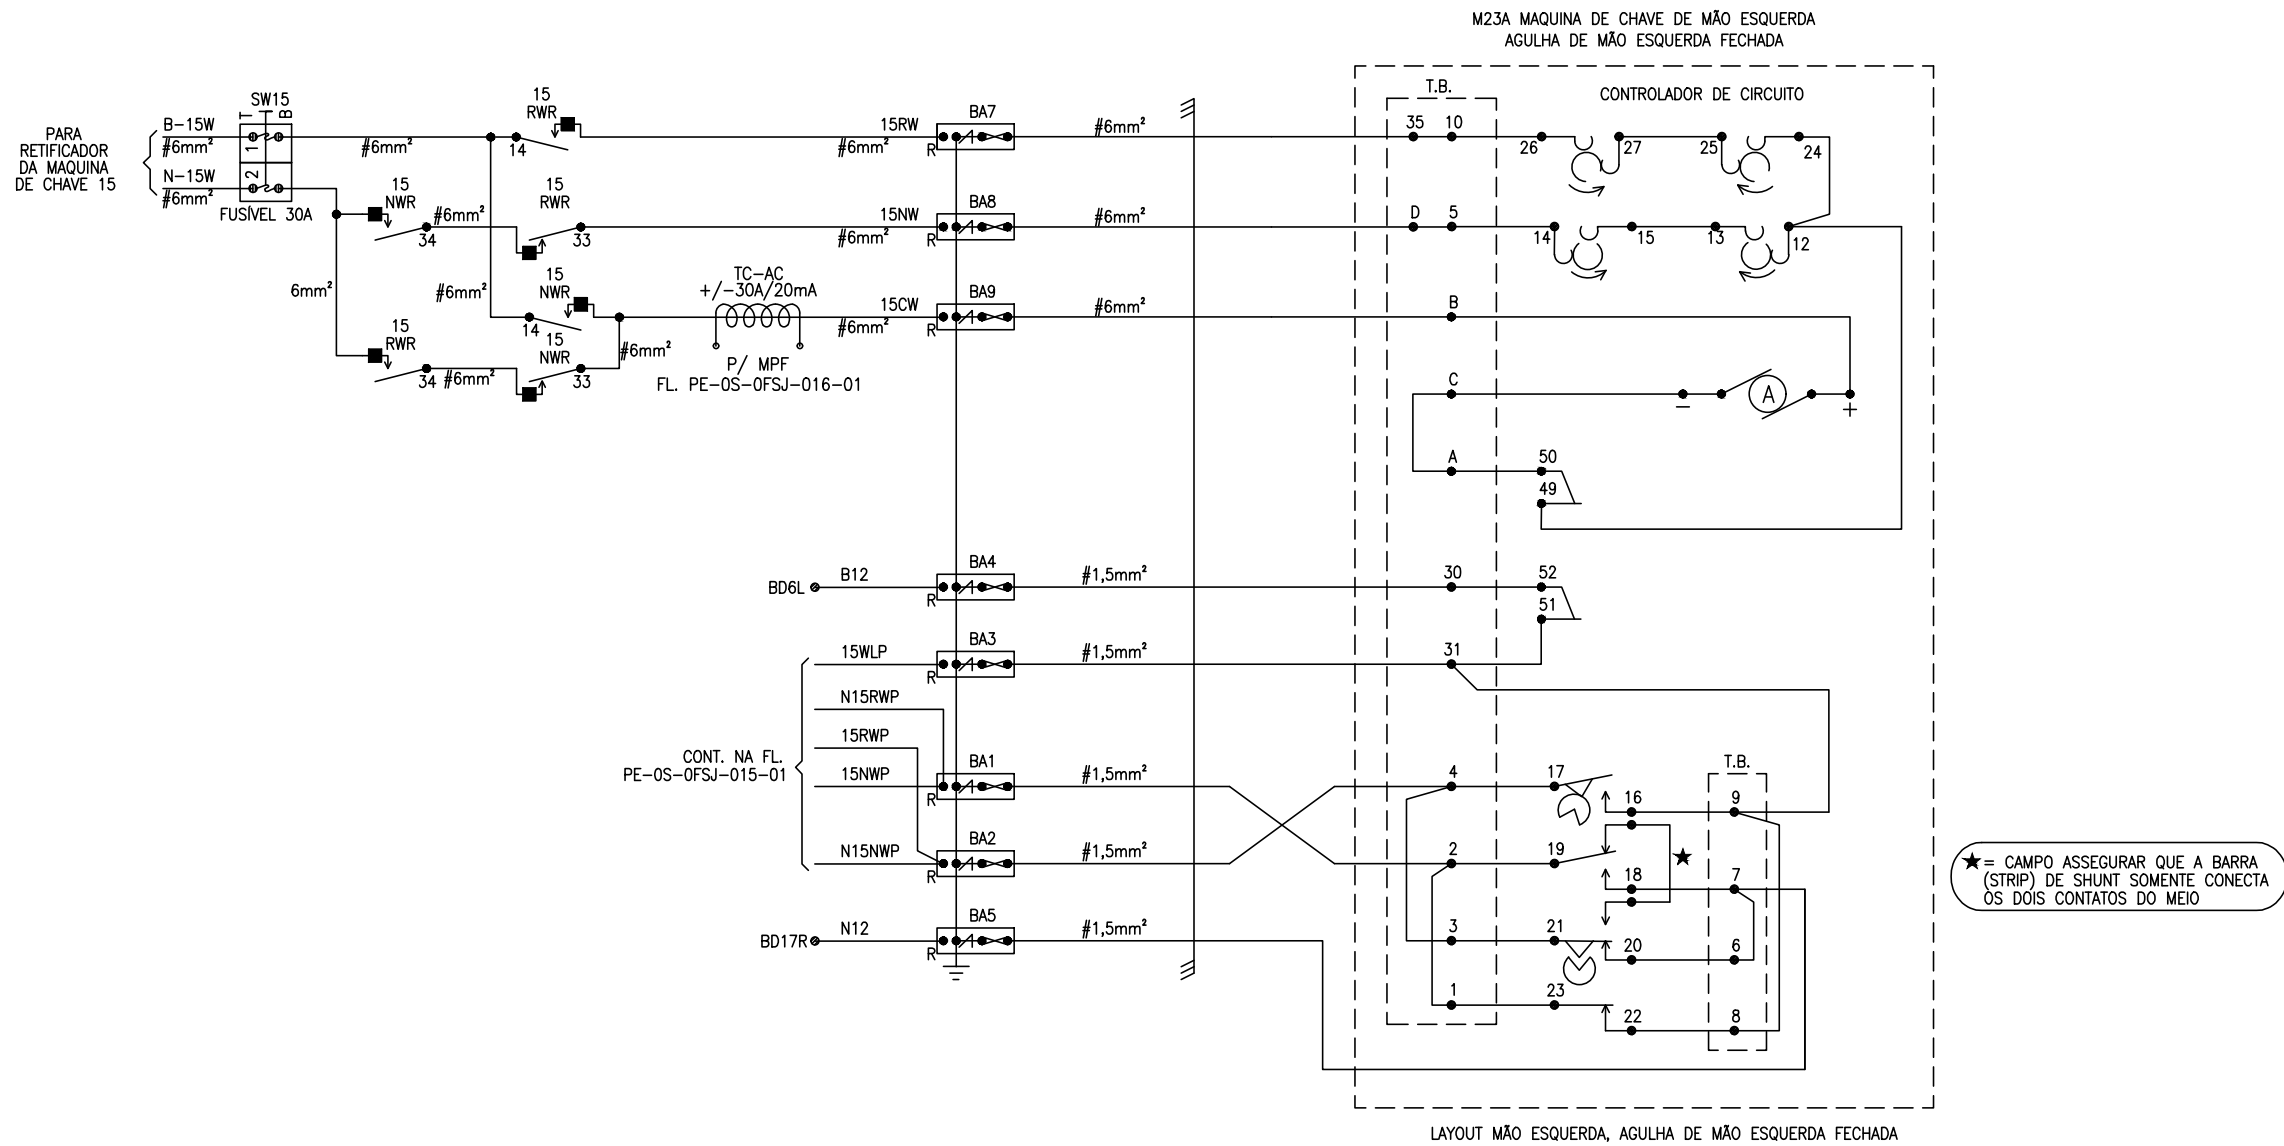

OBSERVAÇÃO:

1. $\angle$ = SUPRESSOR

2. TODOS CABOS DA HOUSE #1,5mm² EXCETO QUANDO INDICADO

ANOTAÇÕES

A Operação dos circuitos e equipamentos aqui representados não podem ser completamente verificados senão após a sua instalação de modo a formar um sistema completo de sinalização ferroviária e ser devidamente submetido a "Testes de seleção de contatos(BREAKDOWN)" e "Testes operacionais de serviço"(Através de planilhas e fluxo de testes) antes de sua colocação em serviços normal definitivo.

ENGENHARIA DE ELETROELETRÔNICA DE PROJETOS



TÍTULO DES.:

LINHA DE SÃO PAULO
 CIRCUITOS DA MÁQUINA DE CHAVE 15
 ABR 25
 SÃO JOSÉ DOS CAMPOS – FSJ

CONTROLE INTERNO DE PROJETOS GEPEE	DATA
ELABORADOR: ANTÔNIO LEAL	27/01/2023
REVISOR: MÁRCIO MOREIRA	07/02/2023
APROVADOR: MARCOS REINH	28/02/2023

FIRMA CONTRATADA:

Nº ARQUIVO MRS:

ENG.RESP.:	HAROLDO ENNES
PROJ.:	MÁRCIO MOREIRA
DES.PROJ.:	ANTÔNIO LEAL

PE-0S-0FSJ-017-01

ENG.RESP.:	HAROLDO ENNES	DATA:	27/01/2023	
PROJ.:	MÁRCIO MOREIRA	ESCALA:	—	FORMATO: A3
DES.PROJ.:	ANTÔNIO LEAL	REV./DATA:	—	
PE-0S-0FSJ-017-01		SUBST./REF.: —		

ATENÇÃO:

ESSA PLANTA SERÁ ATUALIZADA DEPOIS DA ELABORAÇÃO DO SOFTWARE DO PAINEL DE CONTROLE LOCAL

ANOTAÇÕES

A Operação dos circuitos e equipamentos aqui representados não podem ser completamente verificados senão após a sua instalação de modo a formar um sistema completo de sinalização ferroviária e ser devidamente submetido a "Testes de seleção de contatos(BREAKDOWN)" e "Testes operacionais de serviço"(Através de planilhas e fluxo de testes) antes de sua colocação em serviços normal definitivo.
ENGENHARIA DE ELETROELETRÔNICA DE PROJETOS

CONTROLE INTERNO DE PROJETOS CEPEE	DATA
ELABORADOR: ANTÔNIO LEAL	27/01/2023
REVISOR: MÁRCIO MOREIRA	07/02/2023
APROVADOR: MARCOS REINH	28/02/2023




FIRMA CONTRATADA:

—

Nº ARQUIVO MRS:


TÍTULO DES.:
**LINHA DE SÃO PAULO
LAYOUT DO PAINEL DE CONTROLE LOCAL
ABR 25
SÃO JOSÉ DOS CAMPOS – FSJ**

ENG.RESP.: HAROLDO ENNES	DATA: 27/01/2023
PROJ.: MÁRCIO MOREIRA	ESCALA: — FORMATO: A3
DES.PROJ.: ANTÔNIO LEAL	REV./DATA: —
SUBST./REF.: —	

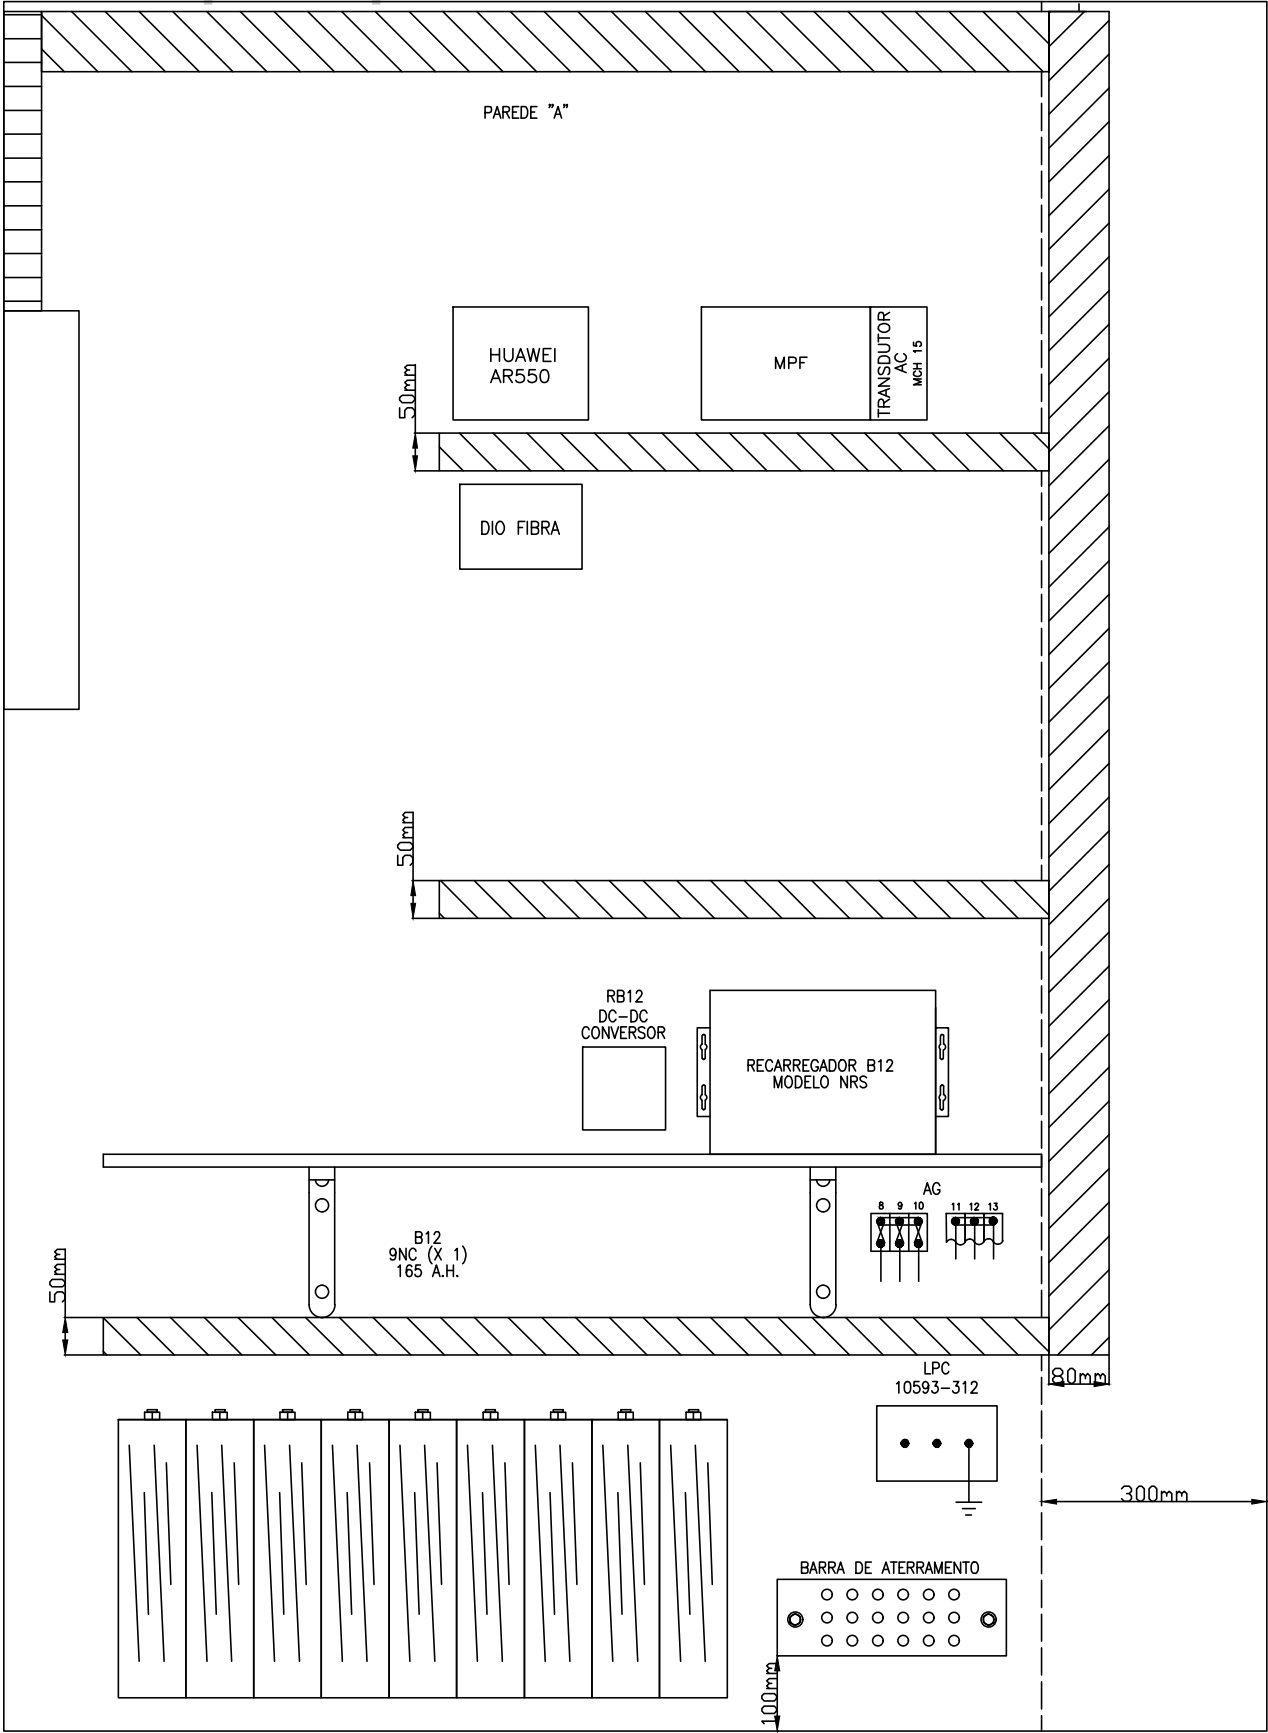

OBSERVAÇÕES:
1. COTAS EM MILÍMETROS

ANOTAÇÕES	A Operação dos circuitos e equipamentos aqui representados não podem ser completamente verificados senão após a sua instalação de modo a formar um sistema completo de sinalização ferroviária e ser devidamente submetido a "Testes de seleção de contatos(BREAKDOWN)" e "Testes operacionais de serviço"(Através de planilhas e fluxo de testes) antes de sua colocação em serviços normal definitivo. ENGENHARIA DE ELETROELETRÔNICA DE PROJETOS			 Logística S.A.	TÍTULO DES.: LINHA DE SÃO PAULO ABRIGO 1829mm x 1829mm LAYOUT DA PAREDE "A"		
		ABR 25 SÃO JOSÉ DOS CAMPOS – FSJ					
		CONTROLE INTERNO DE PROJETOS GEPEE	DATA	FIRMA CONTRATADA: -	ENG.RESP.: HAROLDO ENNES	DATA: 27/01/2023	
		ELABORADOR: ANTONIO LEAL	27/01/2023		PROJ.: MÁRCIO MOREIRA	ESCALA: 1:10	FORMATO: A3
		REVISOR: MÁRCIO MOREIRA	07/02/2023		DES.PROJ.: ANTÔNIO LEAL	REV./DATA: -	
APROVADOR: MARCOS REINH	28/02/2023	Nº ARQUIVO MRS: PE-0S-0FSJ-019-01			SUBST./REF.: -		

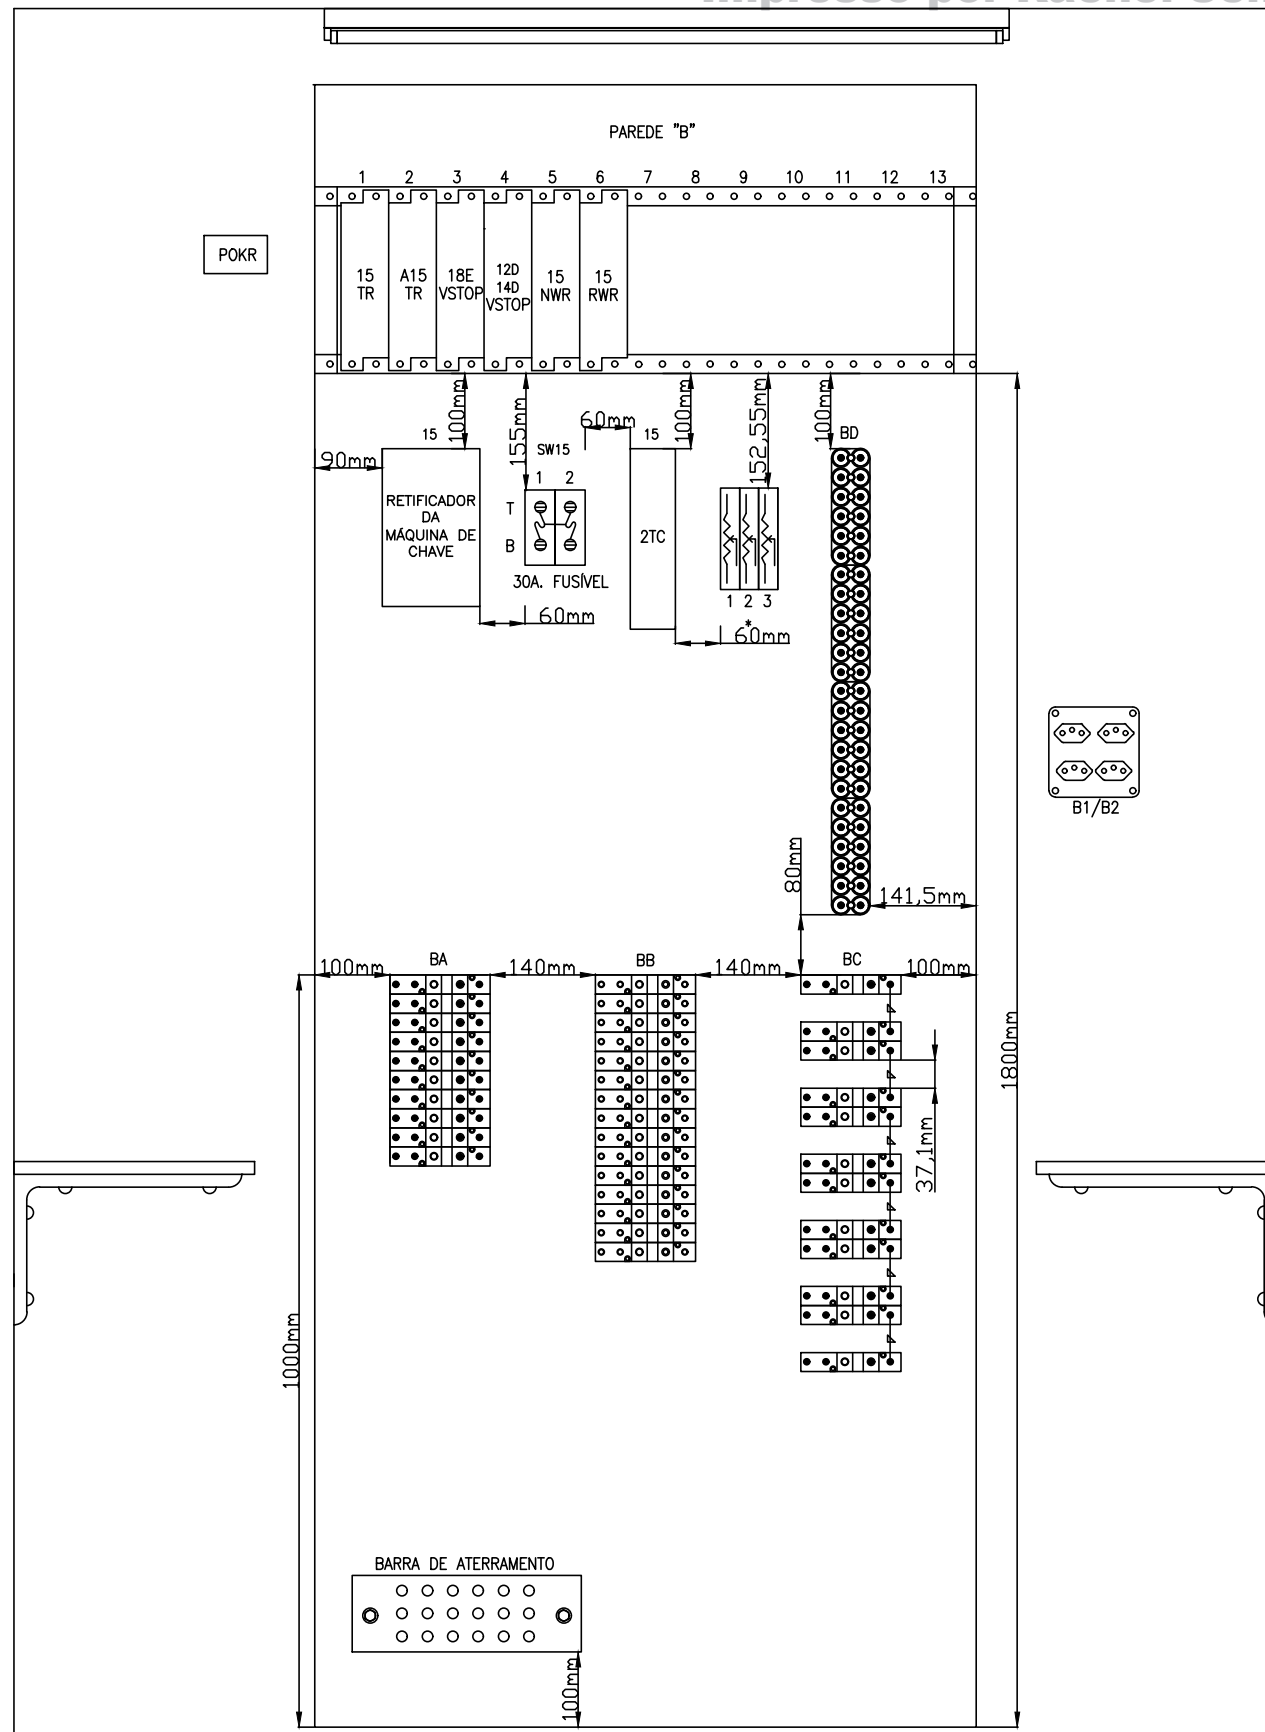

1/1	1/2	1/3	1/4	1/5	1/6	1/7	1/8	1/9	1/10	1/11
15TR	A15TR	18EVSTOP	12D-14DVSTOP	15NWR	15RWR					
▽ ▽ ▽ △ ▽ △ ▽ ▽ ▽ △ ▽ △	▽ ▽ ▽ △ ▽ △ ▽ ▽ ▽ △ ▽ △	▽ ▽ ▽ △ ▽ △ ▽ ▽ ▽ △ ▽ △	▽ ▽ ▽ △ ▽ △ ▽ ▽ ▽ △ ▽ △	▽ ▽ △ ▽	▽ ▽ △ ▽					
A62-0120	A62-0120	A62-0311	A62-0311	A62-0429	A62-0429					CARREIRA DE RELÉ

$1/12$	$1/13$

LEGENDA DE RELÉ

▼ = CONTATO FRONT UTILIZADO
 √ = CONTATO FRONT NÃO UTILIZADO
 — = CALCANHAR
 ∧ = CONTATO BACK NÃO UTILIZADO
 ▲ = CONTATO BACK UTILIZADO

REFERÊNCIA CRUZADA

TABELA MRS	ALSTOM RELAY PN	SAFETRAN RELAY PN	DIAGRAMA DE CONTATO
B49	A62-0429	400520	A
B44	A62-0311	400022	B
B42	A62-0120	400510	B

RESISTORES DE CDV

- *1 15TB RES (5 Ω)
- *2 15RB RES (5 Ω)
- *3 A15RB RES (5 Ω)

VISÃO DE TRÁS DOS RELÉS


3	2	1
∇	∇	6
—	—	4
—	—	3
∧	∧	2
		1

A

3	2	1
∇	∇	6
—	—	5
∧	∇	4
∇	—	3
—	—	2
∧	∧	1

B

POKR		
9	F	11
10	—	12

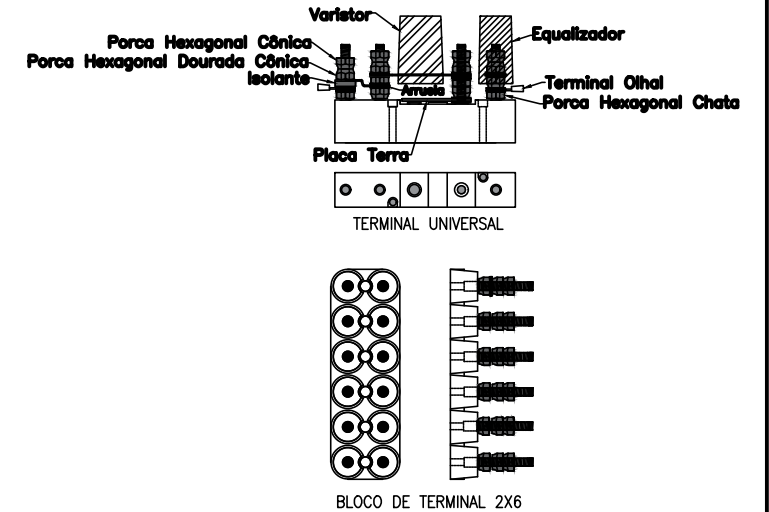

OBSERVAÇÕES:
1. COTAS EM MILÍMETROS

ANOTAÇÕES

REV. 1 - 18/05/2023

REVISÃO DEVIDO ALTERAÇÃO DO PROJETO PELA ÁREA DE ENG. OPERAÇÕES, RETIRANDO A MCH 5 E 11 E PASSANDO PARA TRAVADORES ELÉTRICOS

PROJ.: MÁRCIO MOREIRA
DES.: HYGOR TEODORO
REVISOR: MARCOS REINH
REV. 2 - 04/10/2023

REVISÃO DO PROJETO RETIRANDO O VERMELHO E AMARELO E REALIZANDO A ENTREGA EM DEFINITIVO (PRETO)

PROJ.: MÁRCIO MOREIRA
DES.: ANTÔNIO LEAL
REVISOR: HYGOR TEODORO

A Operação dos circuitos e equipamentos aqui representados não podem ser completamente verificados senão após a sua instalação de modo a formar um sistema completo de sinalização ferroviária e ser devidamente submetido a "Testes de seleção de contatos(BREAKDOWN)" e "Testes operacionais de serviço"(Através de planilhas e fluxo de testes) antes de sua colocação em serviços normal definitivo.

ENGENHARIA DE ELETROELETRÔNICA DE PROJETOS

CONTROLE INTERNO DE PROJETOS GEPEE	DATA
ELABORADOR: ANTÔNIO LEAL	04/10/2023
REVISOR: MARCOS REINH	19/10/2023
APROVADOR: ALEXANDRE MENEGHEL	05/12/2023



FIRMA CONTRATADA:

Nº ARQUIVO MRS:

TÍTULO DES.:

LINHA DE SÃO PAULO
 ABRIGO 1829mm x 1829mm LAYOUT DA PAREDE "B"
 ABR 25
SÃO JOSÉ DOS CAMPOS – FSJ

ENG.RESP.: HAROLDO ENNES


DES.PROJ.: ANTONIO LEAL

DATA: 06/02/2023

ESCALA:	1:10	FORMATO:	A3
---------	------	----------	----


REV./DATA: 2 - 04/10/2023

SUBST./REF.: -

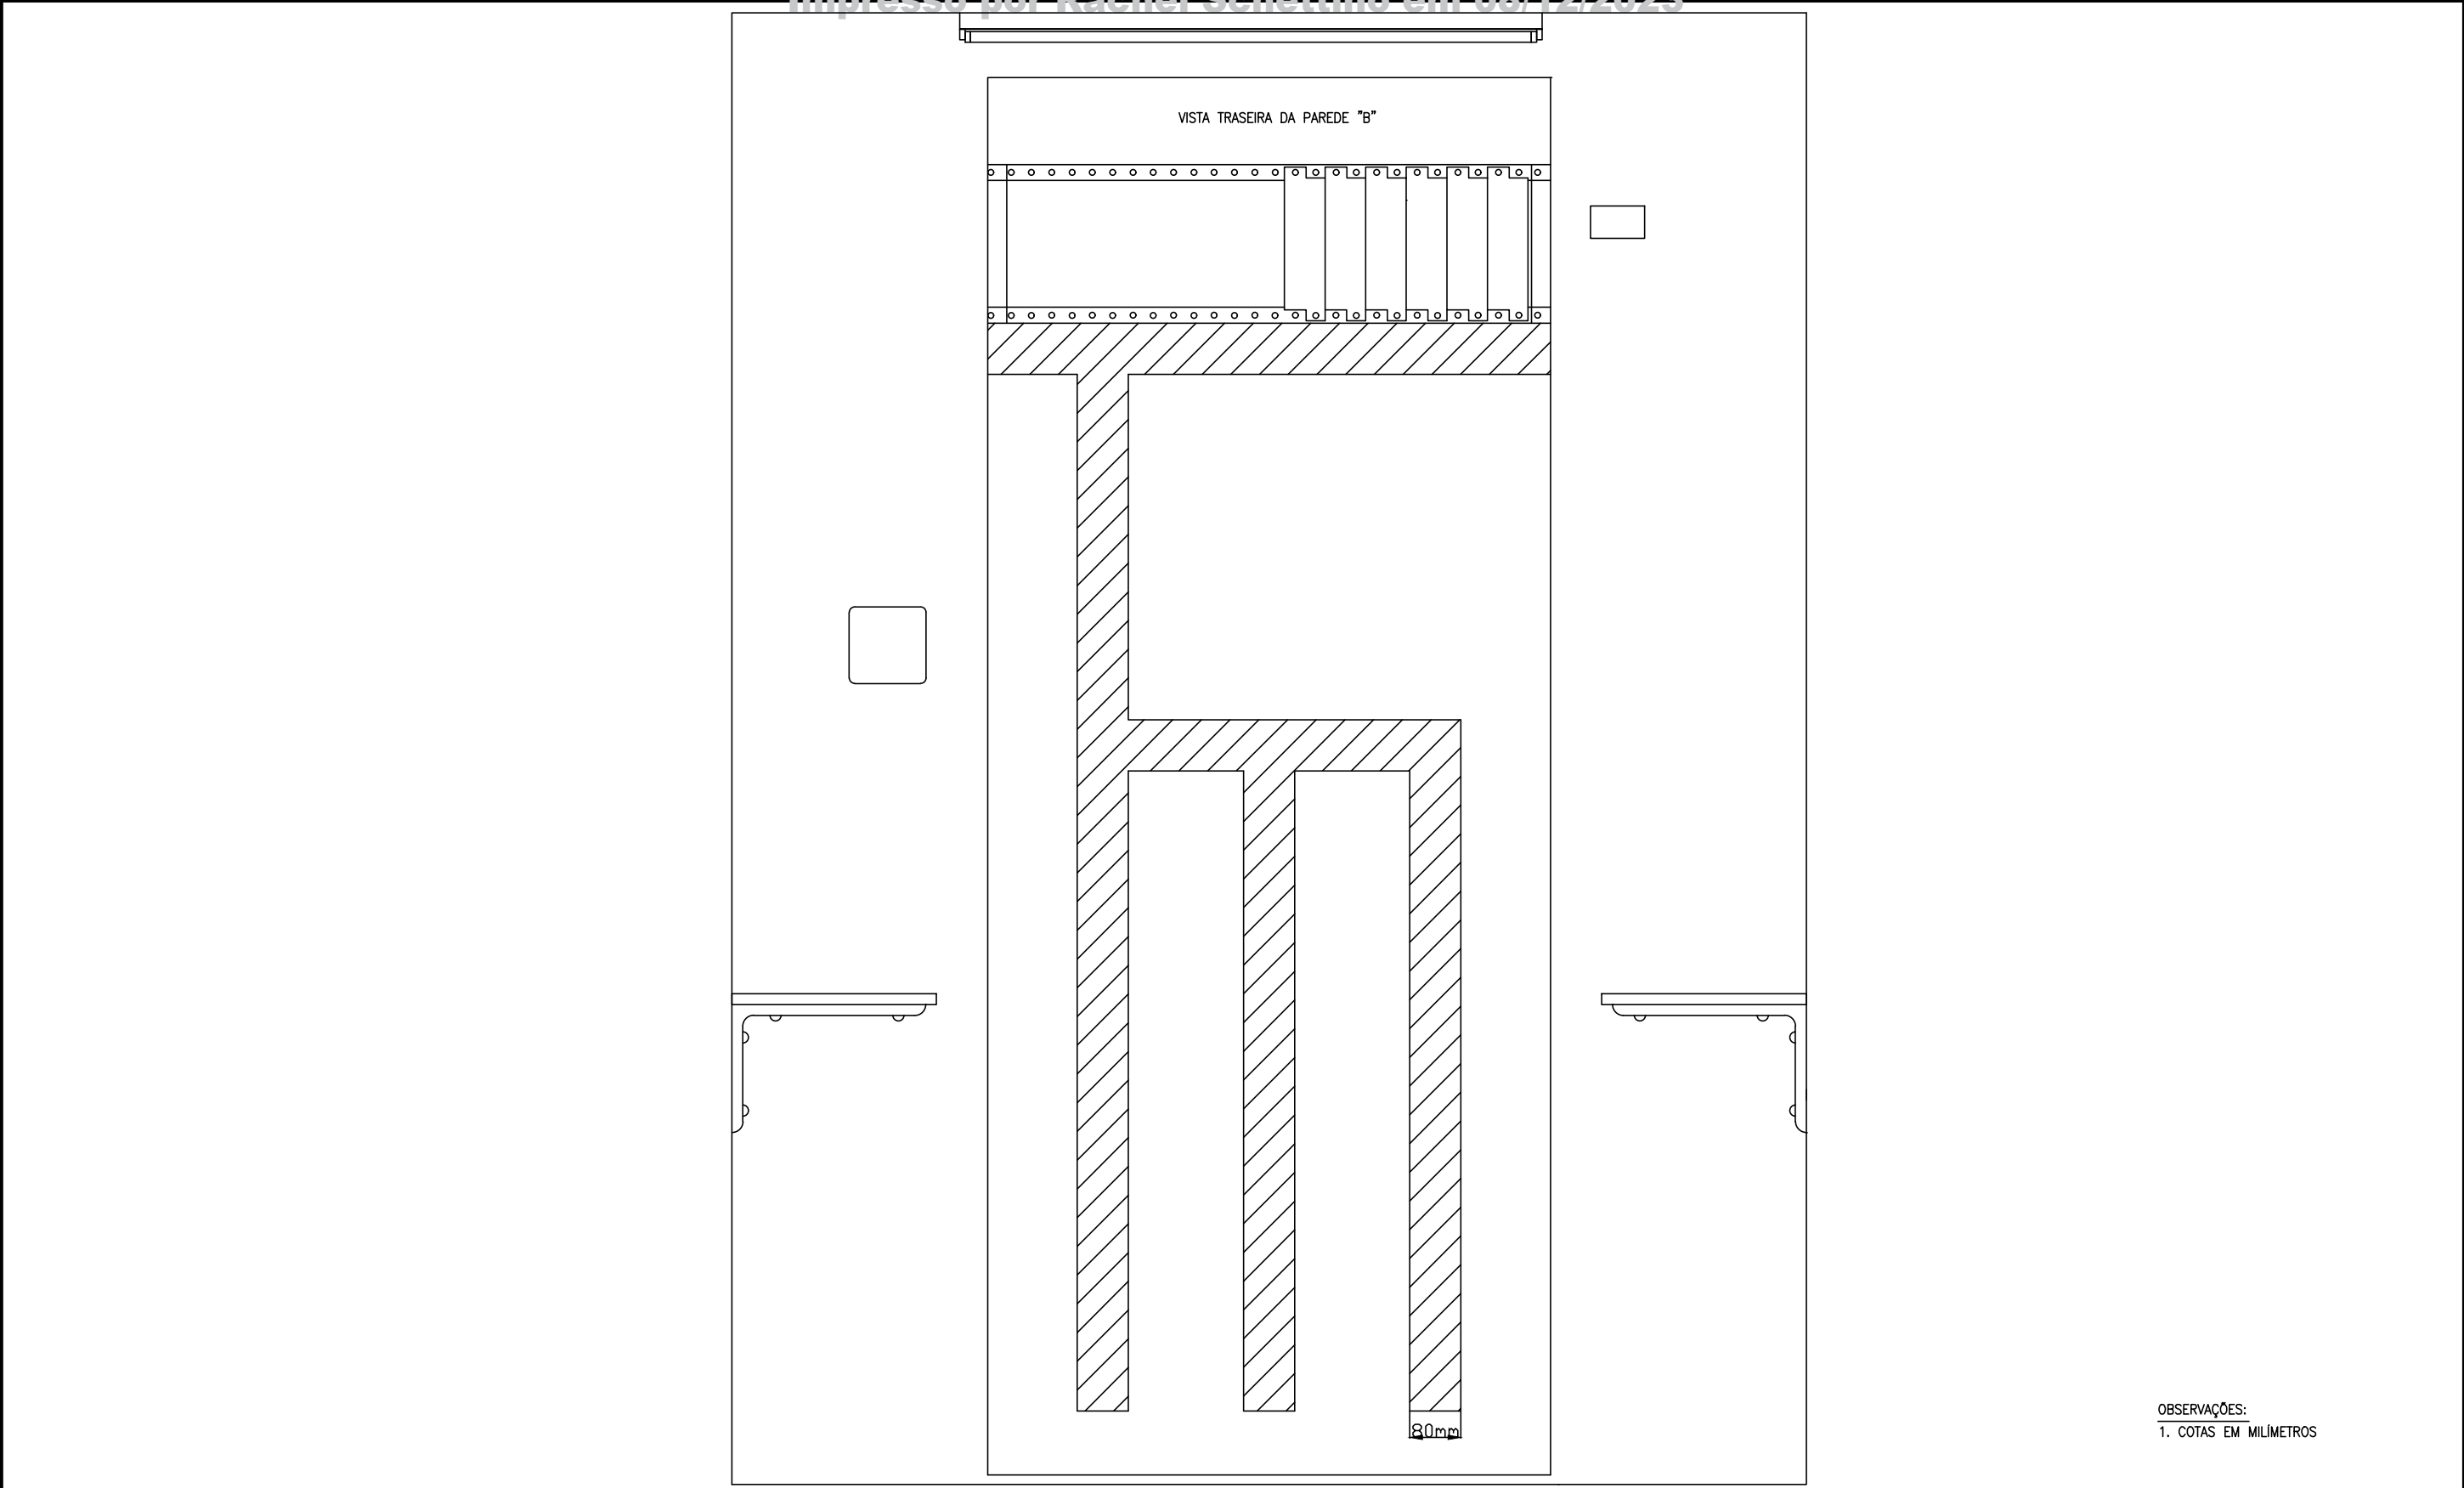


OBSERVAÇÕES:
1. COTAS EM MILÍMETROS

ANOTAÇÕES	A Operação dos circuitos e equipamentos aqui representados não podem ser completamente verificados senão após a sua instalação de modo a formar um sistema completo de sinalização ferroviária e ser devidamente submetido a "Testes de seleção de contatos(BREAKDOWN)" e "Testes operacionais de serviço"(Através de planilhas e fluxo de testes) antes de sua colocação em serviços normal definitivo. ENGENHARIA DE ELETROELETRÔNICA DE PROJETOS	MRS Logística S.A.		TÍTULO DES.: LINHA DE SÃO PAULO			
				ABRIGO 1829mm x 1829mm LAYOUT DO PAINEL TRASEIRO PAREDE "B"			
				ABR 25			
				SÃO JOSÉ DOS CAMPOS – FSJ			
	CONTROLE INTERNO DE PROJETOS GEPEE	DATA	FIRMA CONTRATADA: -	ENG.RESP.: HAROLDO ENNES	DATA: 06/02/2023		
	ELABORADOR: ANTÔNIO LEAL	06/02/2023		PROJ.: MÁRCIO MOREIRA	ESCALA: 1:10	FORMATO: A3	
	REVISOR: MÁRCIO MOREIRA	07/02/2023		DES.PROJ.: ANTÔNIO LEAL	REV./DATA: -		
	APROVADOR: MARCOS REINH	28/02/2023		Nº ARQUIVO MRS: PE-0S-0FSJ-021-01		SUBST./REF.: -	

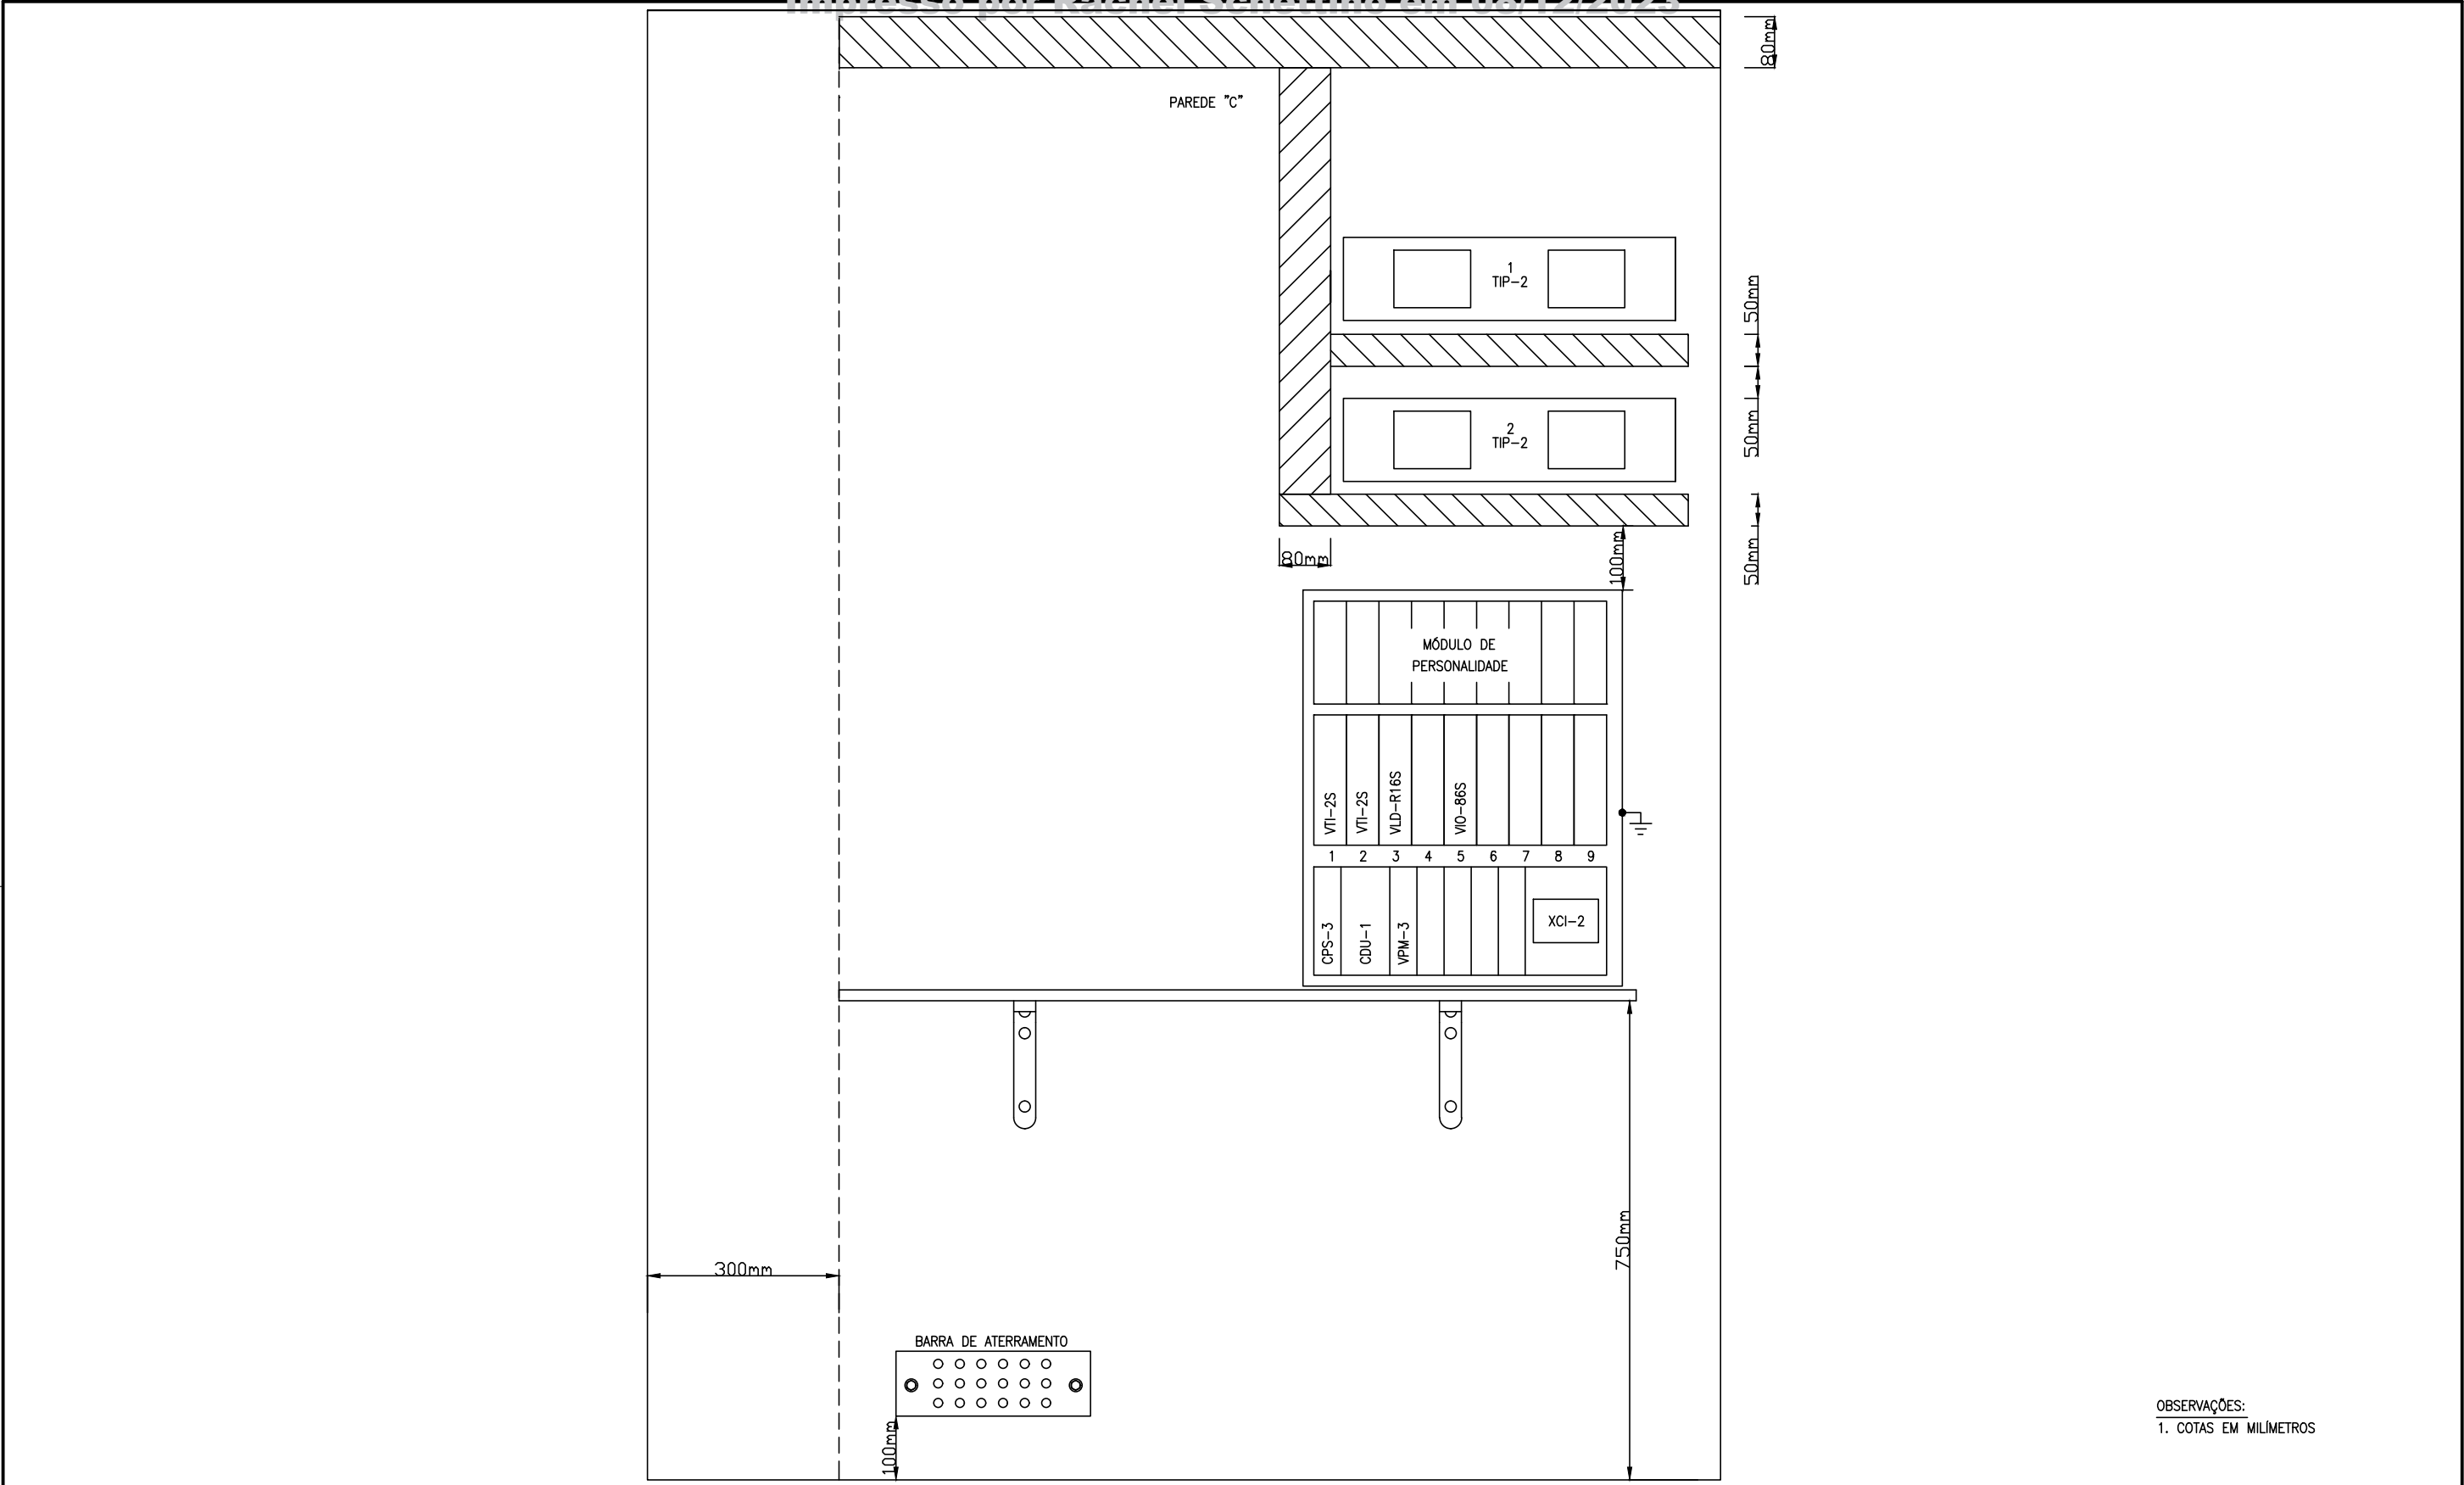

ANOTAÇÕES	A Operação dos circuitos e equipamentos aqui representados não podem ser completamente verificados senão após a sua instalação de modo a formar um sistema completo de sinalização ferroviária e ser devidamente submetido a "Testes de seleção de contatos(BREAKDOWN)" e "Testes operacionais de serviço"(Através de planilhas e fluxo de testes) antes de sua colocação em serviços normal definitivo. ENGENHARIA DE ELETROELETRÔNICA DE PROJETOS			 Logística S.A.	TÍTULO DES.: LINHA DE SÃO PAULO ABRIGO 1829mm x 1829mm LAYOUT DA PAREDE "C" ABR 25 SÃO JOSÉ DOS CAMPOS – FSJ								
					FIRMA CONTRATADA:		ENG.RESP.: HAROLDO ENNES		DATA: 06/02/2023				
		CONTROLE INTERNO DE PROJETOS GEPEE		DATA		-		PROJ.: MÁRCIO MOREIRA		ESCALA: 1:10		FORMATO: A3	
		ELABORADOR: ANTÔNIO LEAL		06/02/2023				DES.PROJ.: ANTÔNIO LEAL		REV./DATA: -			
		REVISOR: MÁRCIO MOREIRA		07/02/2023				N° ARQUIVO MRS: PE-0S-0FSJ-022-01					
		APROVADOR: MARCOS REINH		28/02/2023		SUBST./REF.: -							

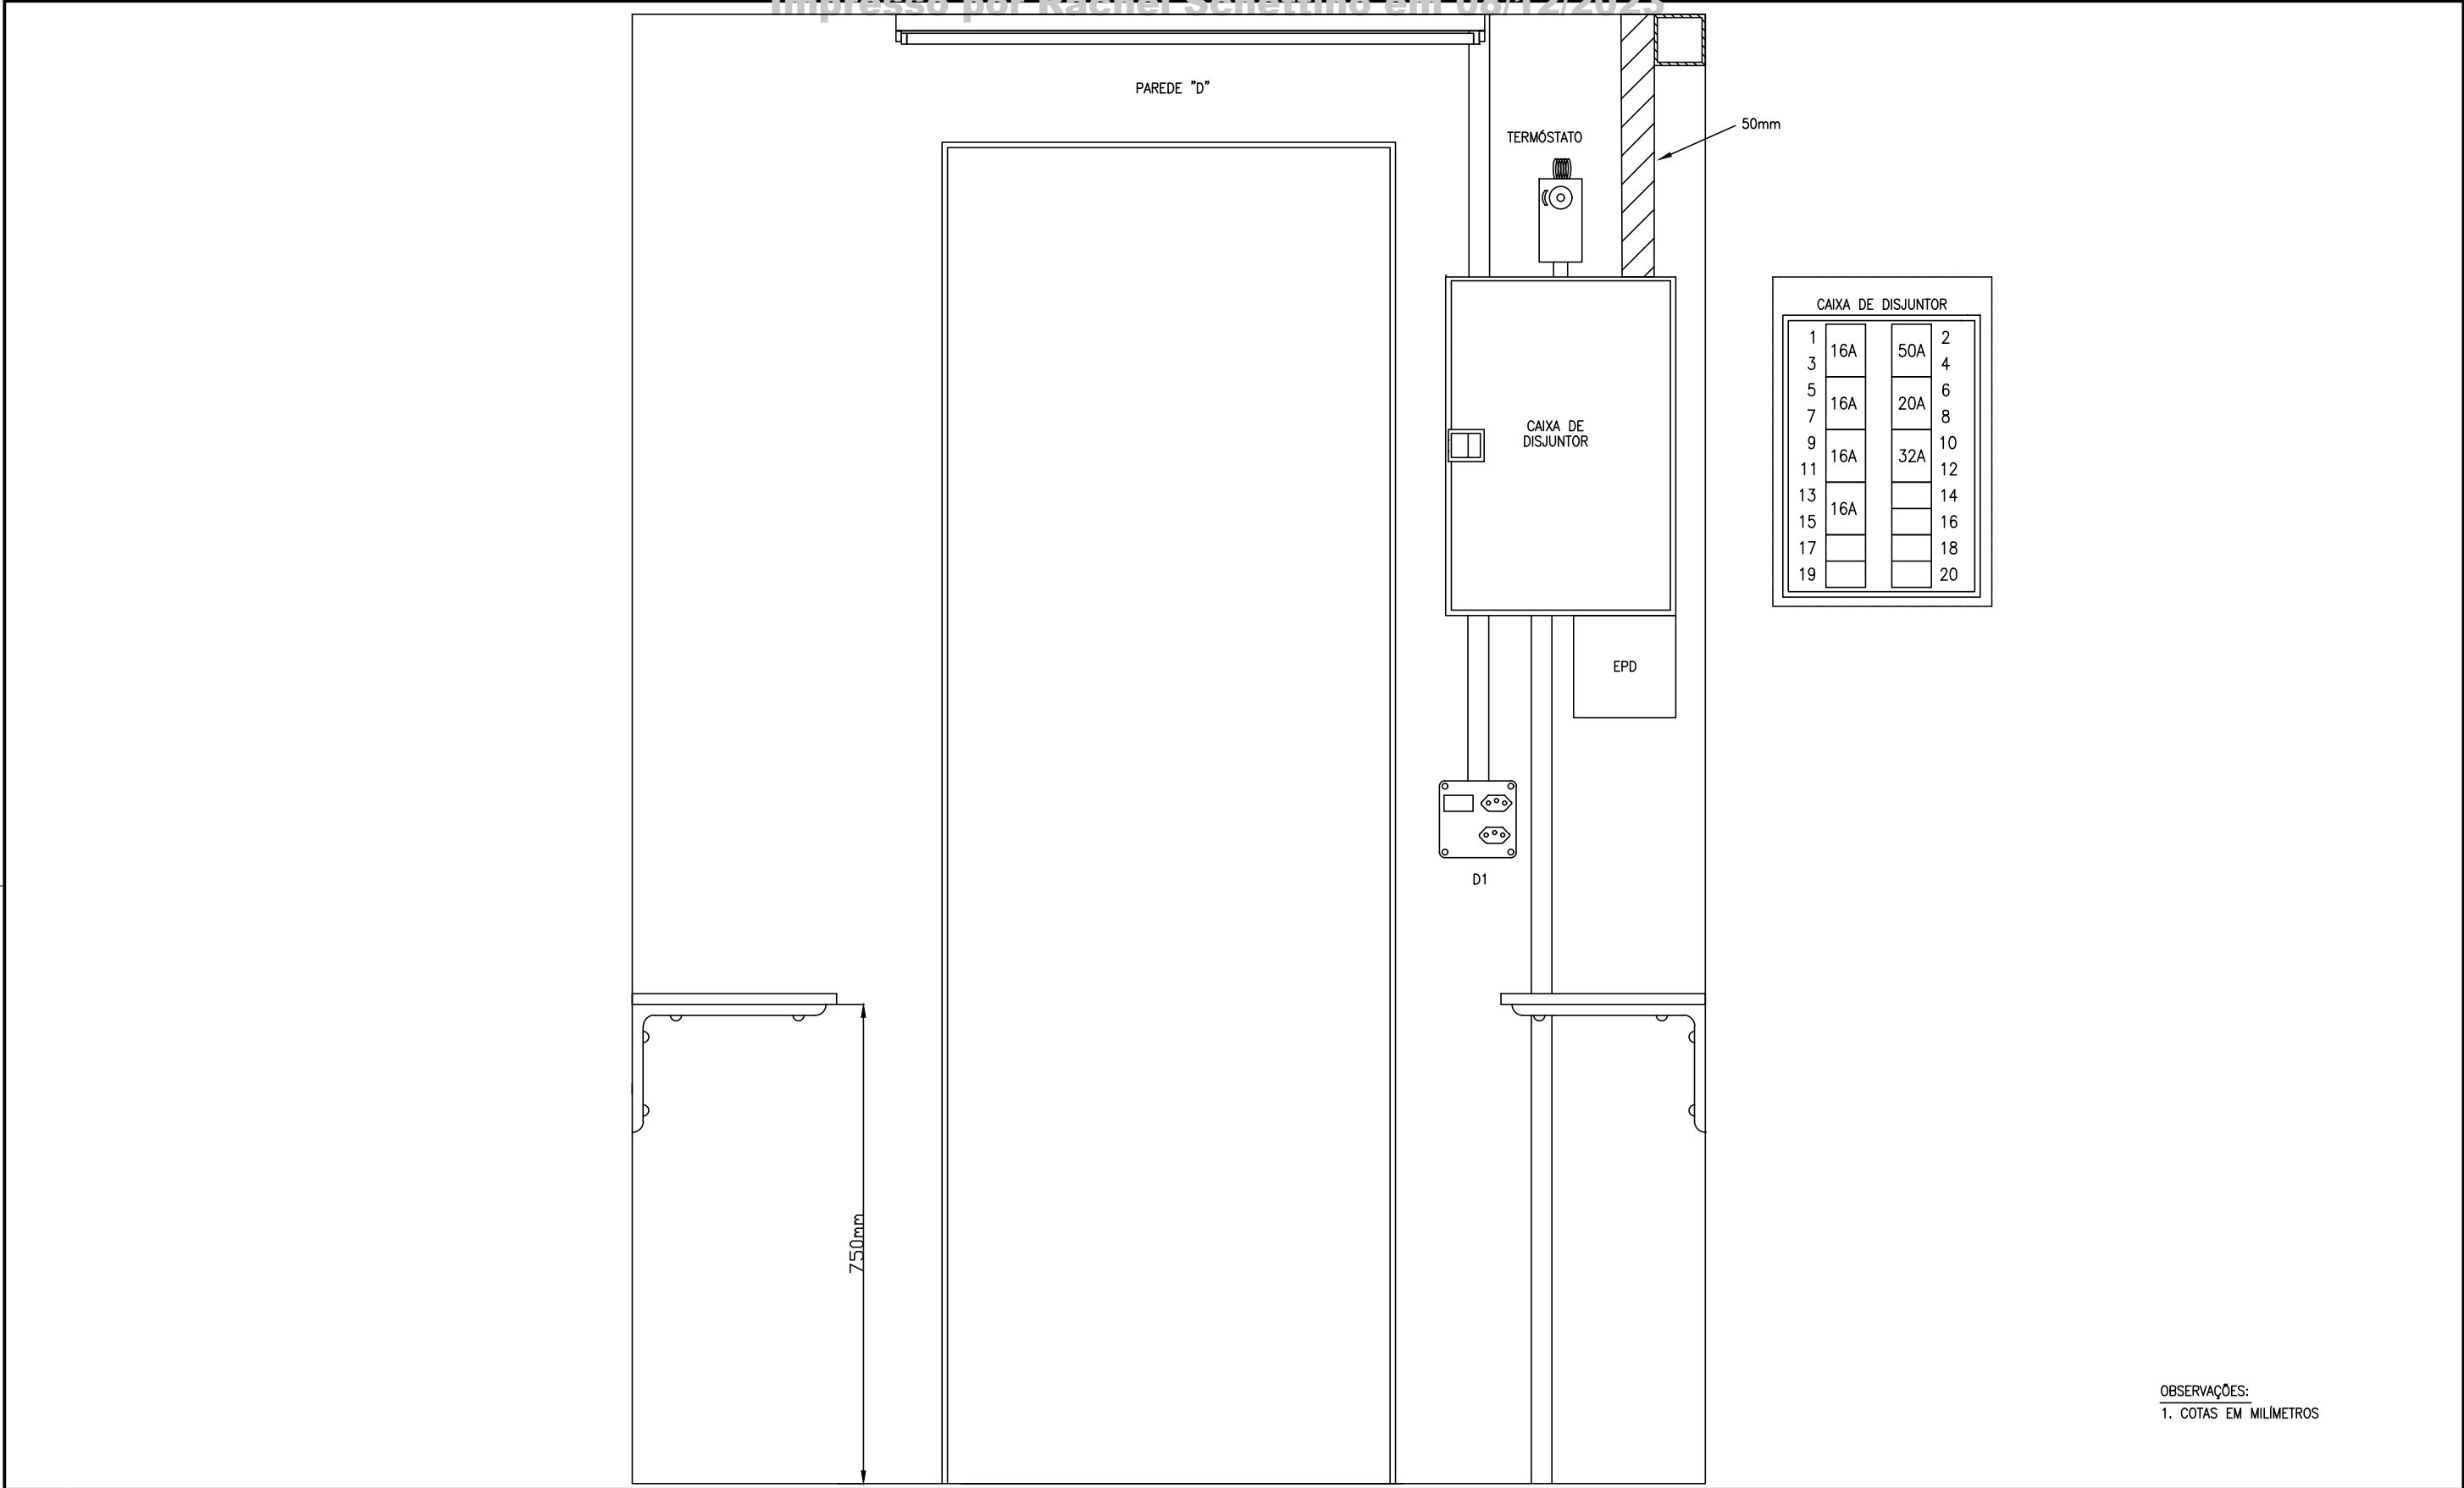

OBSERVAÇÕES:
1. COTAS EM MILÍMETROS

ANOTAÇÕES

A Operação dos circuitos e equipamentos aqui representados não podem ser completamente verificados senão após a sua instalação de modo a formar um sistema completo de sinalização ferroviária e ser devidamente submetido a "Testes de seleção de contatos(BREAKDOWN)" e "Testes operacionais de serviço"(Através de planilhas e fluxo de testes) antes de sua colocação em serviços normal definitivo.
ENGENHARIA DE ELETROELETRÔNICA DE PROJETOS

CONTROLE INTERNO DE PROJETOS GEPEE	DATA
ELABORADOR: ANTÔNIO LEAL	06/02/2023
REVISOR: MÁRCIO MOREIRA	07/02/2023
APROVADOR: MARCOS REINH	28/02/2023







FIRMA CONTRATADA:

Nº ARQUIVO MRS:


TÍTULO DES.:
LINHA DE SÃO PAULO
ABRIGO 1829mm x 1829mm LAYOUT DA PAREDE "D"
ABR 25
SÃO JOSÉ DOS CAMPOS – FSJ

ENG.RESP.: HAROLDO ENNES	DATA: 06/02/2023
PROJ.: MÁRCIO MOREIRA	ESCALA: 1:10 FORMATO: A3
DES.PROJ.: ANTÔNIO LEAL	REV./DATA: -
SUBST./REF.: -	

PE-OS-0FSJ-023-01

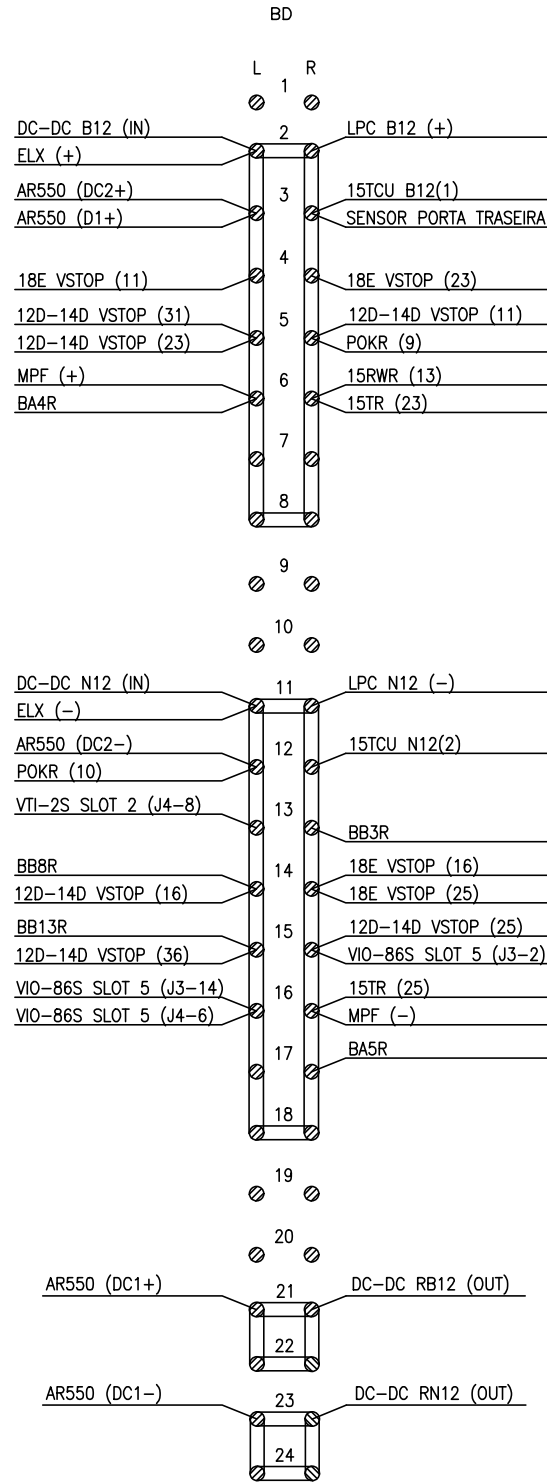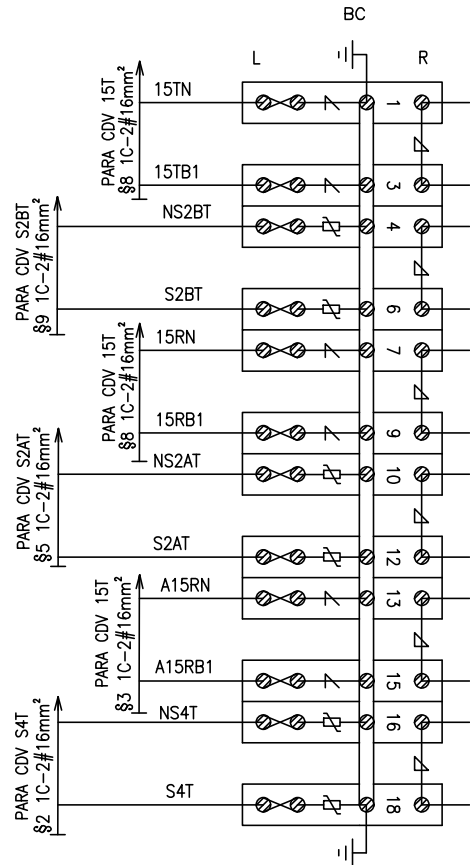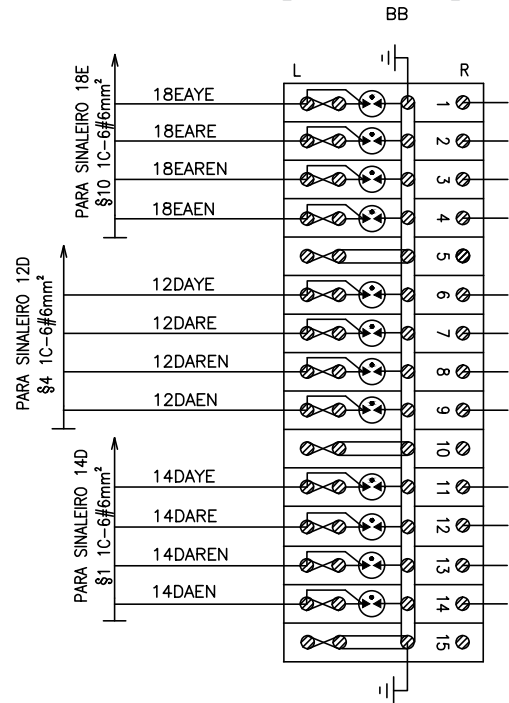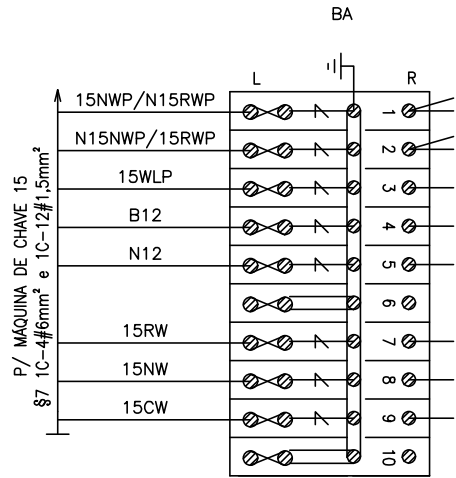

LEGENDA DE NOMENCLATURA

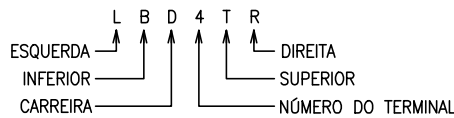

OBSERVAÇÕES:

- ∠ = SUPRESSOR
B = VARISTOR CLAMPER
⊗ = SUPRESSOR HÍBRIDO
Δ = EQUALIZADOR
⊙ = PINO DE TERMINAL
⊗ = LINK DE TESTE
⊖ = LINK SOLIDO
⊥ = TERRA

ANOTAÇÕES

REV. 1 - 18/05/2023
REVISÃO DEVIDO ALTERAÇÃO DO PROJETO PELA ÁREA DE ENG OPERAÇÕES, RETIRANDO A MCH 5 E 11 E PASSANDO PARA TRAVADORES ELÉTRICOS
PROJ.: MÁRCIO MOREIRA DES.: HYGOR TEODORO REVISOR: MARCOS REINH
REV. 2 - 04/10/2023
REVISÃO DO PROJETO, RETIRANDO O VERMELHO E AMARELO E REALIZANDO A ENTREGA EM DEFINITIVO (PRETO)
PROJ.: MÁRCIO MOREIRA DES.: ANTONIO LEAL REVISOR: HYGOR TEODORO

A Operação dos circuitos e equipamentos aqui representados não podem ser completamente verificados senão após a sua instalação de modo a formar um sistema completo de sinalização ferroviária e ser devidamente submetido a "Testes de seleção de contatos(BREAKDOWN)" e "Testes operacionais de serviço"(Através de planilhas e fluxo de testes) antes de sua colocação em serviços normal definitivo.
ENGENHARIA DE ELETROELETRÔNICA DE PROJETOS



TÍTULO DES.: LINHA DE SÃO PAULO
DETALHE DO PAINEL DE TERMINAIS [TB]
ABR 25
SÃO JOSÉ DOS CAMPOS – FSJ

CONTROLE INTERNO DE PROJETOS GEPEE	DATA
ELABORADOR: ANTONIO LEAL	04/10/2023
REVISOR: MARCOS REINH	19/10/2023
APROVADOR: ALEXANDRE MENEHUEL	05/12/2023

FIRMA CONTRATADA:
-
Nº ARQUIVO MRS:

ENG.RESP.: HAROLDO ENNES	DATA: 07/02/2023
PROJ.: MÁRCIO MOREIRA	ESCALA: -
DES.PROJ.: ANTONIO LEAL	FORMATO: A3
REV./DATA: 2 - 04/10/2023	
SUBST./REF.: -	

PE-0S-0FSJ-024-01