


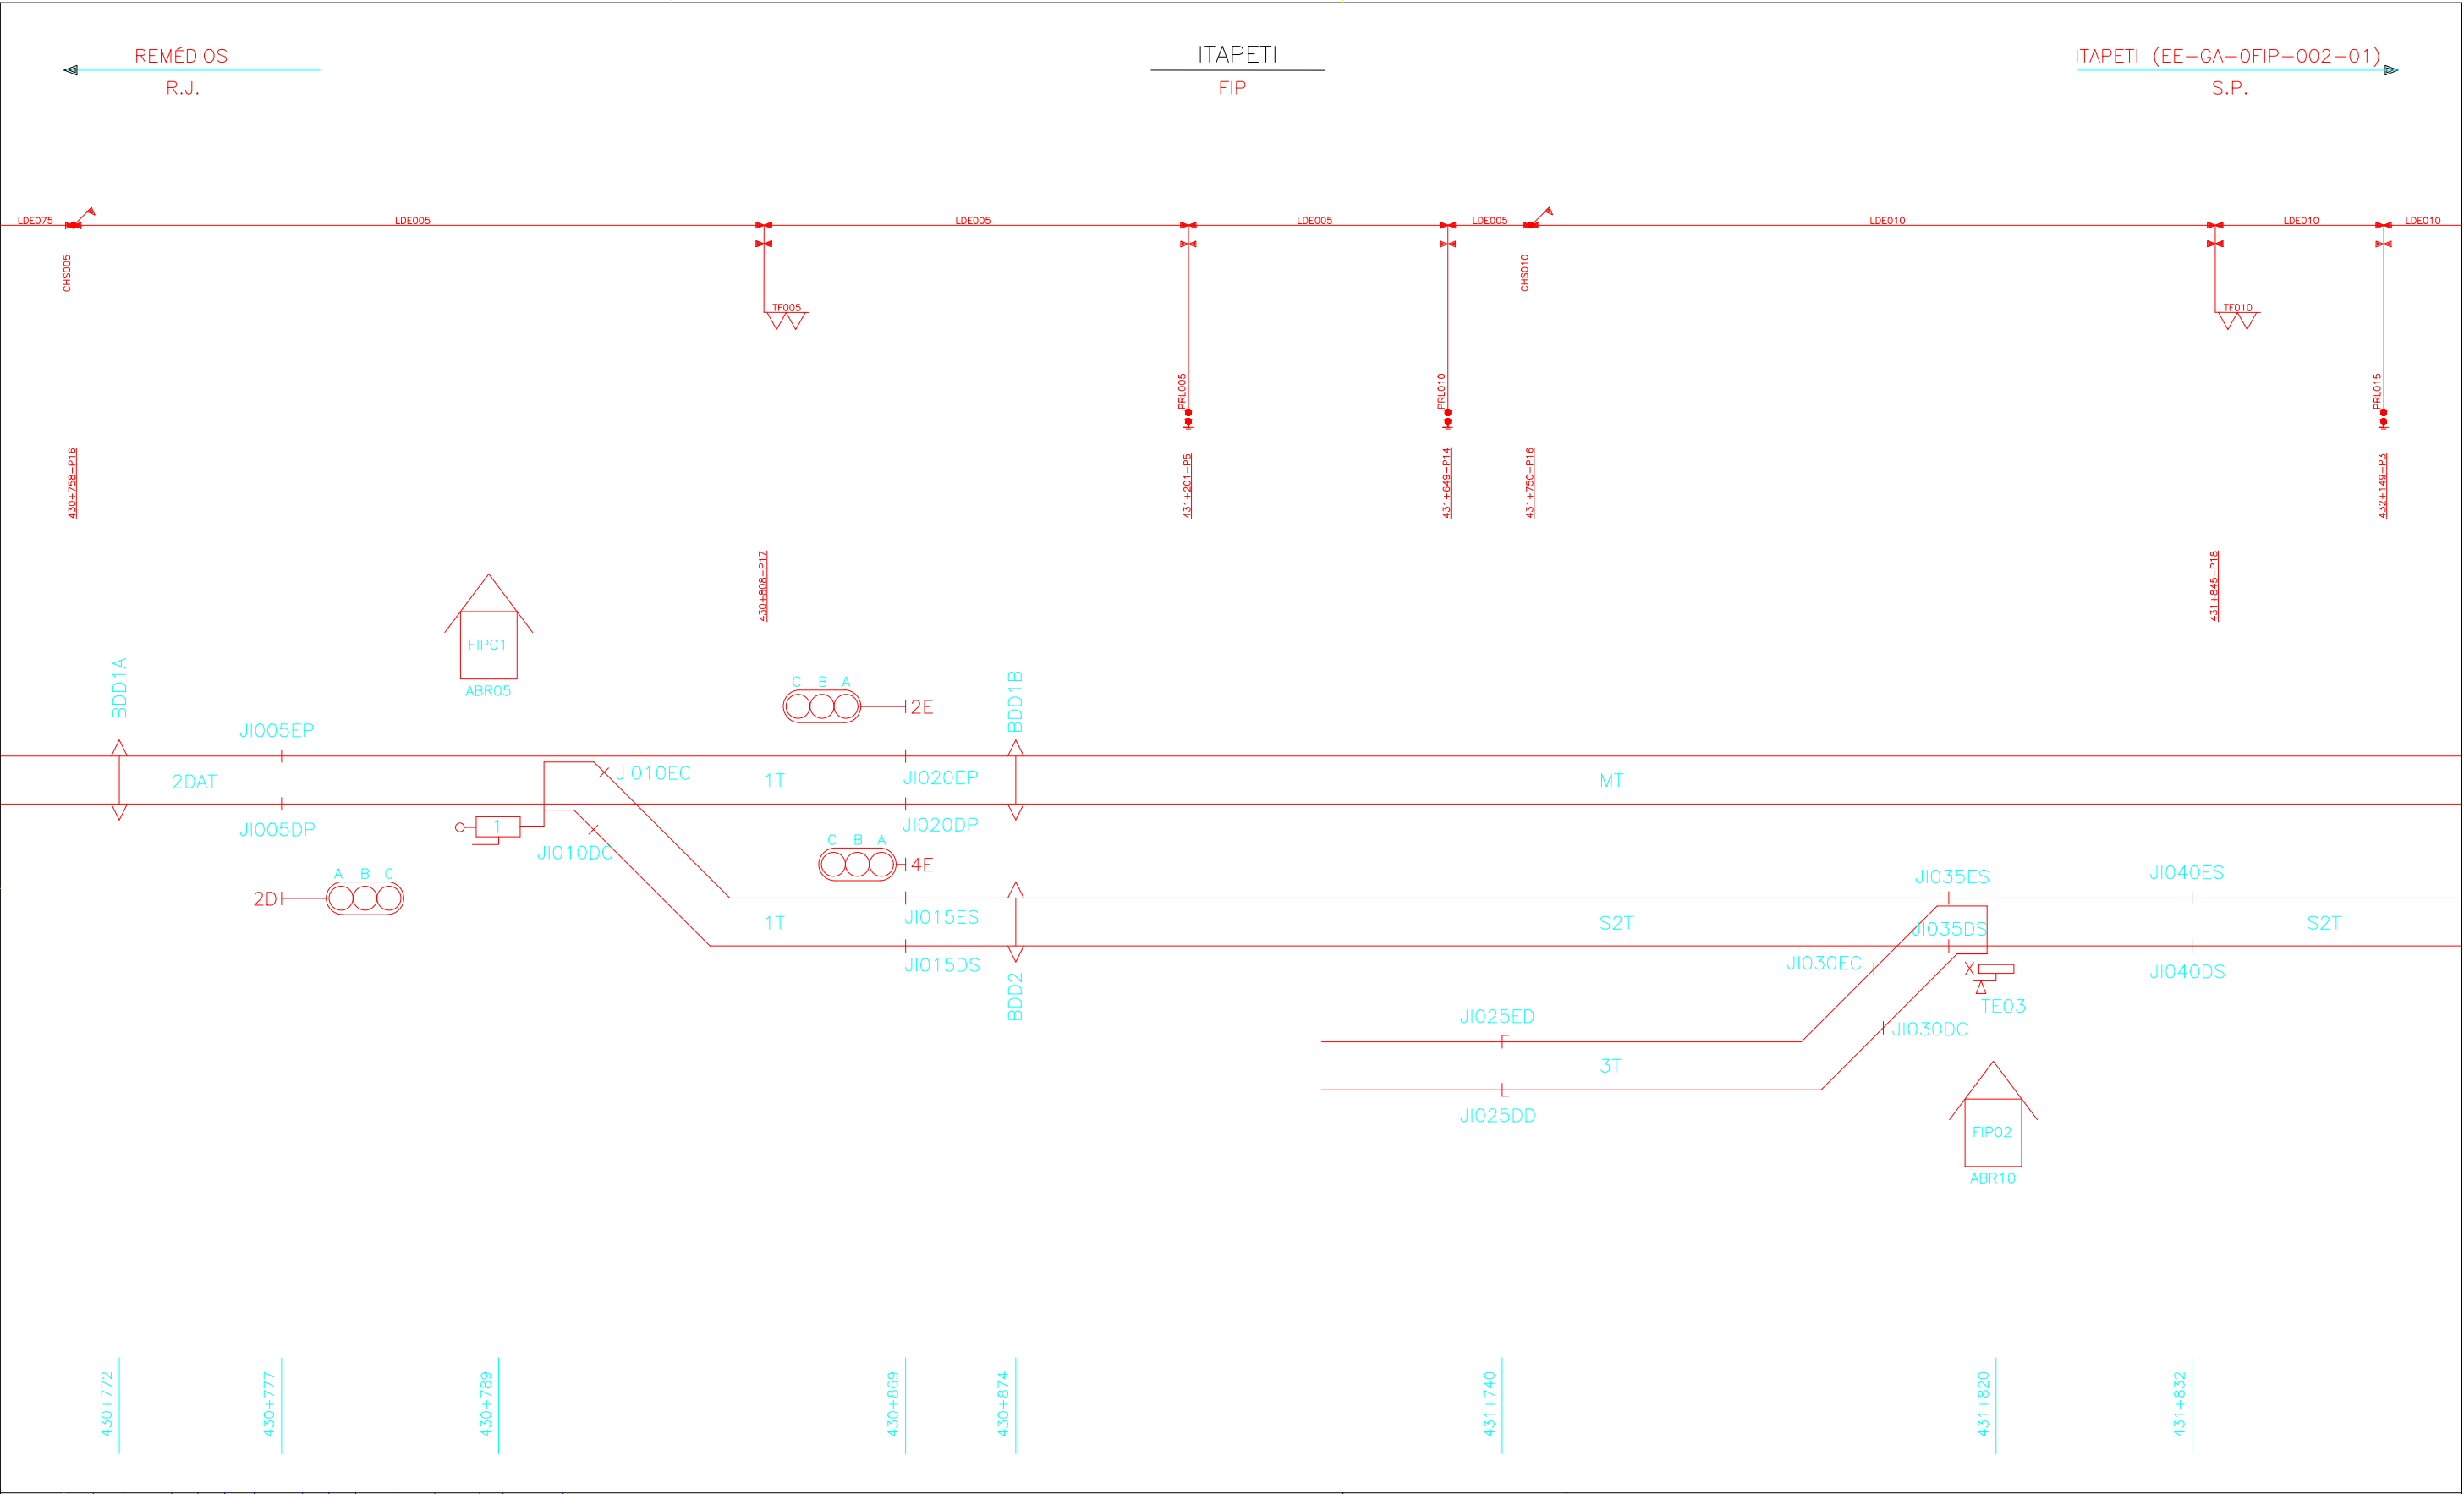

ANOTAÇÕES	ATUALIZADA EM 27/11/2002	 TÍTULO DES.: S I N G E M CADASTRO DE EQUIPAMENTOS ITAPETI – FIP	
	REV. 2 – 31/10/2006 REVISÃO DEVIDO A ENTRADA DE CHAVE DE MOLA		
	PROJ.: BEMON DES.: DEISE AGUIAR	ENG.RESP.: –	DATA: 12/09/95
	REV. 3 – 29/03/2007 REVISÃO DEVIDO A ENTRADA DE SINAL AZUL	PROJ.: –	ESCALA: – FORMATO: A3
	PROJ.: SERGIO BARBOSA DES.: GISELI	DES.PROJ.: GISELI	REV./DATA: 5 – 15/07/2025
REV. 4 – 28/05/2008 ATUALIZAÇÃO CONFORME O LEVANTA MENTO NO CAMPO EM 2007		SUBST./REF.: F0.CST2:FIP-001	
PROJ.: PCM – EDUARDO SILVA LIMA DES.: GISELI		Nº ARQUIVO MRS: EE-GA-0FIP-001-01	
REV. 5 – 15/07/2025 REVISÃO DEVIDO SINLIZAÇÃO DO PATIO, PROJETO CTC DO VALE RAFAEL BEMON – 15/07/2025			

