



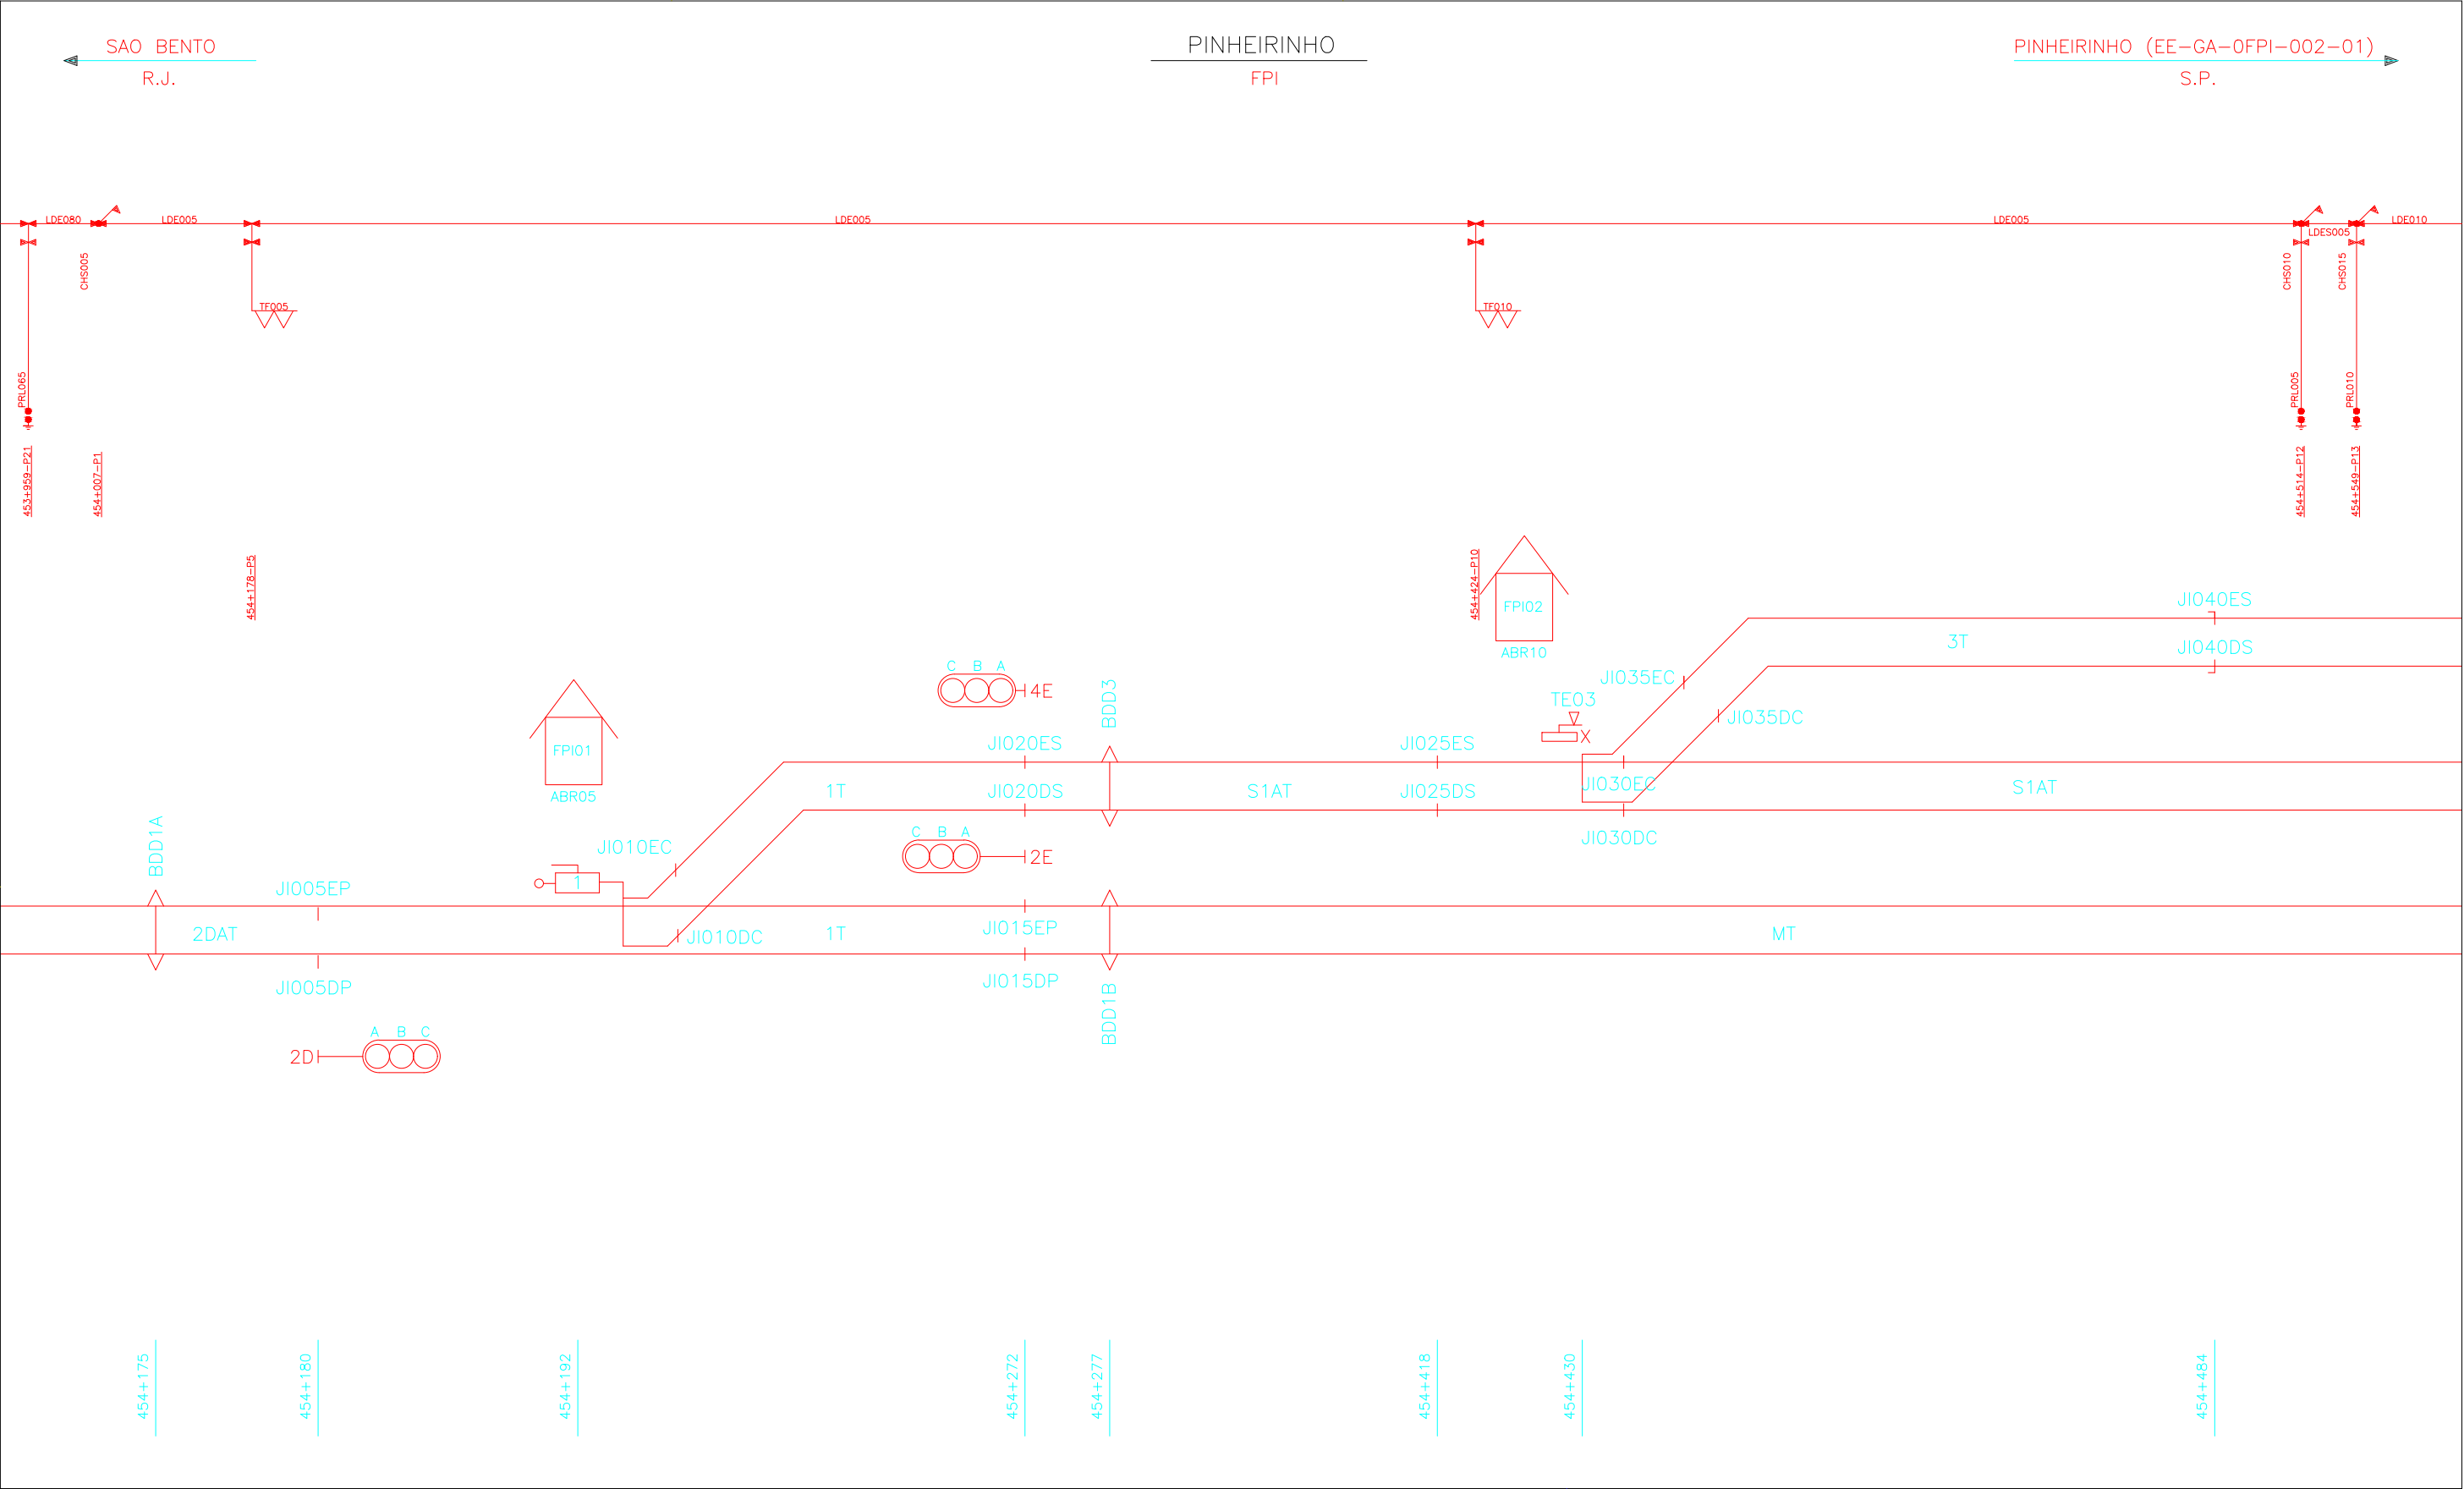

ANOTAÇÕES			
ATUALIZADA EM 27/11/2002		MRS Logística S.A. TÍTULO DES.: S I N G E M CADASTRO DE EQUIPAMENTOS PINHEIRINHO – FPI	
ATUALIZADA EM 05/04/2004			
ATUALIZADA EM 09/09/2004			
ATUALIZADA EM 29/10/2004			
REV. 5 – 29/05/2008			
ATUALIZAÇÃO CONFORME O LEVANTAMENTO NO CAMPO EM 2007		ENG.RESP.: –	
PROJ.: PCM – EDUARDO SILVA LIMA DES.: GISELI		DATA: 14/09/1995	
REV. 6 – 19/09/2014		PROJ.: –	
ALTERAÇÃO DEVIDO A ENTRADA DO DESVIO DA JULIO SINÕES POR EDILSON COELHO		DES.PROJ.: DEISE	
PROJ.: DES.: GISELI		ESCALA: –	
REV. 7 – 20/04/2018		FORMATO: A3	
REVISÃO DEVIDO ACERTO DA NUMERAÇÃO DAS CHAVES CONFORME PAI-NEL CCO		REV./DATA: 8 – 15/07/2025	
EDILSON COELHO – 19/04/2018			
PROJ.: DES.: DANIELE HELENA REVISOR.: MARCOS REINH			
REV. 8 – 15/07/2025			
REVISÃO DEVIDO SINALIZAÇÃO DO PÁTIO, PROJETO CTC DO VALE RAFAEL BEMON – 15/07/2025			
		Nº ARQUIVO MRS: FP-0A-0FPI-001-01	
		SUBST./REF.: F0.CST2:FPI-001	

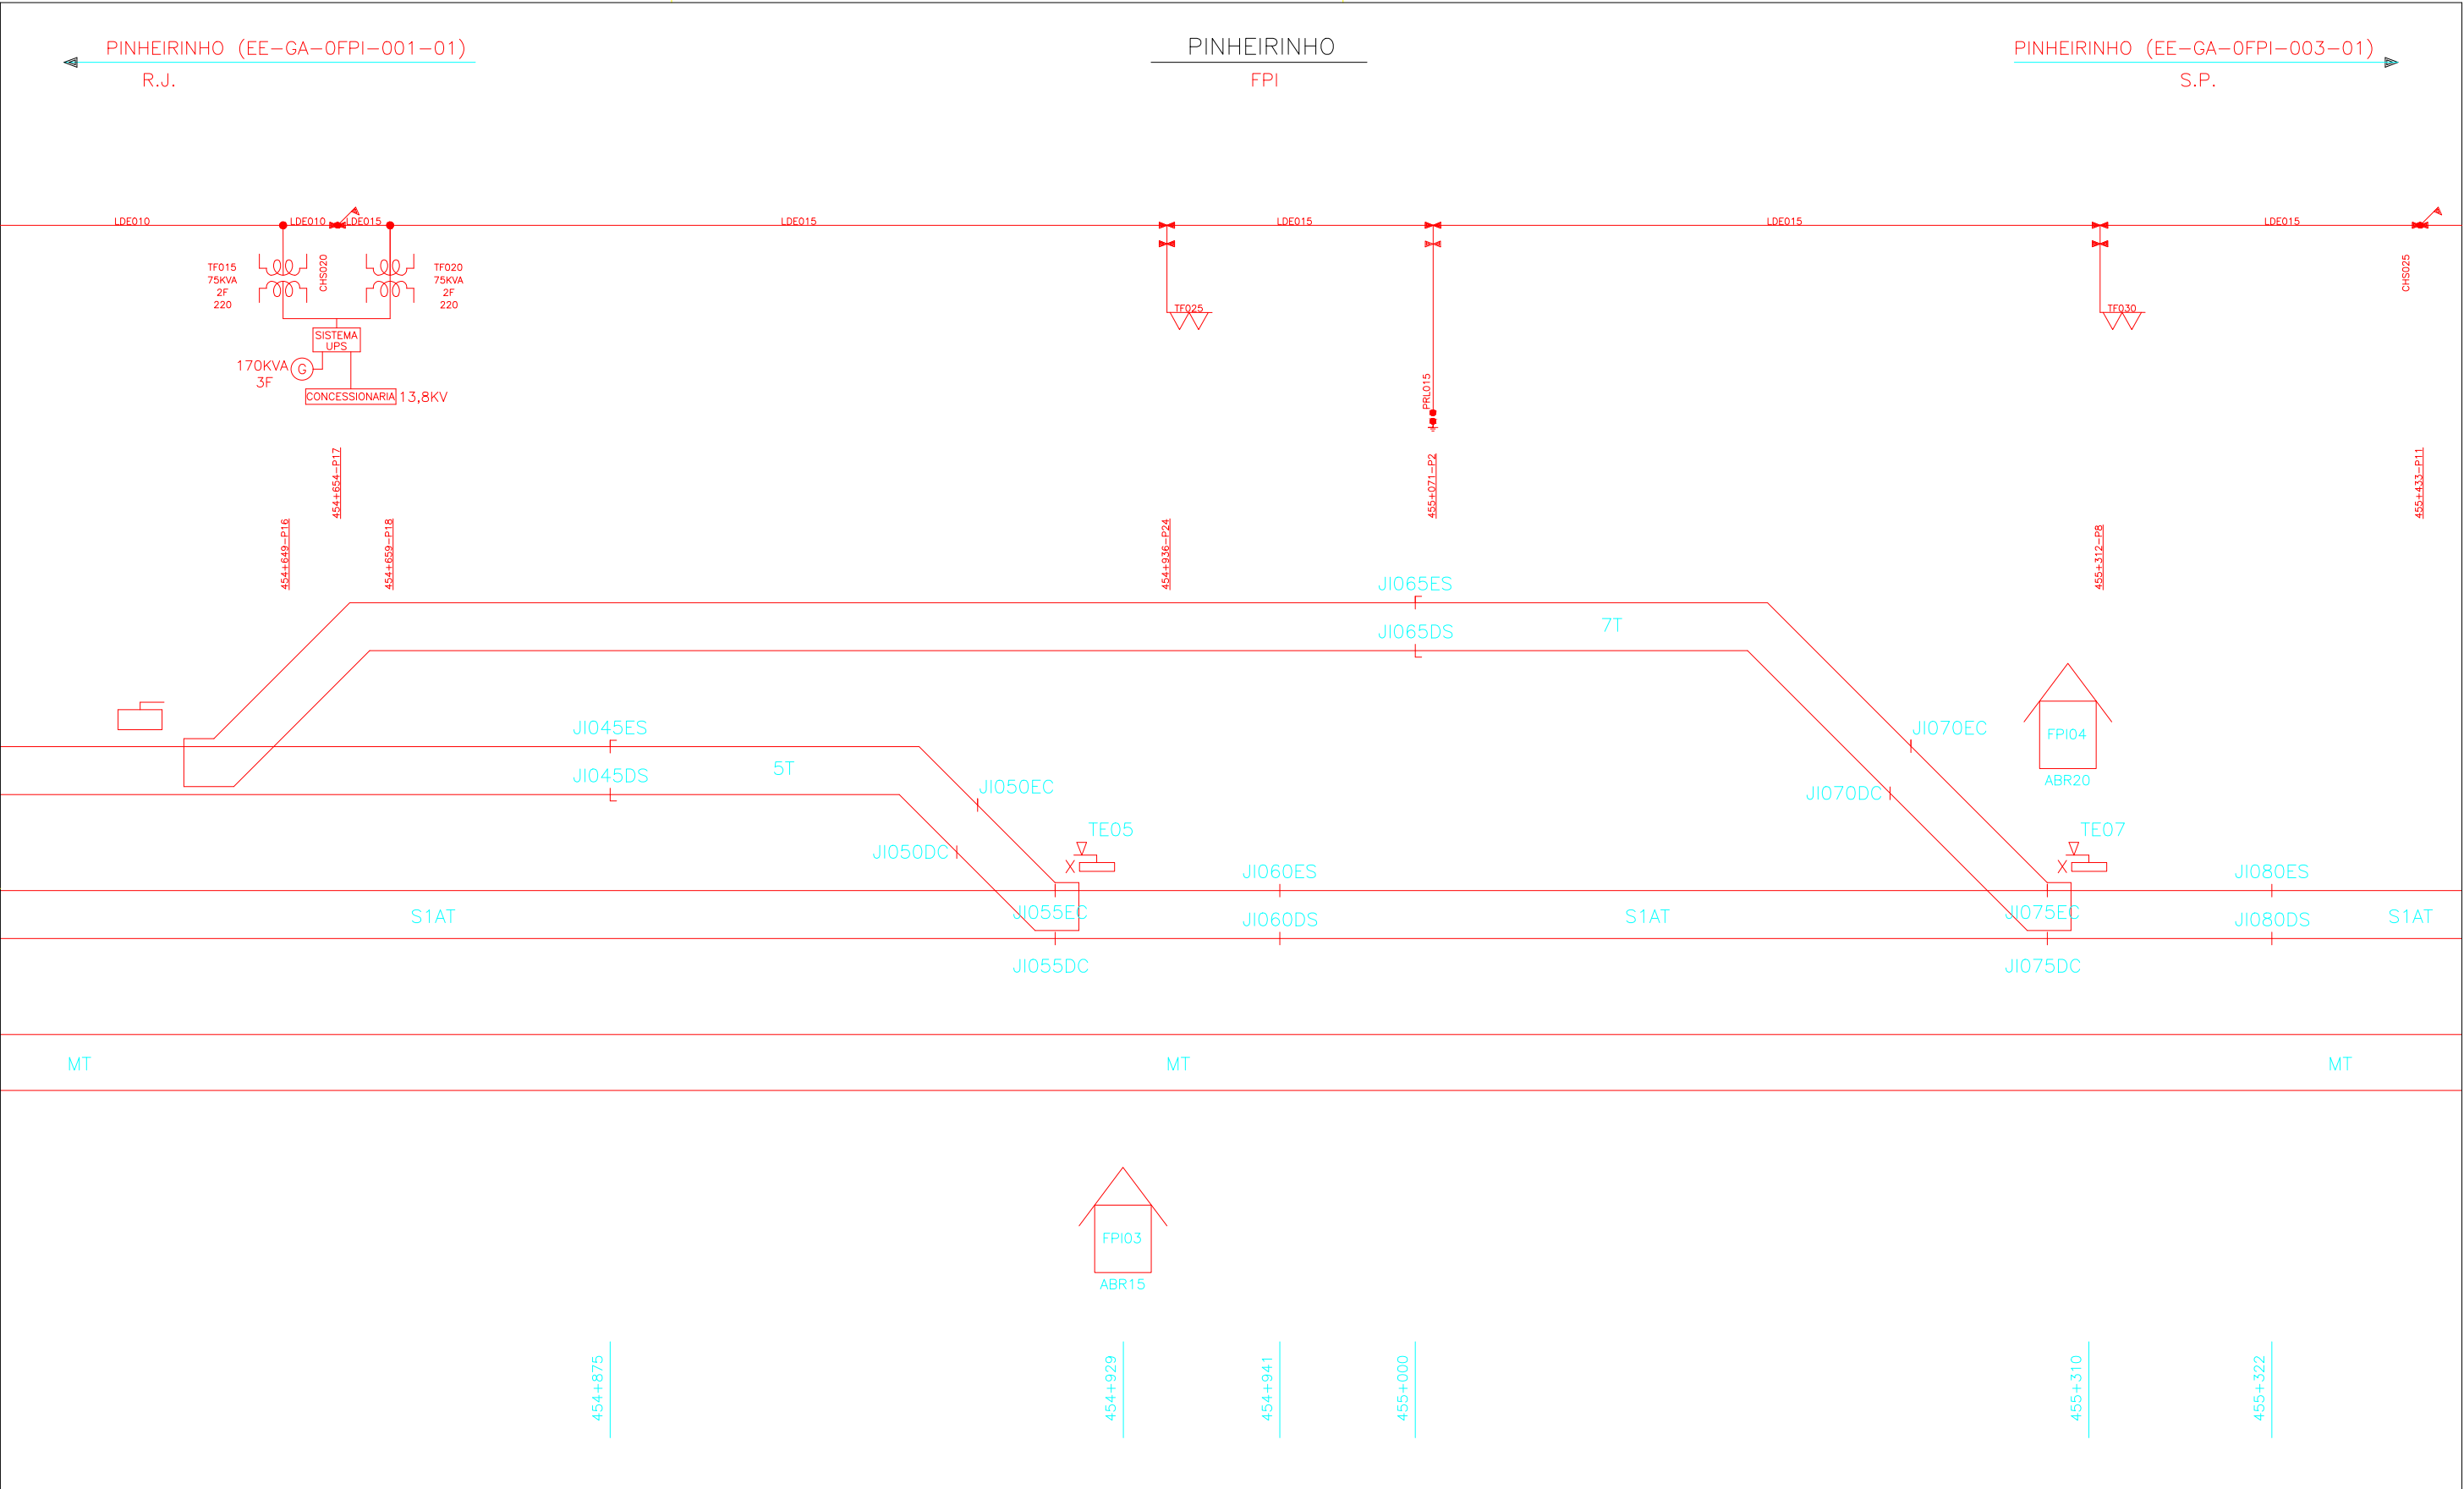

ANOTAÇÕES	
ATUALIZADA EM 27/11/2002	
ATUALIZADA EM 05/04/2004	
ALHADAS	
ATUALIZADA EM 09/09/2004	
WILLIAN	
ATUALIZADA EM 29/10/2004	
WILLIAN	
REV. 5 – 29/05/2008	
ATUALIZAÇÃO CONFORME O LEVANTA- MENTO NO CAMPO EM 2007	
PROJ.: PCM – EDUARDO SILVA LIMA DES.: GISELI	
REV. 6 – 19/09/2014	
ALTERAÇÃO DEVIDO A ENTRADA DO DESVIO DA JULIO SINÕES POR EDILSON COELHO	
PROJ.: DES.: GISELI	
REV. 7 – 20/04/2018	
REVISÃO DEVIDO ACERTO DA NOME- RAÇÃO DAS CHAVES CONFORME FAL- NEL COO.	
EDILSON COELHO – 19/04/2018	
PROJ.: DES.: DANIELE HELENA REVISOR.: MARCOS REINH	
REV. 8 – 15/07/2025	
REVISÃO DEVIDO SINALIZAÇÃO DO PÁTIO, PROJETO CTC DO VALE	
RAFAEL BEMON – 15/07/2025	

MRS Logística S.A. FIRMA CONTRATADA: - Nº ARQUIVO MRS: EE-GA-OFPI-002-01	TÍTULO DES.: S I N G E M CADASTRO DE EQUIPAMENTOS PINHEIRINHO – FPI	
	ENG.RESP.: –	DATA: 14/09/1995
	PROJ.: –	ESCALA: – FORMATO: A3
	DES.PROJ.: DEISE	REV./DATA: 8 – 15/07/2025
SUBST./REF.: F0.CST2:FPI-001		

