


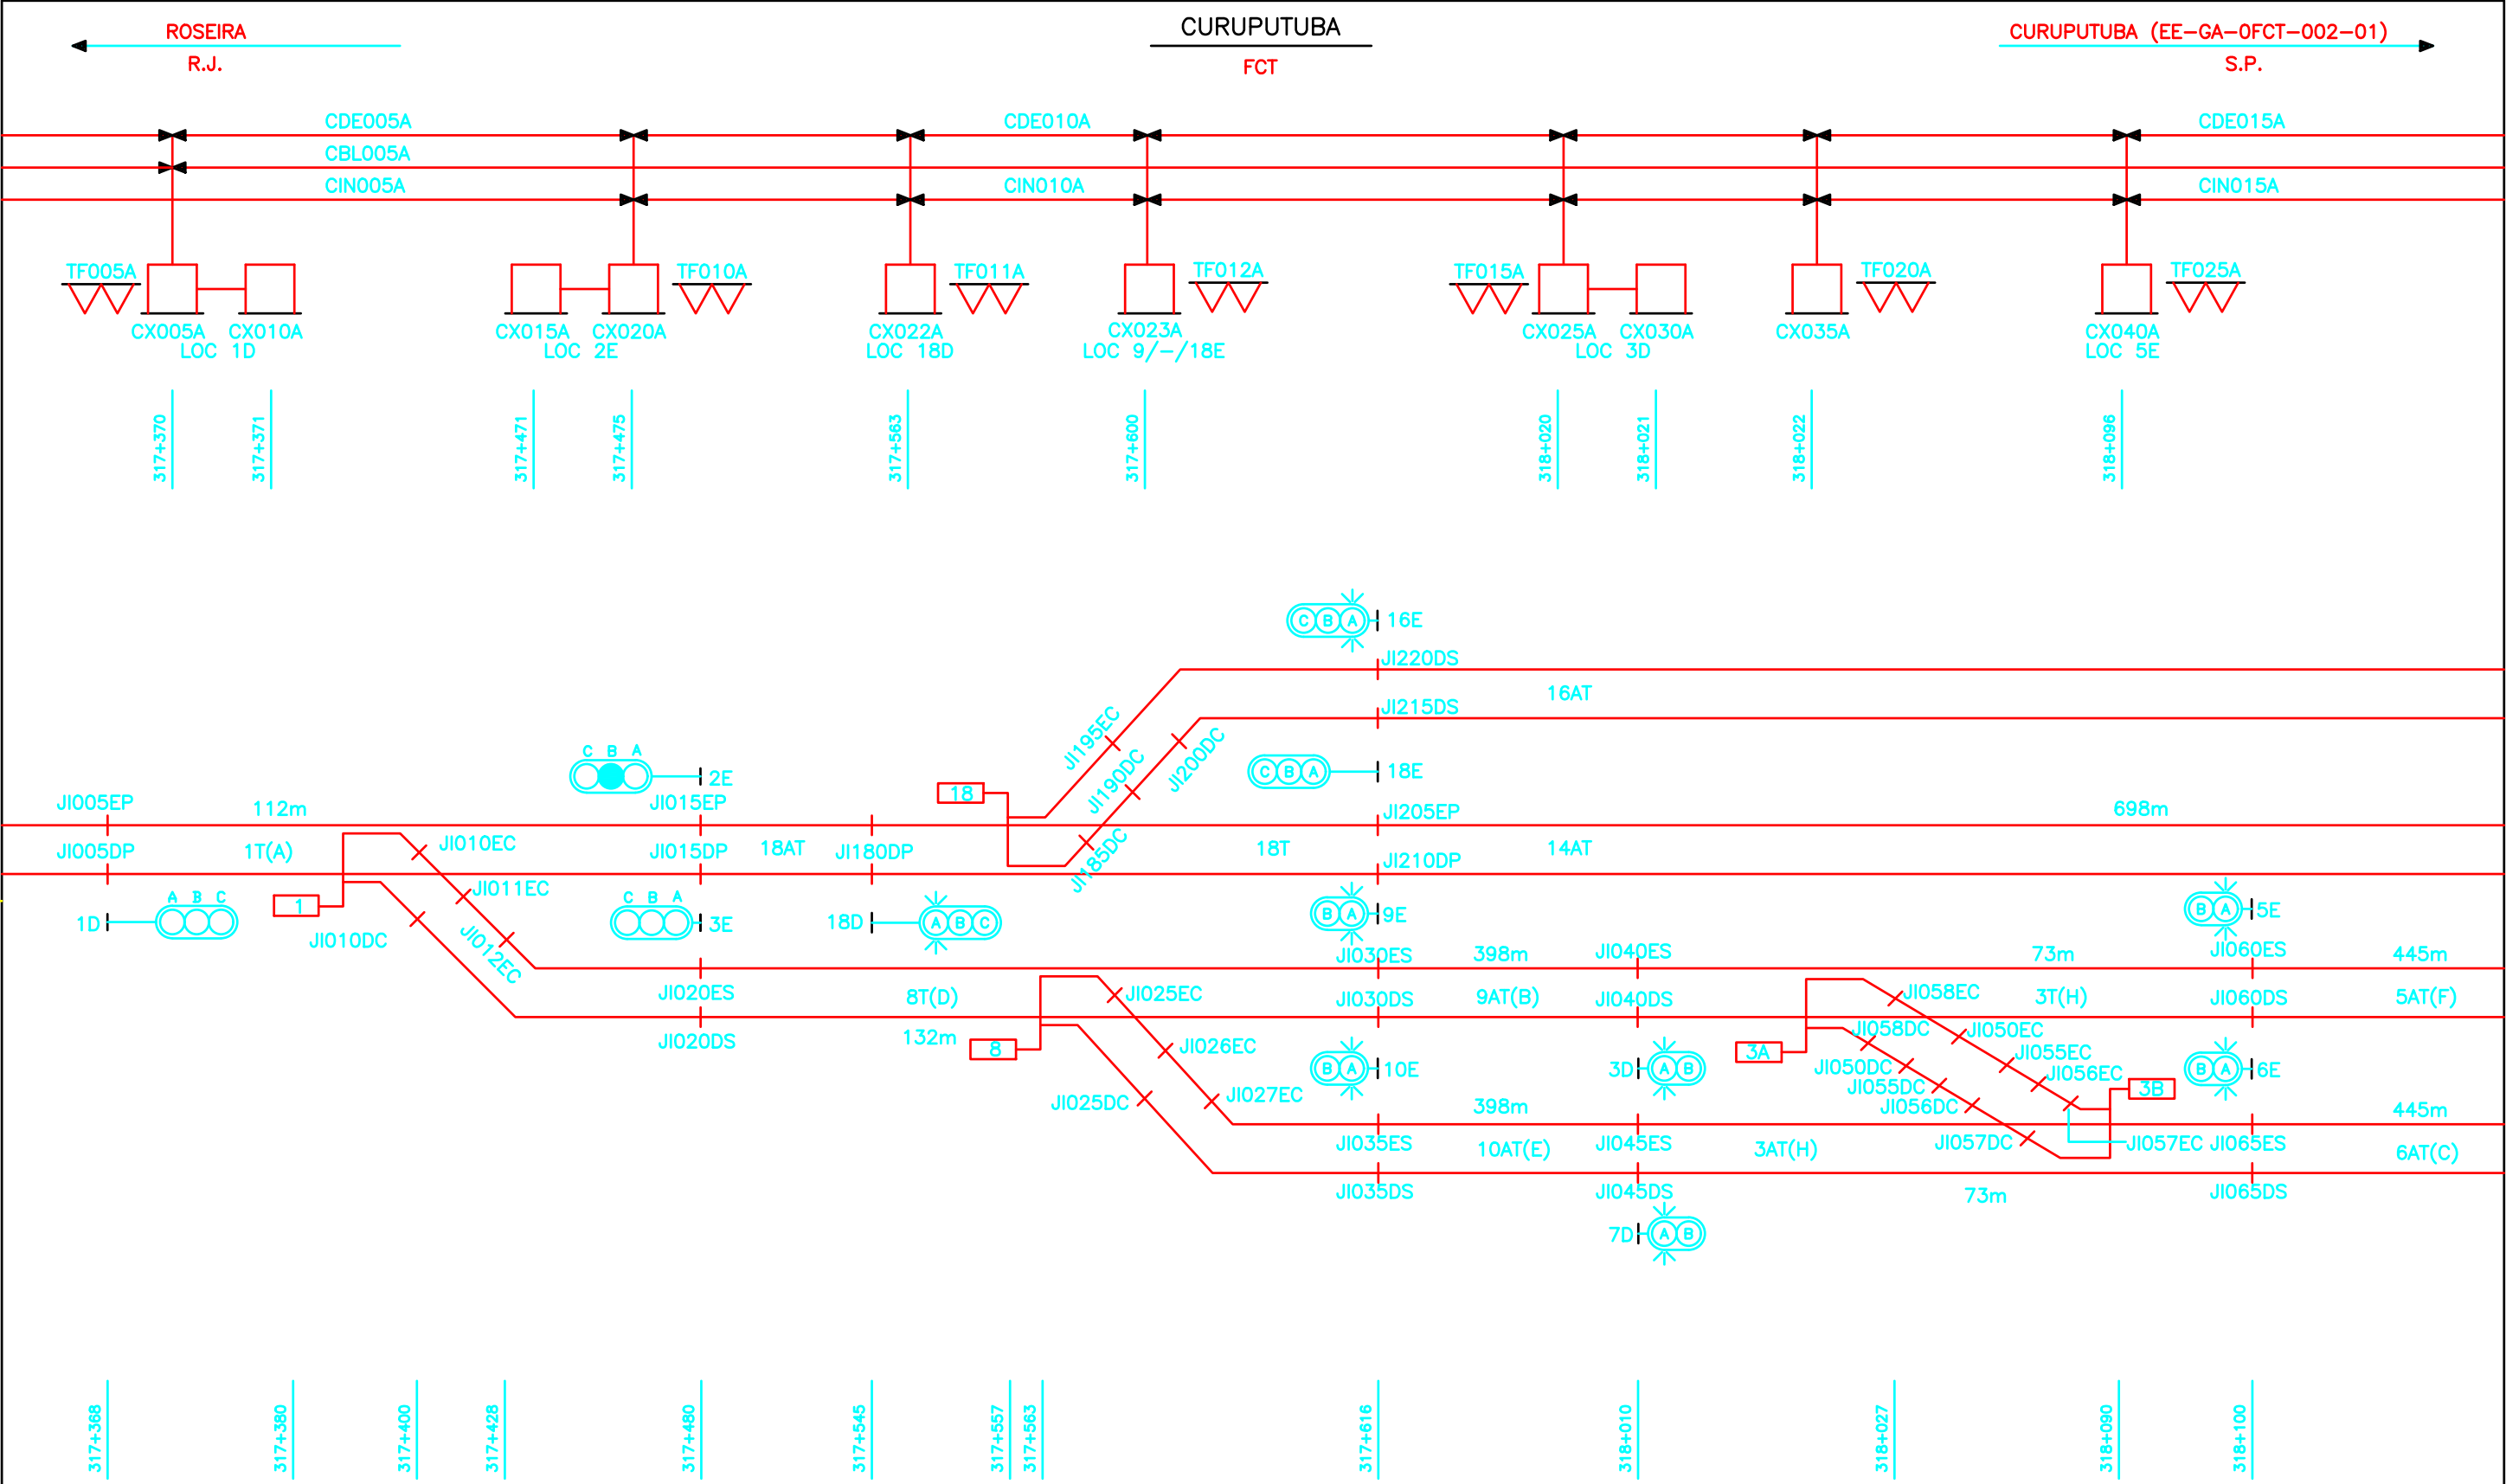

ANOTAÇÕES	ATUALIZADA EM 20/11/2002	MRS Logística S.A. FIRMA CONTRATADA: TÍTULO DES.: S I N G E M CADASTRO DE EQUIPAMENTOS CURUPUTUBA – FCT	
	REV. 2 – 18/11/2006		
	ATUALIZADA POR WILLIAM		
	PROJ.: DEISE AGUIAR		
	REV. 4 – 19/06/2007		
REVISADA POR EDILSON COELHO MOTIVO: CIRCUITO DE VIA EM SERIE	PROJ.: DEISE AGUIAR	DATA: 27/11/2023	
	REV. 5 – 26/05/2008	ESCALA: –	
	ATUALIZAÇÃO CONFORME O LEVANTA- MENTO NO CAMPO EM 2007	FORMATO: A3	
	PROJ.: PCM – EDUARDO SILVA LIMA DES.: GISELI	REV./DATA: 9 – 27/11/2023	
	REV. 6 – 20/06/2012	SUBST./REF.: FO.CST2:FCT-001	
REVISÃO DEVIDO A ADEQUAÇÃO DO PÁTIO DE CORUPUTUBA	PROJ.: MRS2015		
	DES.: GISELI		
	REV. 7 – 06/08/2012		
	MODIFICAÇÃO DEVIDO OBRA DO PÁTIO DE CORUPUTUBA		
	PROJ.: MRS2015		
REVISÃO DEVIDO ADEQUAÇÃO DO PÁTIO DE CORUPUTUBA	DES.: GISELI		
	REV. 8 – 04/02/2013		
	REVISÃO DEVIDO ADEQUAÇÃO DO PÁTIO DE CORUPUTUBA		
	PROJ.: MRS2015		
	DES.: GISELI		
ATUALIZAÇÃO DEVIDO AS BUILT RE- FERENTE AO PROJETO TERMINAL NOVELIS. POR GEPEE.	REV. 9 – 27/11/2023		
	PROJ.: RACHEL SCHETTINO REVISOR.: MARCOS REINH		
N° ARQUIVO MRS: EE-GA-0FCT-001-01			

