


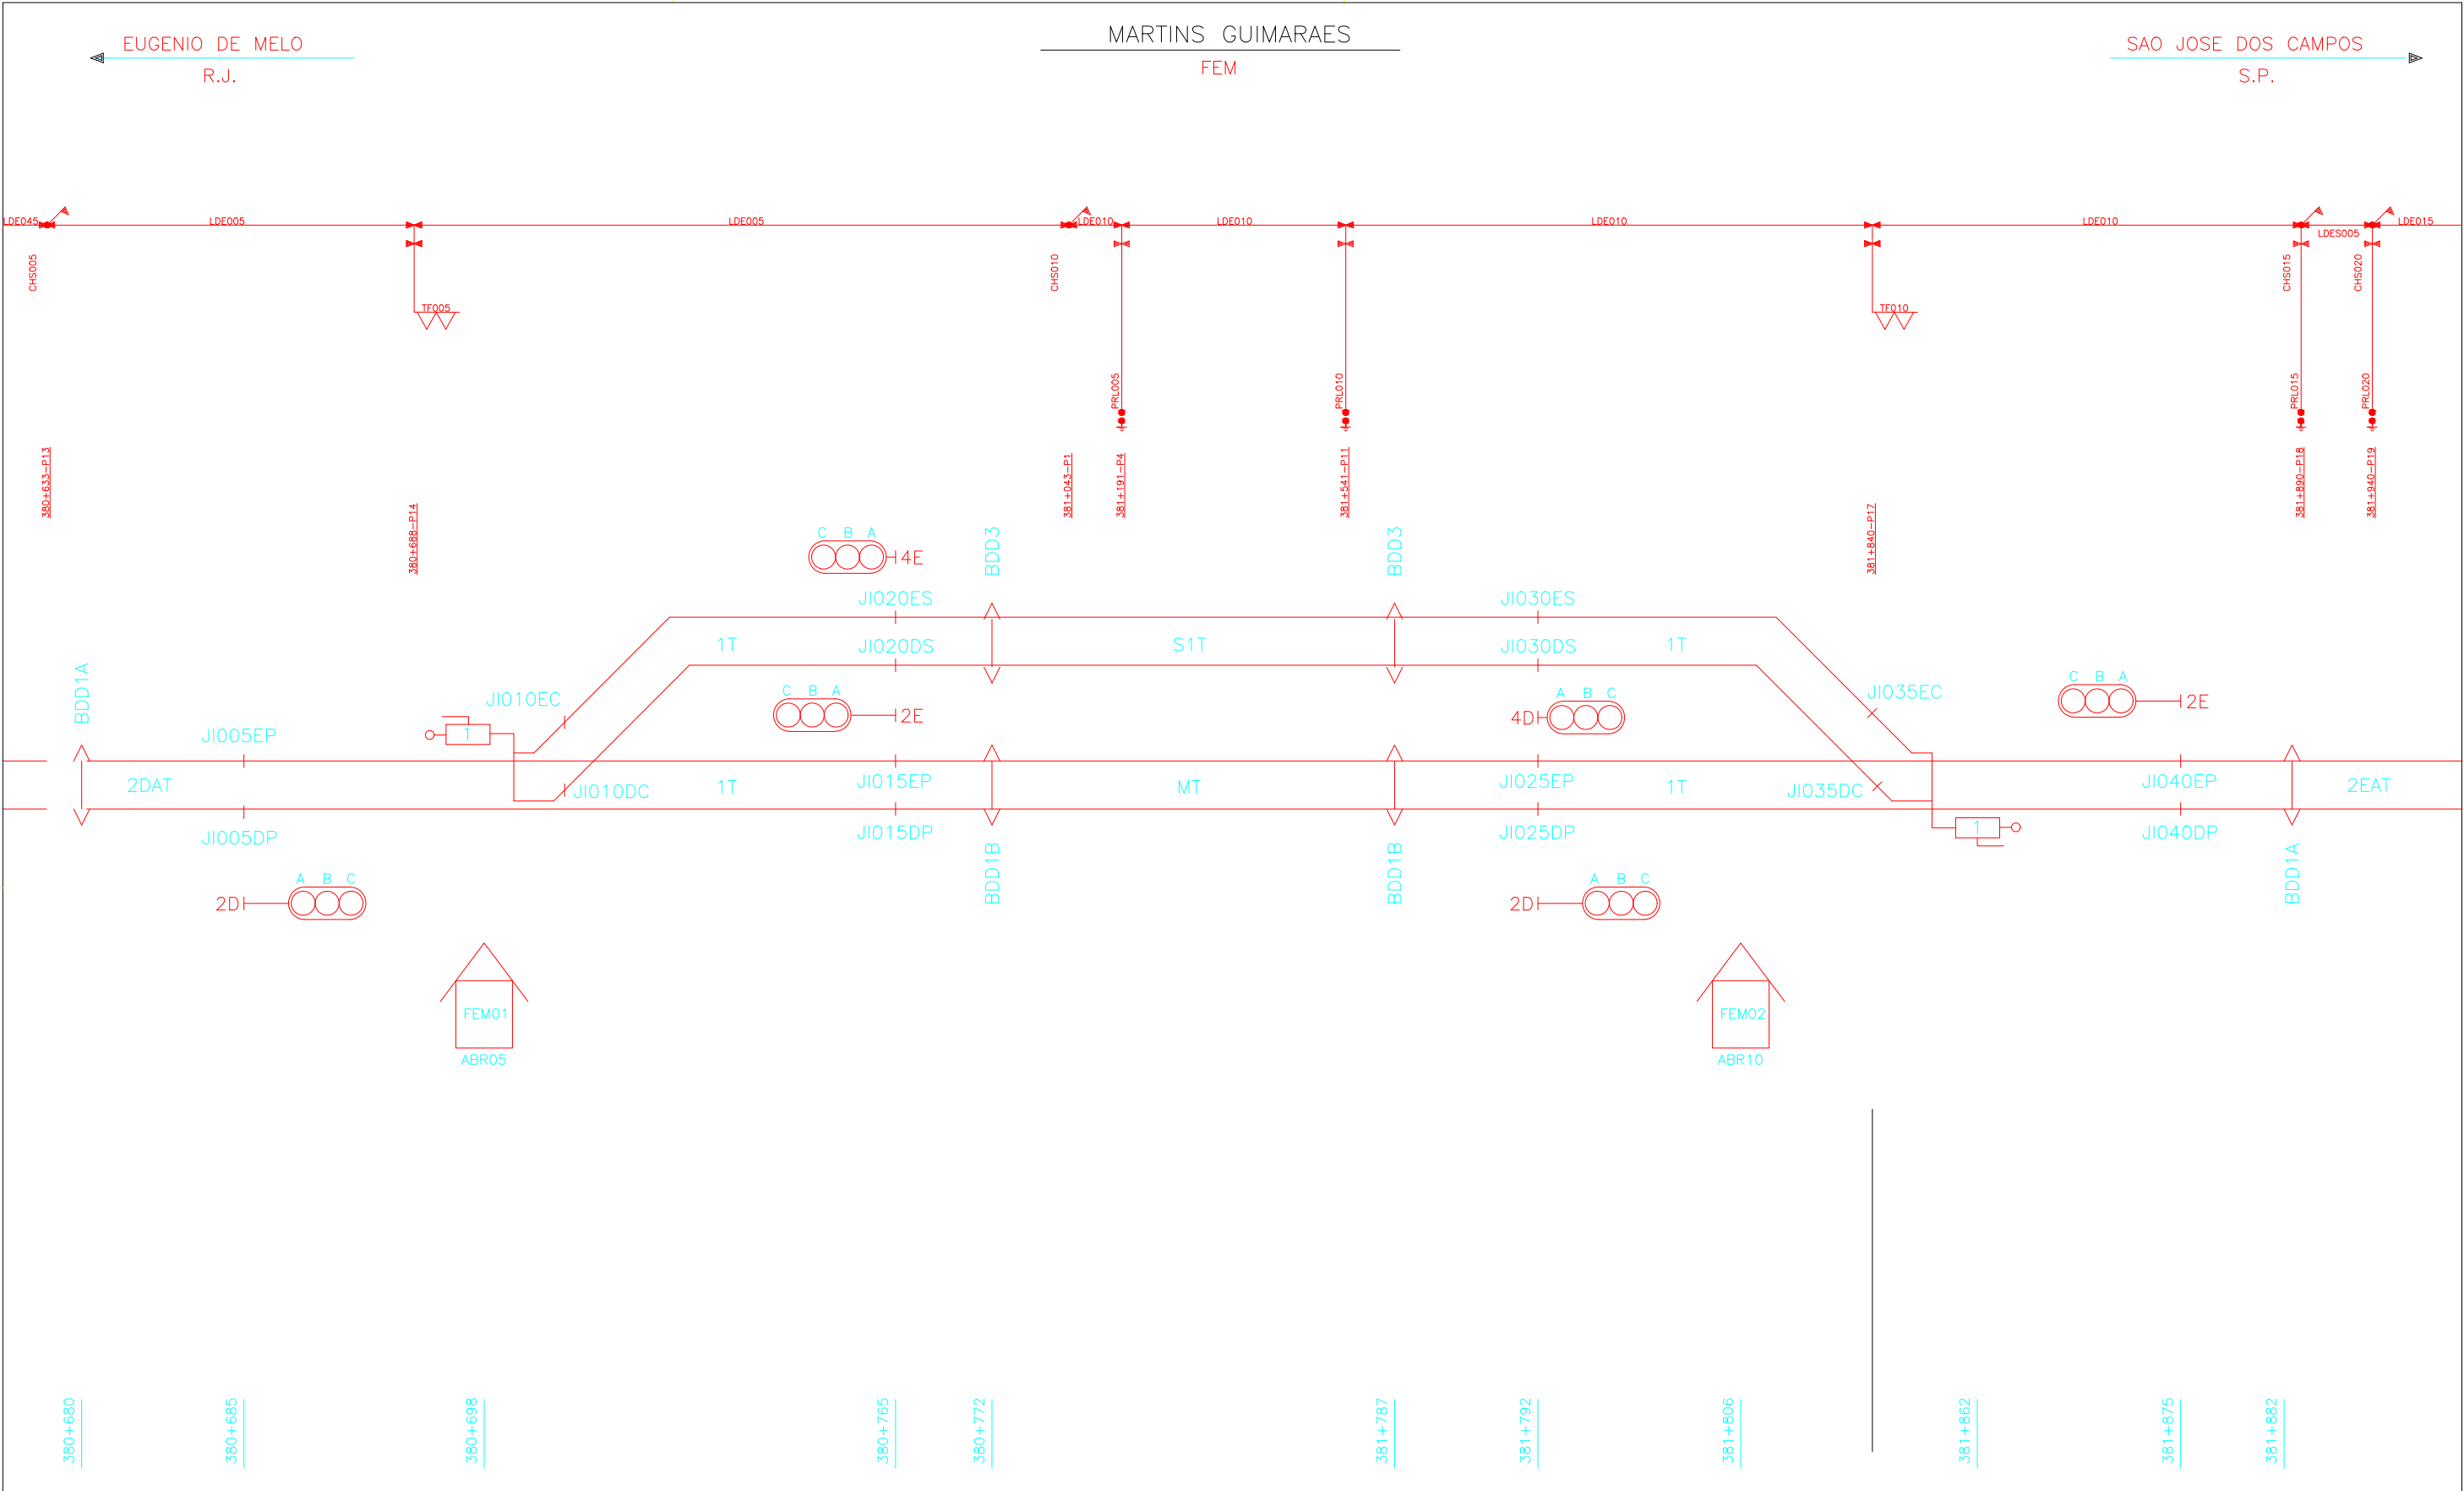

|   |   |                                          |                                                                                        |                              |
|---|---|------------------------------------------|----------------------------------------------------------------------------------------|------------------------------|
| ANOTAÇÕES   | ATUALIZADA EM 27/11/2002                                                                                                | <div>MRS</div> <div>Logística S.A.</div> | TÍTULO DES.:<br><br>S I N G E M<br>CADASTRO DE EQUIPAMENTOS<br>MARTINS GUIMARÃES – FEM |                              |
|   | REV. 2 – 28/05/2008   |                                          |                                                                                        |                              |
|   | ATUALIZAÇÃO CONFORME O LEVANTAMENTO NO CAMPO EM 2007<br>PROJ.: PCM – EDUARDO SILVA LIMA<br>DES.: GISELI                 | FIRMA CONTRATADA:                        | ENG.RESP.: –                                                                           | DATA: 16/06/1995             |
|   | REV. 3 – 20/04/2012<br>ATUALIZADA COFORME O CAMPO POR EDILSON COELHO<br>PROJ.:<br>DES.: GISELI                          | –                                        | PROJ.: –                                                                               | ESCALA: –      FORMATO: A3   |
|   | REV. 4 – 07/01/2013<br>ATUALIZADA COFORME O CAMPO (INSTALAÇÃO CHAVE DE MOLLA) POR SISTEN ENG*<br>PROJ.:<br>DES.: GISELI | Nº ARQUIVO MRS:                          | DES.PROJ.: SANDRA                                                                      | REV./DATA: 5 – 15/07/2025    |
| REV. 5 – 15/07/2025<br>REVISÃO DEVIDO SINALIZAÇÃO DO PÁTIO, PROJETO CTC DO VALE<br>RAFAEL BEVON – 15/07/2025 |   | EE-CA-OFEM-001-01                        |                                                                                        | SUBST./REF.: FO.CST2:FEM-001 |

