PINDAMONHANGABA (EE-GA-0FPG-003-01)
R.J.

ENG. LUIS RENATO
FLT

PINDAMONHANGABA (EE-GA-0FPH-002-01)
S.P.

LDE050 LDES005 LDE005 LDE005 LDE005 LDE010 LDE010 LDE010 LDES010 LDE015

CHS005 CHS010 TE005 CHS015 CHS020 CHS025

PRL005 PRL010 PRL015 PRL020 PRL025 PRL030 PRL035

X331+168=P4 X331+212=P5 X331+257=P6 X331+472=P11 X331+735=P18 X332+130=P3 X332+586=P12 X332+772=P18 X333+024=P1

CDE040B CDE045B CDE050B CDE055B CDE060B CDE065B CDE070B

4E C B A

JI015ES

BDD2A

1T JI015DS S1T

VIADUTO

BDD1A

JI005EP

1 JI01QEC JI01QDC

JI020EP

2DAT JI005DP 1T 1T JI020DP MT

2D A B C A B C

C B A

2E

BDD1B

FLT01
ABR05

324+969 331+183 331+188 331+200 331+265 331+270

ANOTAÇÕES

ATUALIZADA EM 20/11/2002
ATUALIZADA EM 30/11/2005
DES. GISELI
REV. 3 - 19/06/2007
REVISADA POR EDILSON COELHO
MOTIVO: CIRCUITO DE VIA EM SERIE
PROJ.:
DES.: DEISE AGUIAR
REV. 4 - 26/05/2008
ATUALIZAÇÃO CONFORME O LEVANTA
MENTO NO CAMPO EM 2007
PROJ.: PCM - EDUARDO SILVA LIMA
DES.: GISELI
REV. 5 - 16/01/2013
ATUALIZAÇÃO CONFORME O CAMPO
POR: EDILSON COELHO
PROJ.:
DES.: GISELI
REV. 6 - 22/08/2025
REVISÃO DEVIDO SINALIZAÇÃO DO
PÁTIO, PROJETO CTC DO VALE
RAFAEL BEMON - 22/08/2025

MRS Logística S.A.

FIRMA CONTRATADA: -


TÍTULO DES.:
S I N G E M
CADASTRO DE EQUIPAMENTOS
ENG. LUIS RENATO - FLT


ENG.RESP.:	-	DATA:	04/07/94
PROJ.:	-	ESCALA: -	FORMATO:
DES.PROJ.:	GISELI	REV./DATA:	22/08/2025
Nº ARQUIVO MRS:	EE-GA-0FLT-001-01	SUBST./REF.:	F0.CST2:FPG-001

CURUPUTUBA
R.J.

ENG. LUIS RENATO
FLT

TAUBATÉ
S.P.

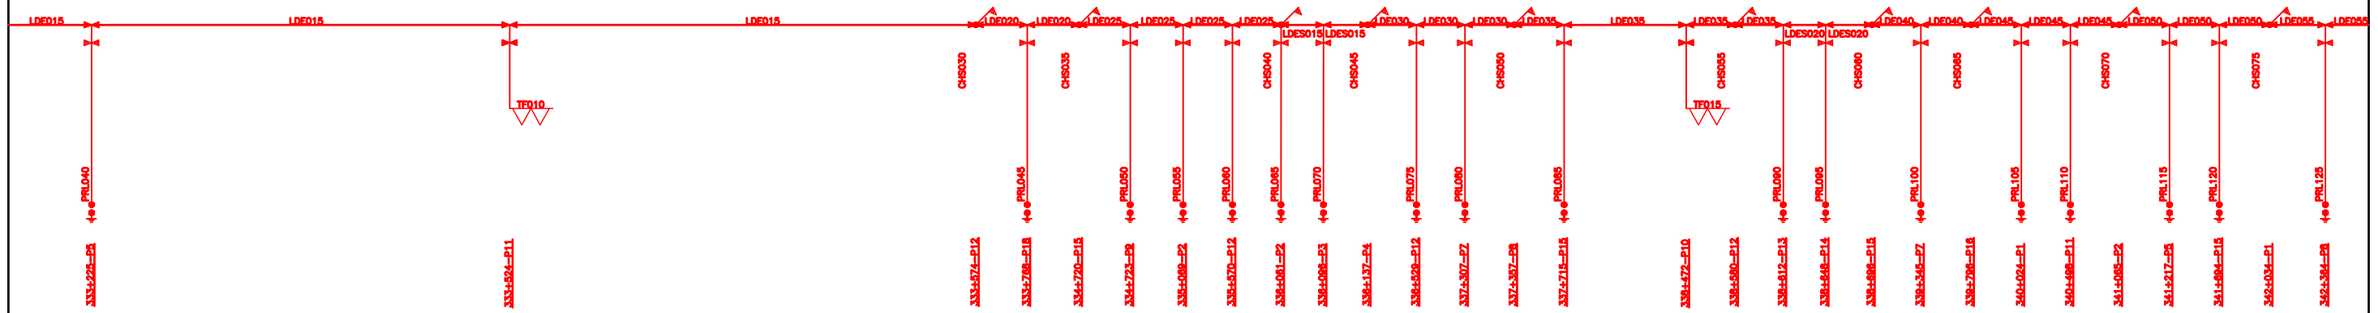

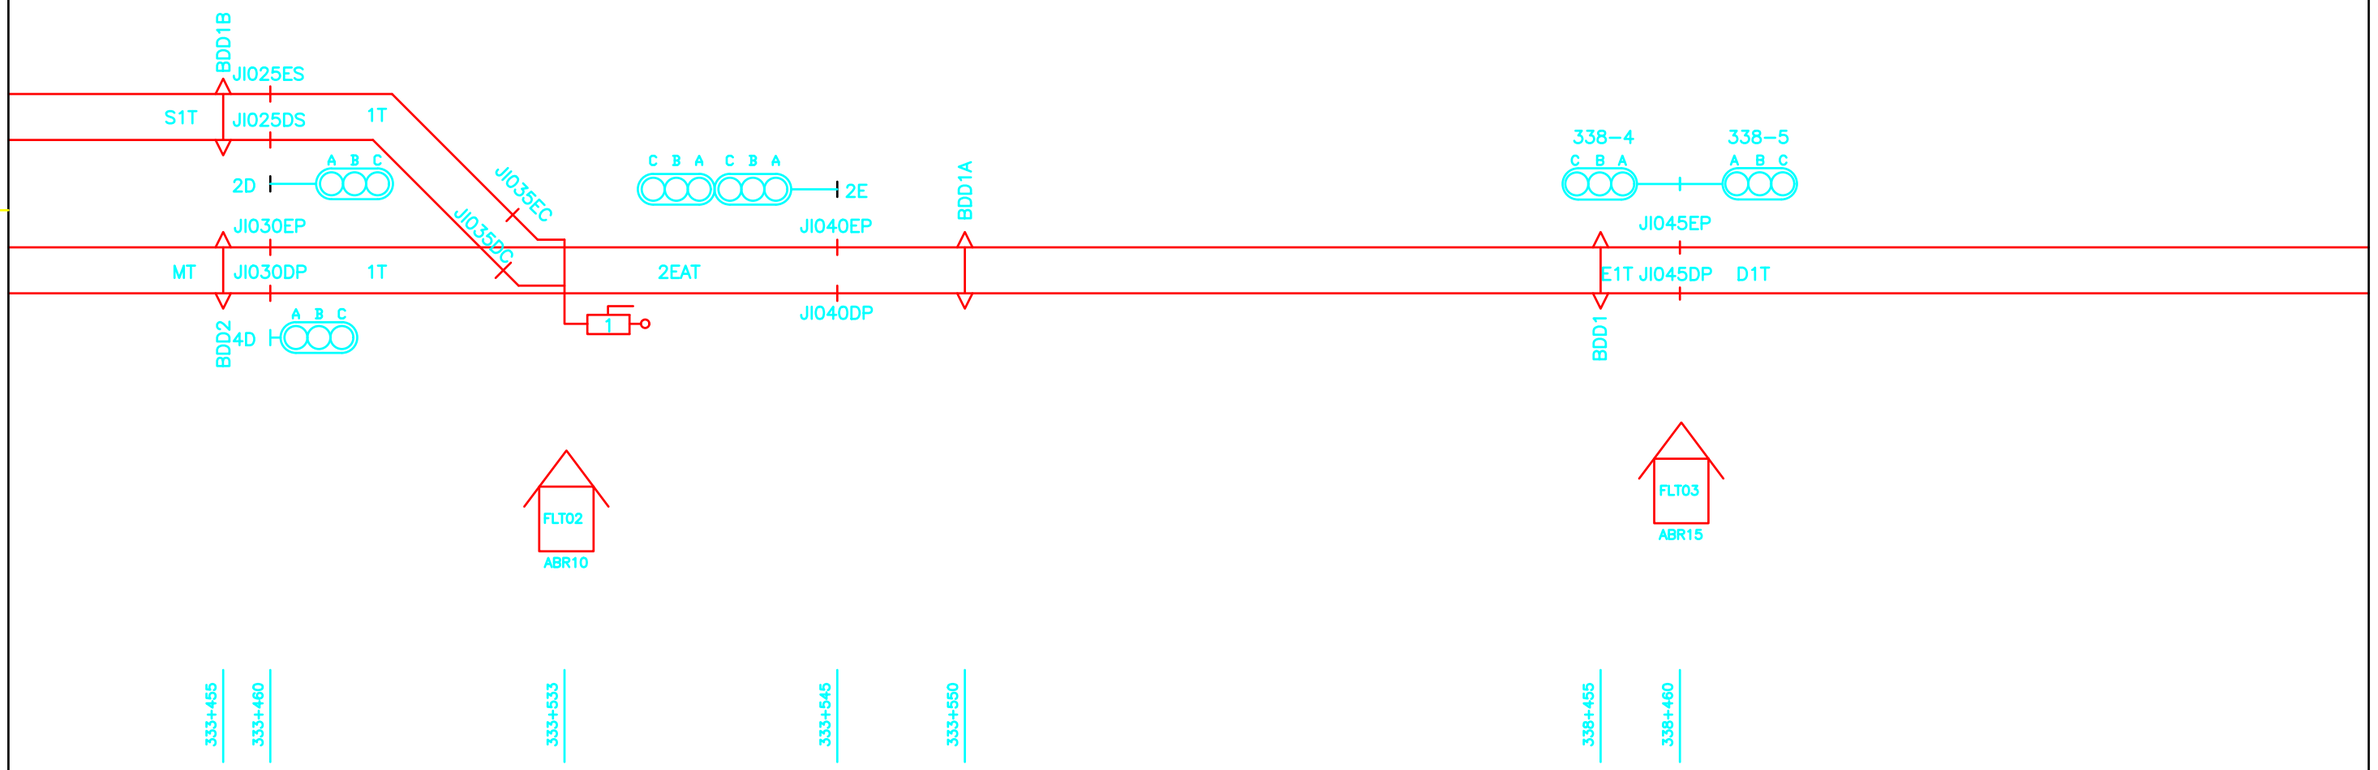

ANOTAÇÕES

ATUALIZADA EM 20/11/2002		
ATUALIZADA EM 30/11/2005	DES. GISELI	
REV. 3 – 19/06/2007		
REVISADA POR EDILSON COELHO	MOTIVO: CIRCUITO DE VIA EM SÉRIE	
PROJ.:	DES.: DEISE AGUIAR	
REV. 4 – 26/05/2008		
ATUALIZAÇÃO CONFORME O LEVANTA	MENTO NO CAMPO EM 2007	
PROJ.: PCM – EDUARDO SILVA LIMA	DES.: GISELI	
REV. 5 – 16/01/2013		
ATUALIZAÇÃO CONFORME O CAMPO	POR: EDILSON COELHO	
PROJ.:	DES.: GISELI	
REV. 6 – 22/08/2025		
REVISÃO DEVIDO SINALIZAÇÃO DO	PÁTIO, PROJETO CTC DO VALE	
RAFAEL BEMON – 22/08/2025		

MRS Logística S.A.

TÍTULO DES.:

S I N G E M
CADASTRO DE EQUIPAMENTOS
ENG. LUIS RENATO – FLT

FIRMA CONTRATADA: –

ENG.RESP.:	–	DATA:	04/07/94
PROJ.:	–	ESCALA: –	FORMATO:
DES.PROJ.:	GISELI	REV./DATA:	22/08/2025
Nº ARQUIVO MRS:	EE–GA–0FLT–002–01	SUBST./REF.:	F0.CST2:FPG–001