



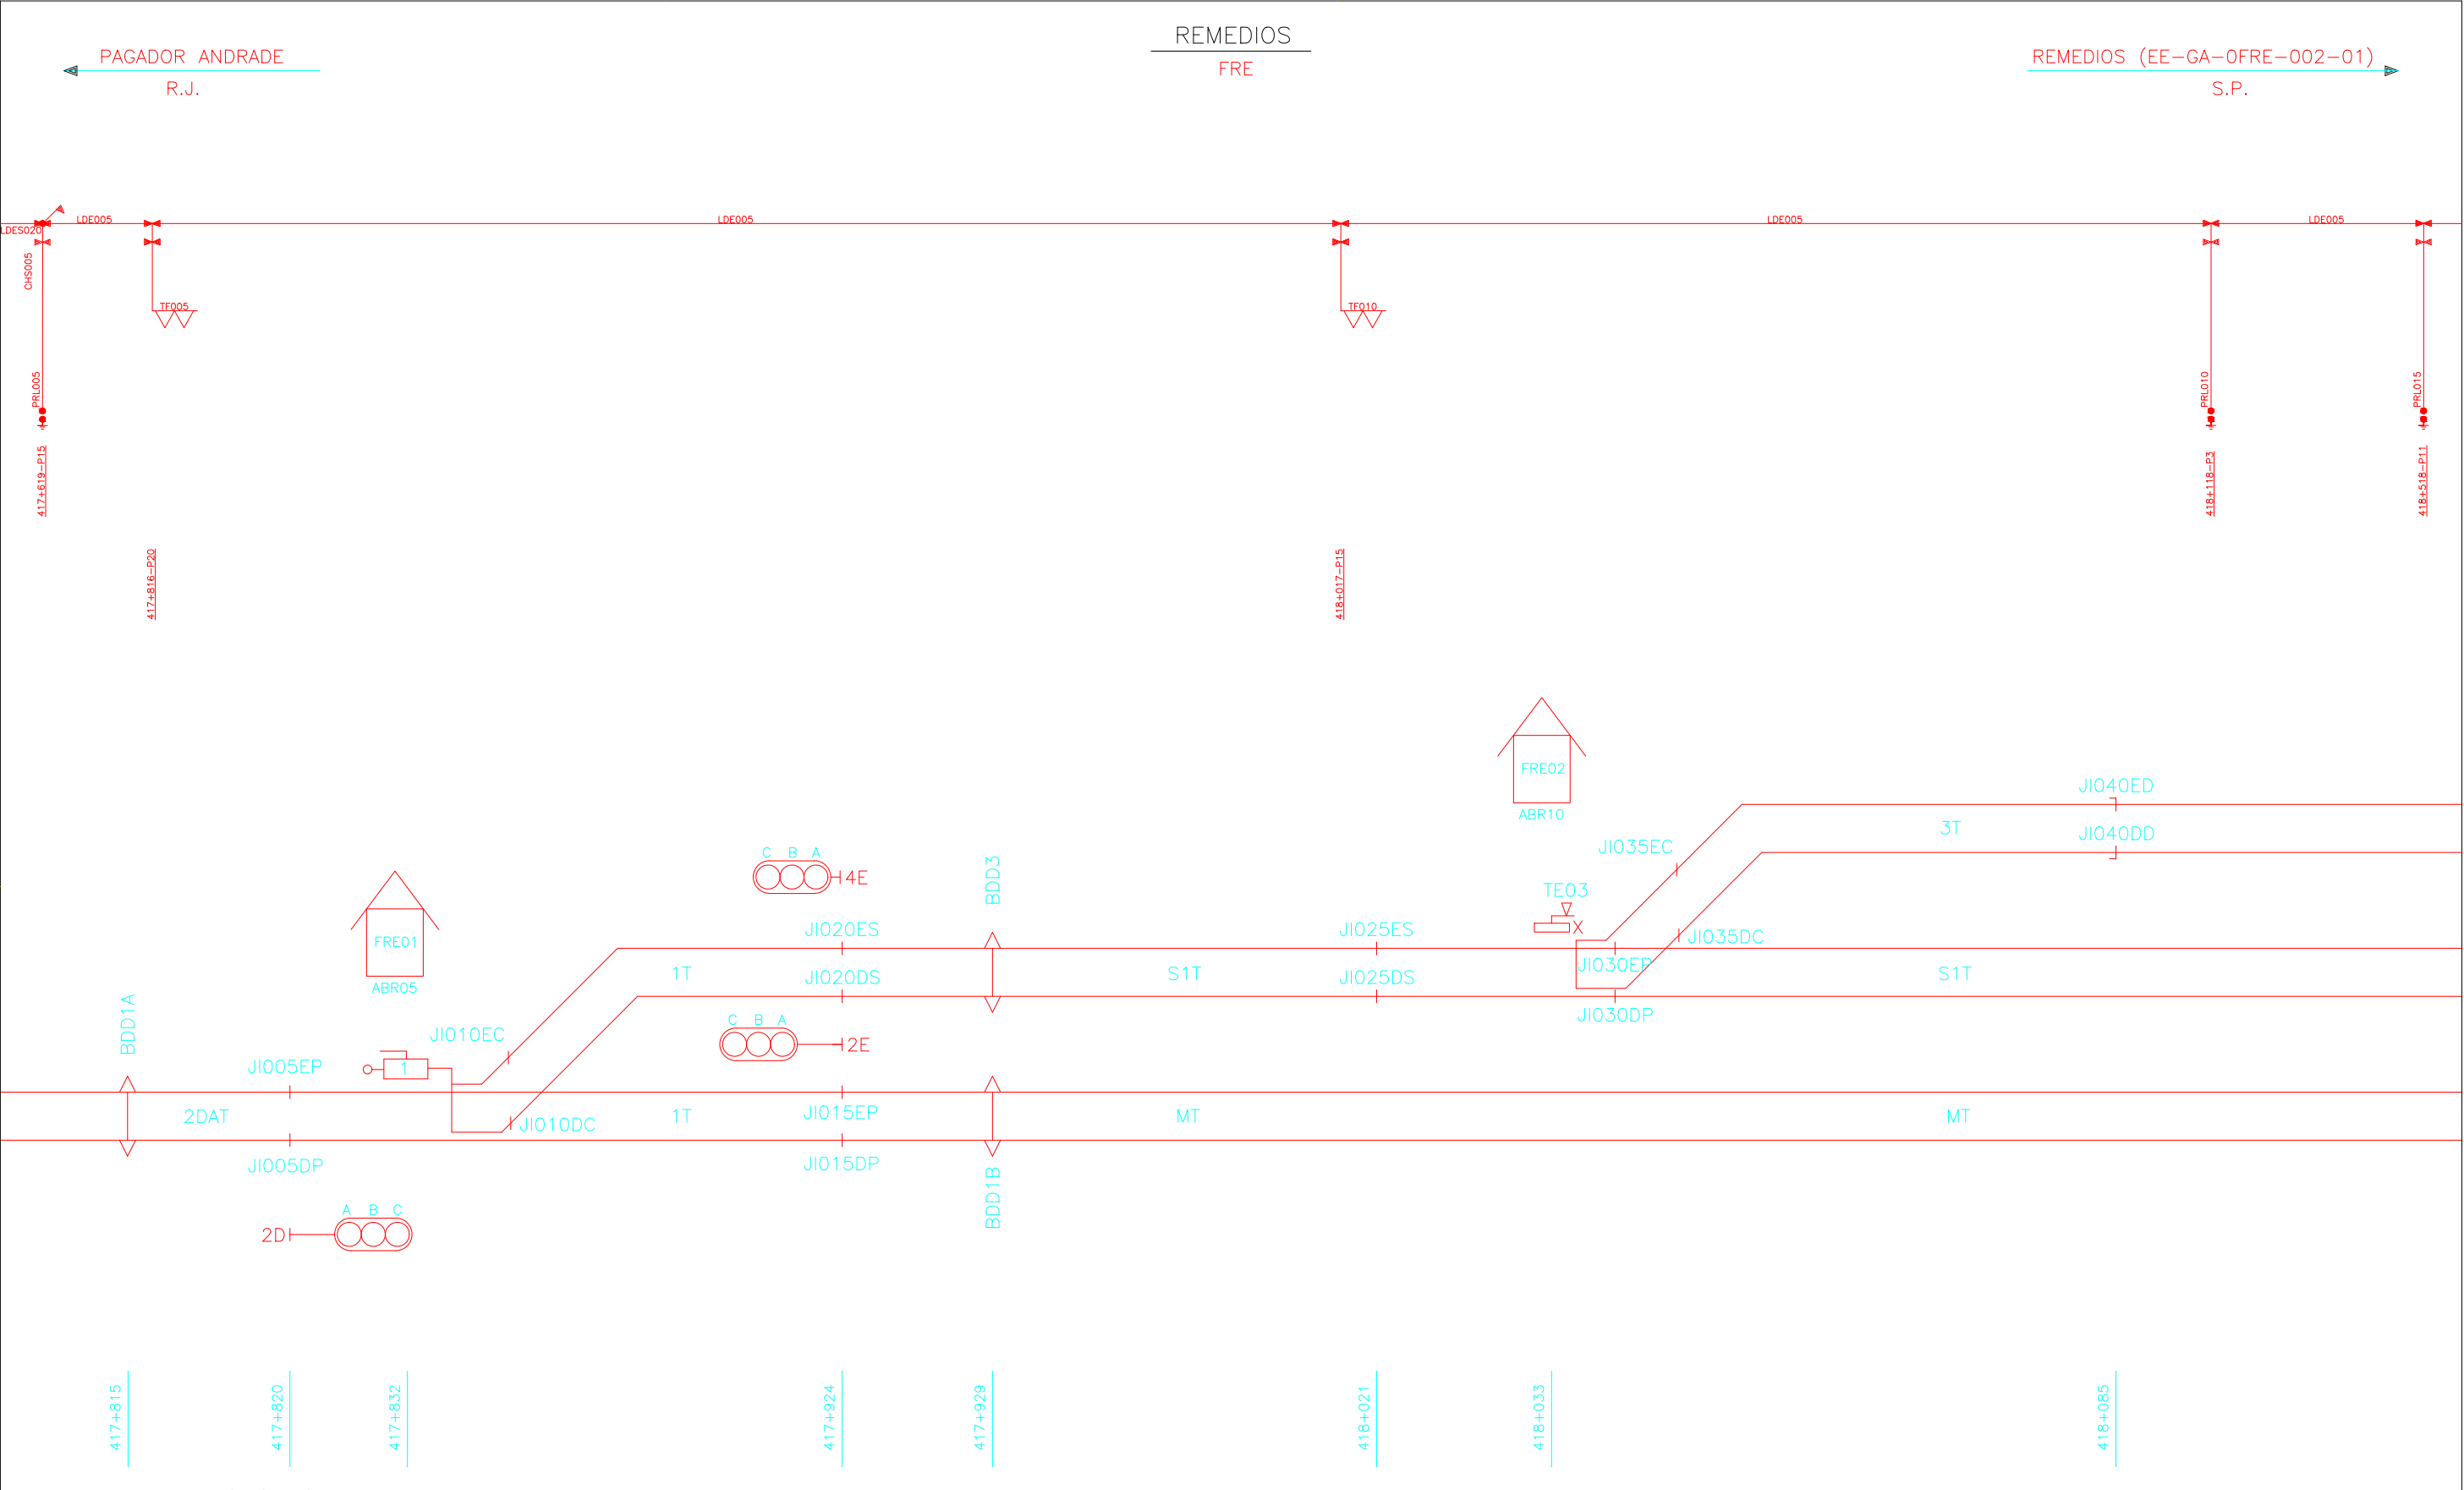

ANOTAÇÕES	ATUALIZADA EM 27/11/2002	MRS Logística S.A.	TÍTULO DES.: S I N G E M CADASTRO DE EQUIPAMENTOS REMEDIOS- FRE	
	REV. 2 - 17/11/2006			
	ATUALIZADA CONFORME O CAMPO	FIRMA CONTRATADA:	ENG.RESP.:	DATA:
	PROJ.: SERGIO BARBOSA DES.: GISELI	-	PROJ.:	14/09/1995
	REV. 3 - 30/03/2007		DES.PROJ.:	FORMATO: A3
ATUALIZAÇÃO	PROJ.: SERGIO BARBOSA DES.: GISELI		REV./DATA:	5 - 15/07/2025
REV.4 - 28/05/2008	ATUALIZAÇÃO CONFORME O LEVANTA MENTO NO CAMPO EM 2007		SUBST./REF.:	F0.CST2:FRE-001
PROJ.: PCM - EDUARDO SILVA LIMA DES.: GISELI	REV. 5 - 15/07/2025	Nº ARQUIVO MRS:	EE-GA-OFRE-001-01	
REVISÃO DEVIDO SINLIZAÇÃO DO PATIO. PROJETO CTC DO VALE RAFAEL BEVON - 15/07/2025				

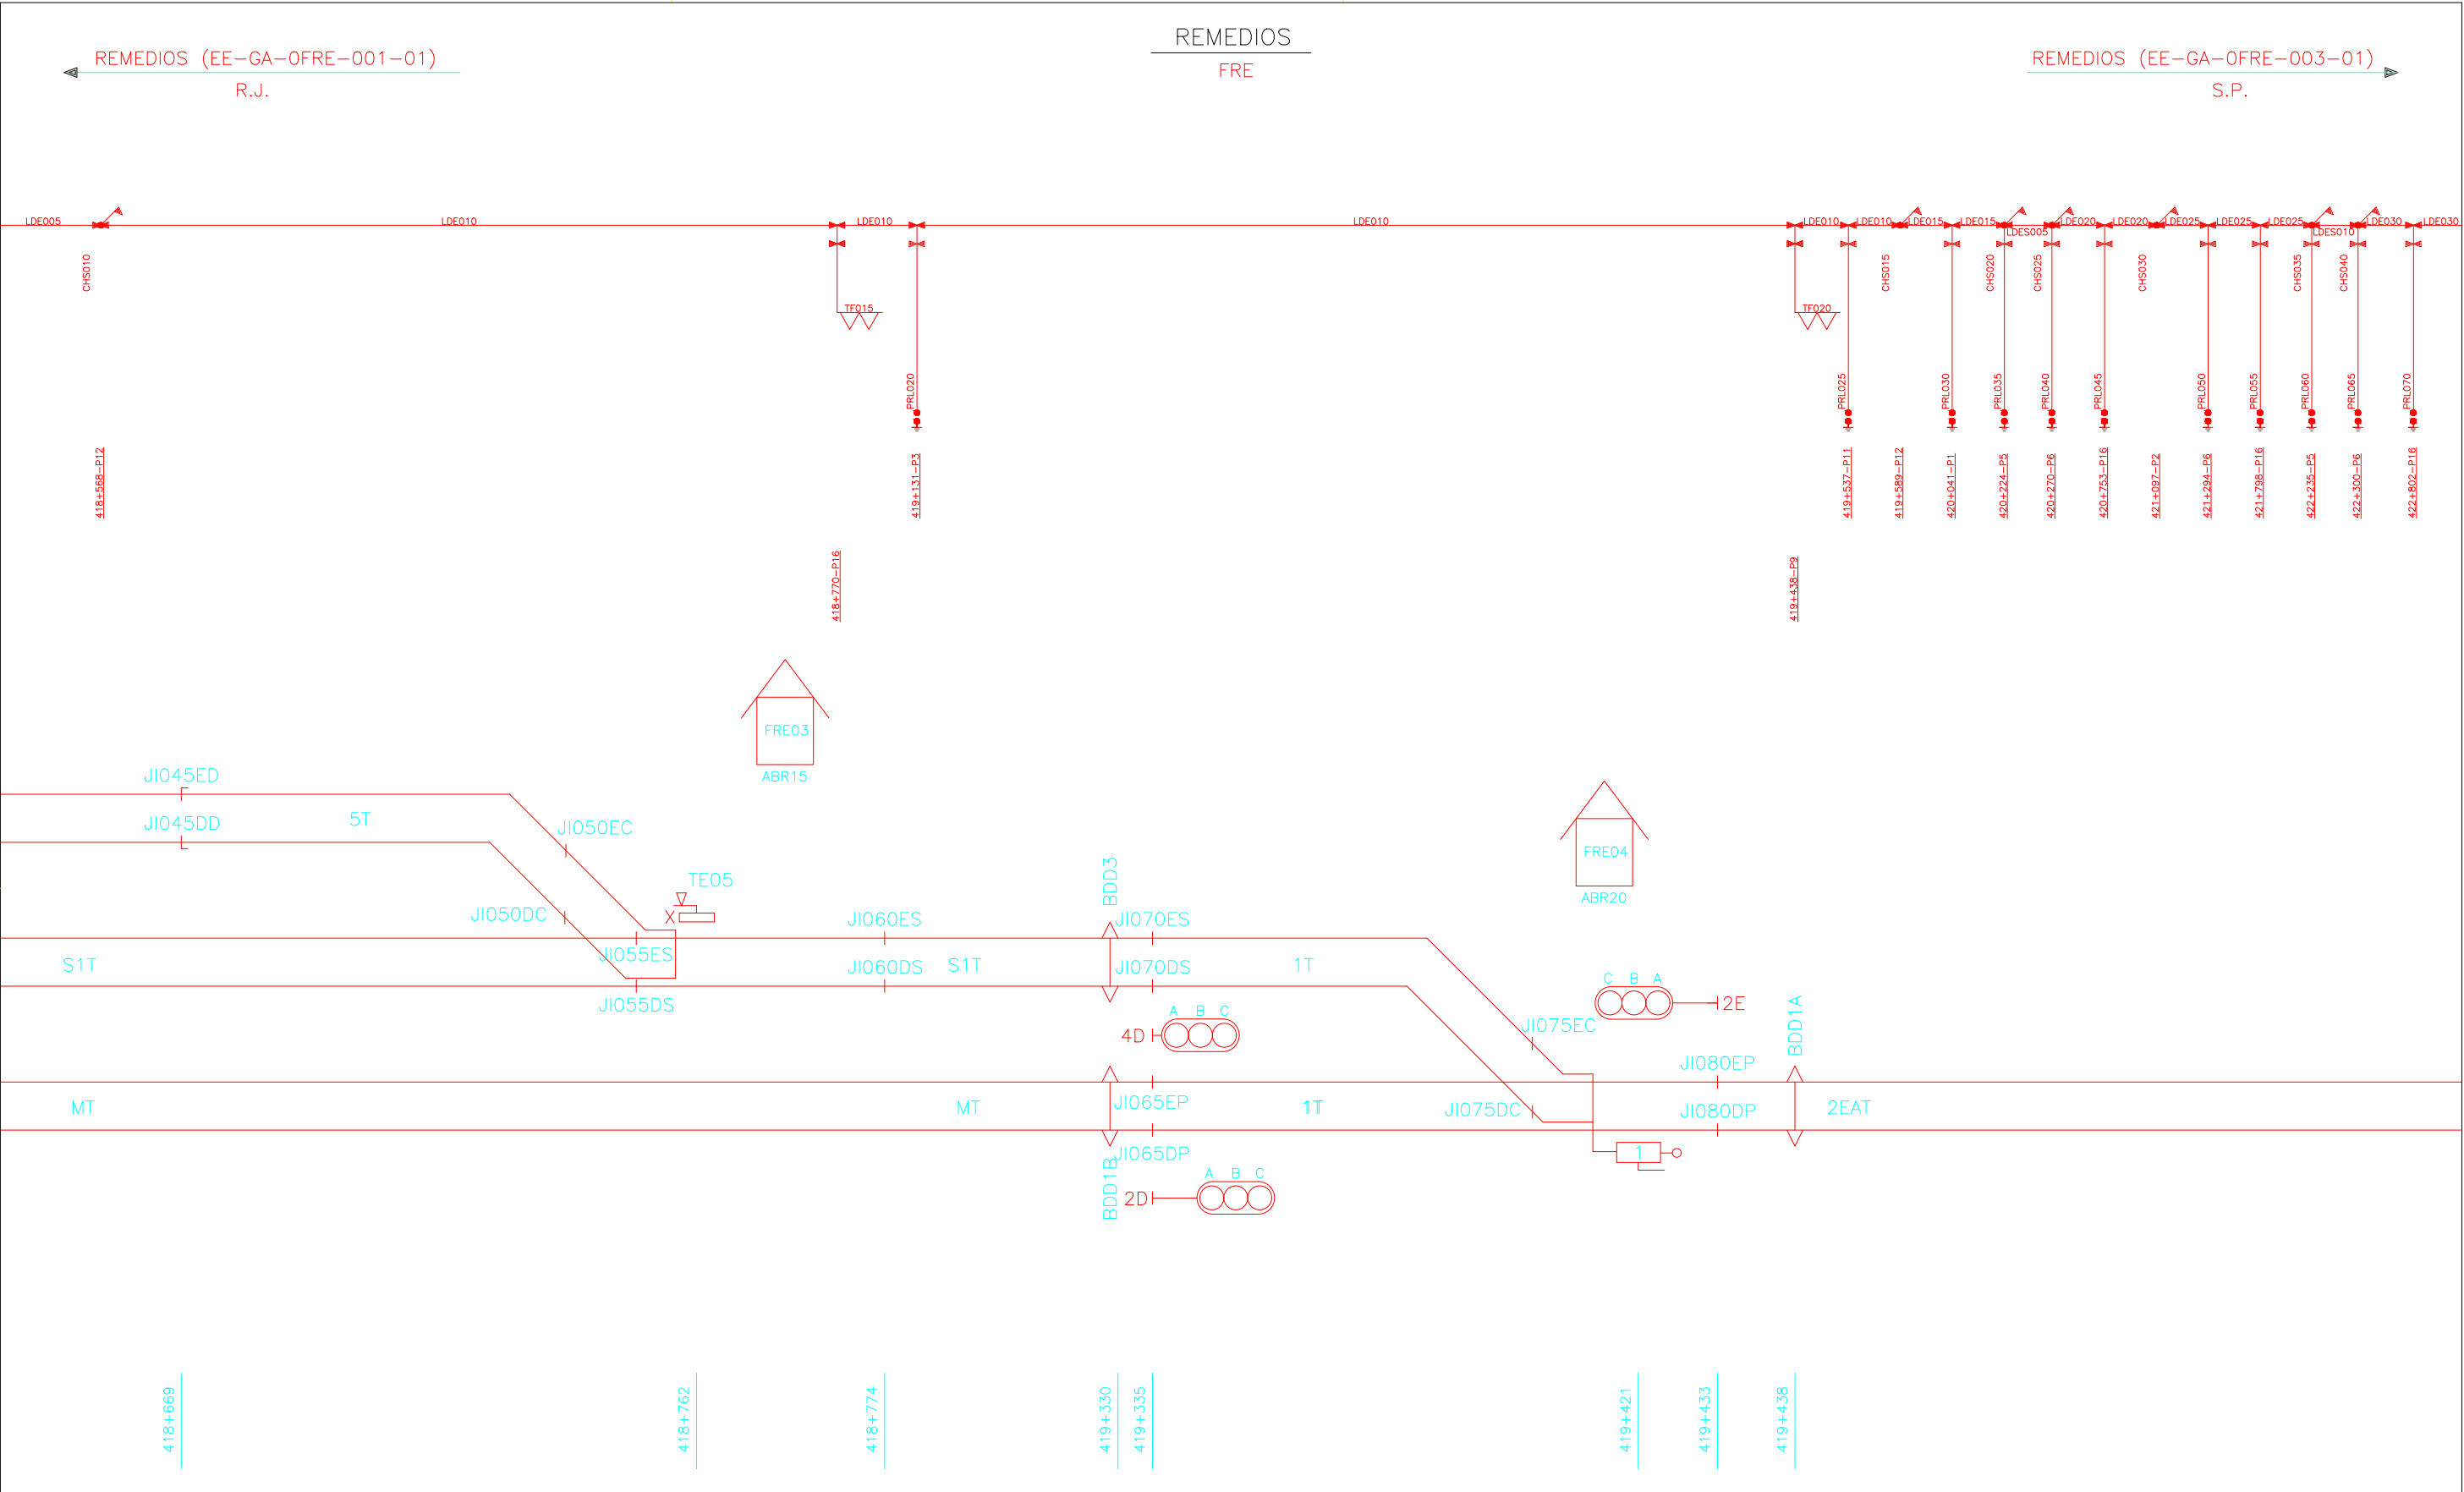

418+669

418+762

418+774

419+330


419+335

419+421

419+433

419+438

ANOTAÇÕES	ATUALIZADA EM 05/10/2004 WILLIAN	MRS Logística S.A.		TÍTULO DES.: S I N G E M CADASTRO DE EQUIPAMENTOS REMEDIOS- FRE	
	REV. 2 - 28/05/2008				
	ATUALIZAÇÃO CONFORME O LEVANTA MENTO NO CAMPO EM 2007				
	PROJ.: PCM - EDUARDO SILVA LIMA DES.: GISELI				
	REV. 3 - 15/07/2025				
REVISÃO DEVIDO SINALIZAÇÃO DO PATIO, PROJETO CTC DO VALE RAFAEL BEVON - 15/07/2025		FIRMA CONTRATADA:		ENG.RESP.: -	DATA: 14/09/1995
				PROJ.: -	ESCALA: -
				DES.PROJ.: GISELI	FORMATO: A3
				REV./DATA: 3 - 15/07/2025	
				SUBST./REF.: F0.CST2:FRE-001	
		Nº ARQUIVO MRS:		EE-GA-OFRE-002-01	

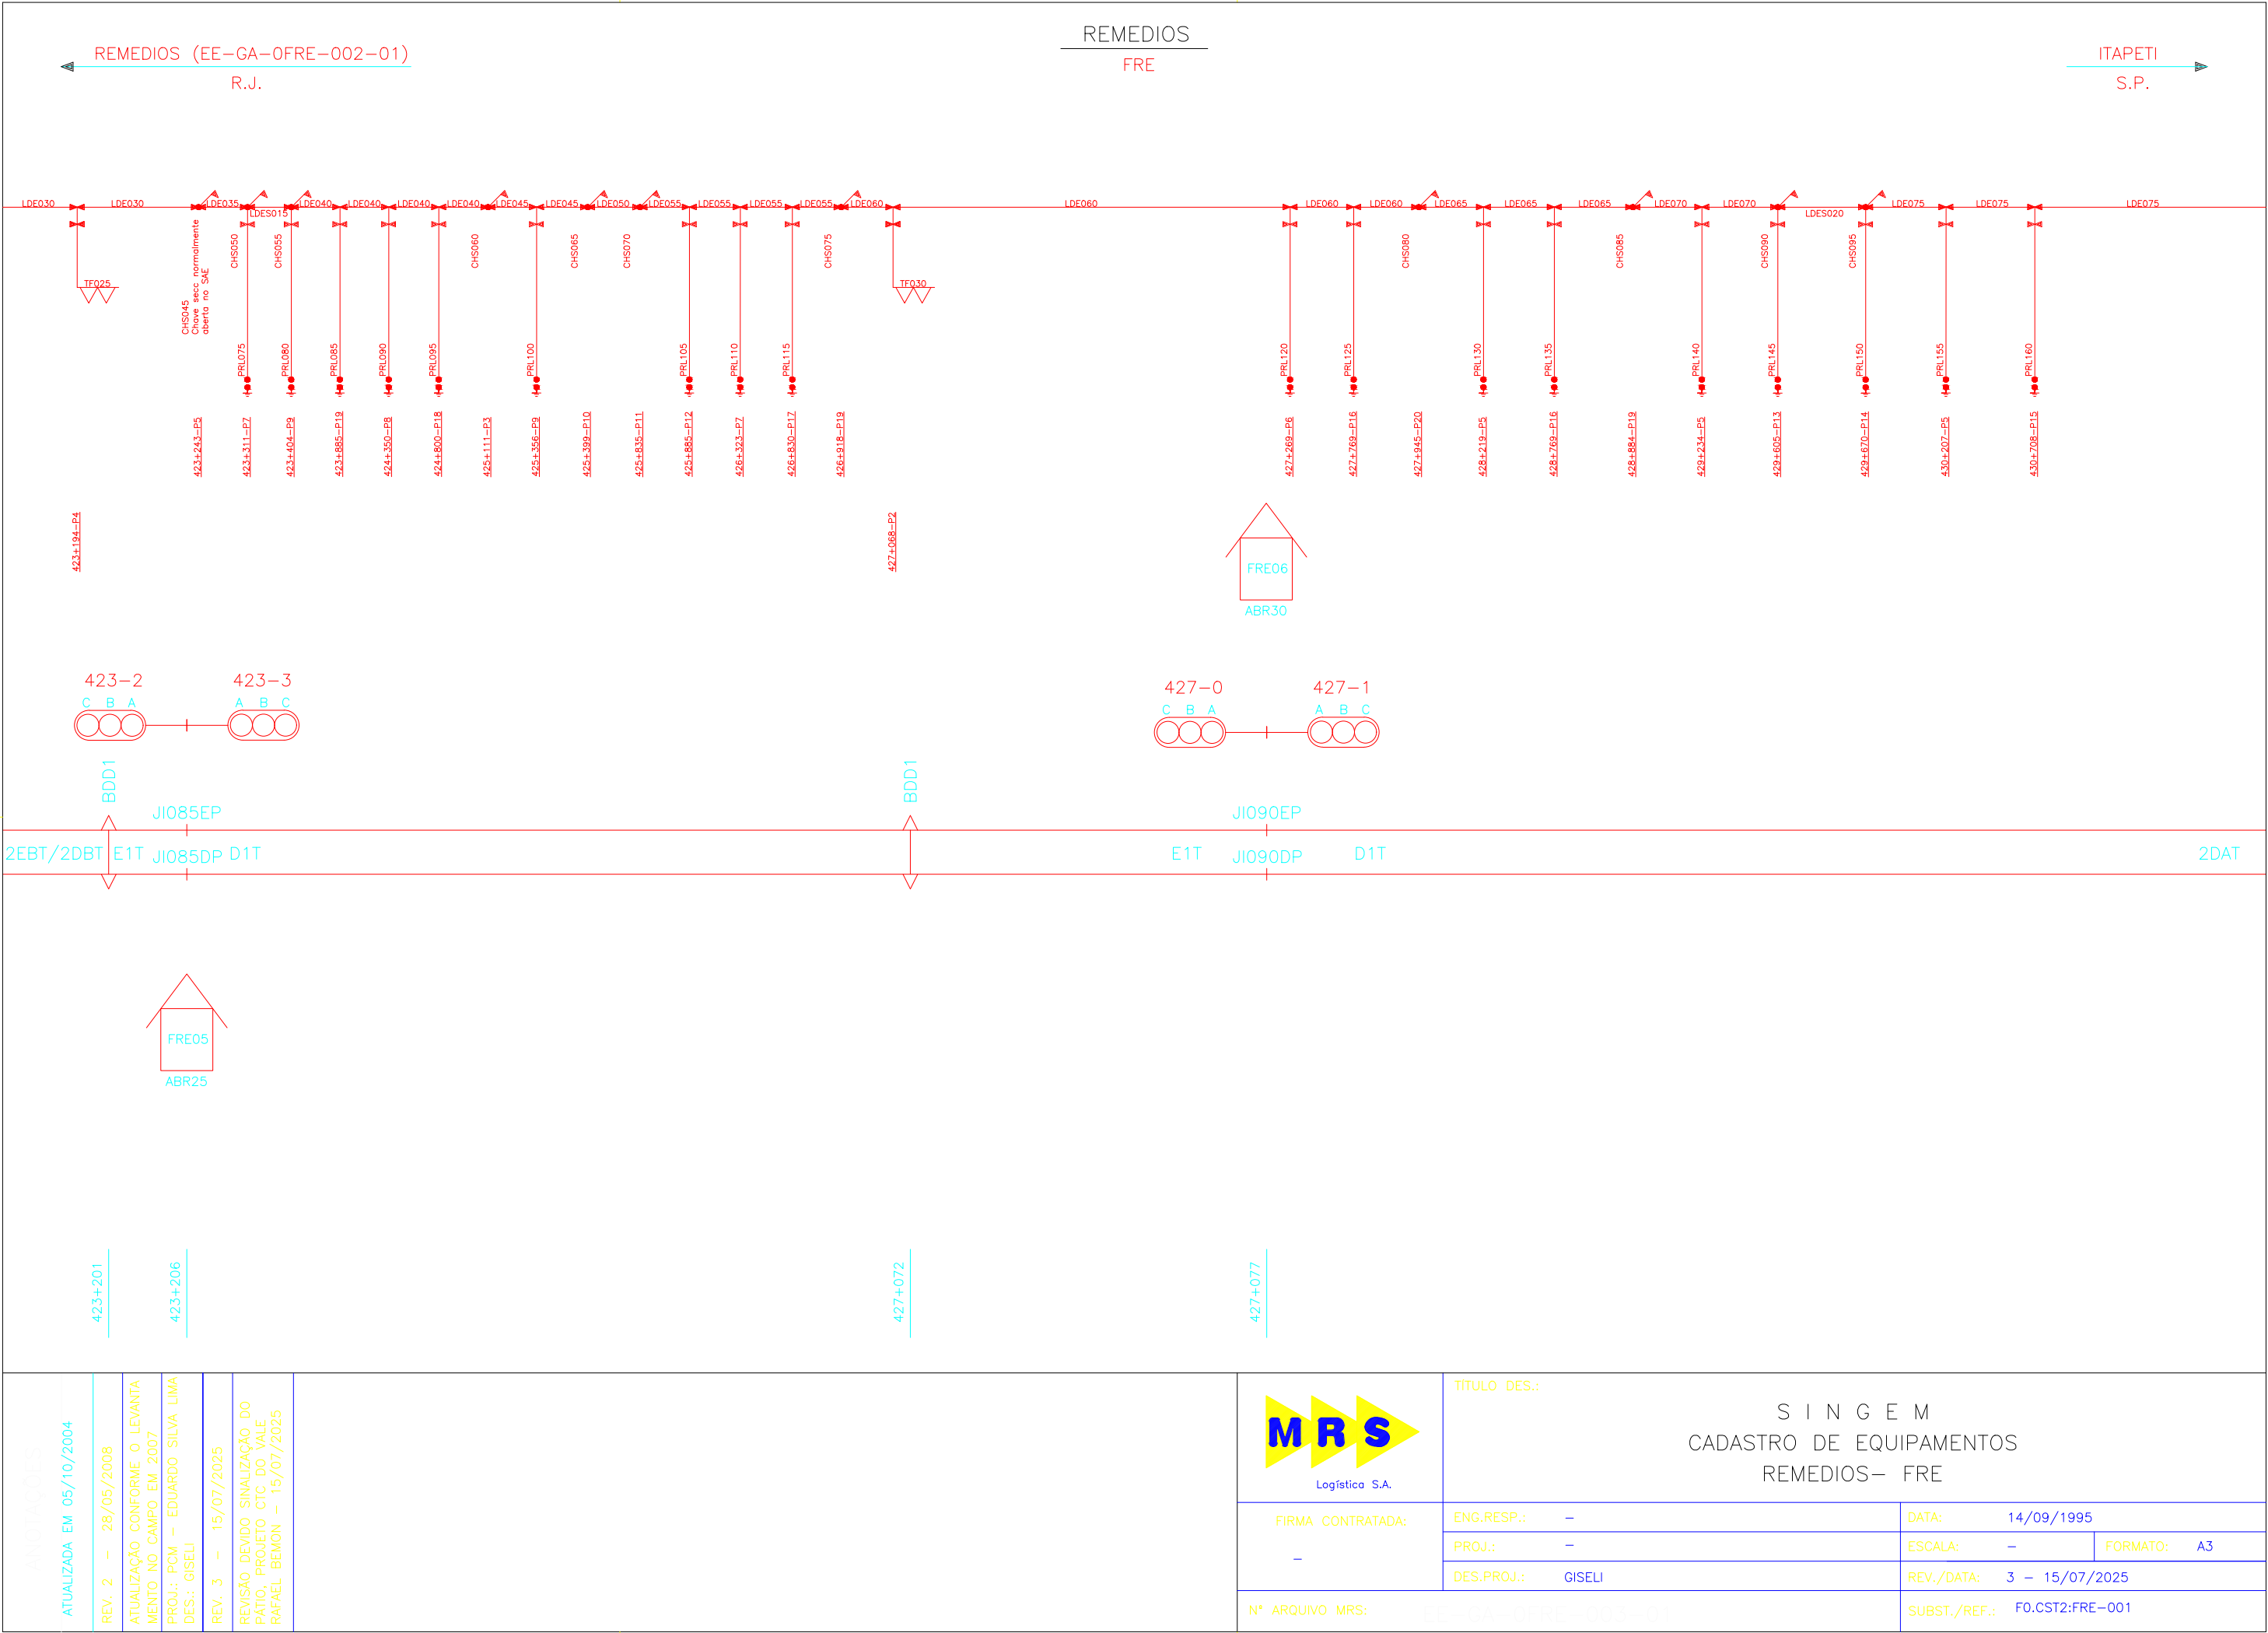

ANOTAÇÕES	ATUALIZADA EM 05/10/2004
	REV. 2 - 28/05/2008
	ATUALIZAÇÃO CONFORME O LEVANTA MENTO NO CAMPO EM 2007
	PROJ.: PCM - EDUARDO SILVA LIMA
	DES.: GISELI
REV. 3 - 15/07/2025	REVISÃO DEVIDO SINLIZAÇÃO DO PÁLIO, PROJETO CTC DO VALE
	RAFAEL BEMON - 15/07/2025

MRS Logística S.A. FIRMA CONTRATADA: - Nº ARQUIVO MRS: EE-GA-OFRE-003-01	TITULO DES.: S I N G E M CADASTRO DE EQUIPAMENTOS REMEDIOS- FRE		
	ENG.RESP.:	-	DATA: 14/09/1995
	PROJ.:	-	ESCALA: - FORMATO: A3
	DES.PROJ.:	GISELI	REV./DATA: 3 - 15/07/2025
		SUBST./REF.:	F0.CST2:FRE-001