



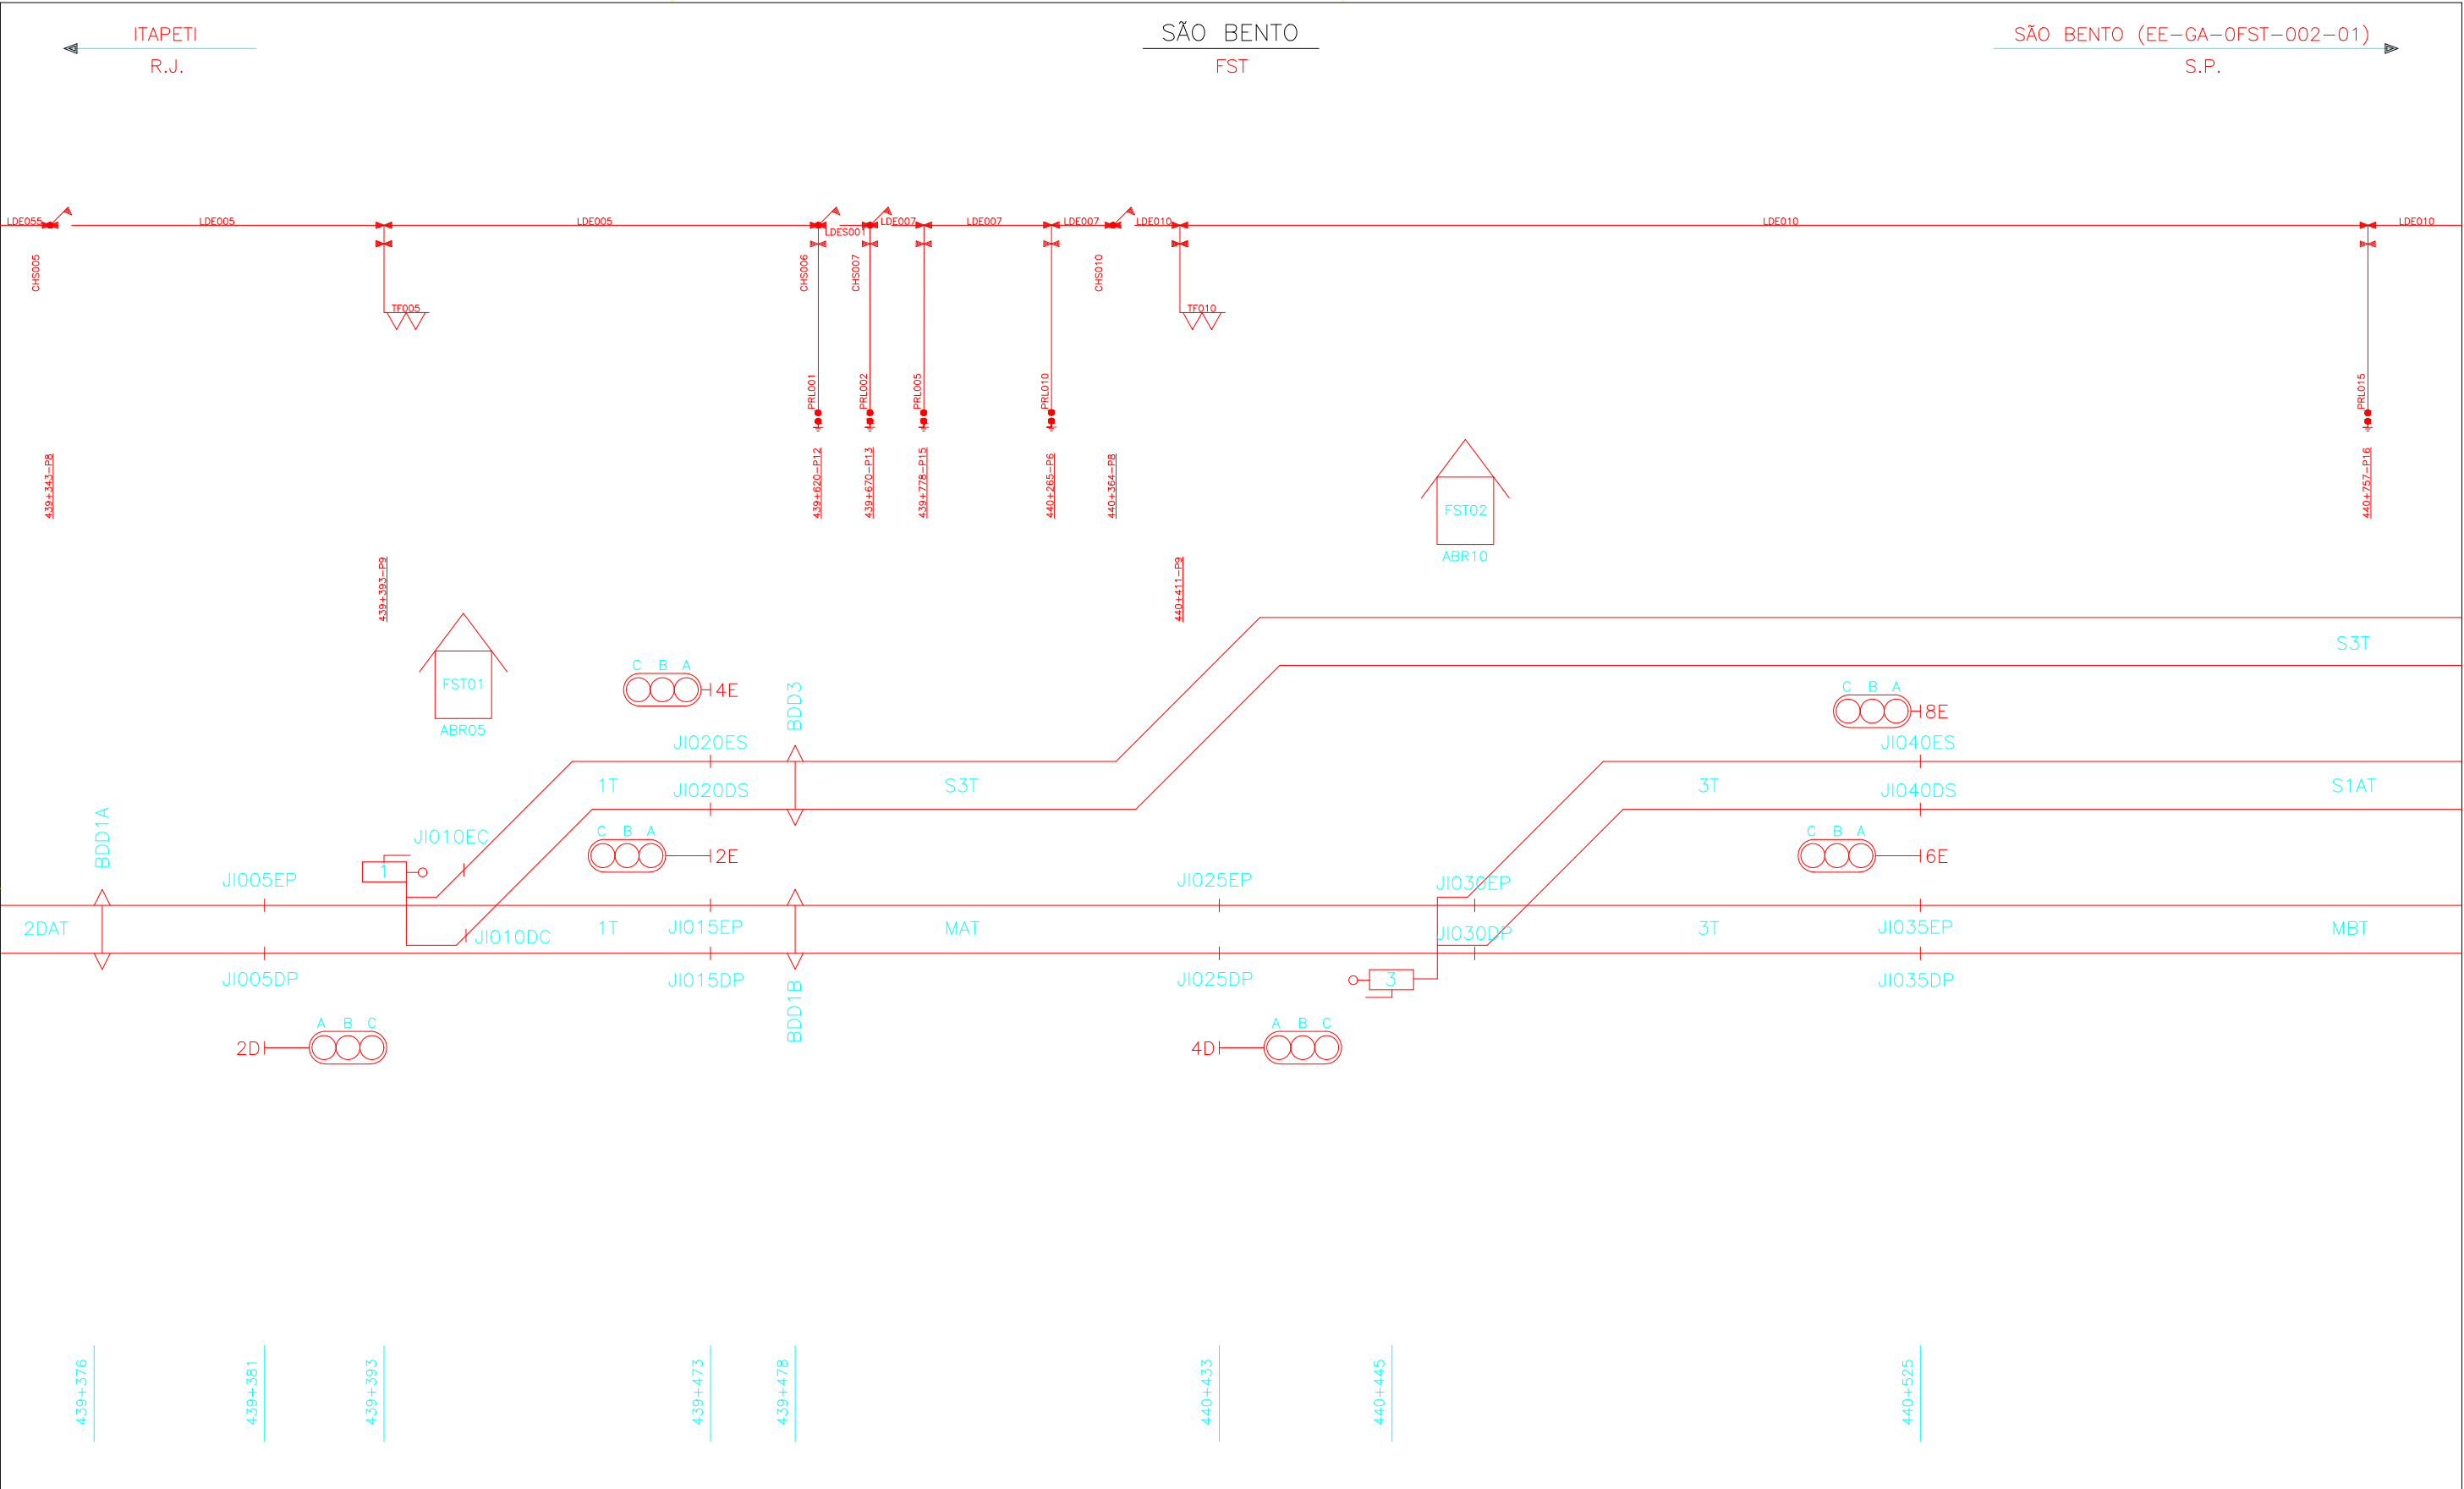

ANOTAÇÕES	ATUALIZADA EM 27/11/2002	MRS Logística S.A.	TÍTULO DES.: S I N G E M CADASTRO DE EQUIPAMENTOS SÃO BENTO – FST	
	ATUALIZADA EM 06/04/2004 ALHADAS			
	ATUALIZADA EM 28/06/2005	FIRMA CONTRATADA:	ENG.RESP.:	DATA: 13/09/1995
	REV. 4 – 28/05/2008	–	PROJ.:	ESCALA: – FORMATO: A3
	ATUALIZAÇÃO CONFORME O LEVANTA MENTO NO CAMPO EM 2007 PROJ.: PCM – EDUARDO SILVA LIMA DES.: GISELI	DES.PROJ.: GISELI	REV./DATA: 6 – 15/07/2025	SUBST./REF.: F0.CST2:FSJ-001
REV. 5 – 21/02/2013				
ATUALIZADA CONFORME O CAMPO POR EDILSON COELHO				
PROJ.: DES.: DEISE AGUIAR				
REV. 6 – 15/07/2025				
REVISÃO DEVIDO SINALIZAÇÃO DO PÁTIO, PROJETO CTC DO VALE RAFAEL BEMON – 15/07/2025				
Nº ARQUIVO MRS: EE-GA-OFST-001-01				

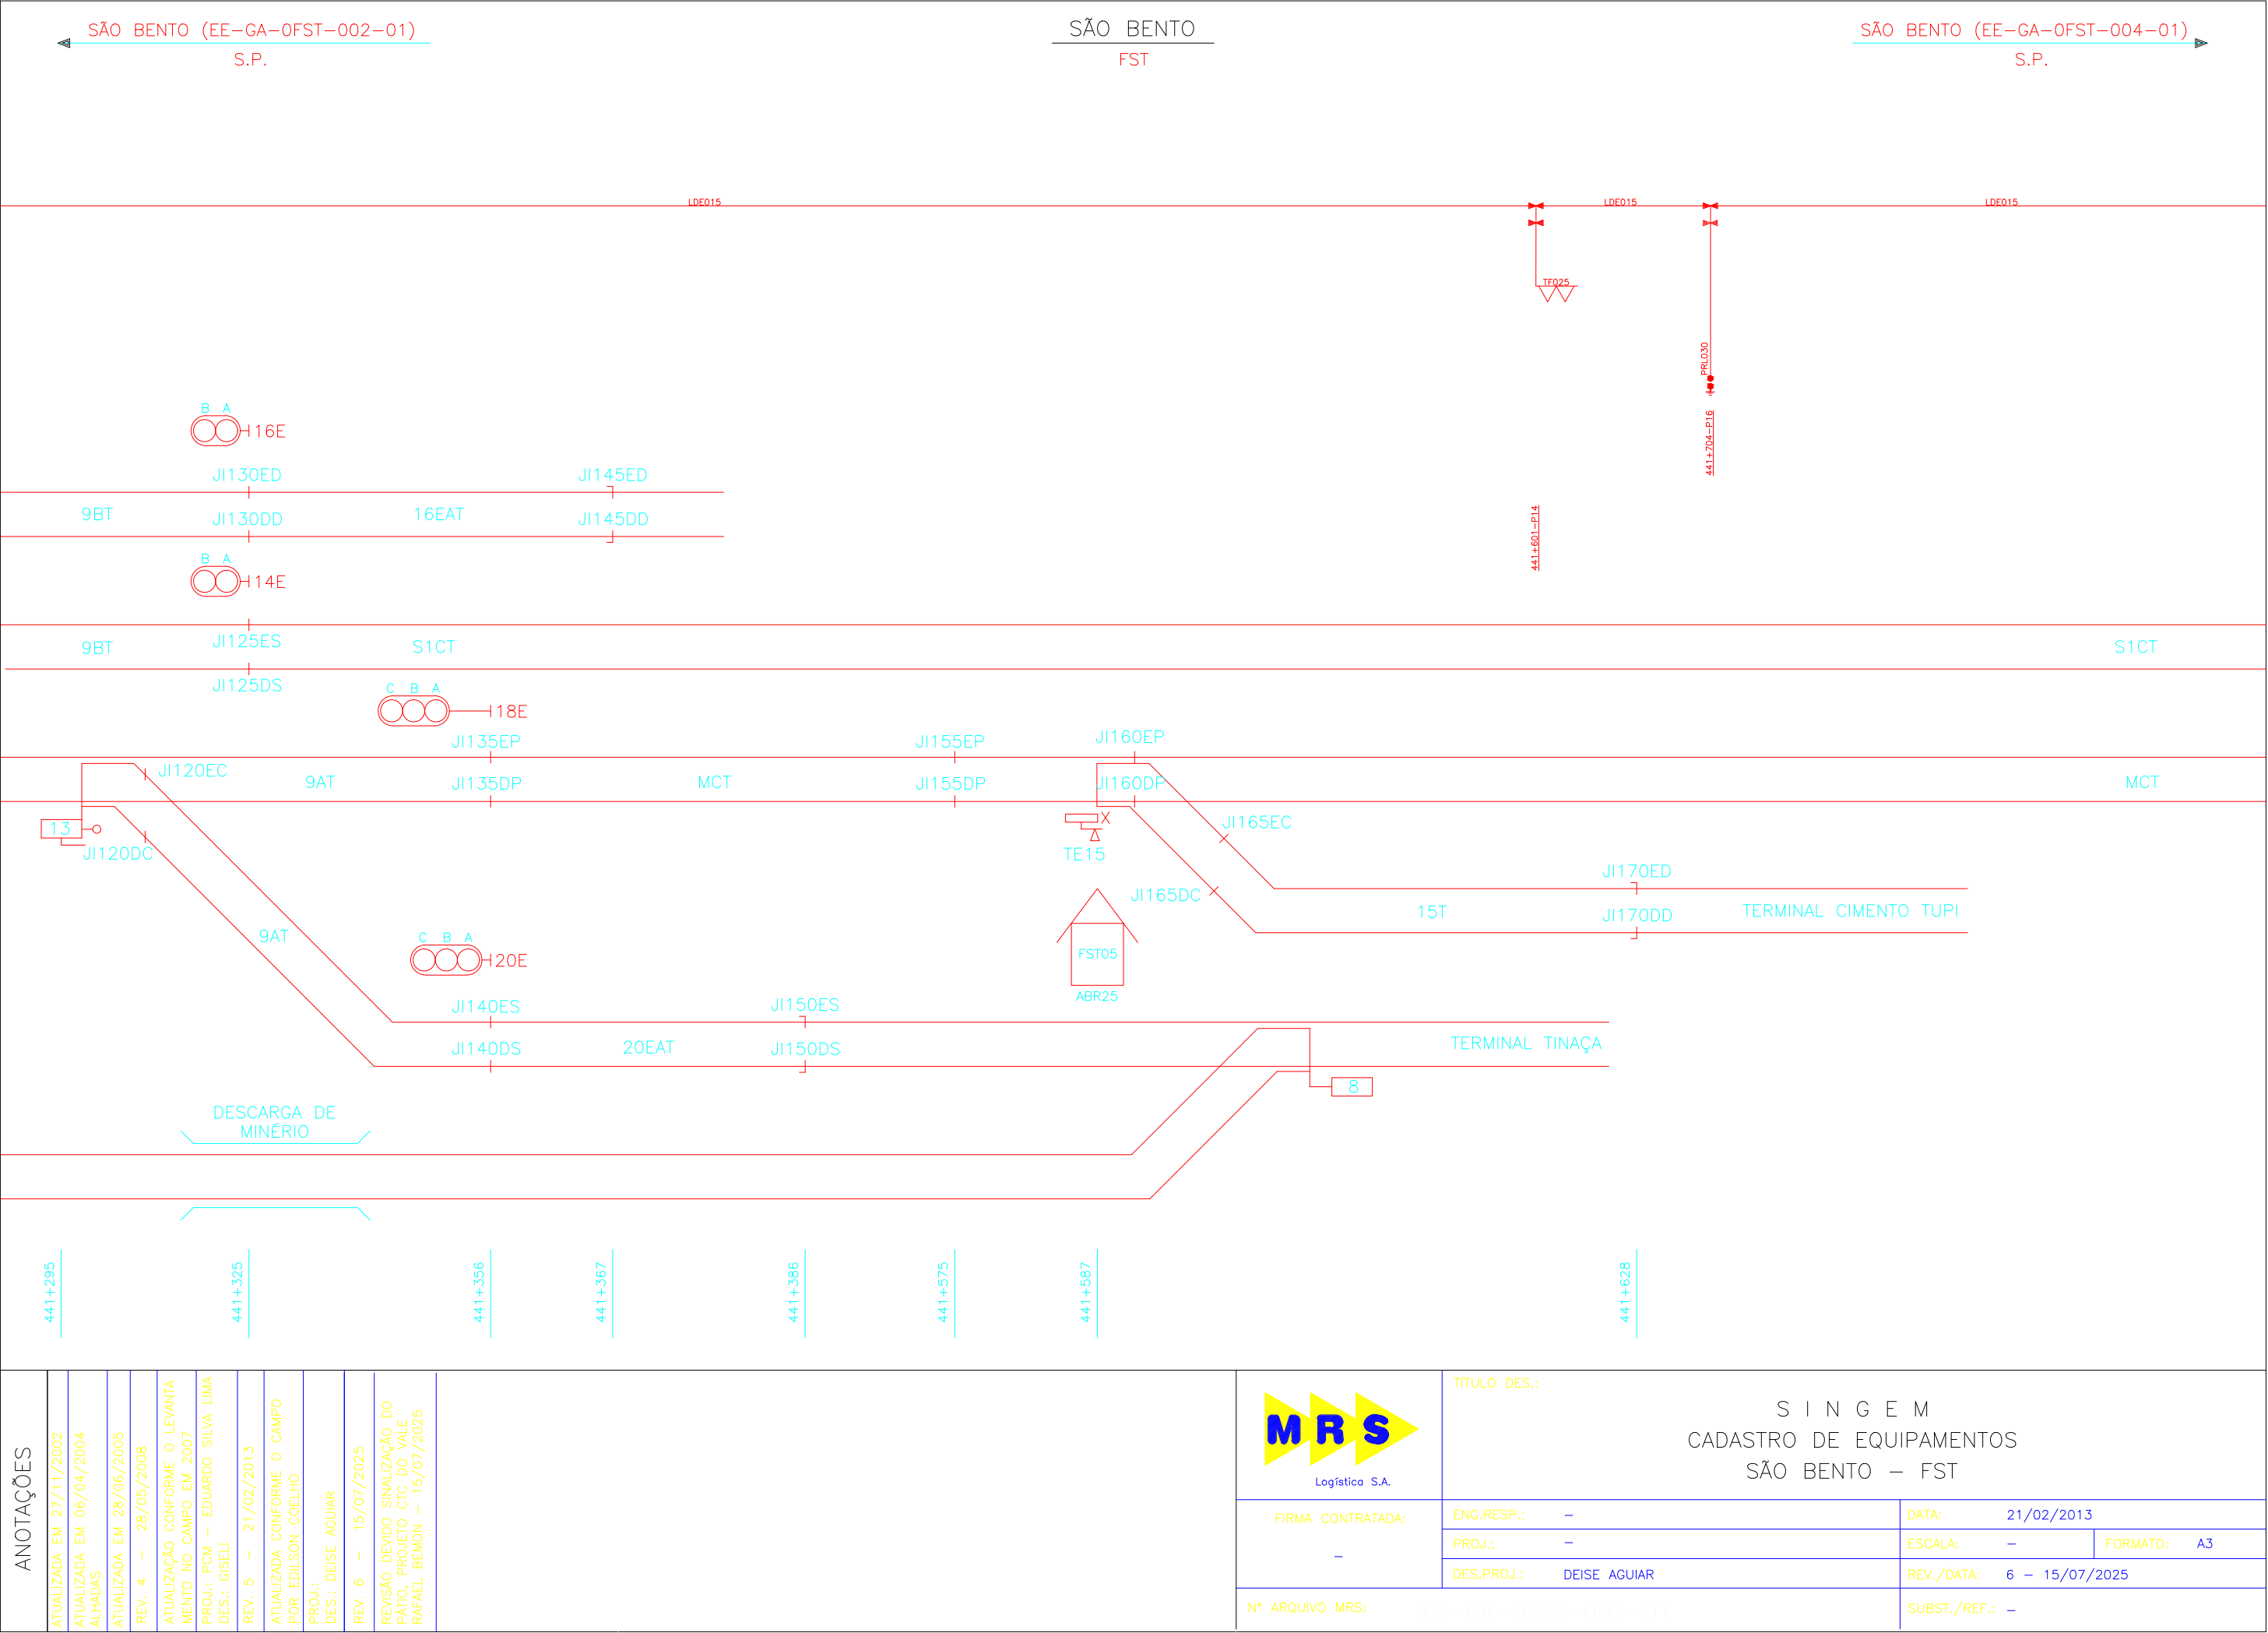

ANOTAÇÕES	ATUALIZADA EM 27/11/2002	MRS Logística S.A.	TÍTULO DES.: S I N G E M CADASTRO DE EQUIPAMENTOS SÃO BENTO – FST	
	ATUALIZADA EM 06/04/2004 ALHADAS			
	ATUALIZADA EM 28/06/2005	FIRMA CONTRATADA:	ENG.RESP.:	DATA:
	REV. 4 – 28/05/2008	–	PROJ.:	21/02/2013
	ATUALIZAÇÃO CONFORME O LEVANTA MENTO NO CAMPO EM 2007 PROJ.: PCM – EDUARDO SILVA LIMA DES.: GISELI	–	DES.PROJ.:	ESCALA: – FORMATO: A3
REV. 5 – 21/02/2013		EE-GA-0FST-003-01		REV./DATA: 6 – 15/07/2025
ATUALIZADA CONFORME O CAMPO POR EDILSON COELHO PROJ.: DES.: DEISE AGUIAR				SUBST./REF.: –
REV. 6 – 15/07/2025				
REVISÃO DEVIDO SINLIZAÇÃO DO PÁTIO, PROJETO CTC DO VALE RAFAEL BEMON – 15/07/2025				

