


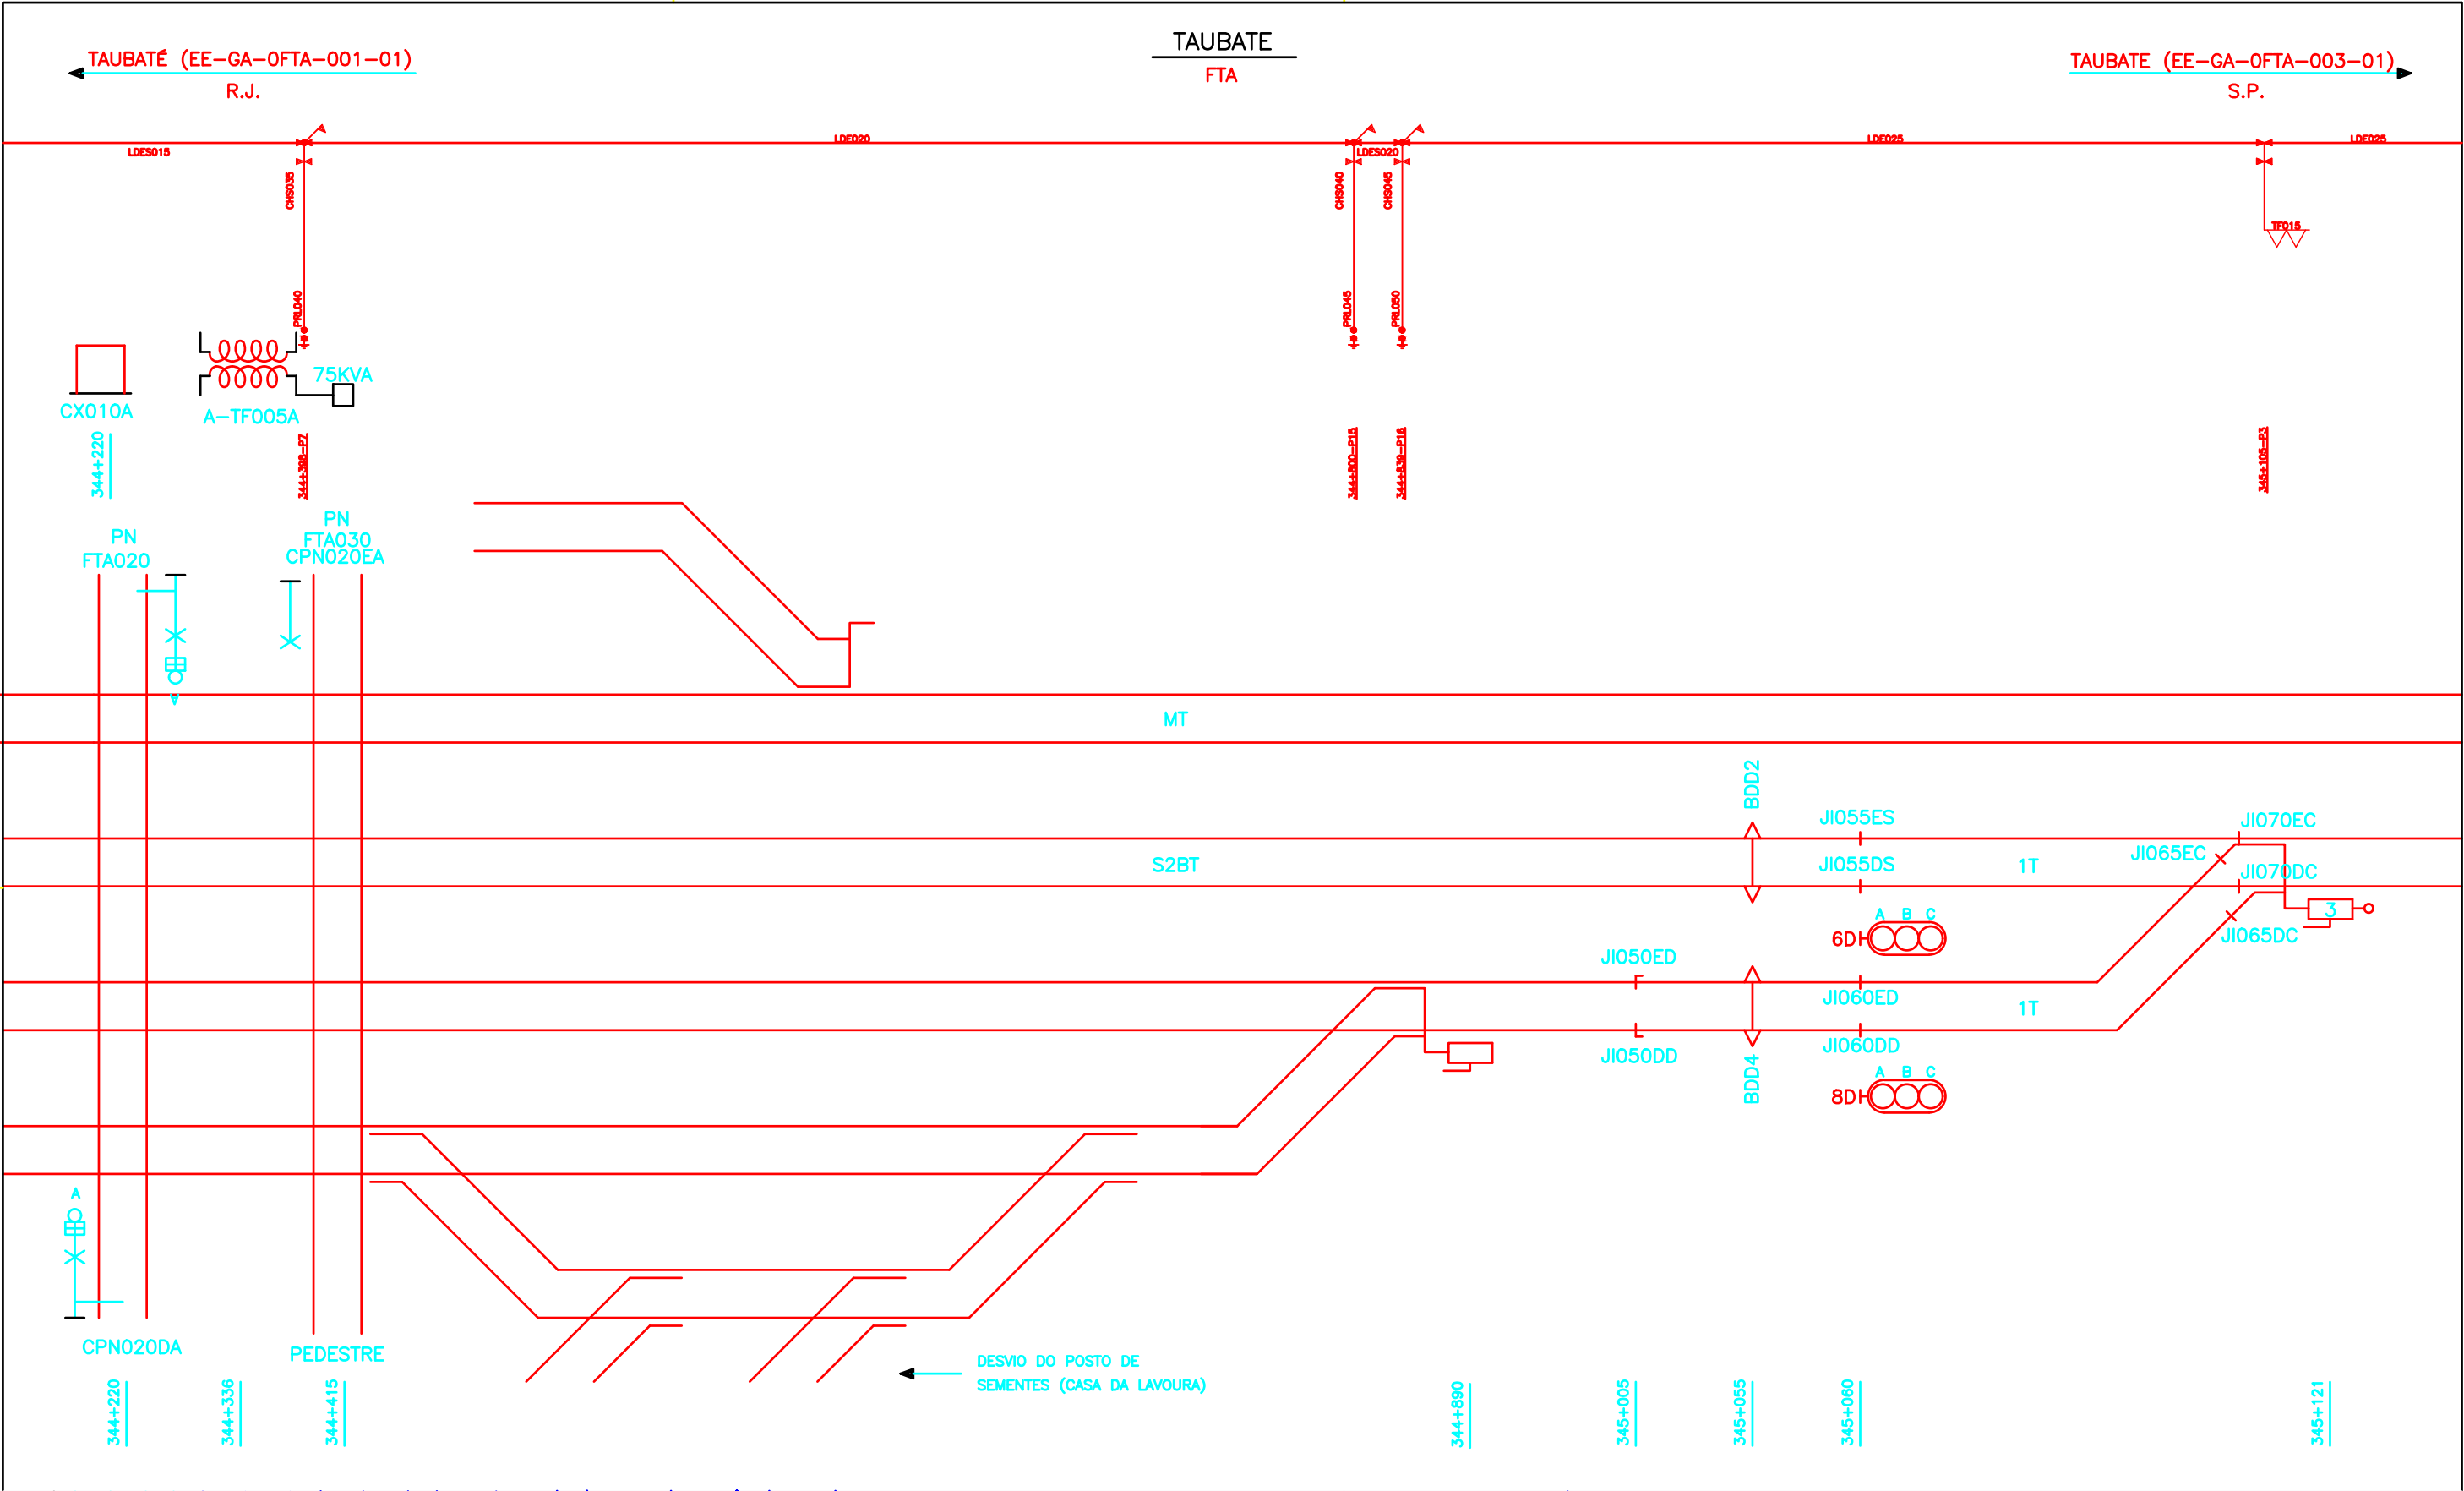


ANOTAÇÕES		TÍTULO DES.:	
ATUALIZADA EM 27/11/2002	WILLIAN	CADASTRO DE EQUIPAMENTOS TAUBATE – FTA	
ATUALIZADA EM 09/08/2004	WILLIAN		
ATUALIZADA EM 21/12/2004	WILLIAN		
ATUALIZADA EM 17/03/2005	WILLIAN	ENG.RESP.: –	
REV. 5 – 26/05/2008	WILLIAN		
ATUALIZAÇÃO CONFORME O LEVANTA- MENTO NO CAMPO EM 2007	WILLIAN		
PROJ.: PCM – EDUARDO SILVA LIMA	DES.: GISELI	PROJ.: –	DATA: 22/06/1994
REV. 6 – 20/04/2012	DES.: GISELI	DES.PROJ.: GISELI	ESCALA: –
ATUALIZADA CONFORME O CAMPO POR EDILSON COELHO	DES.: GISELI		FORMATO: A3
PROJ.: DES.: GISELI	DES.: GISELI		REV./DATA: 9– 22/08/2025
REV. 7 – 30/03/2017	DES.: GISELI		SUBST./REF.: FO.CST2:FTA-001
ATUALIZAÇÃO DEVIDO INCLUSÃO DO SINAL AZUL 3E E CM'S E CL'S.	DES.: GISELI		
PROJ.: DANIELE HELENA	DES.: DANIELE HELENA		
REVISOR.: JOSÉ RENATO	REVISOR.: JOSÉ RENATO		
REV. 8 – 20/04/2018	DES.: DANIELE HELENA		
REVISÃO DEVIDO ACERTO DA NOME- RAÇÃO DAS CHAVES CONFORME PA- NEL COO.	DES.: DANIELE HELENA		
EDILSON COELHO – 19/04/2018	DES.: DANIELE HELENA		
PROJ.: DES.: DANIELE HELENA	DES.: DANIELE HELENA		
REVISOR.: MARCOS REINH	REVISOR.: MARCOS REINH		
REV. 9 – 22/08/2025	DES.: DANIELE HELENA		
REVISÃO DEVIDO SINLAZIZAÇÃO DO PÁTO, PROJETO CTC DO VALE	DES.: DANIELE HELENA		
RAFAEL BEMON – 22/08/2025	DES.: DANIELE HELENA		




FIRMA CONTRATADA:


Nº ARQUIVO MRS:

EE-GA-OFTA-002-01

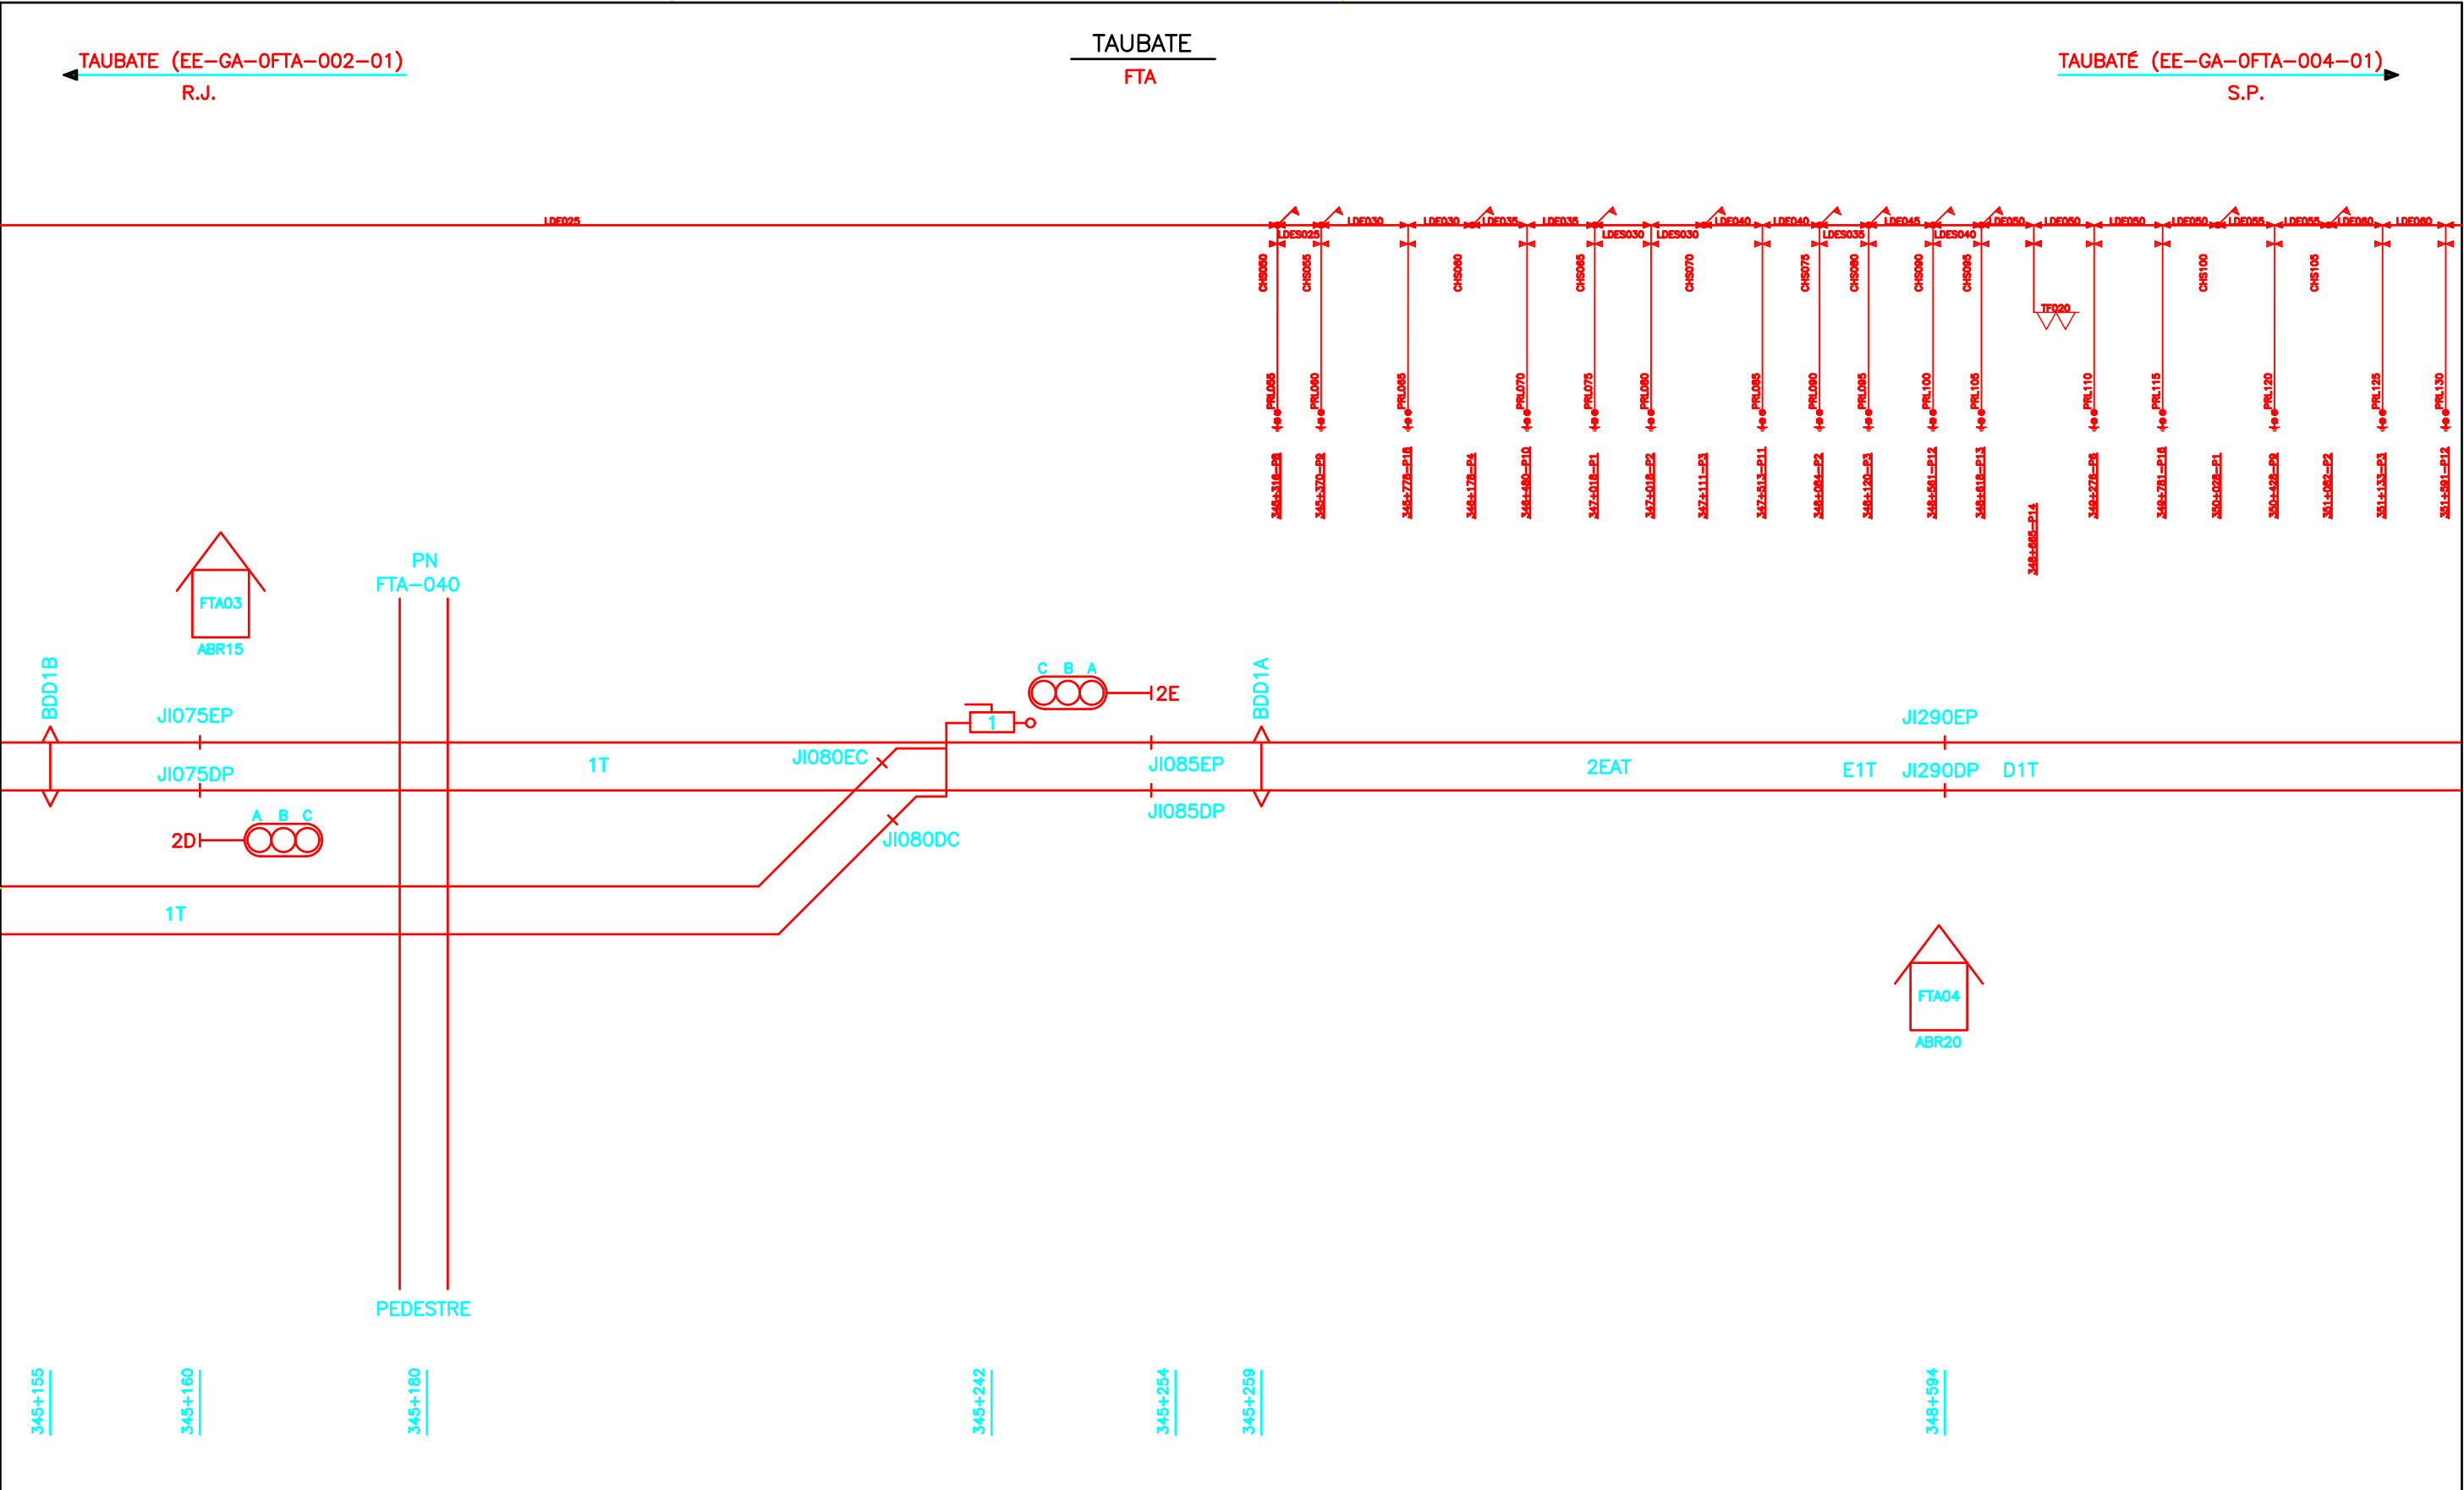

ANOTAÇÕES		TÍTULO DES.:	
ATUALIZADA EM 27/11/2002	ATUALIZADA EM 09/09/2004	CADASTRO DE EQUIPAMENTOS TAUBATE – FTA	
WILLIAN	WILLIAN		
WILLIAN	WILLIAN		
ATUALIZADA EM 05/10/2004	ATUALIZADA EM 21/12/2004	ENG.RESP.: – PROJ.: – DES.PROJ.: MONICA	
WILLIAN	WILLIAN		
WILLIAN	WILLIAN		
ATUALIZADA EM 17/03/2005	ATUALIZADA EM 17/03/2005	DATA: 28/06/1994 ESCALA: – FORMATO: A3	
REV. 6 – 26/05/2008	REV. 6 – 26/05/2008		
REV. 6 – 26/05/2008	REV. 6 – 26/05/2008		
ATUALIZAÇÃO CONFORME O LEVANTA- MENTO NO CAMPO EM 2007	ATUALIZAÇÃO CONFORME O LEVANTA- MENTO NO CAMPO EM 2007	REV./DATA: 9– 22/08/2025 SUBST./REF.: FO.CST2:FPG–002	
PROJ.: PCM – EDUARDO SILVA LIMA DES.: GISELI	PROJ.: PCM – EDUARDO SILVA LIMA DES.: GISELI		
REV. 7 – 30/03/2017	REV. 7 – 30/03/2017		
ATUALIZAÇÃO DEVIDO INCLUSÃO DO SINAL AZUL 3E E CM'S E CL'S.	ATUALIZAÇÃO DEVIDO INCLUSÃO DO SINAL AZUL 3E E CM'S E CL'S.	Nº ARQUIVO MRS: EE-GA-OFTA-003-01	
RUBENS BRANDI 01/12/2016	RUBENS BRANDI 01/12/2016		
PROJ.: DANIELE HELENA REVISOR.: JOSÉ RENATO	PROJ.: DANIELE HELENA REVISOR.: JOSÉ RENATO		
REV. 8 – 20/04/2018	REV. 8 – 20/04/2018	TÍTULO DES.:	
REV. 8 – 20/04/2018	REV. 8 – 20/04/2018		
REV. 8 – 20/04/2018	REV. 8 – 20/04/2018		
REVISÃO DEVIDO ACERTO DA NOME- RAÇÃO DAS CHAVES CONFORME PAI- NEL COO.	REVISÃO DEVIDO ACERTO DA NOME- RAÇÃO DAS CHAVES CONFORME PAI- NEL COO.	CADASTRO DE EQUIPAMENTOS TAUBATE – FTA	
EDILSON COELHO – 19/04/2018	EDILSON COELHO – 19/04/2018		
PROJ.: DANIELE HELENA REVISOR.: MARCOS REINH	PROJ.: DANIELE HELENA REVISOR.: MARCOS REINH		
REV. 9 – 22/08/2025	REV. 9 – 22/08/2025	ENG.RESP.: – PROJ.: – DES.PROJ.: MONICA	
REV. 9 – 22/08/2025	REV. 9 – 22/08/2025		
REV. 9 – 22/08/2025	REV. 9 – 22/08/2025		
REVISÃO DEVIDO SINLIZAÇÃO DO PÁTIO, PROJETO CTC DO VALE	REVISÃO DEVIDO SINLIZAÇÃO DO PÁTIO, PROJETO CTC DO VALE	DATA: 28/06/1994 ESCALA: – FORMATO: A3	
RAFAEL BEMON – 22/08/2025	RAFAEL BEMON – 22/08/2025		
RAFAEL BEMON – 22/08/2025	RAFAEL BEMON – 22/08/2025		

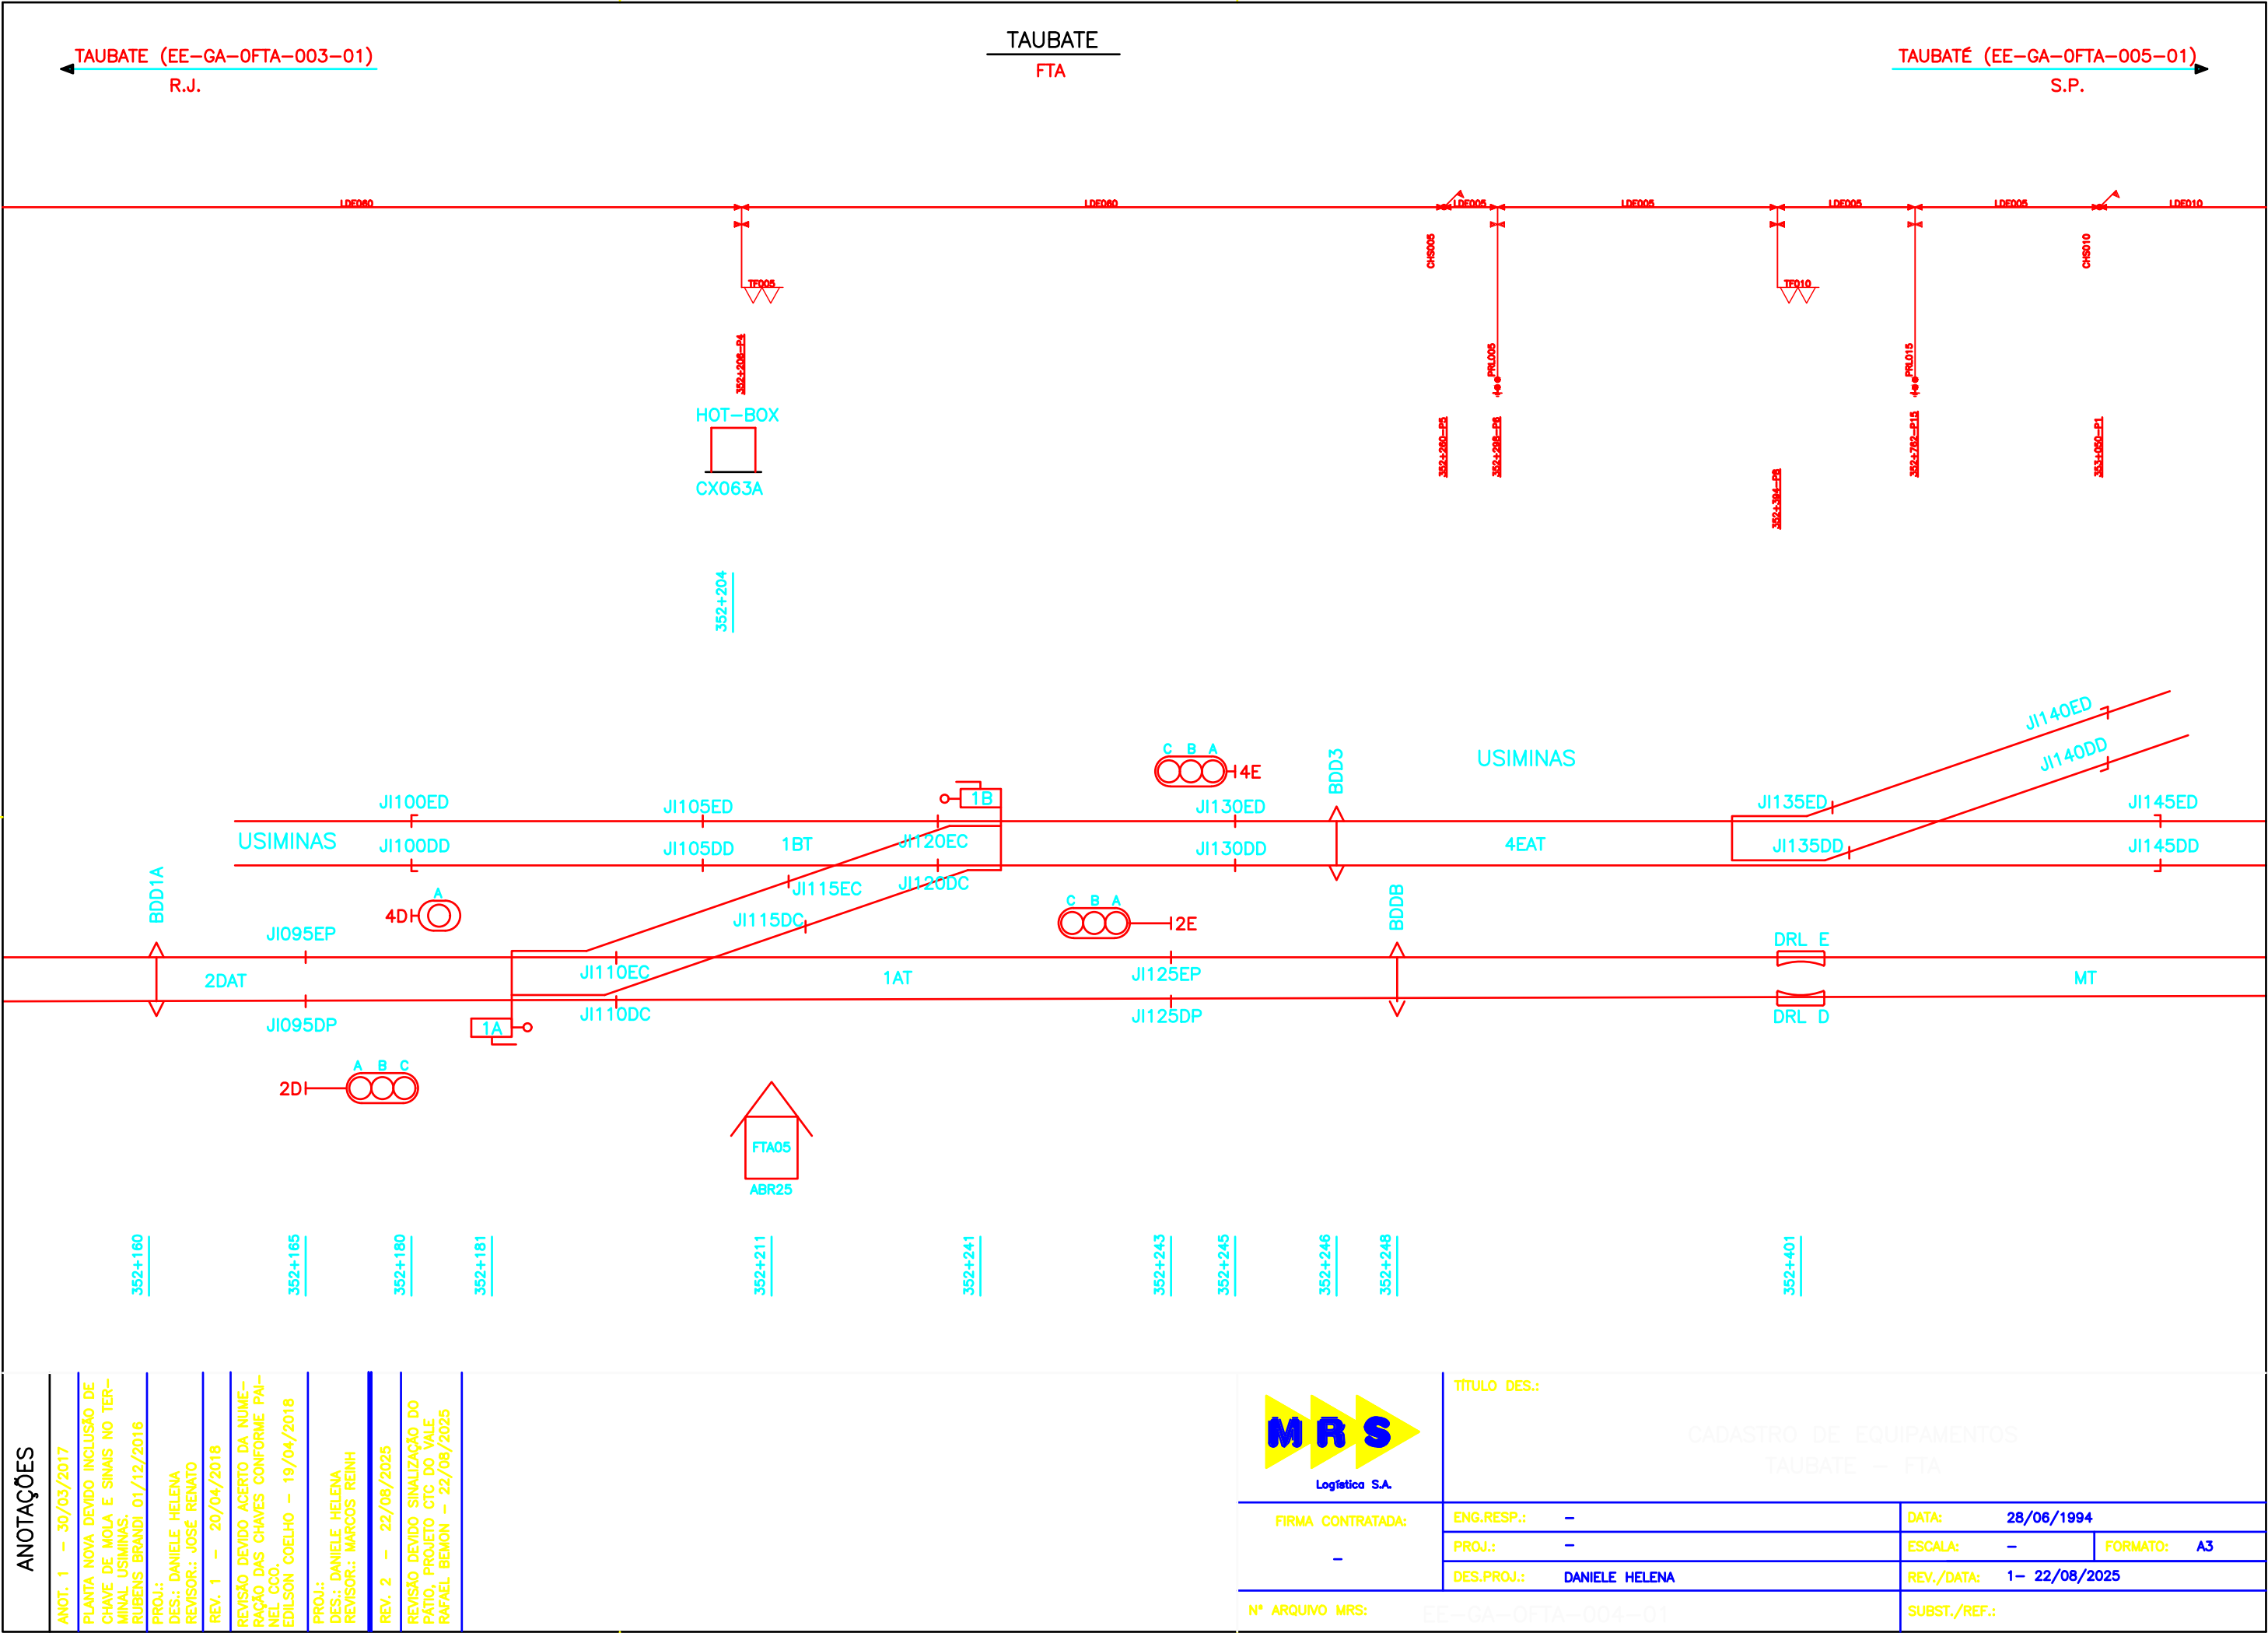

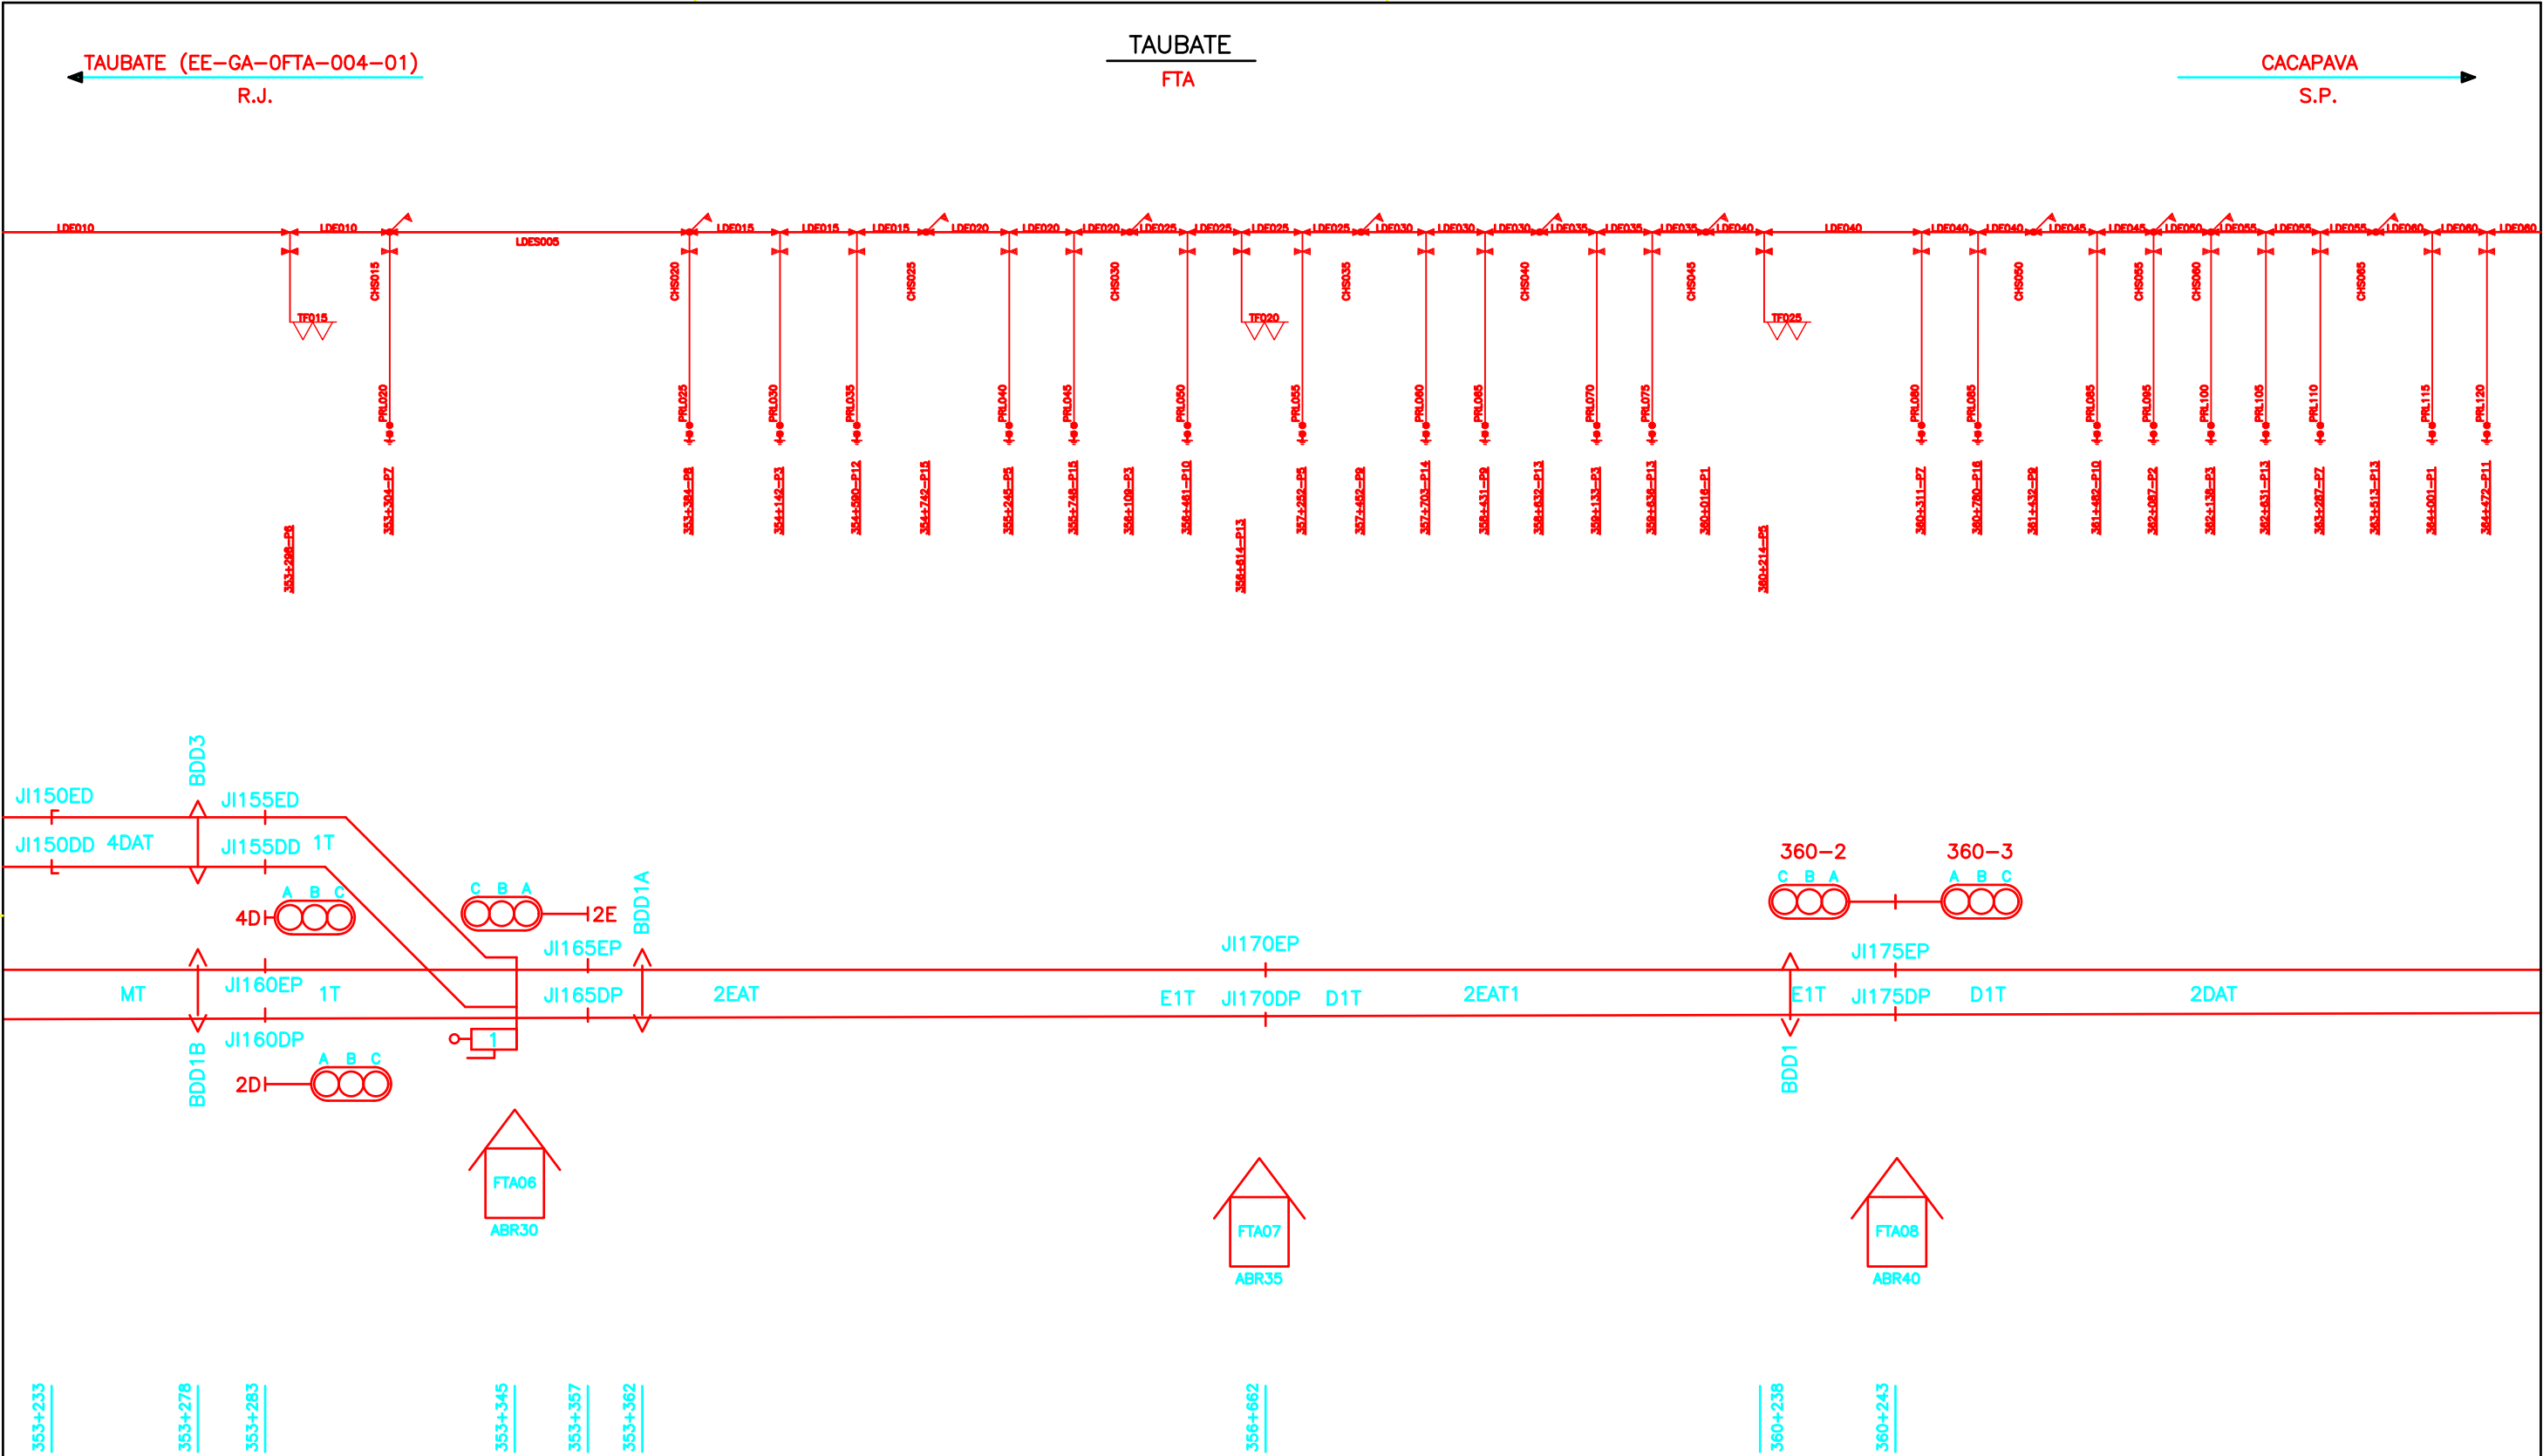

ANOTAÇÕES	
ANOT. 1	30/03/2017
PLANTA NOVA DEVIDO INCLUSÃO DE CHAVE DE MOLA E SINAIIS NO TER-MINAL USIMINAS. RUBENS BRANDI 01/12/2016	
PROJ.:	DANIELE HELENA
DES.:	DANIELE HELENA
REVISOR.:	JOSÉ RENATO
REV. 1	20/04/2018
REVISÃO DEVIDO AGERTO DA NÚME-RAÇÃO DAS CHAVES CONFORME PAI-NEL CCO. EDILSON COELHO - 19/04/2018	
PROJ.:	DANIELE HELENA
DES.:	DANIELE HELENA
REVISOR.:	MARCOS REINH
REV. 2	22/08/2025
REVISÃO DEVIDO SINIALIZAÇÃO DO PATIO, PROJETO CTC DO VALE RAFAEL BEMON - 22/06/2025	

 FIRMA CONTRATADA: -	TÍTULO DES.:	
	CADASTRO DE EQUIPAMENTOS TAUBATE – FTA	
	ENG.RESP.:	-
	PROJ.:	-
N° ARQUIVO MRS:	DES.PROJ.:	DANIELE HELENA
	EE-GA-OFTA-005-01	
DATA:		28/06/1994
ESCALA:		-
FORMATO:		A3
REV./DATA:		2- 22/08/2025
SUBST./REF.:		